


CLIENT NAME


MR.SACHIN & MRS.SAMMITHA

DESIGNER NAME	MUSKAN PAREEK
MOBILE NUMBER	6360240132


SHOERACK:

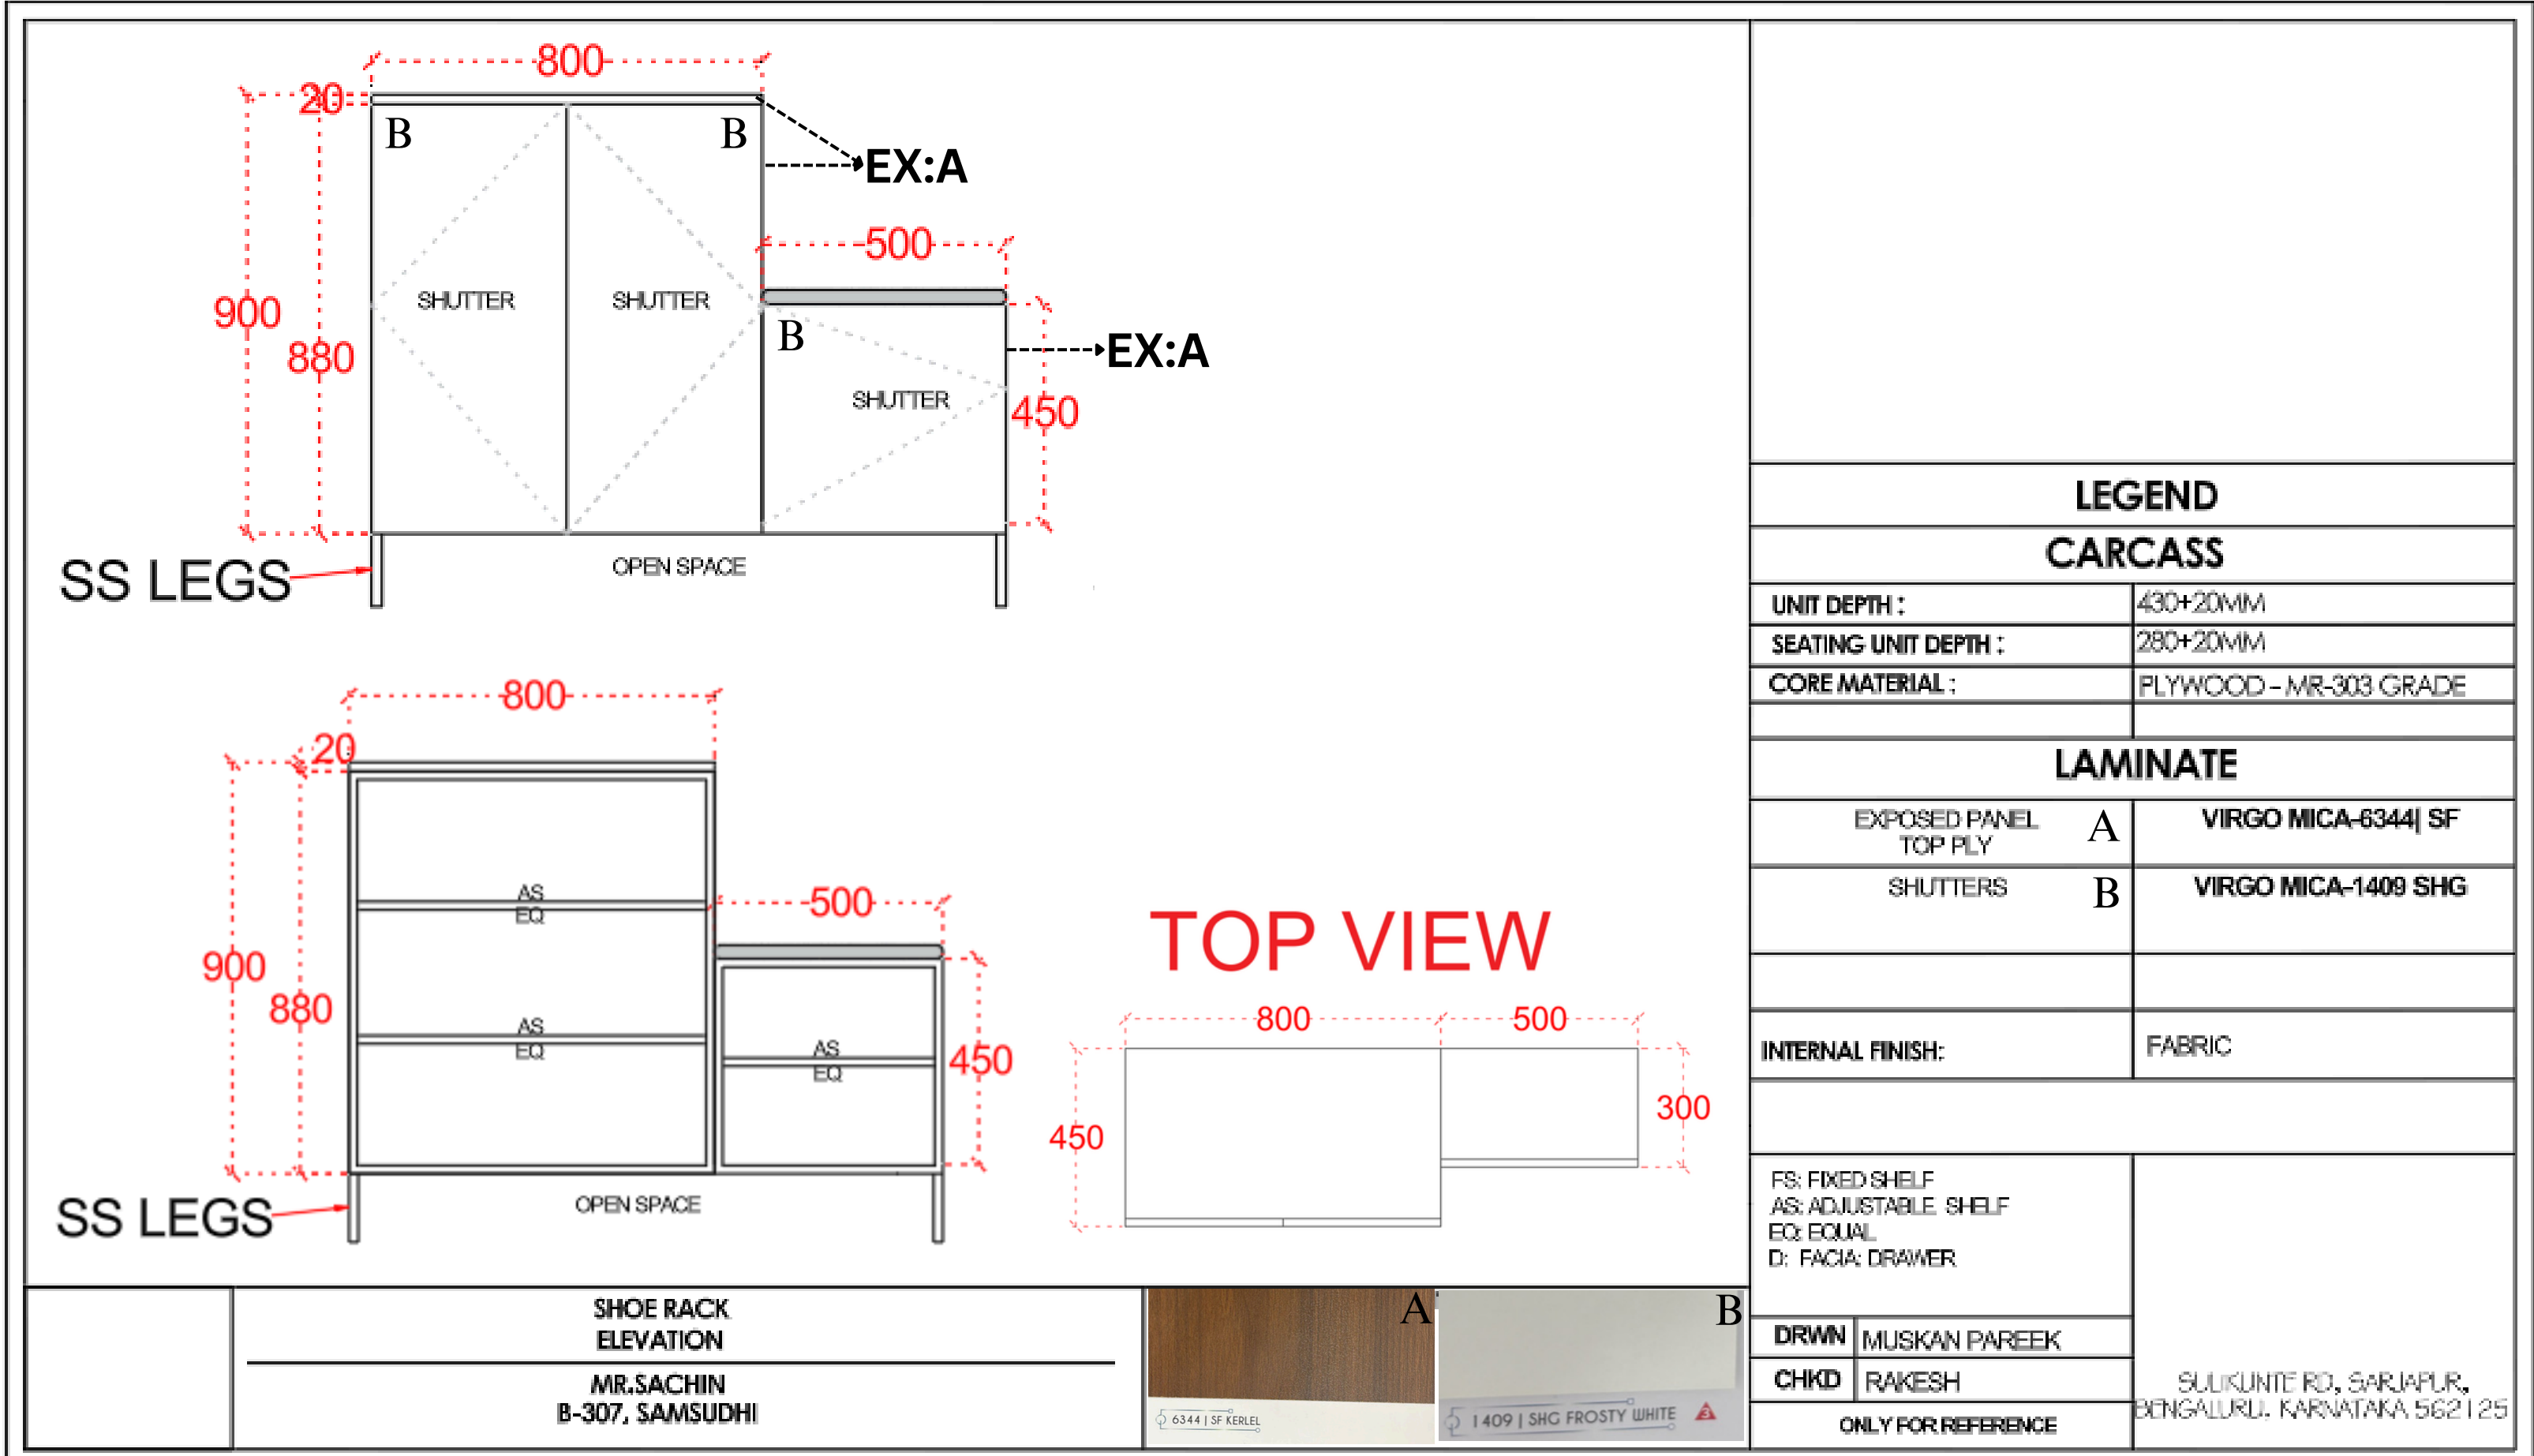


SOFA WALL:

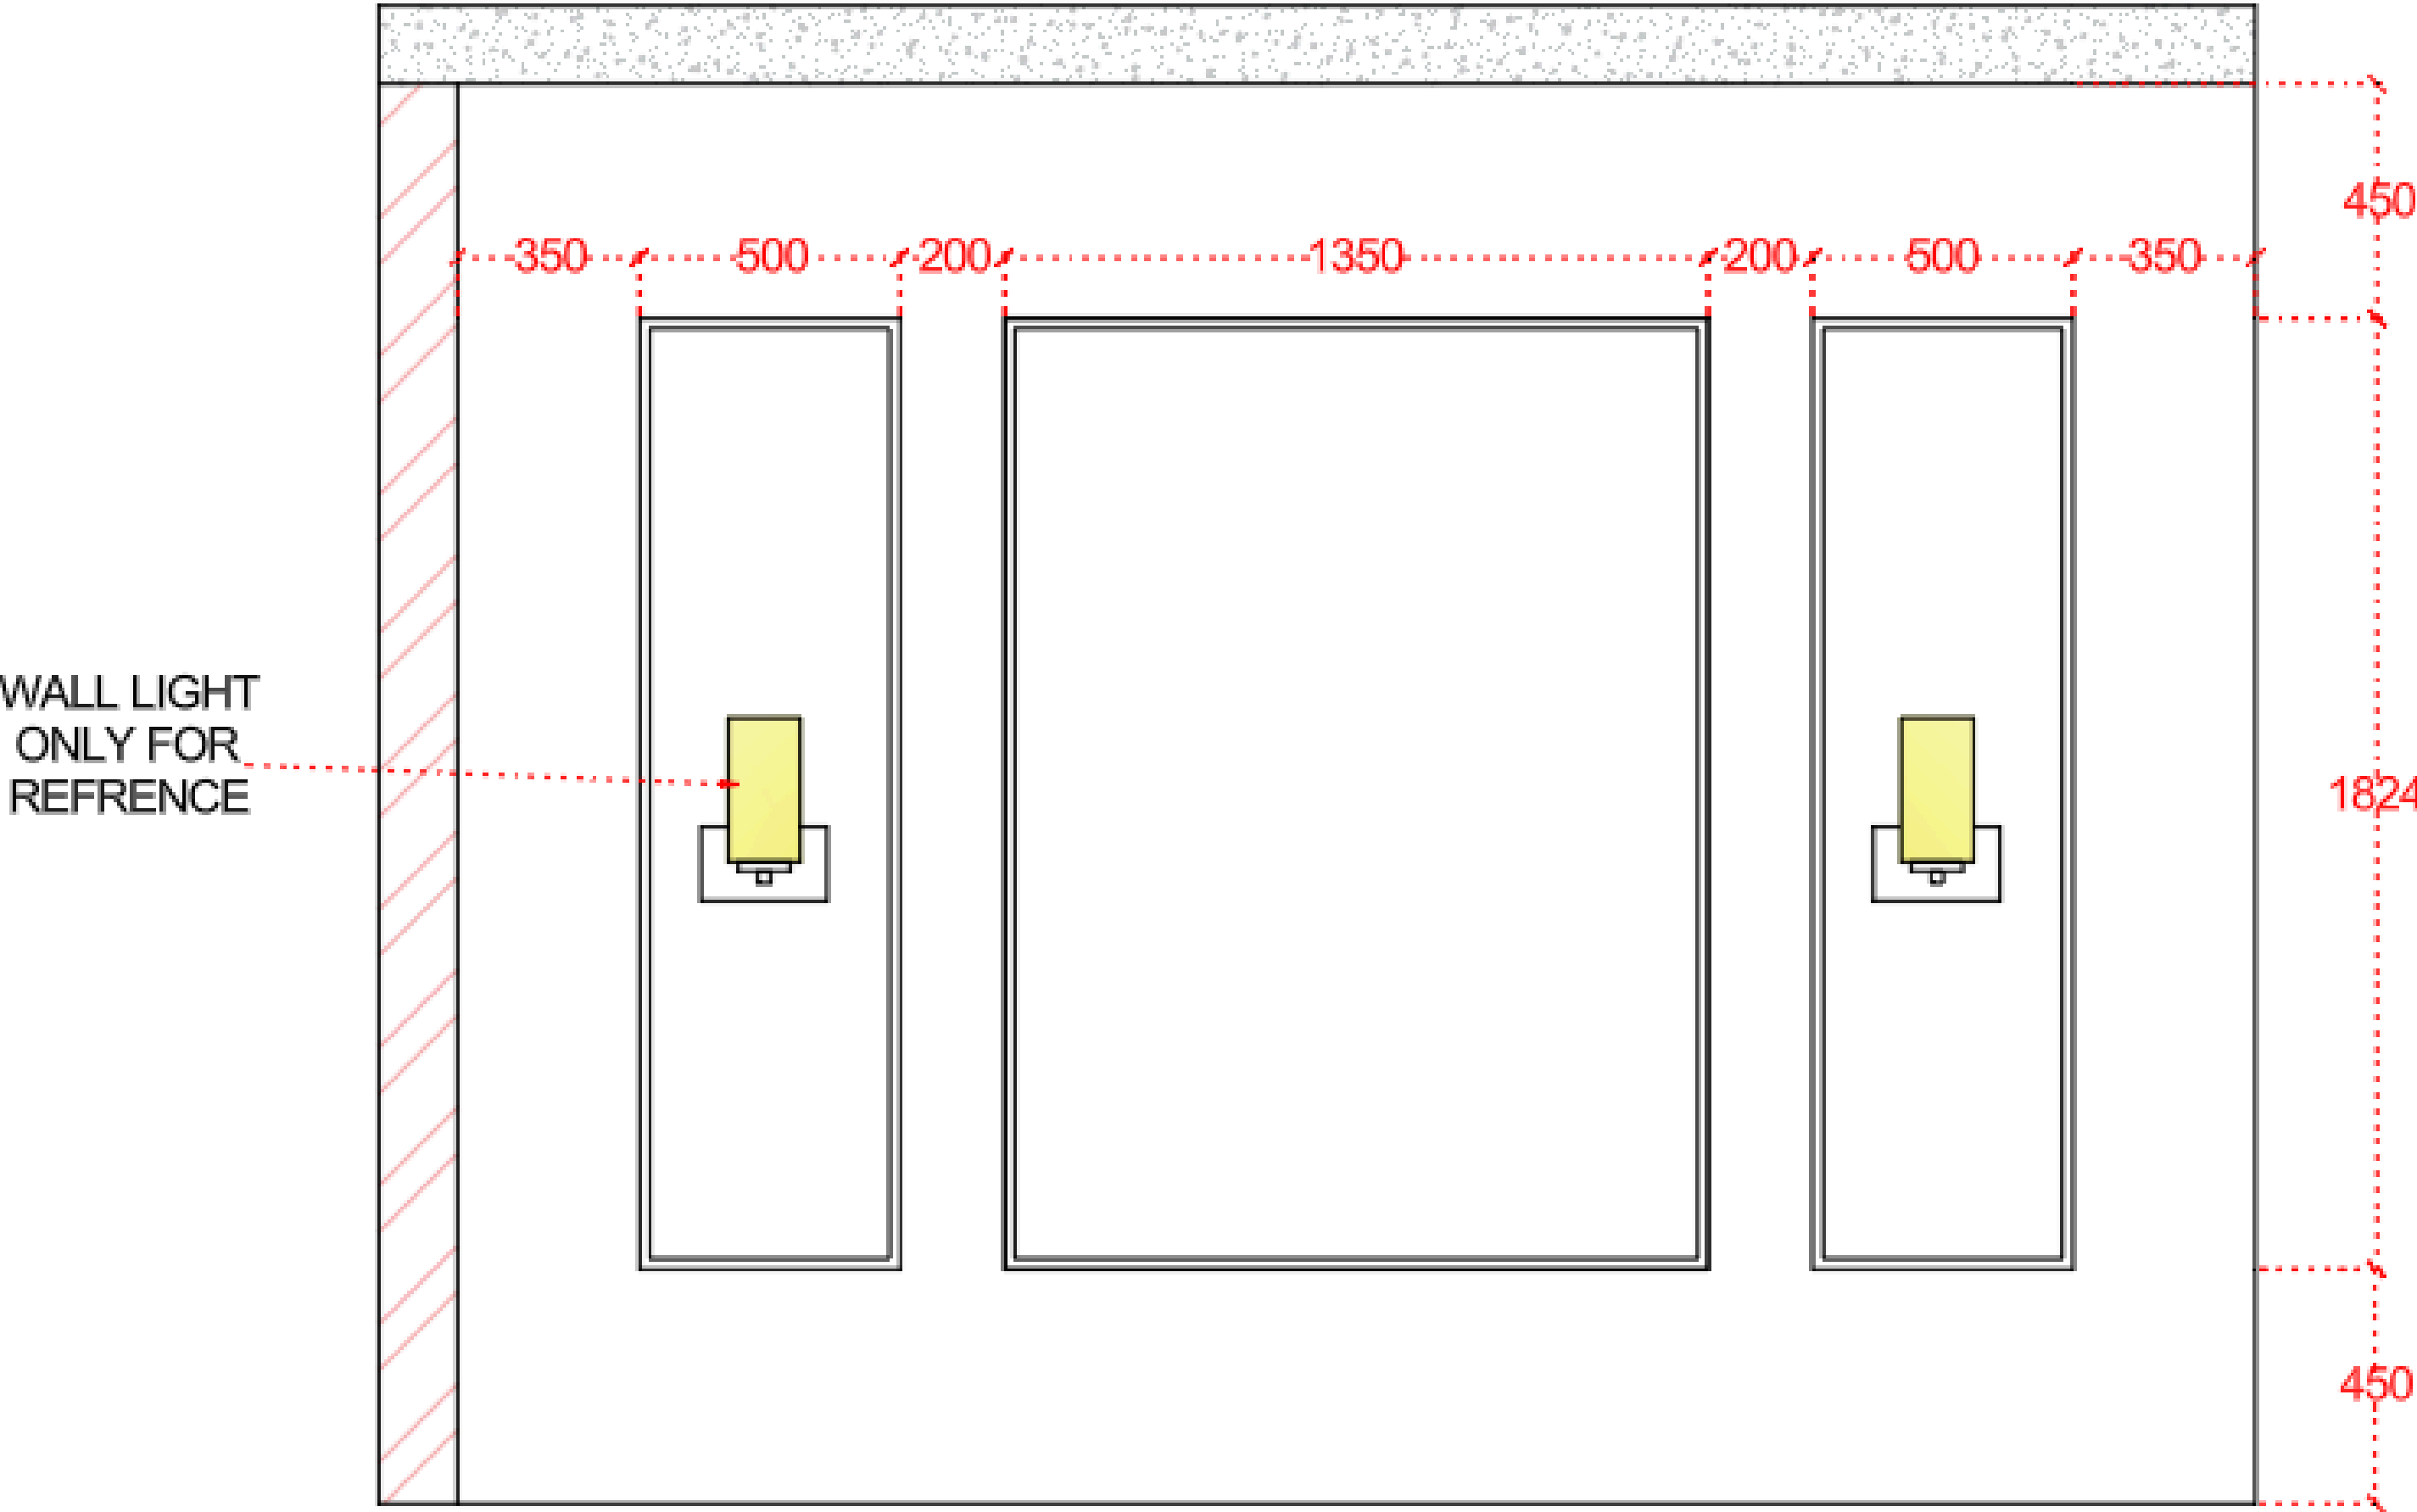


TV UNIT TOP VIEW:

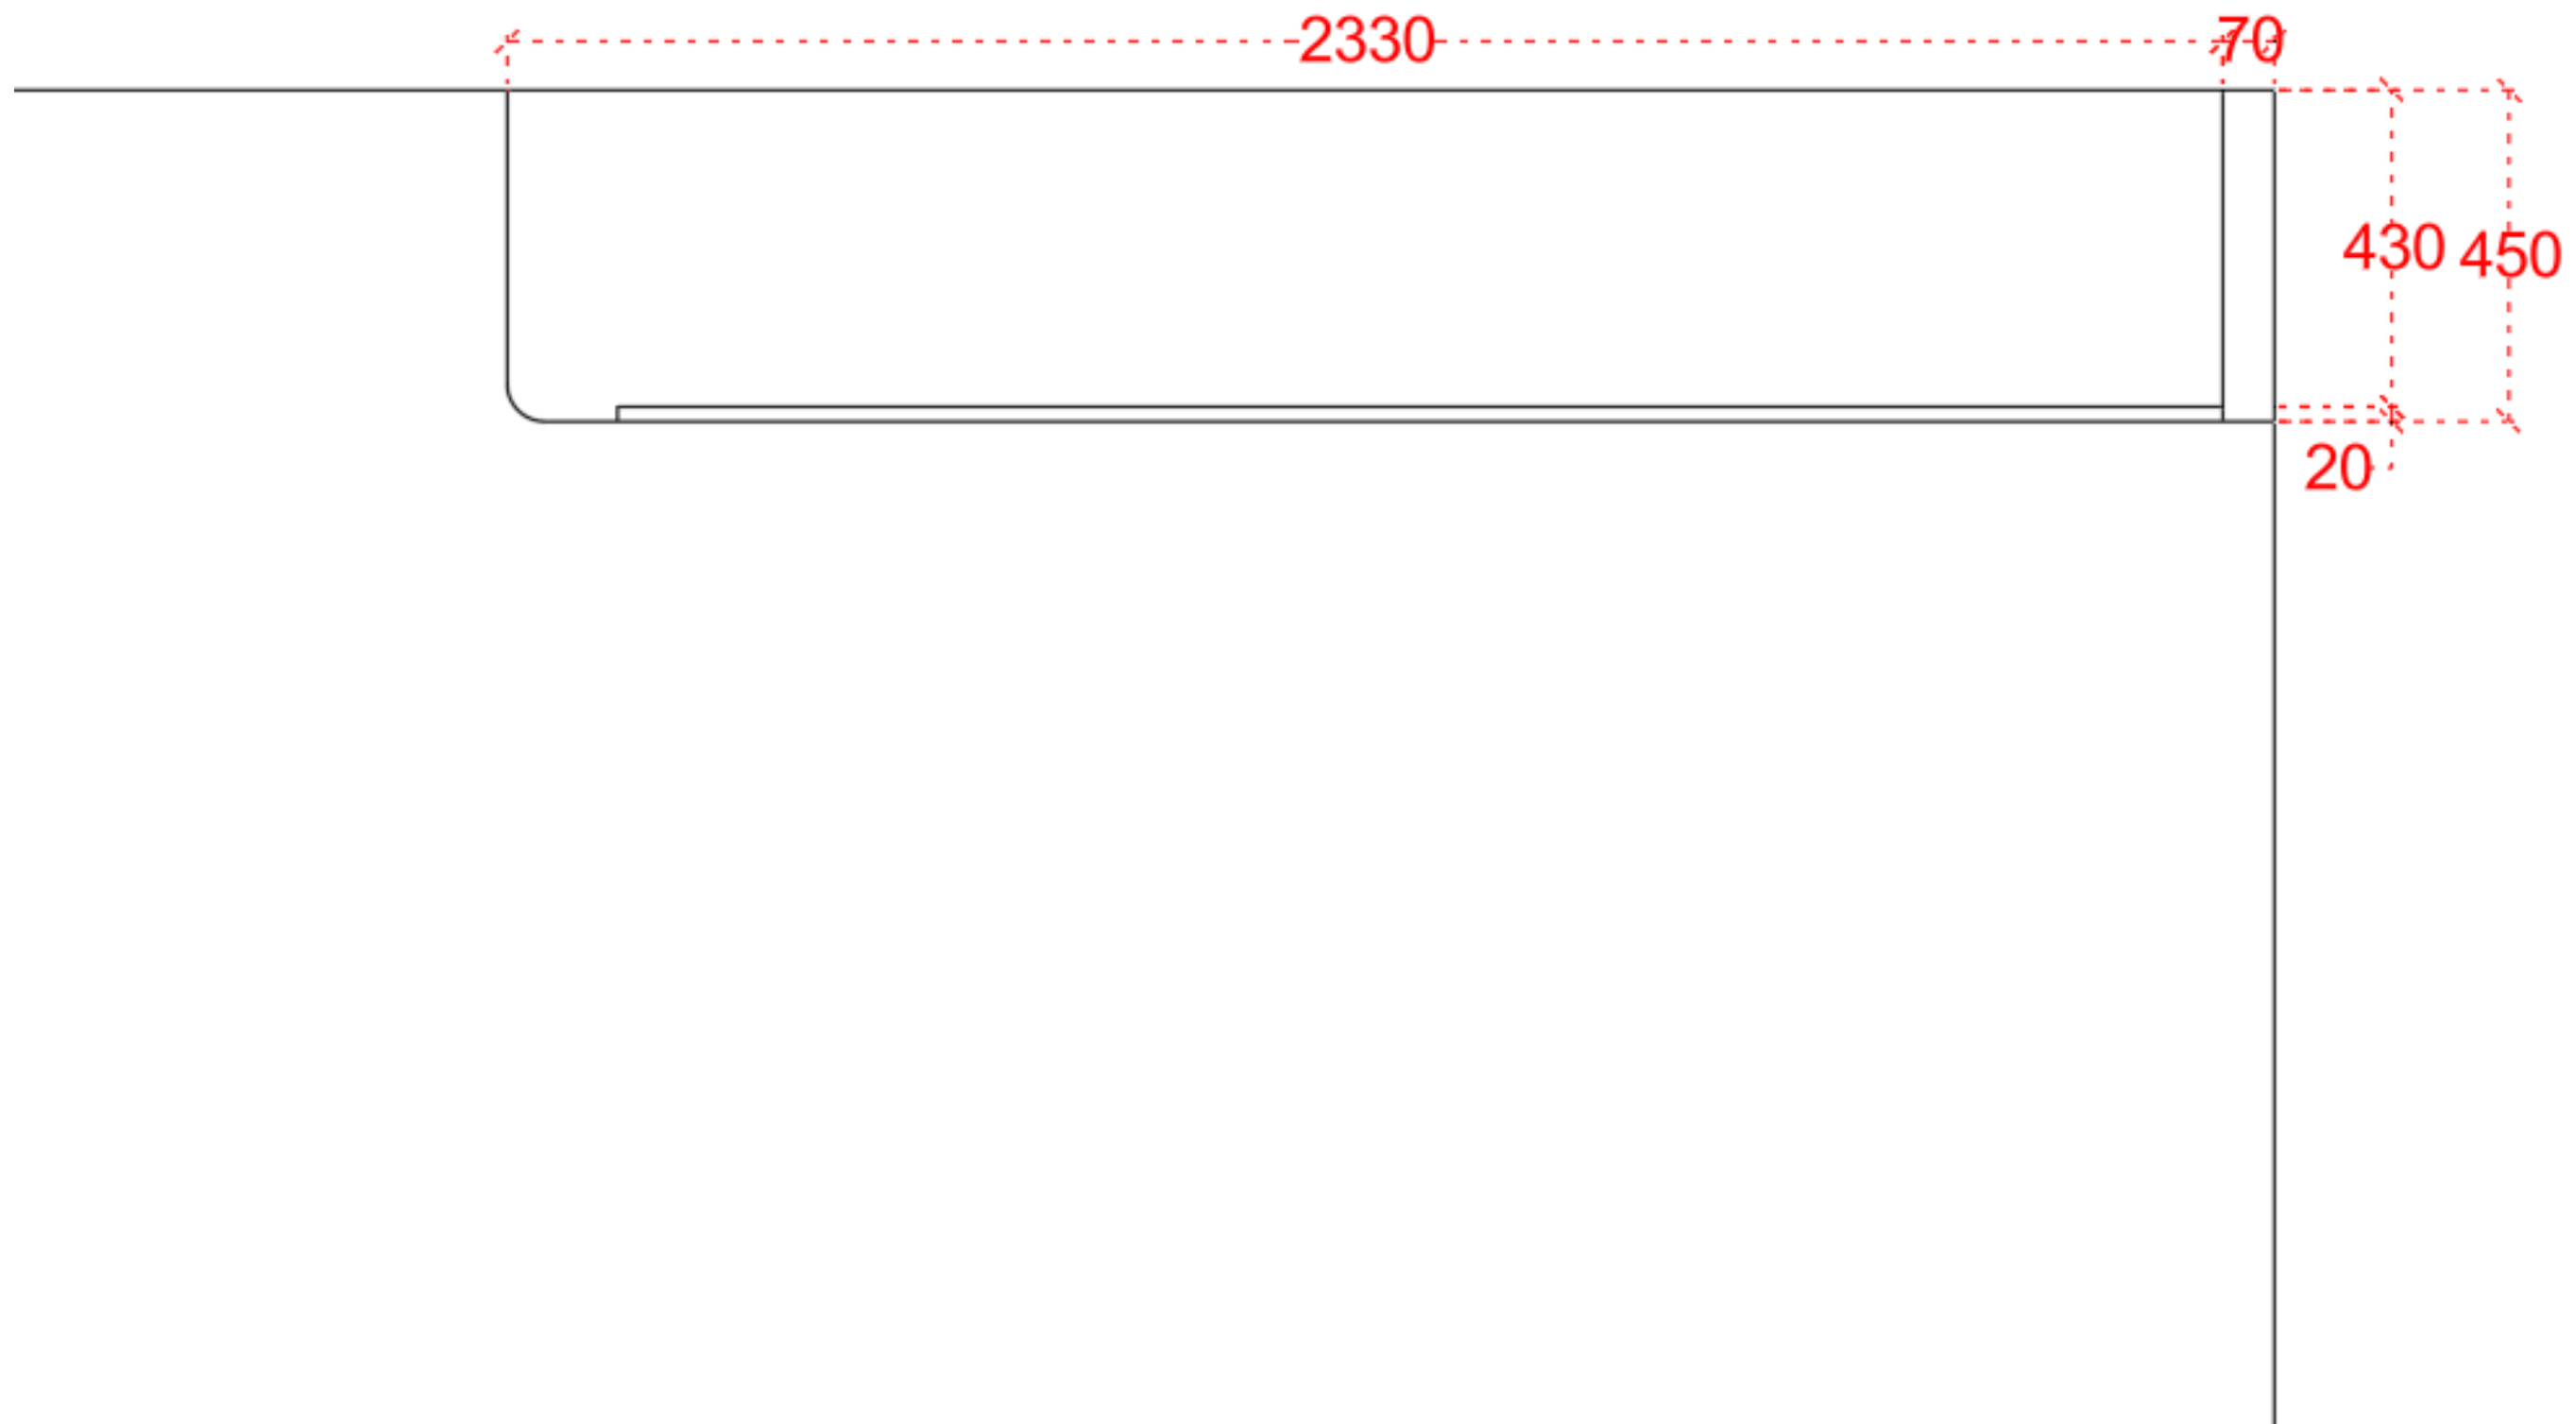

TV UNIT:

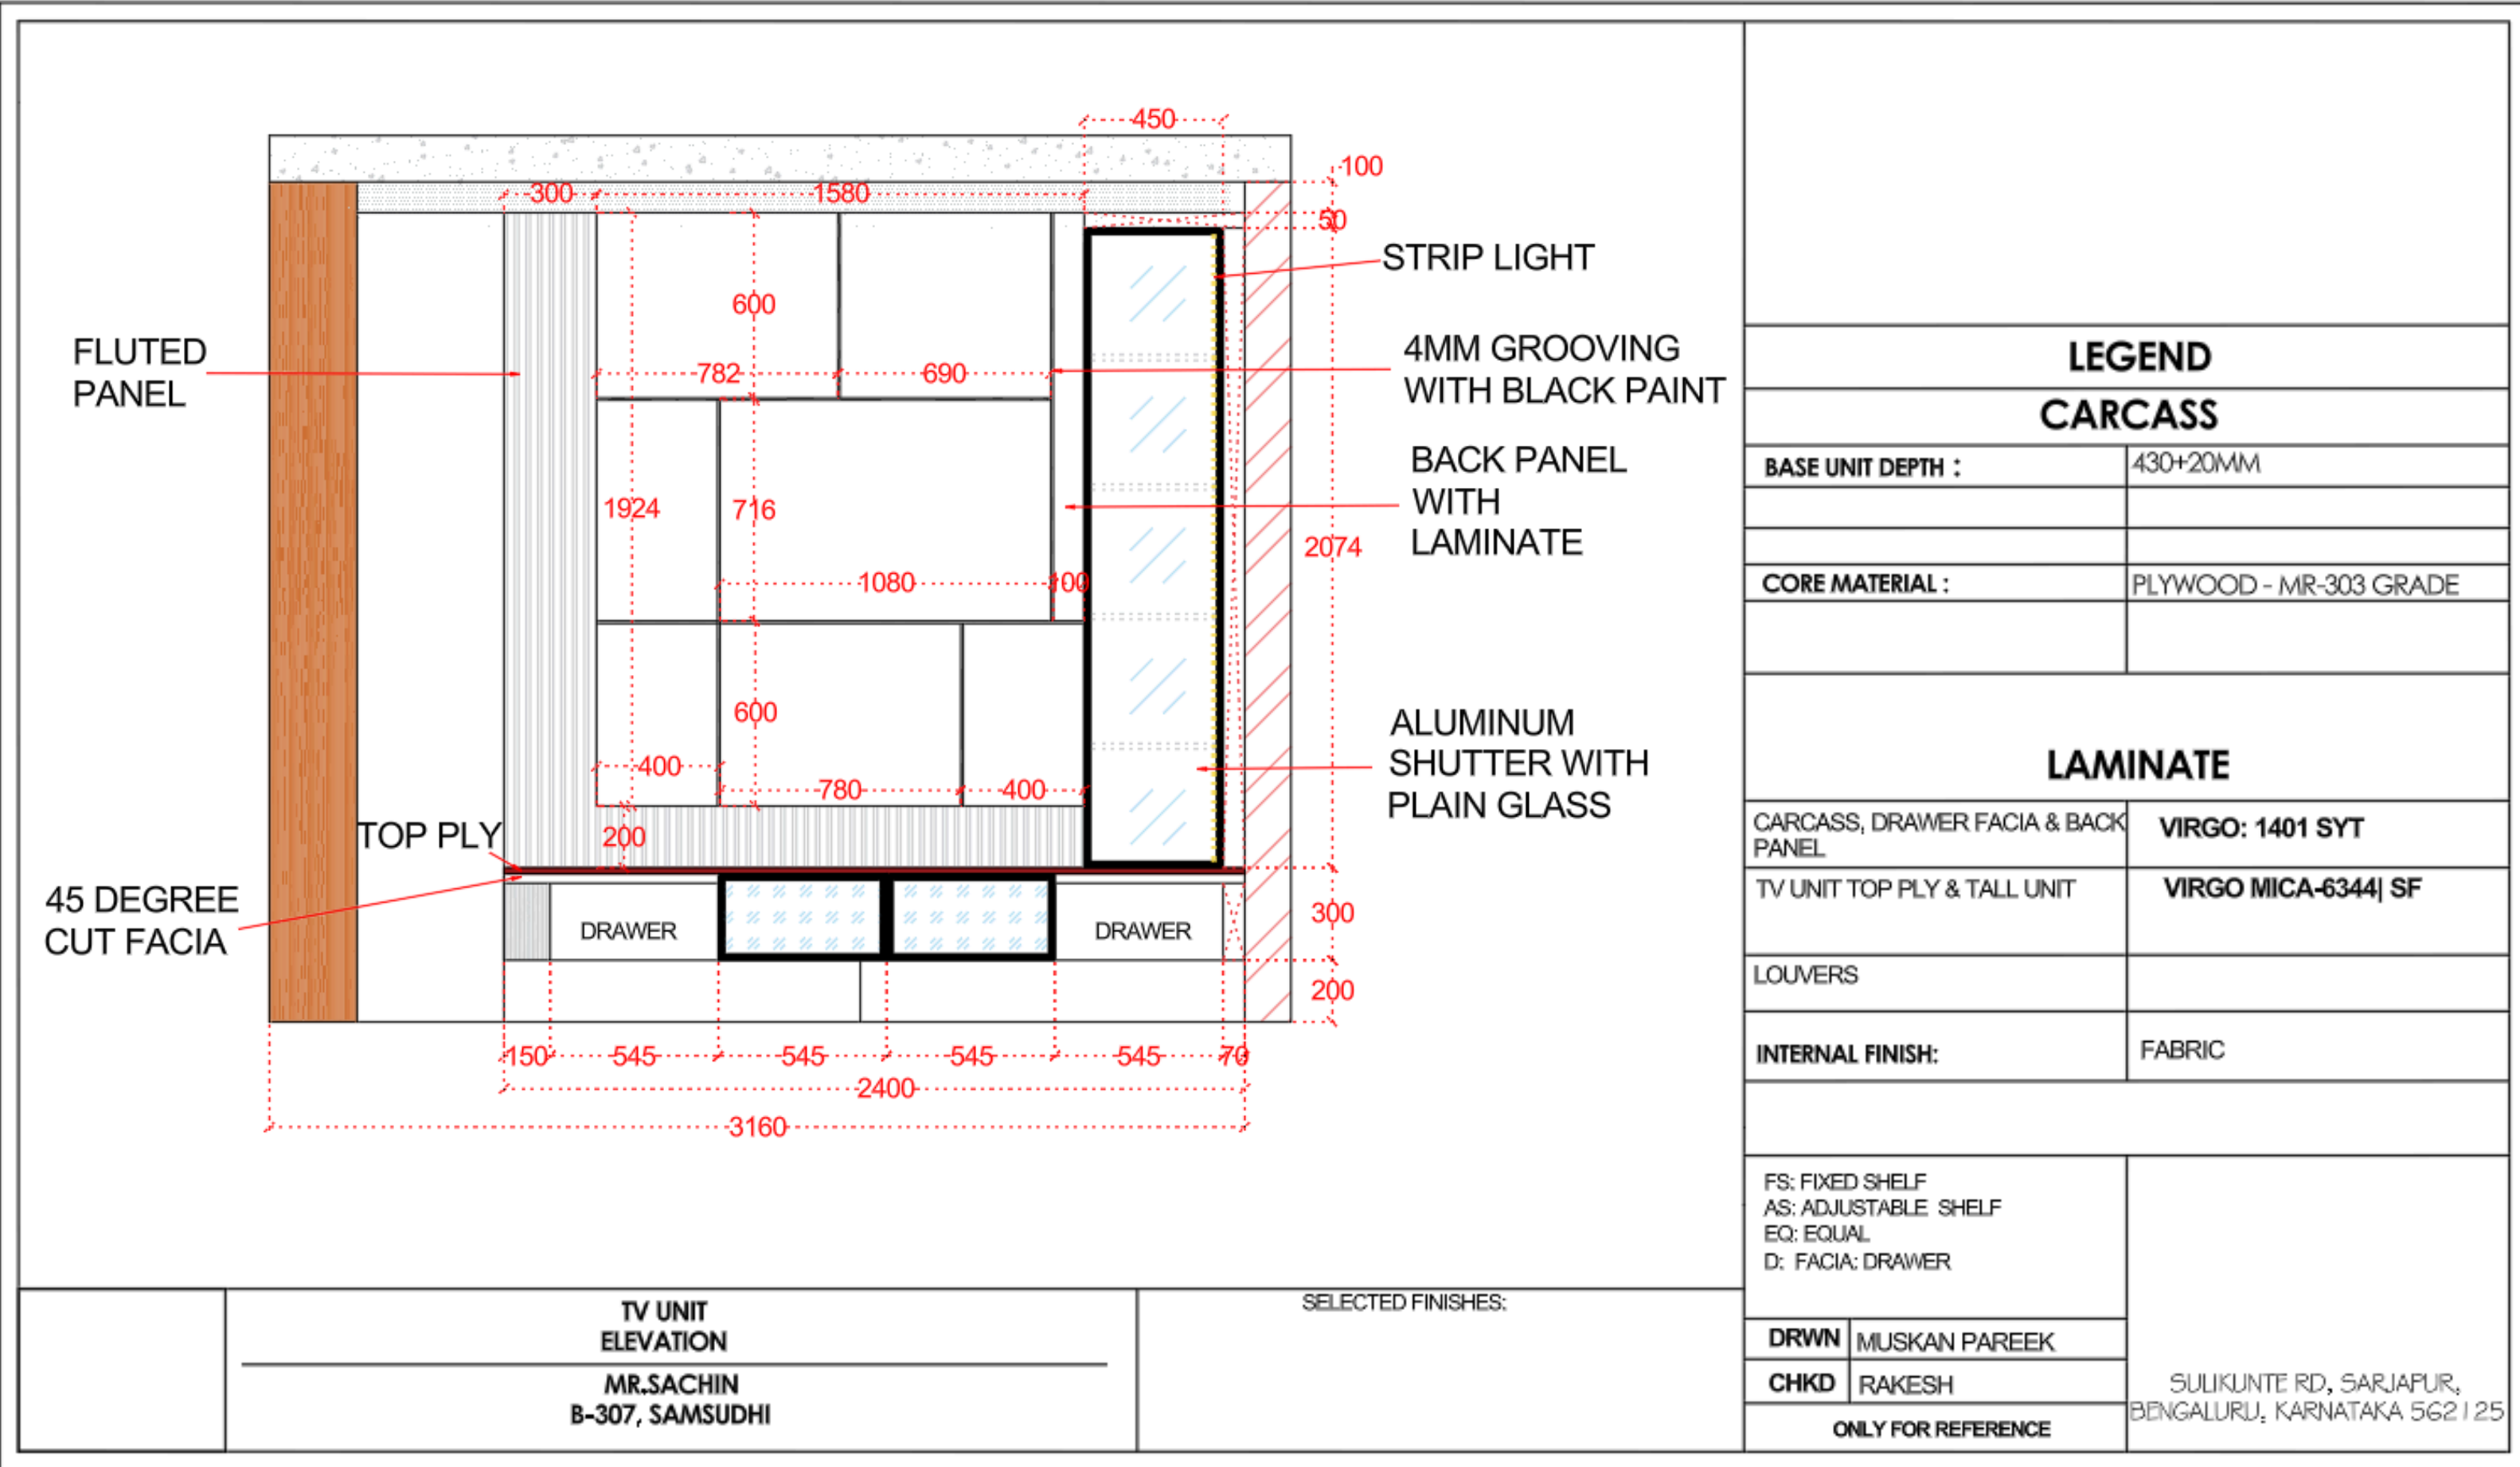

POOJA UNIT:

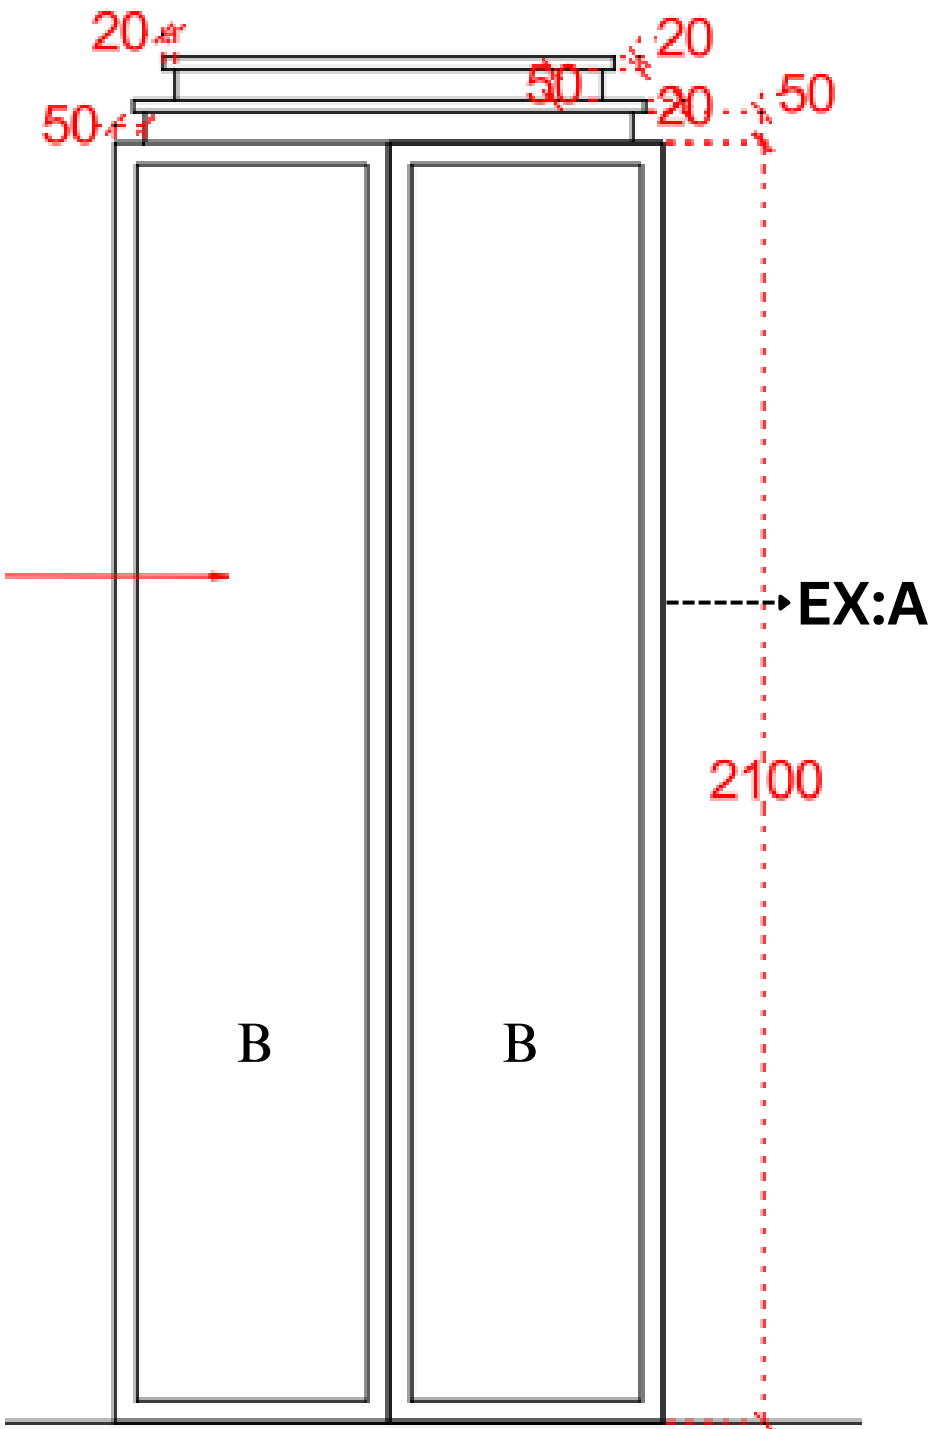

LEGEND	
CARCASS	
UNIT DEPTH :	430+20MM
CORE MATERIAL :	PLYWOOD - MR-303 GRADE
LAMINATE	
EXPOSED PANEL & SHUTTER FRAME	VIRGO MICA-6533 SMT
INTERNAL AND SHUTTER	VIRGO MICA-1409 SHG
INTERNAL FINISH:	
PS: FIXED SHELF AS: ADJUSTABLE SHELF EQ: EQUAL D: FACIA/ DRAWER	
DRWN	MUSKAN PAREEK
CHKD	RAKESH
ONLY FOR REFERENCE	

POOJA UNIT
ELEVATION


MR.SACHIN
B-307, SAMSUDHI

A


B

SULIKUNTE RD, SARJAPUR,
BENGALLURU, KARNATAKA 562125

CROCKERY UNIT EXTERNAL:

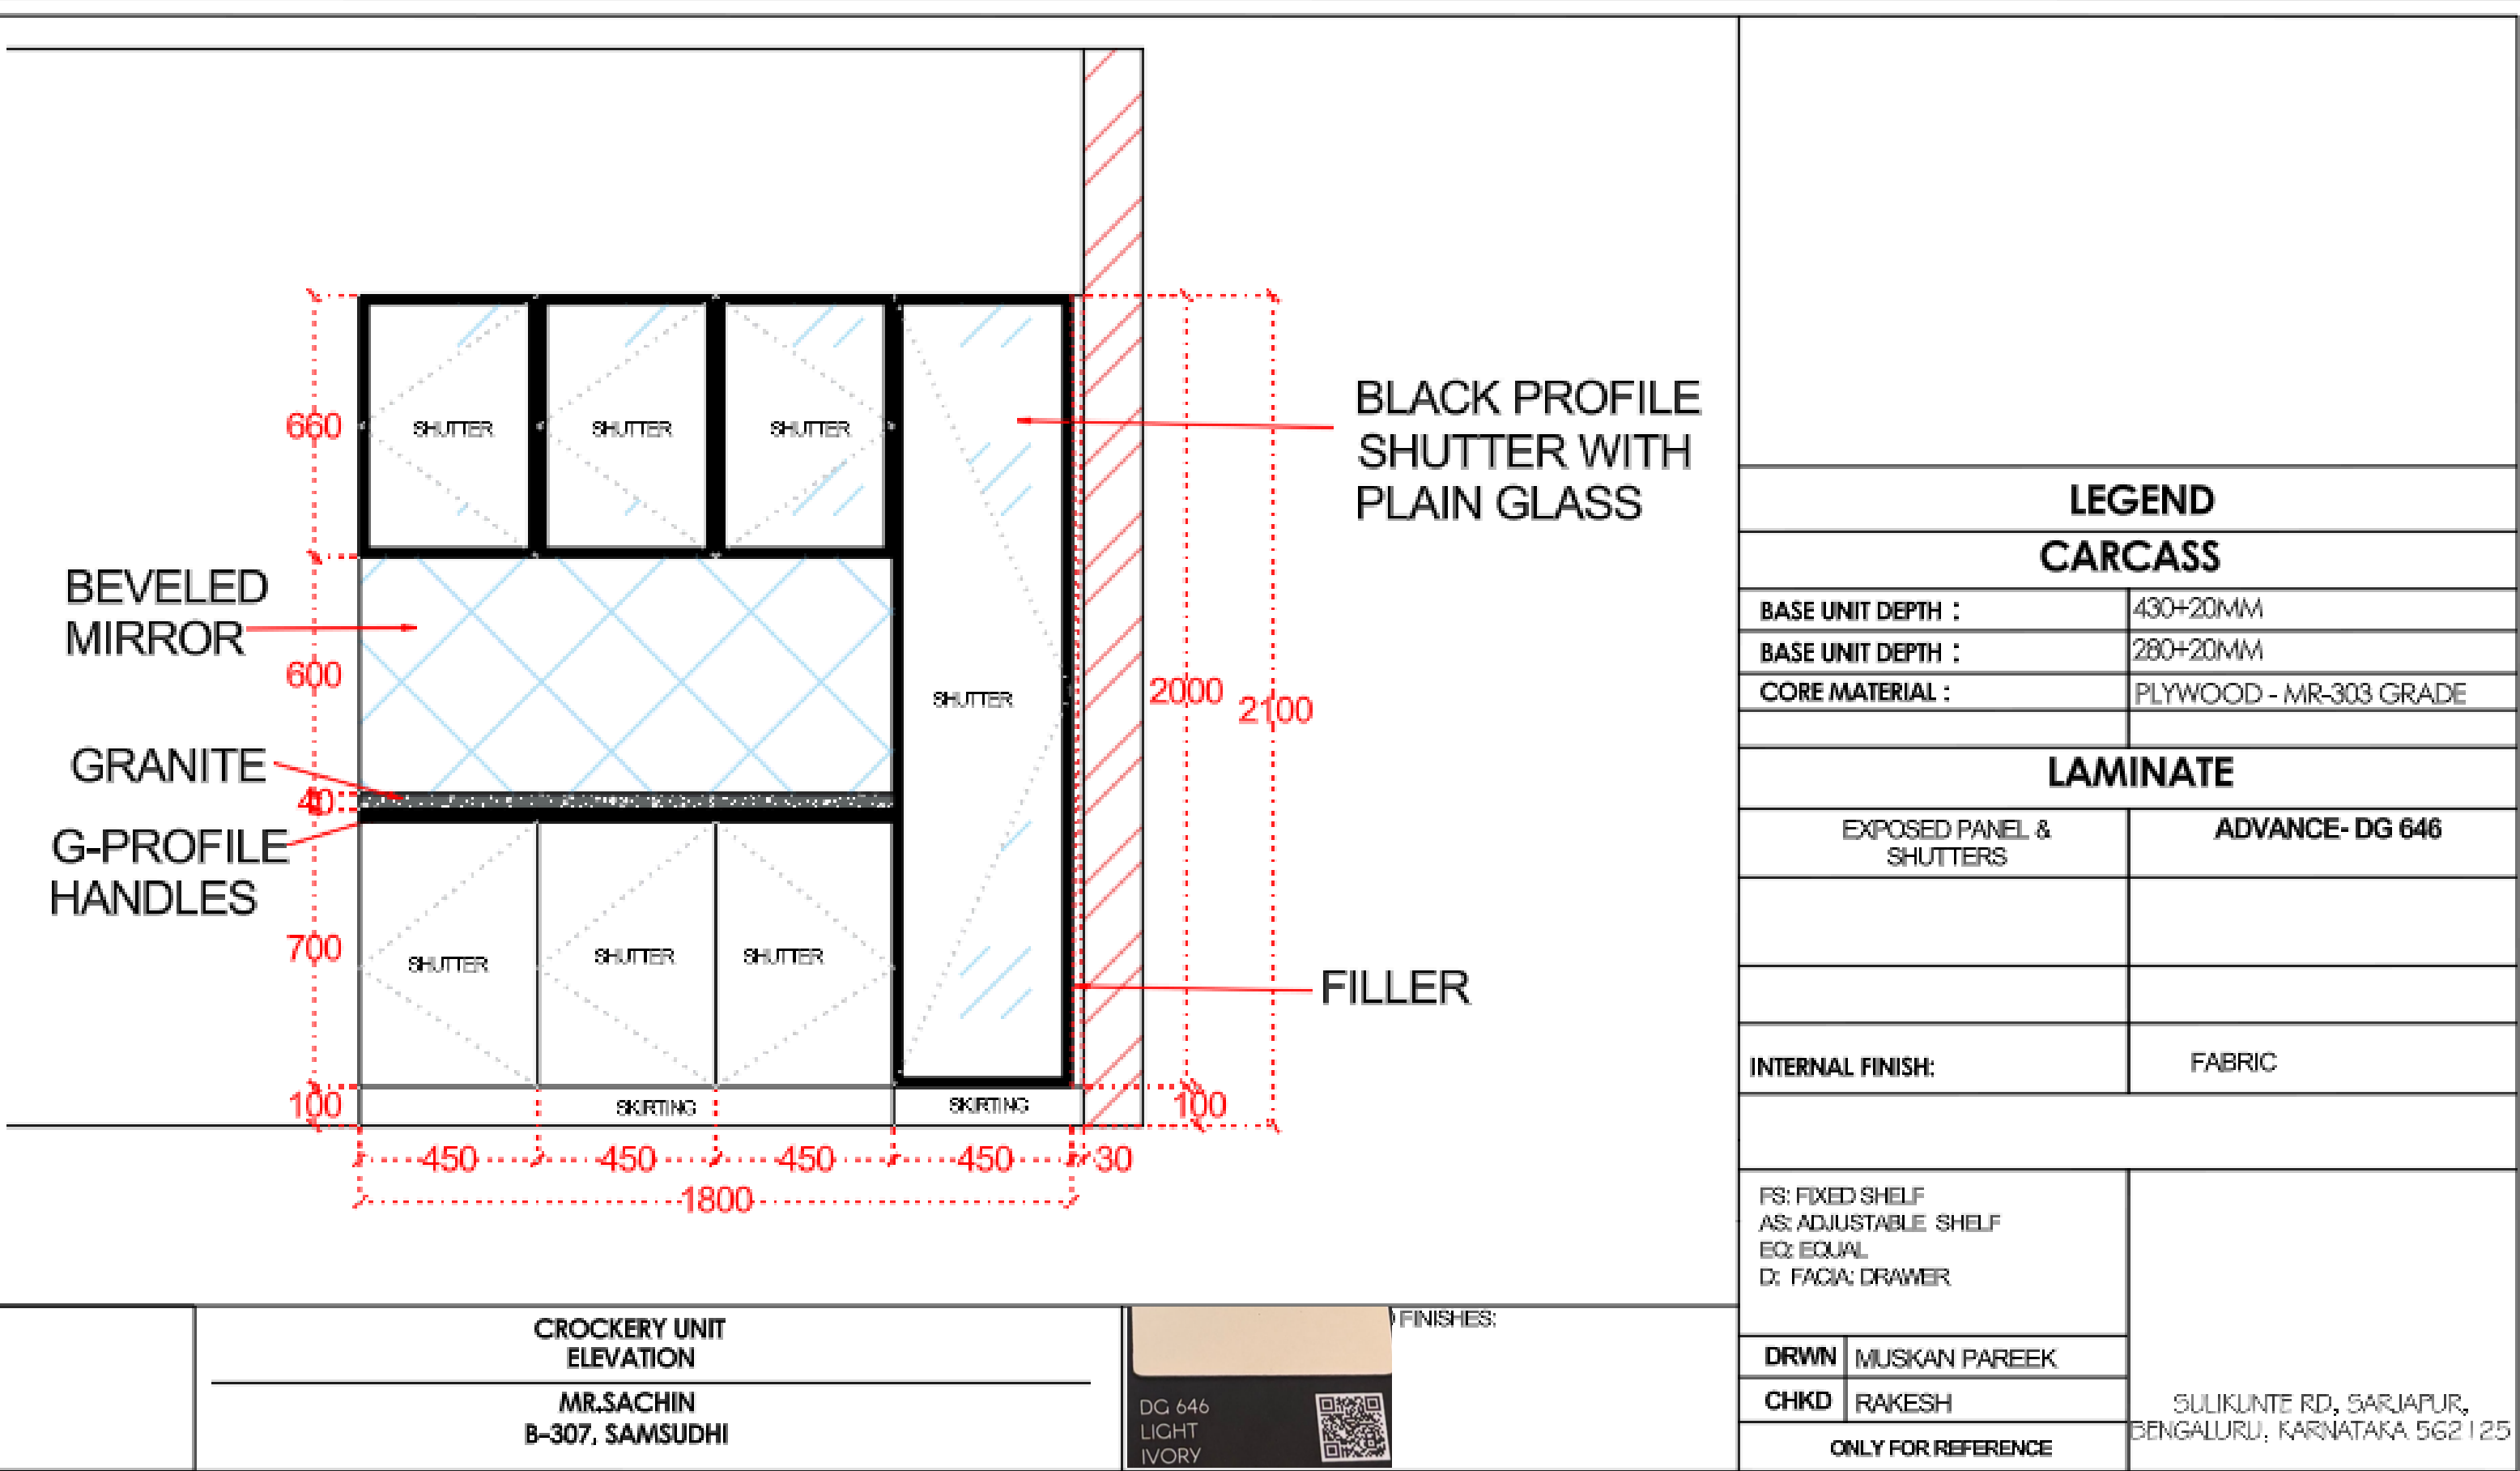

CROCKERY UNIT INTERNAL:

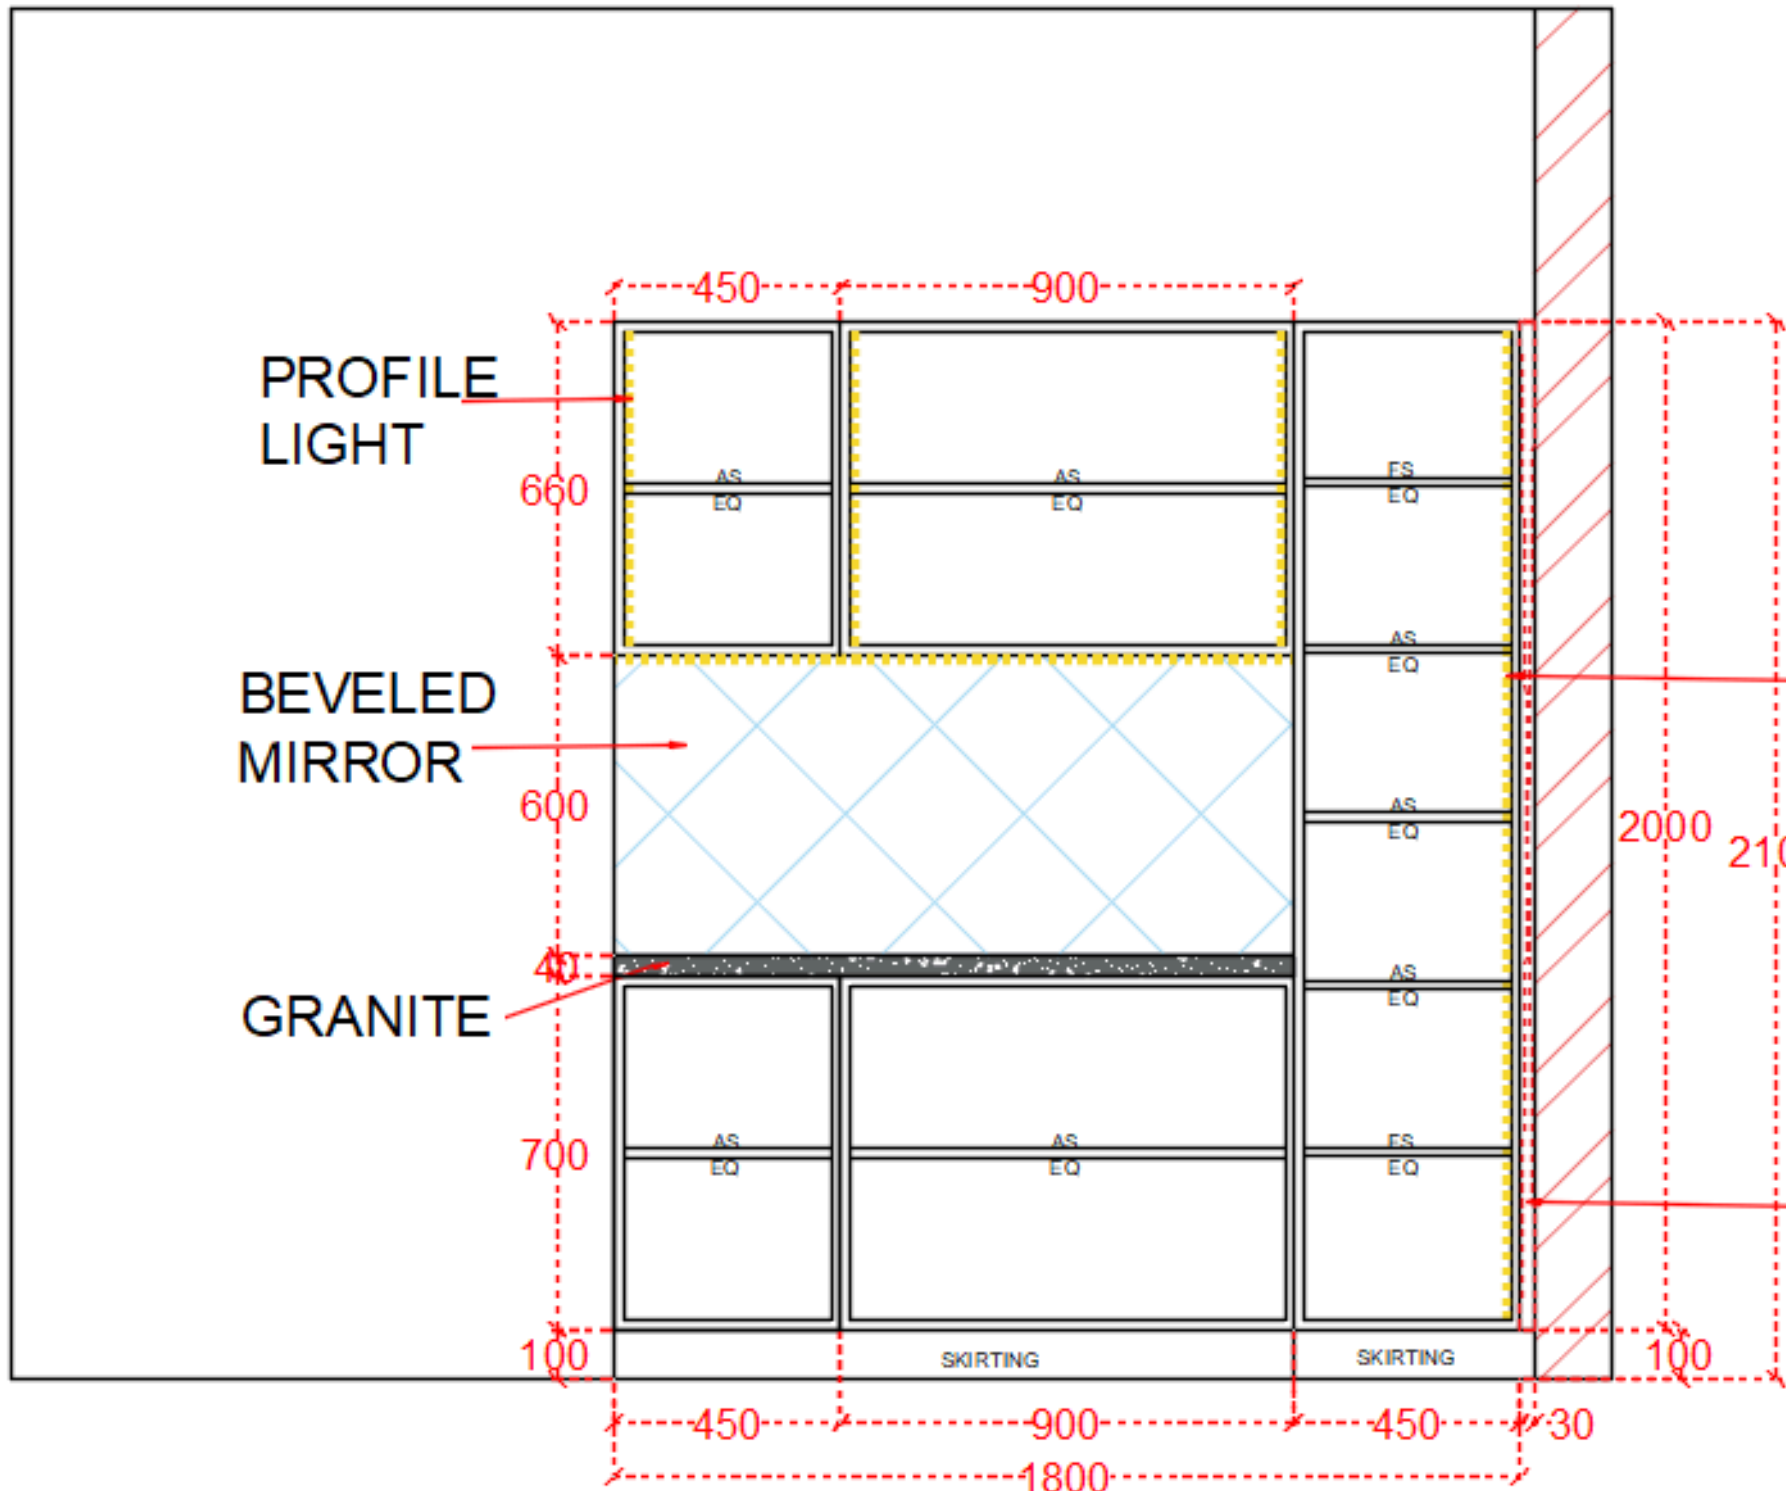

PROFILE LIGHT

FILLER

LEGEND

CARCASS

BASE UNIT DEPTH :	430+20MM
BASE UNIT DEPTH :	280+20MM
CORE MATERIAL :	PLYWOOD - MR-303 GRADE

LAMINATE

EXPOSED PANEL & SHUTTERS	ADVANCE- DG 646
--------------------------	-----------------

INTERNAL FINISH:	FABRIC
------------------	--------

FS: FIXED SHELF
AS: ADJUSTABLE SHELF
EQ: EQUAL
D: FACIA DRAWER

DRWN	MUSKAN PAREEK
CHKD	RAKESH

ONLY FOR REFERENCE

SULIKUNTE RD, SARJAPUR,
BENGALURU, KARNATAKA 562 125

CROCKERY UNIT
ELEVATION



MR.SACHIN
B-307, SAMSUDHI

FINISHES:


DG 646
LIGHT
IVORY



DINING AREA SINK UNIT:

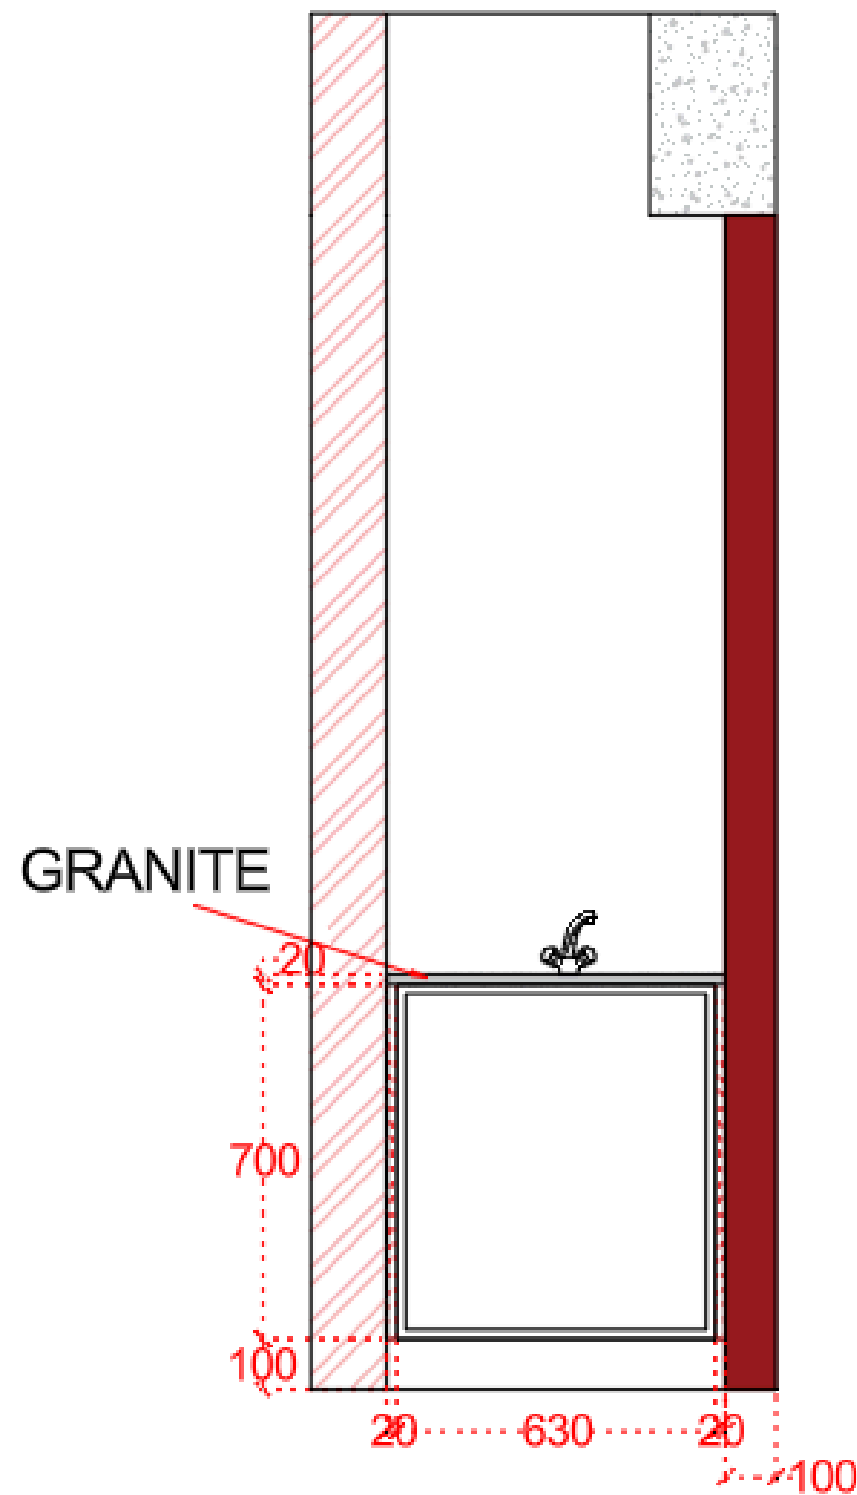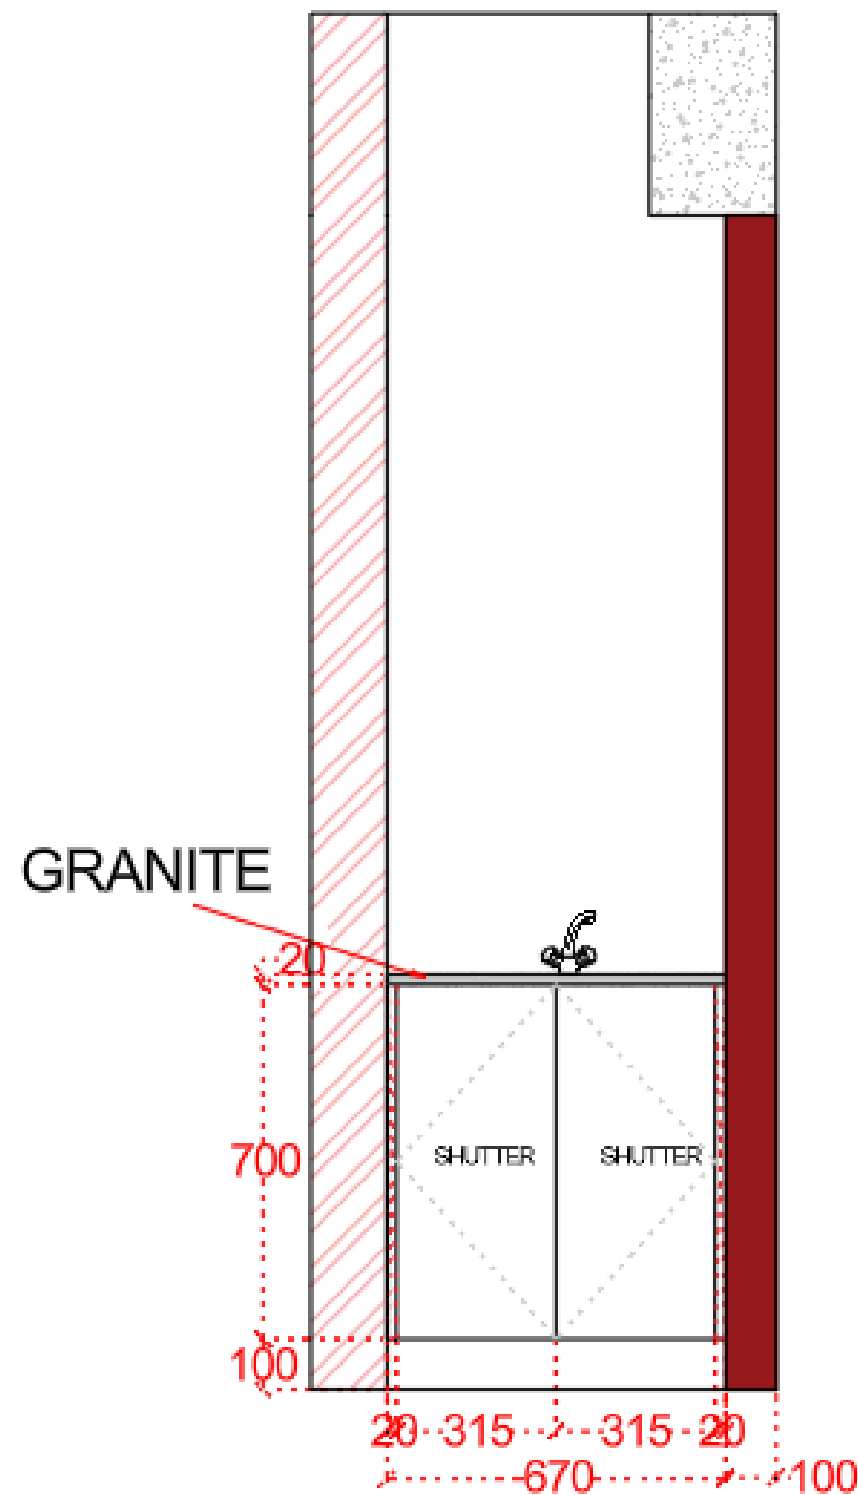

COMMON WASH BASIN
ELEVATION
MR.SACHIN
B-307, SAMUDHI

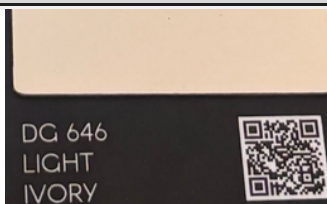

FINISHES:

LEGEND

CARCASS

UNIT DEPTH :	530+20MM
CORE MATERIAL :	PLYWOOD - BWP-710 GRADE

LAMINATE

SHUTTERS EXPOSED PANEL	ADVANCE: DG 646
INTERNAL FINISH:	FABRIC

FS: FIXED SHELF
AS: ADJUSTABLE SHELF
EQ: EQUAL
D: FACIA: DRAWER


DRWN MUSKAN PAREEK
CHKD RAKESH

ONLY FOR REFERENCE


SULIKUNTE RD, SARJAPUR,
BENGALURU, KARNATAKA 562125

KITCHEN TOP VIEW:


KITCHEN BASE UNIT
TOP VIEW

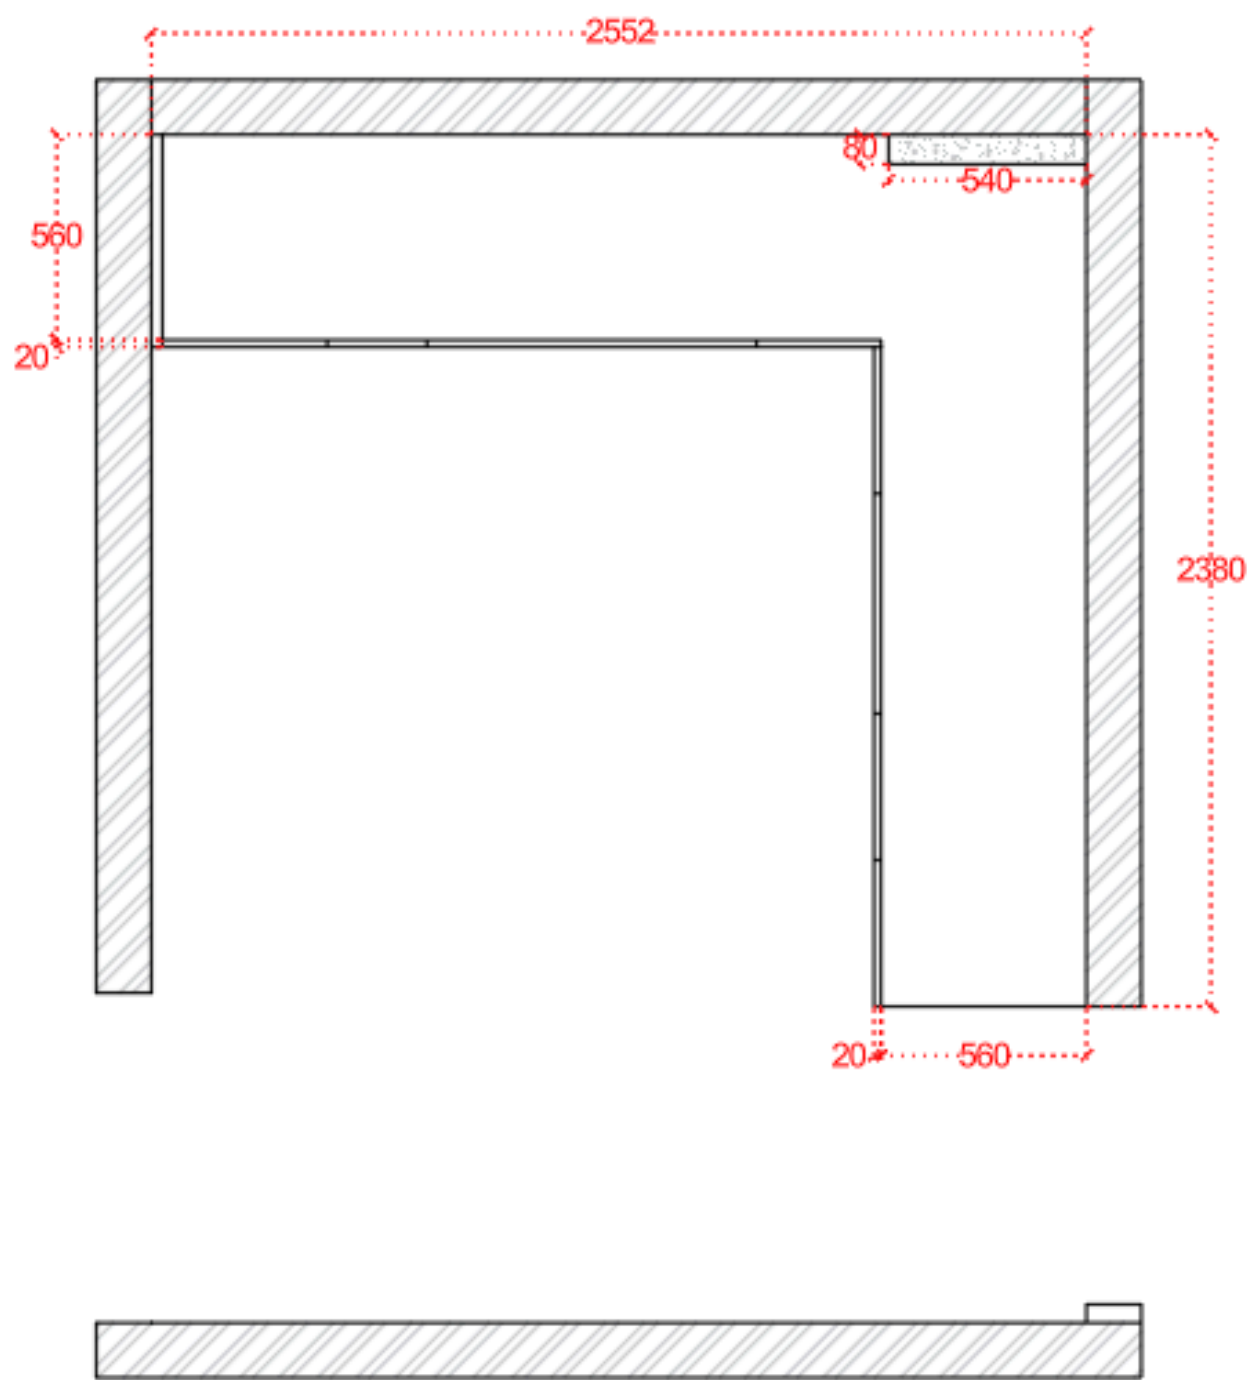


KITCHEN WALL UNIT
TOP VIEW

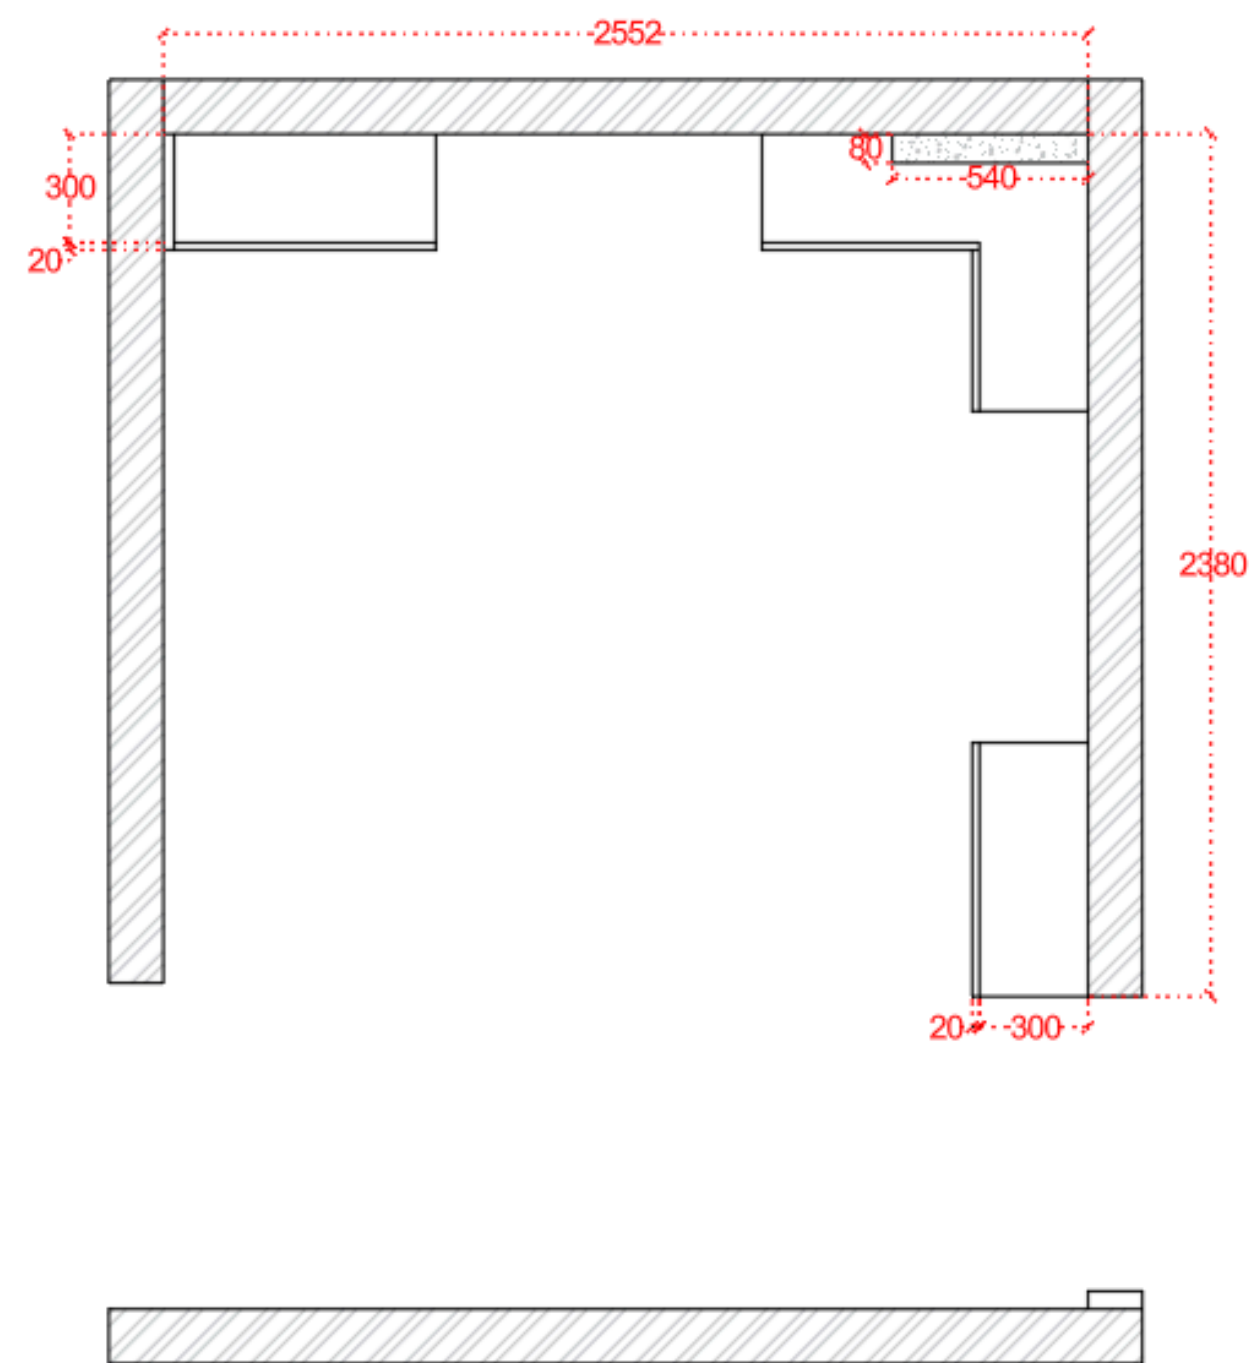


KITCHEN LOFT UNIT
TOP VIEW

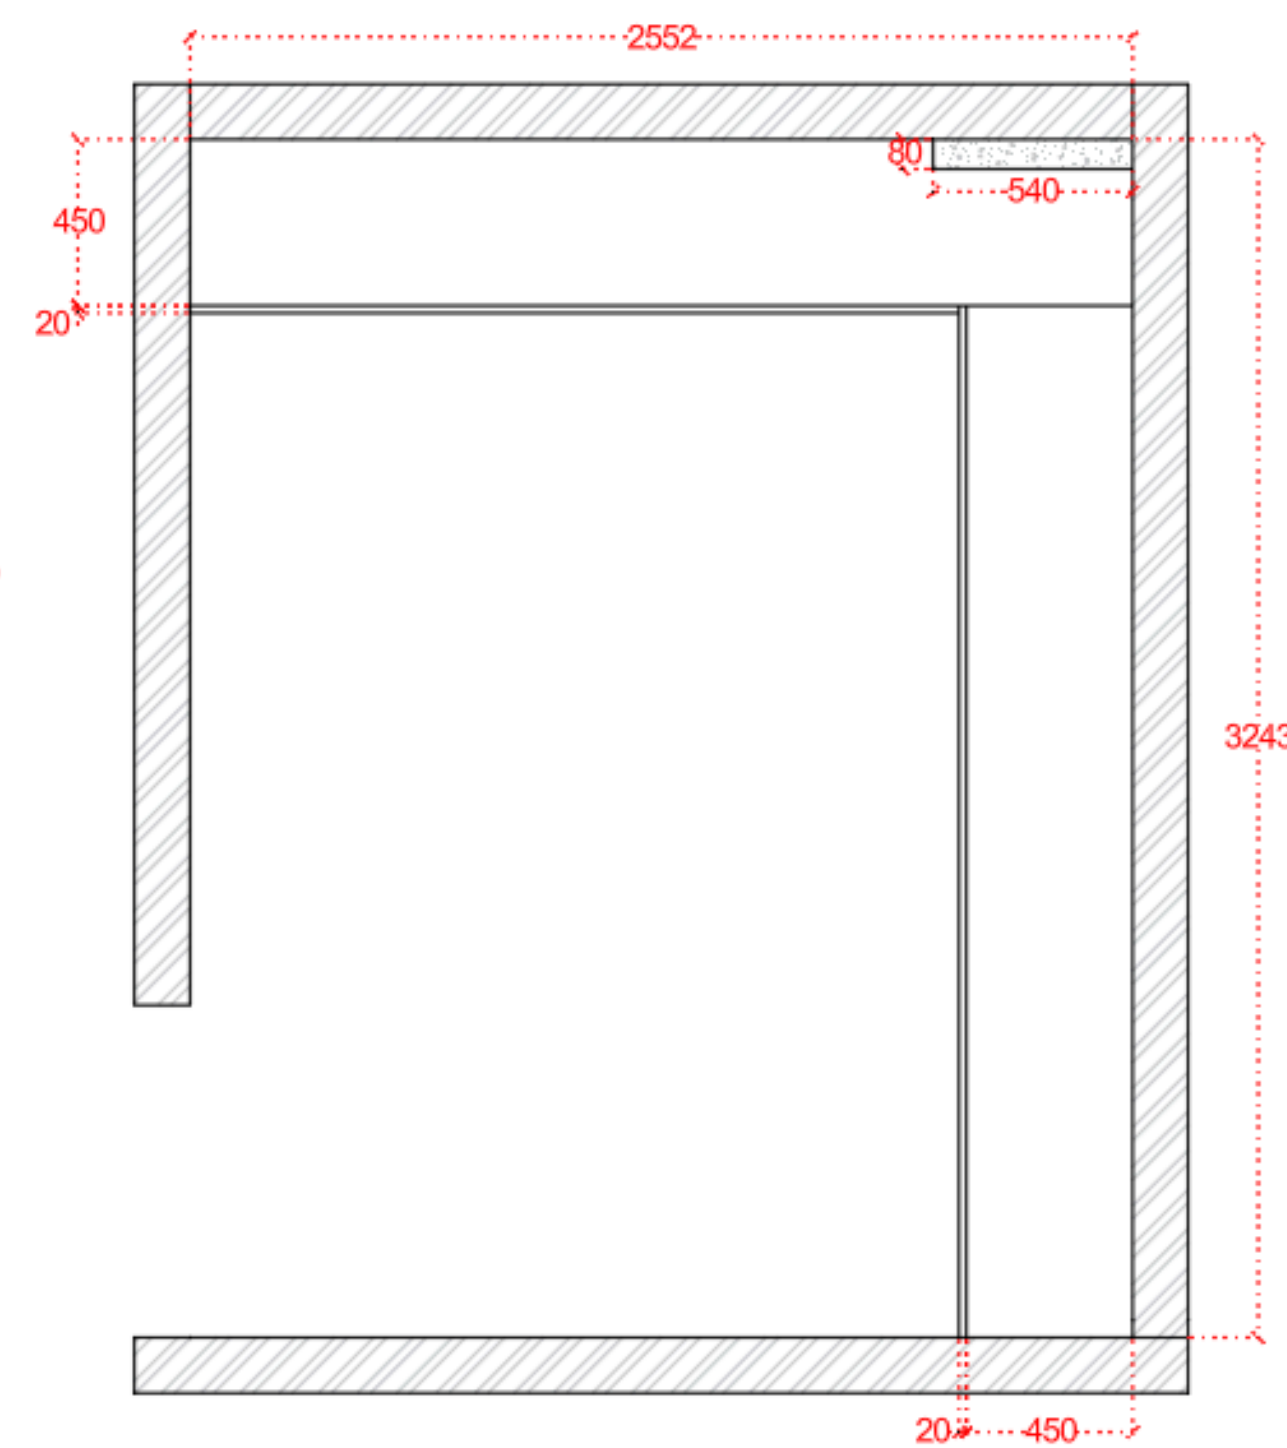


KITCHEN WALL-A EXTERNAL:

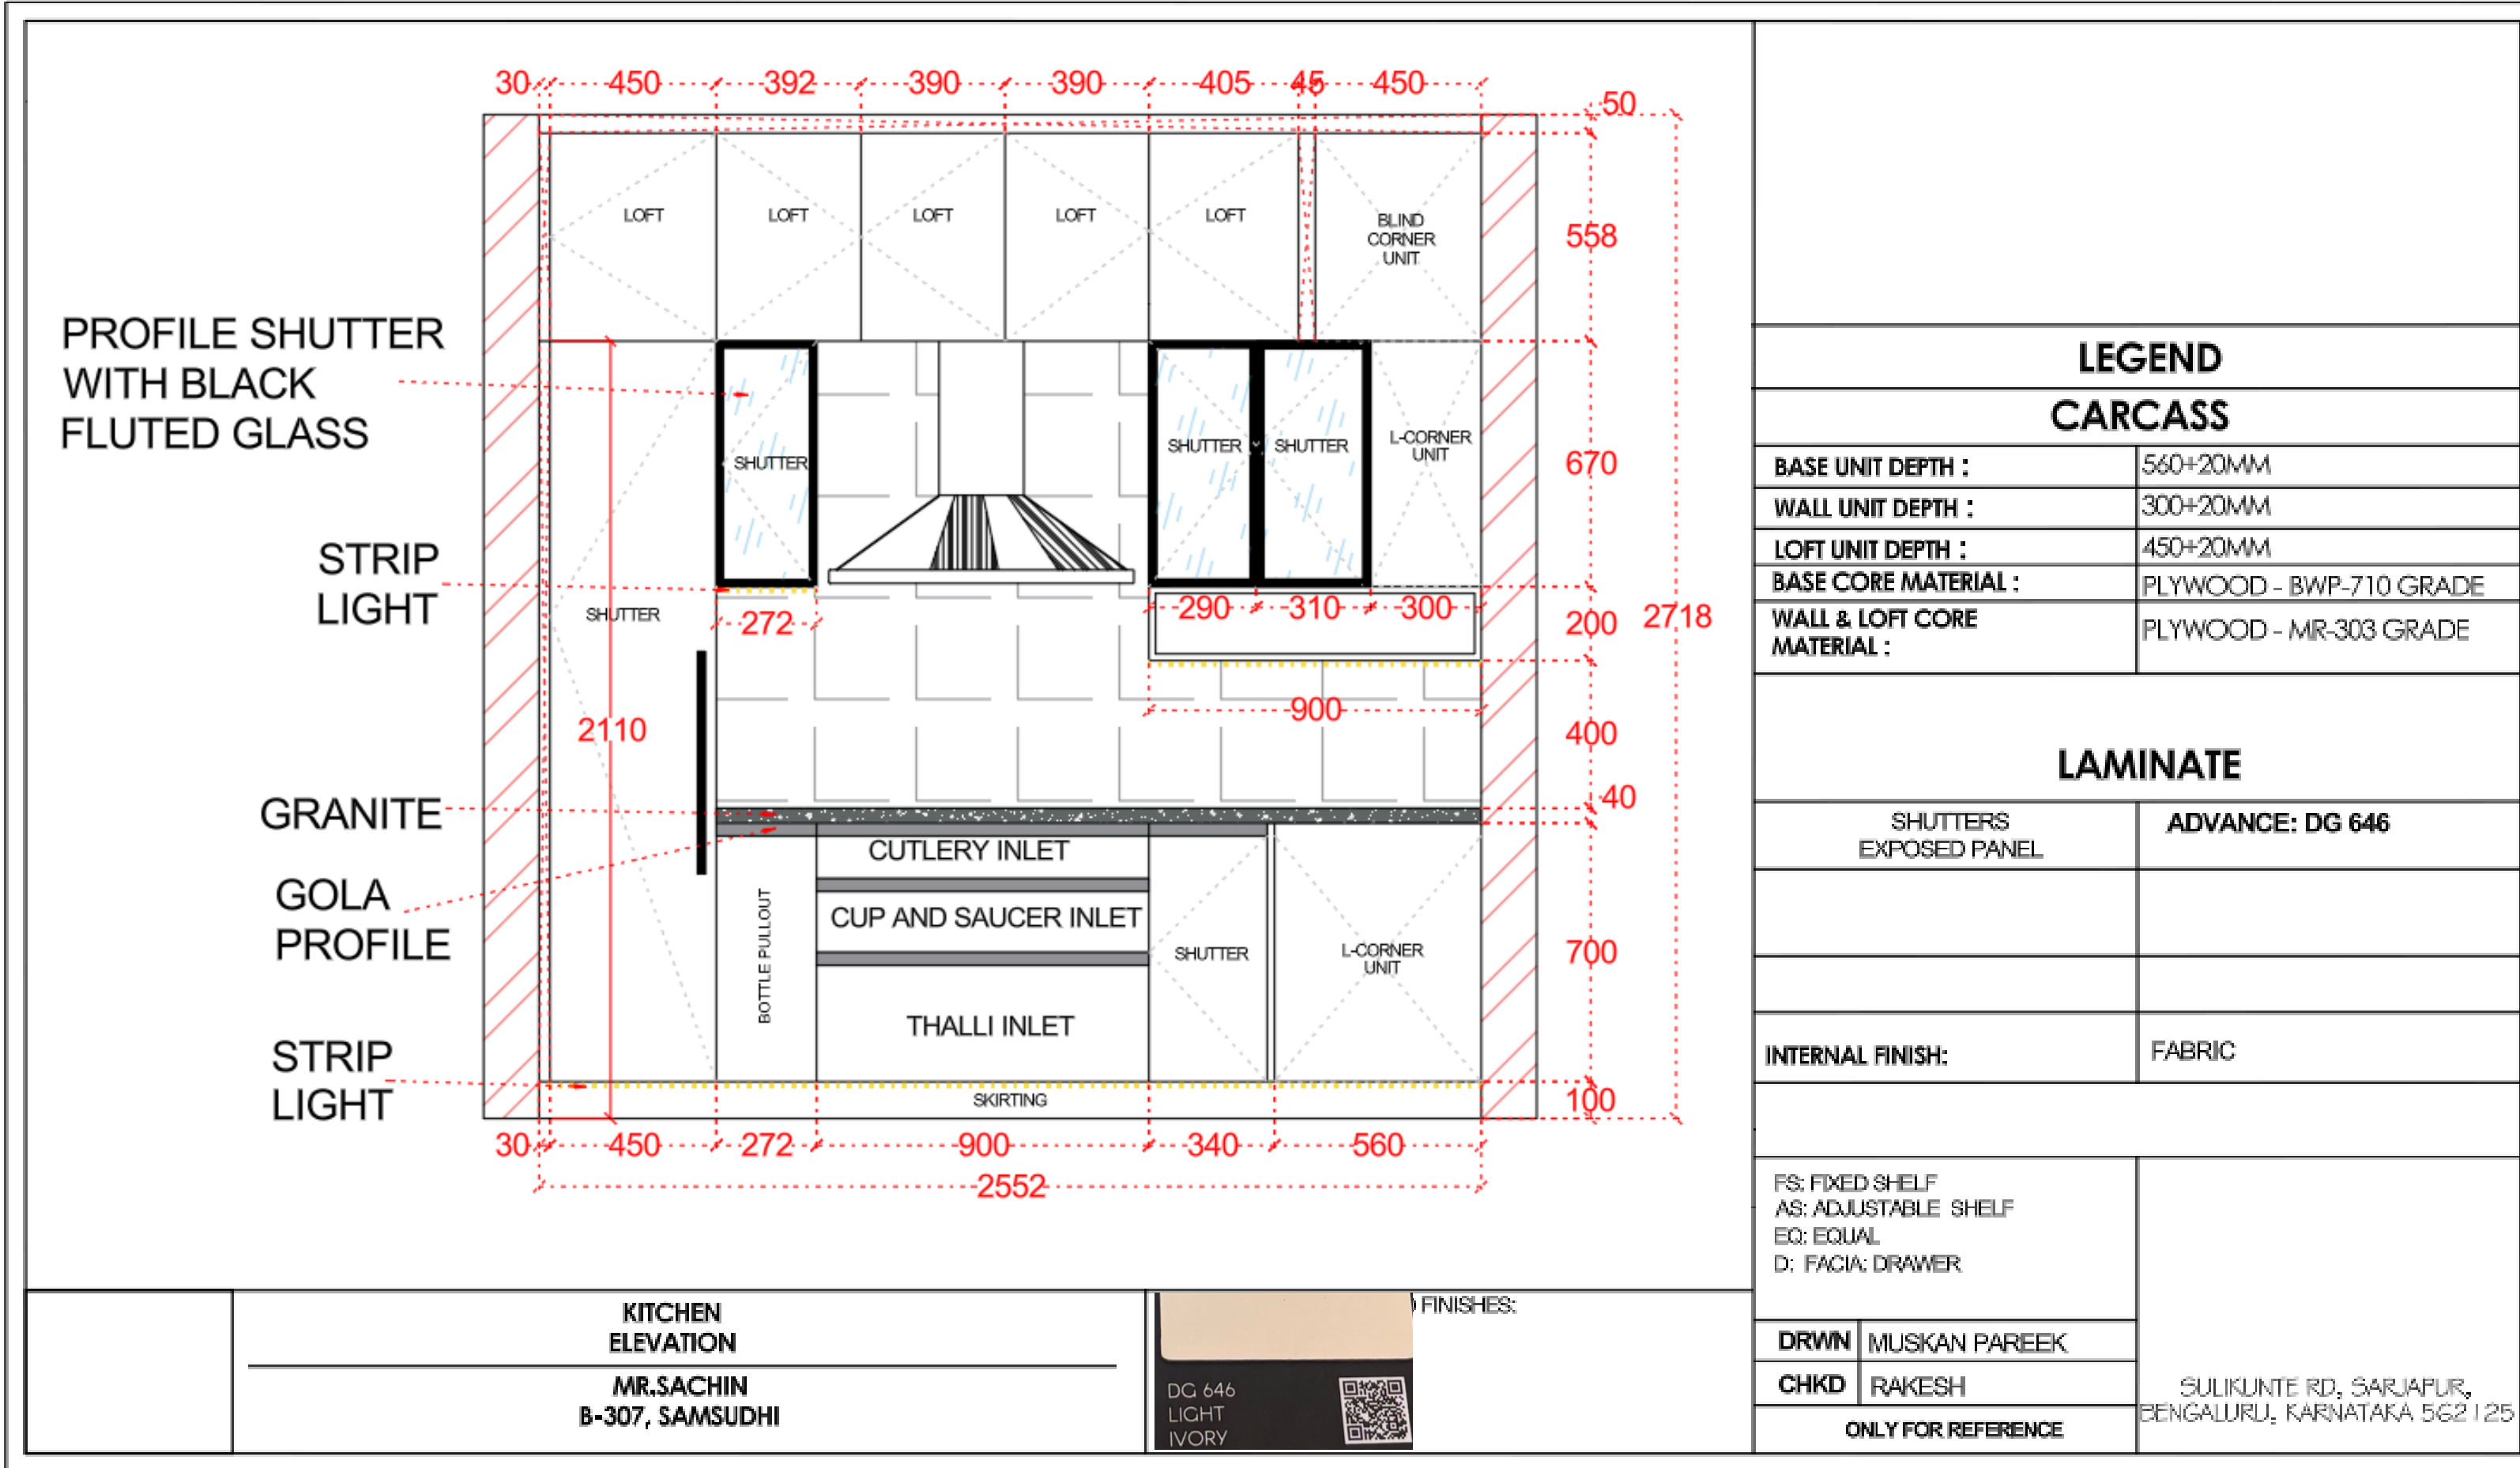


KITCHEN WALL-A INTERNAL:

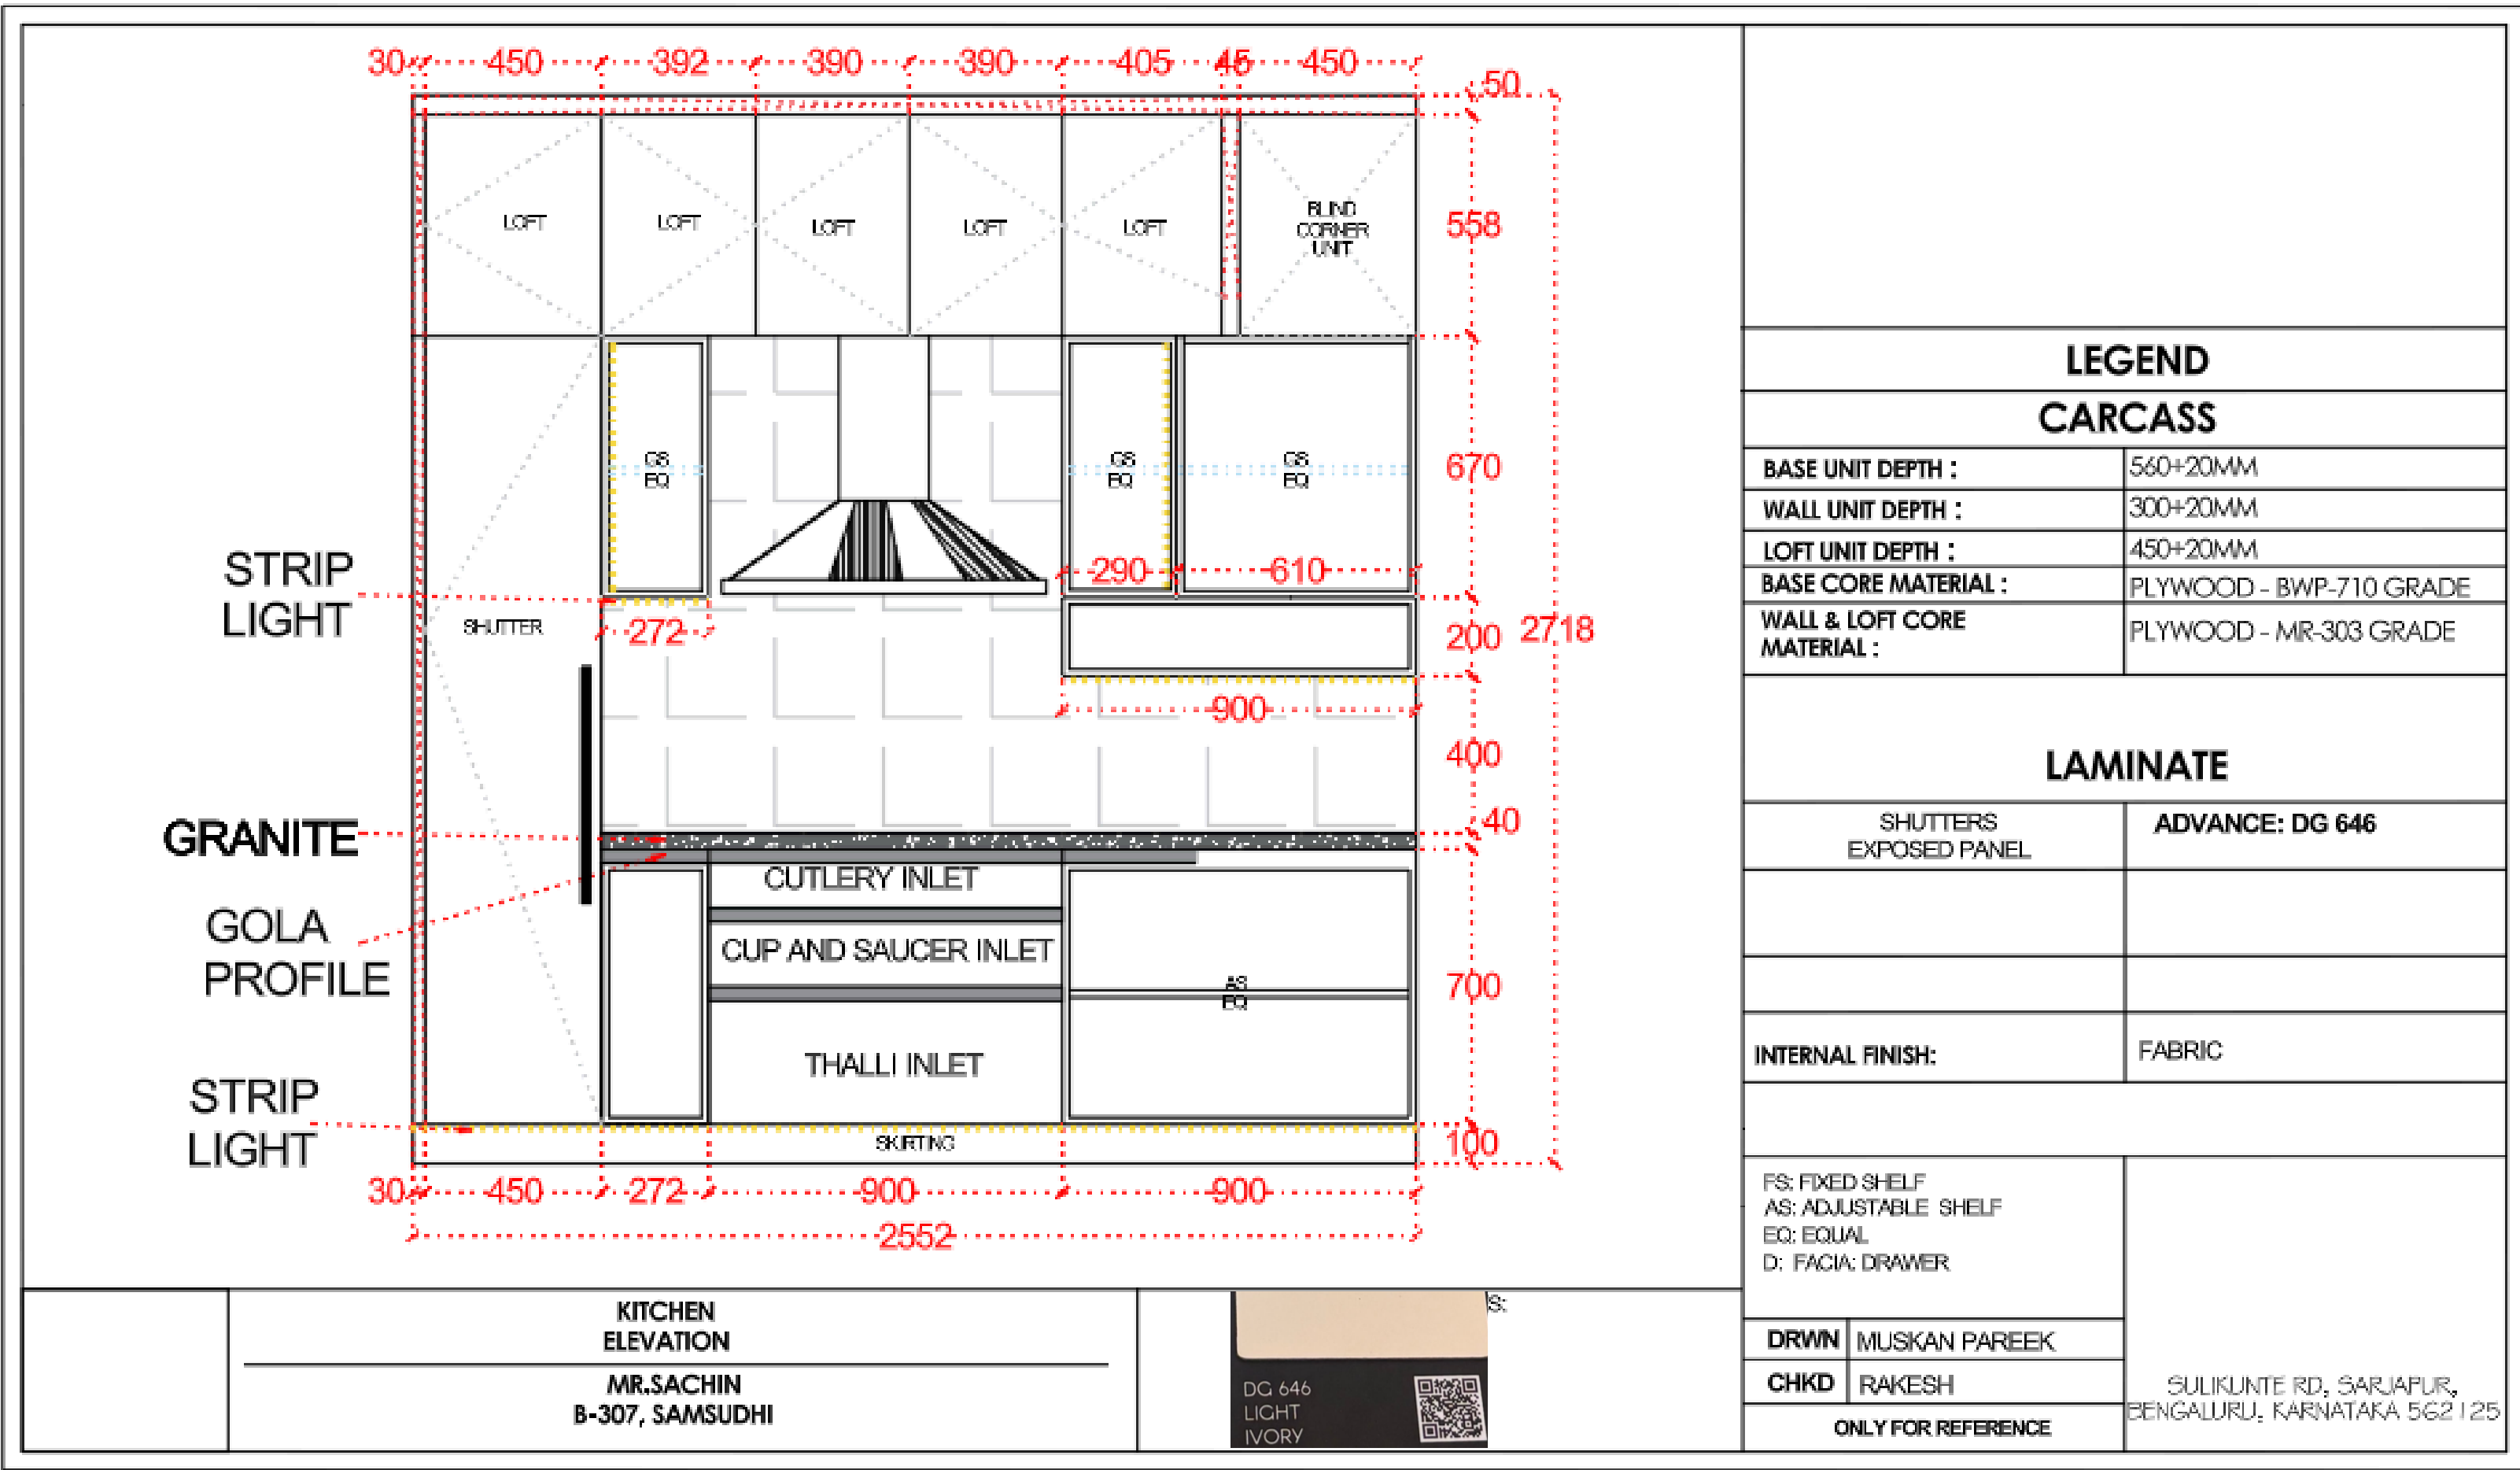

KITCHEN WALL-B EXTERNAL:

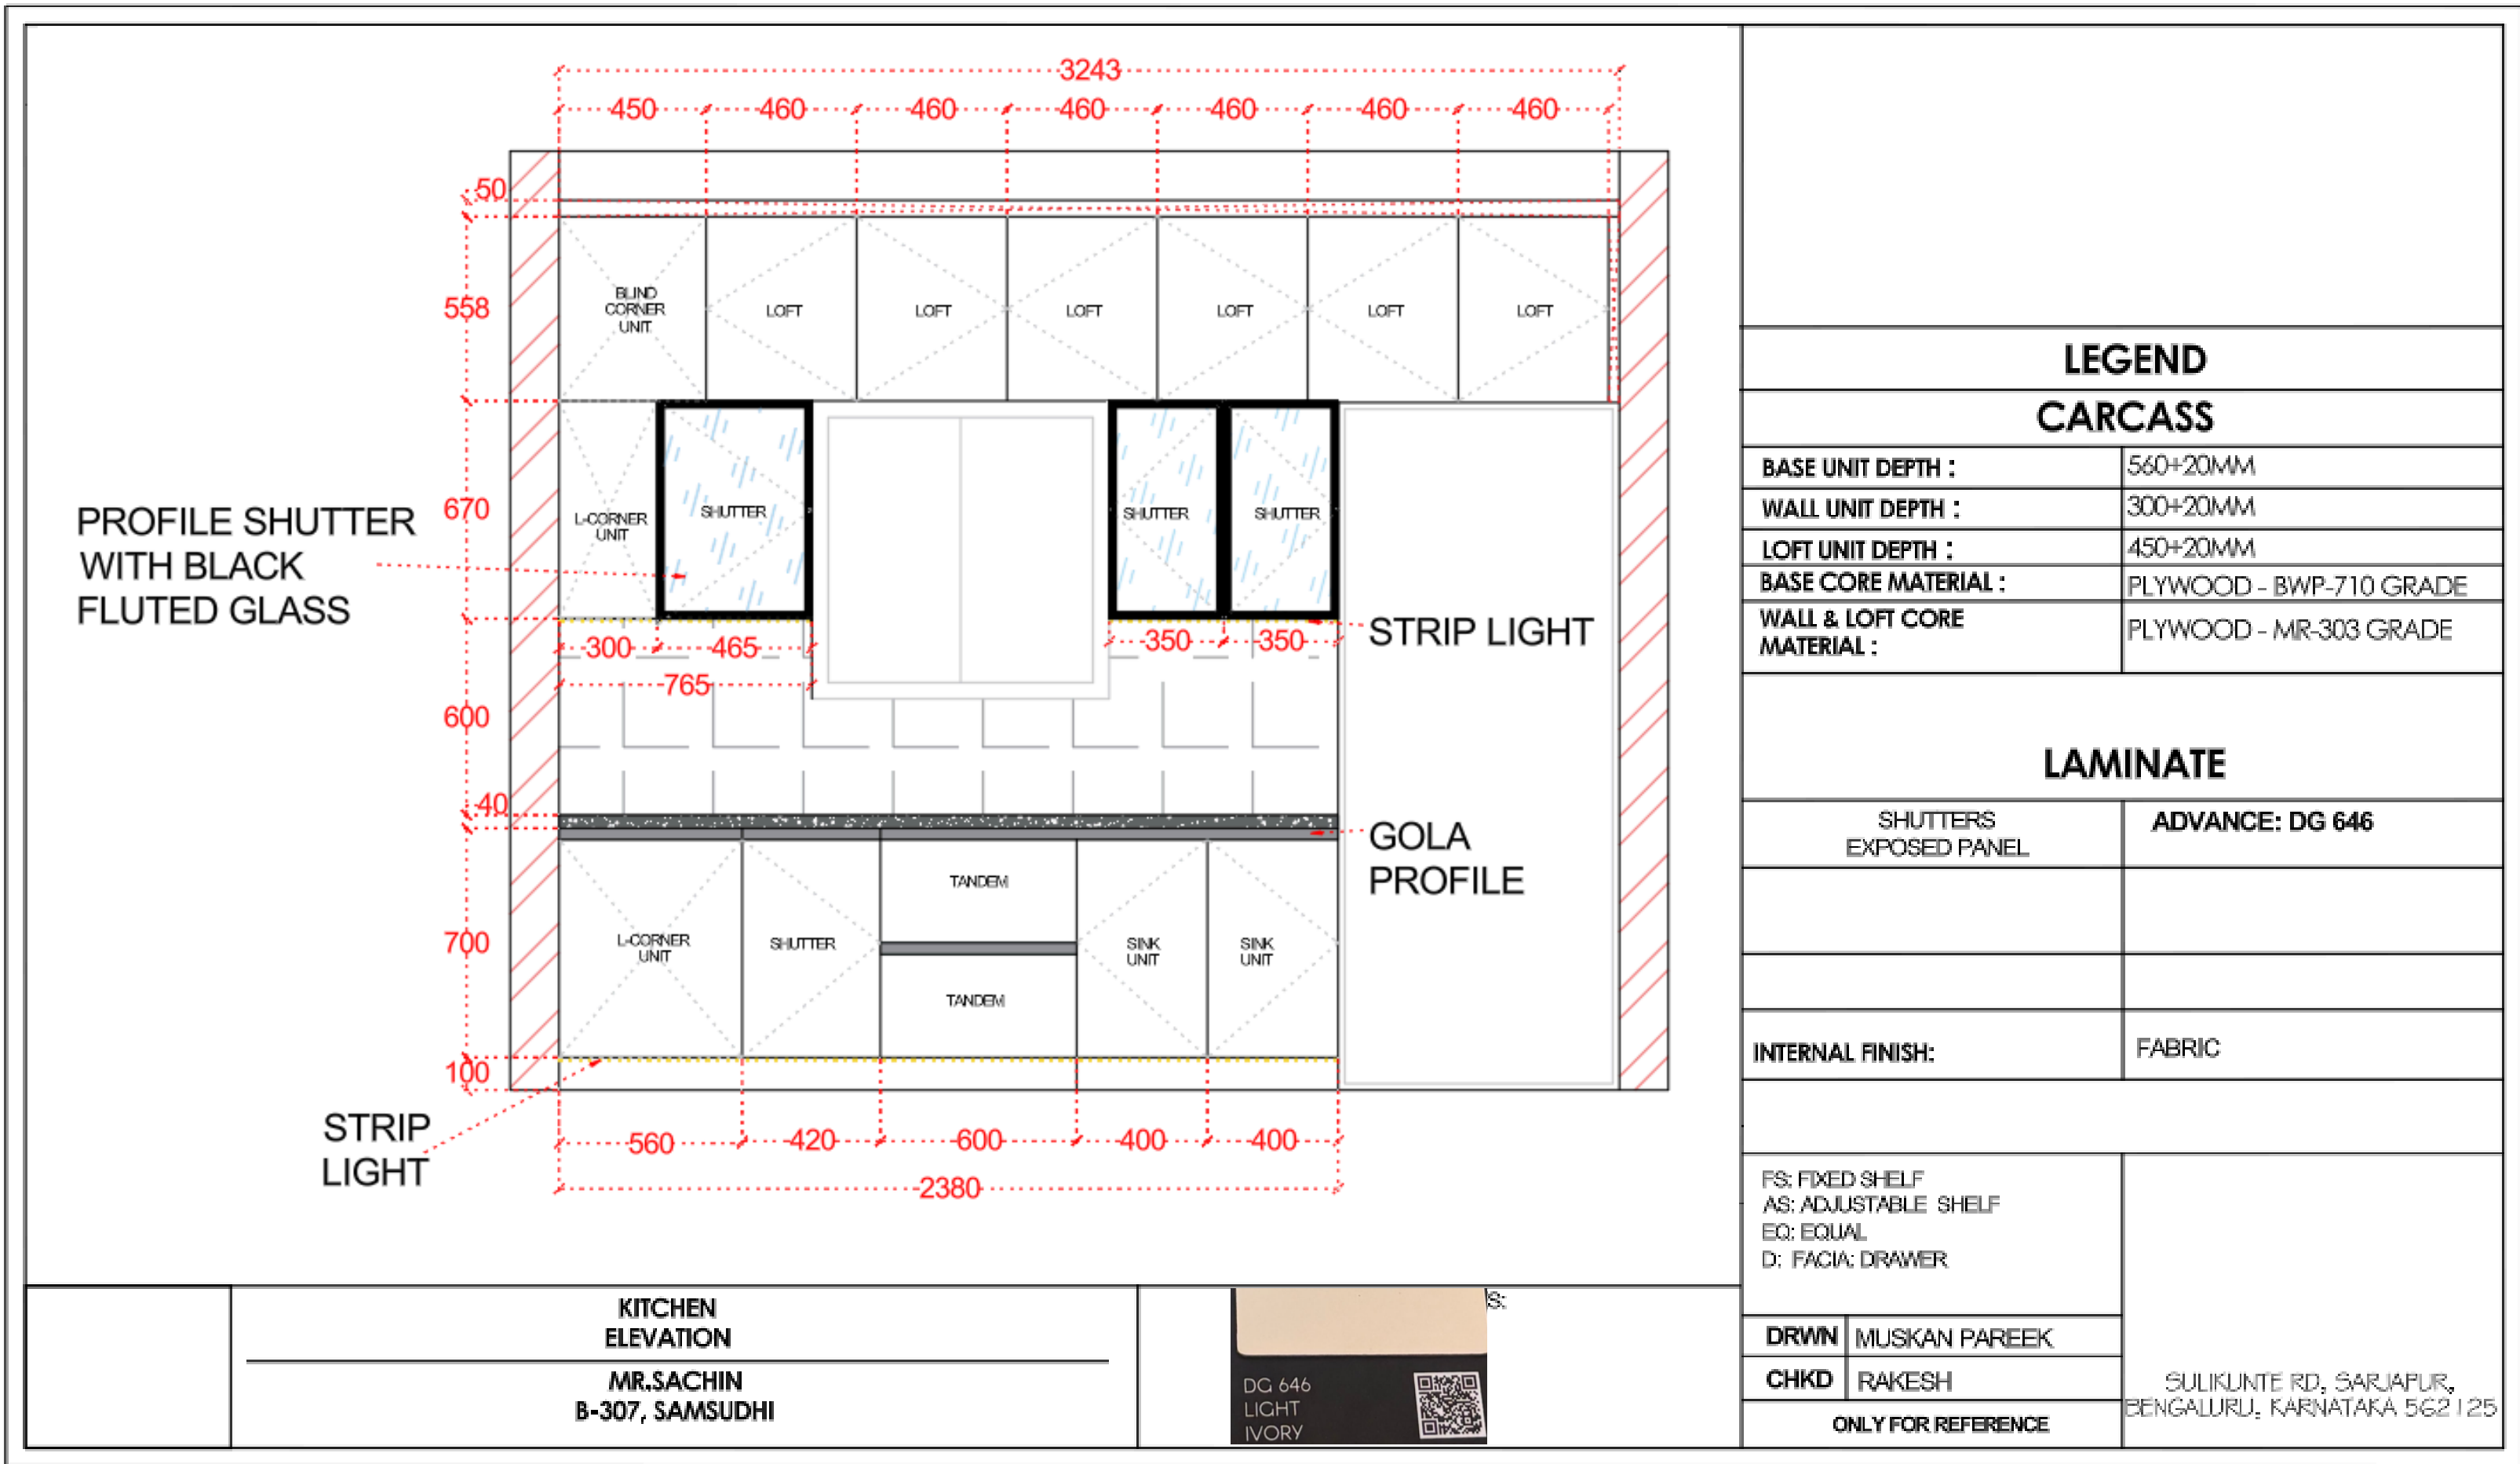

KITCHEN WALL-B INTERNAL:

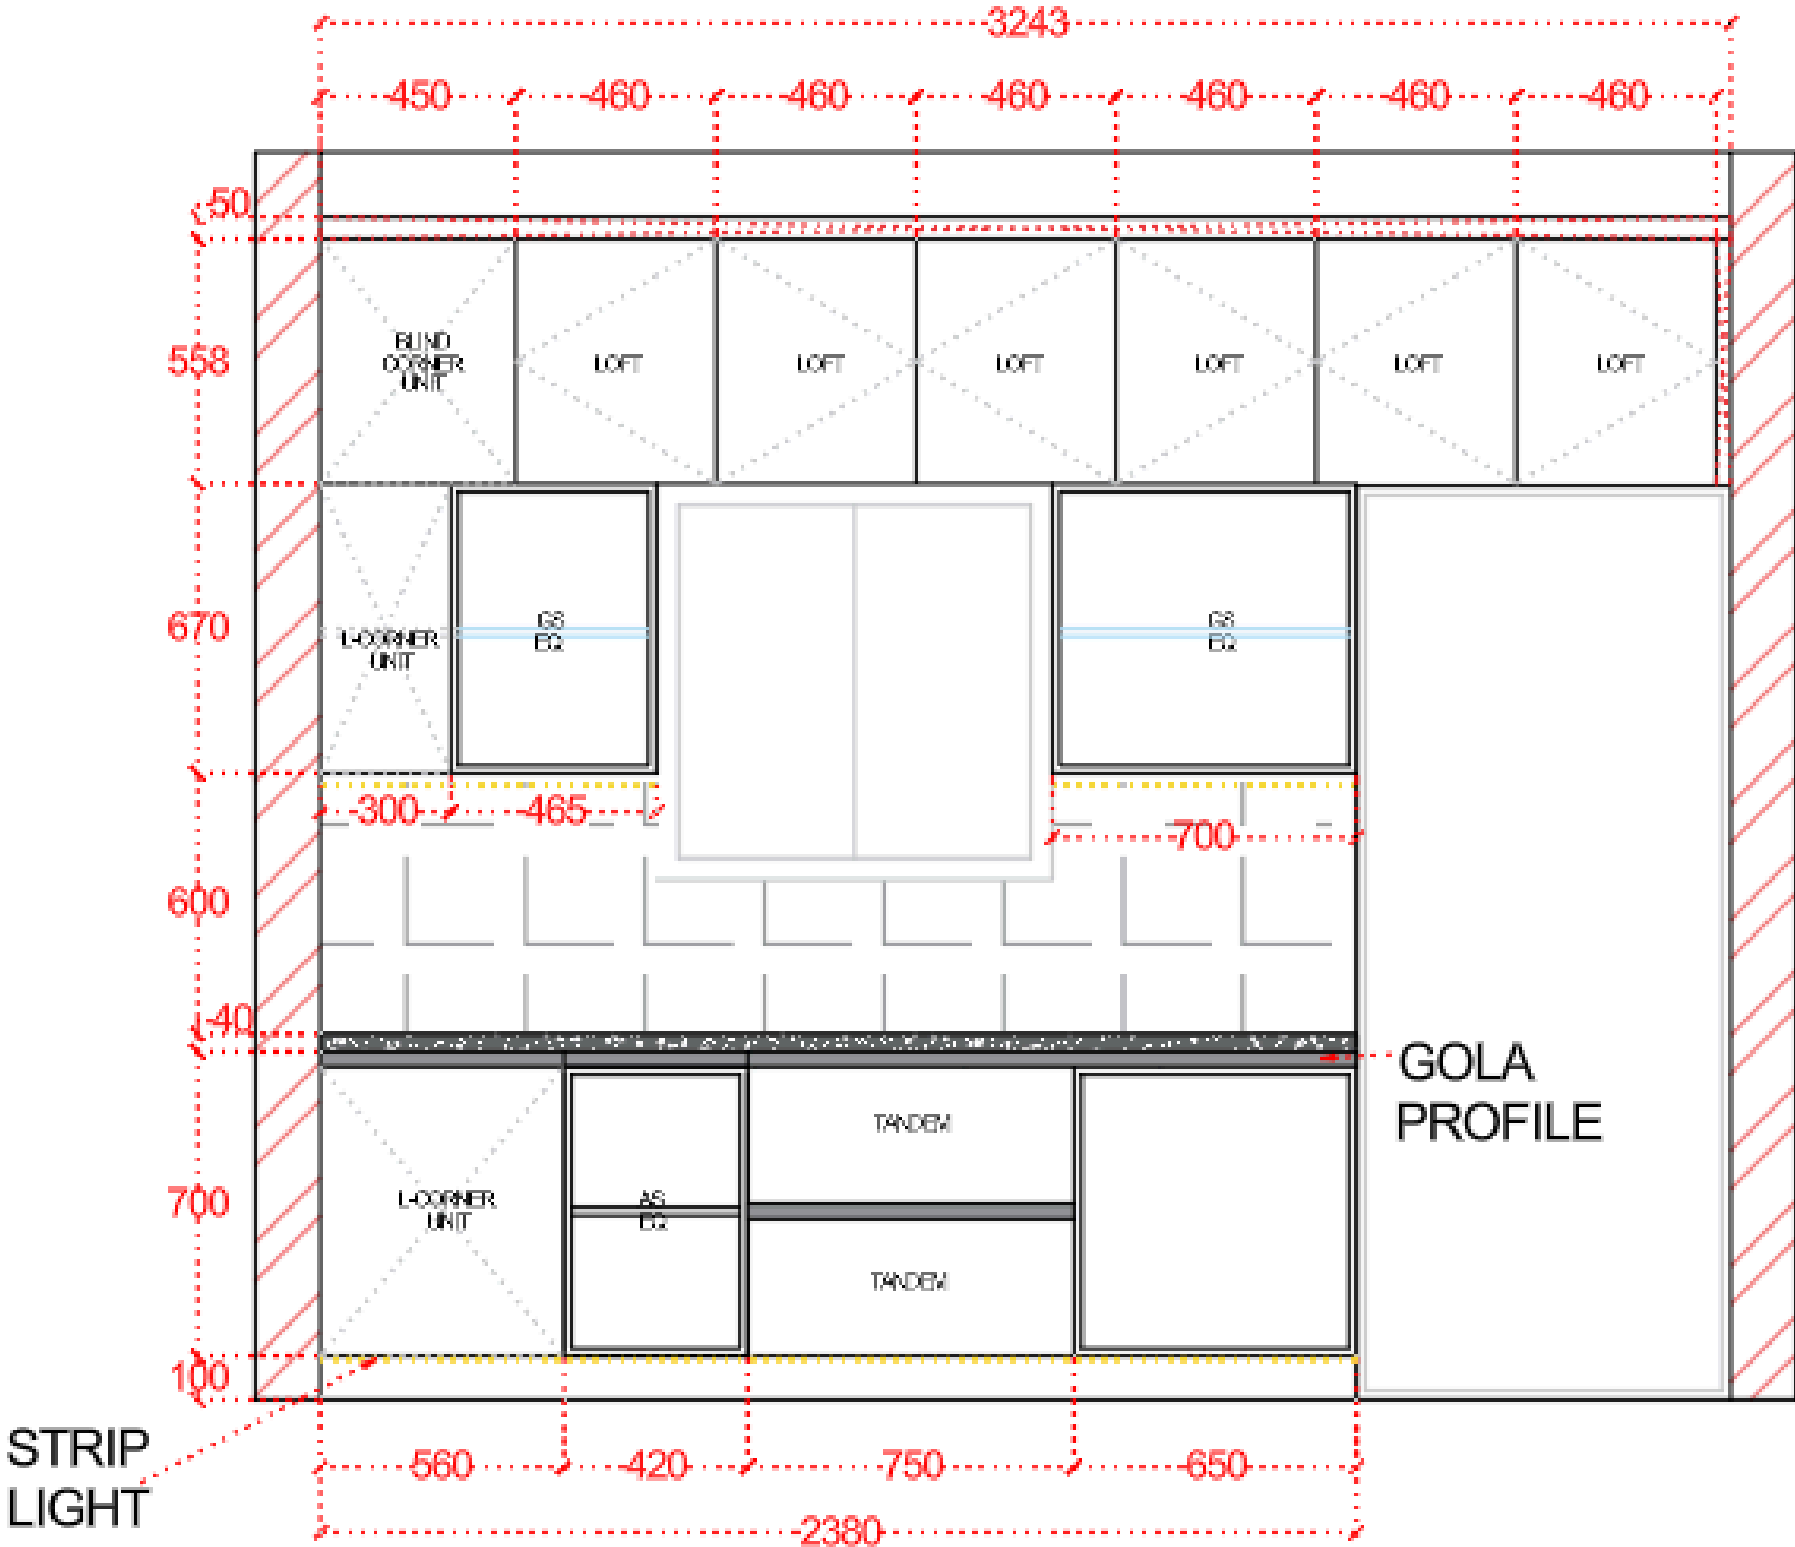

LEGEND

CARCASS

BASE UNIT DEPTH :	560+20MM
WALL UNIT DEPTH :	300+20MM
LOFT UNIT DEPTH :	450+20MM
BASE CORE MATERIAL :	PLYWOOD - BWP-710 GRADE
WALL & LOFT CORE MATERIAL :	PLYWOOD - MR-303 GRADE

LAMINATE

SHUTTERS EXPOSED PANEL	ADVANCE: DG 646
INTERNAL FINISH:	FABRIC

FS: FIXED SHELF
AS: ADJUSTABLE SHELF
EQ: EQUAL
D: FACIA; DRAWER

DRWN MUSKAN PAREEK
CHKD RAKESH

ONLY FOR REFERENCE

SULIKUNTE RD, SARJAPUR,
BENGALURU, KARNATAKA 562 125


KITCHEN
ELEVATION

MR.SACHIN
B-307, SAMSUDHI


DG 646
LIGHT
IVORY




PANTRY UNIT:

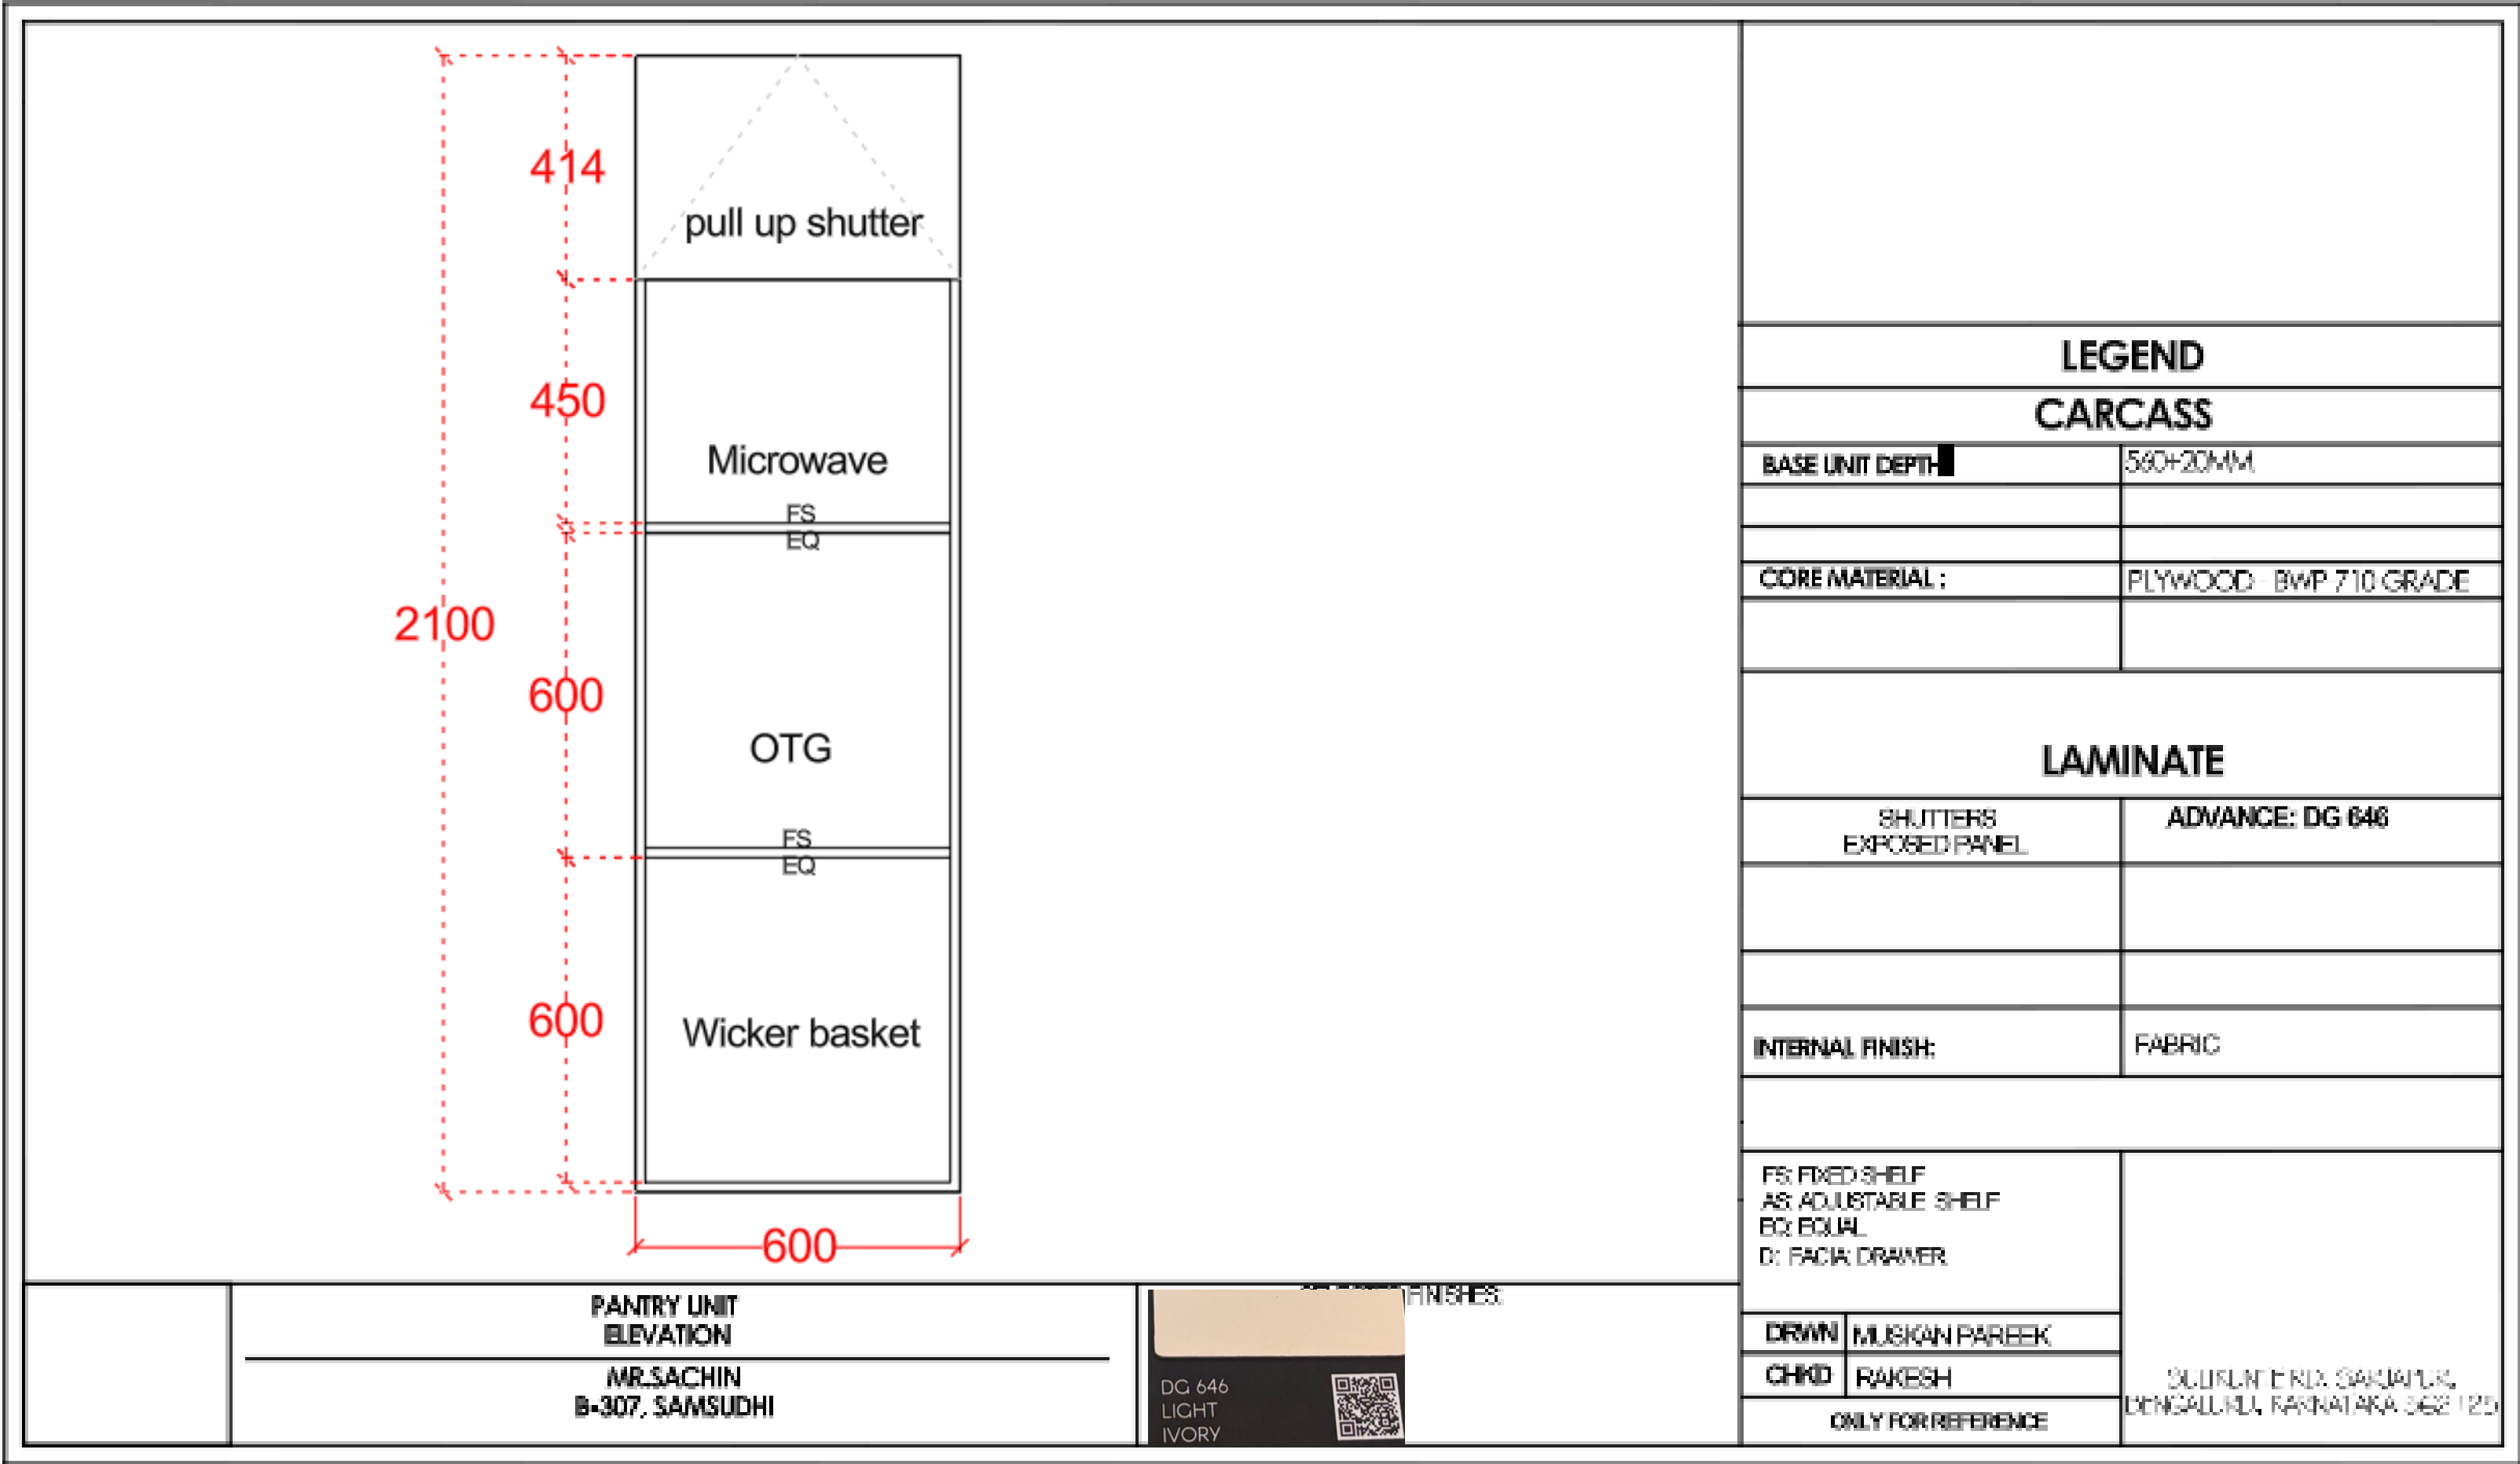


MBR WARDROBE EXTERNAL:

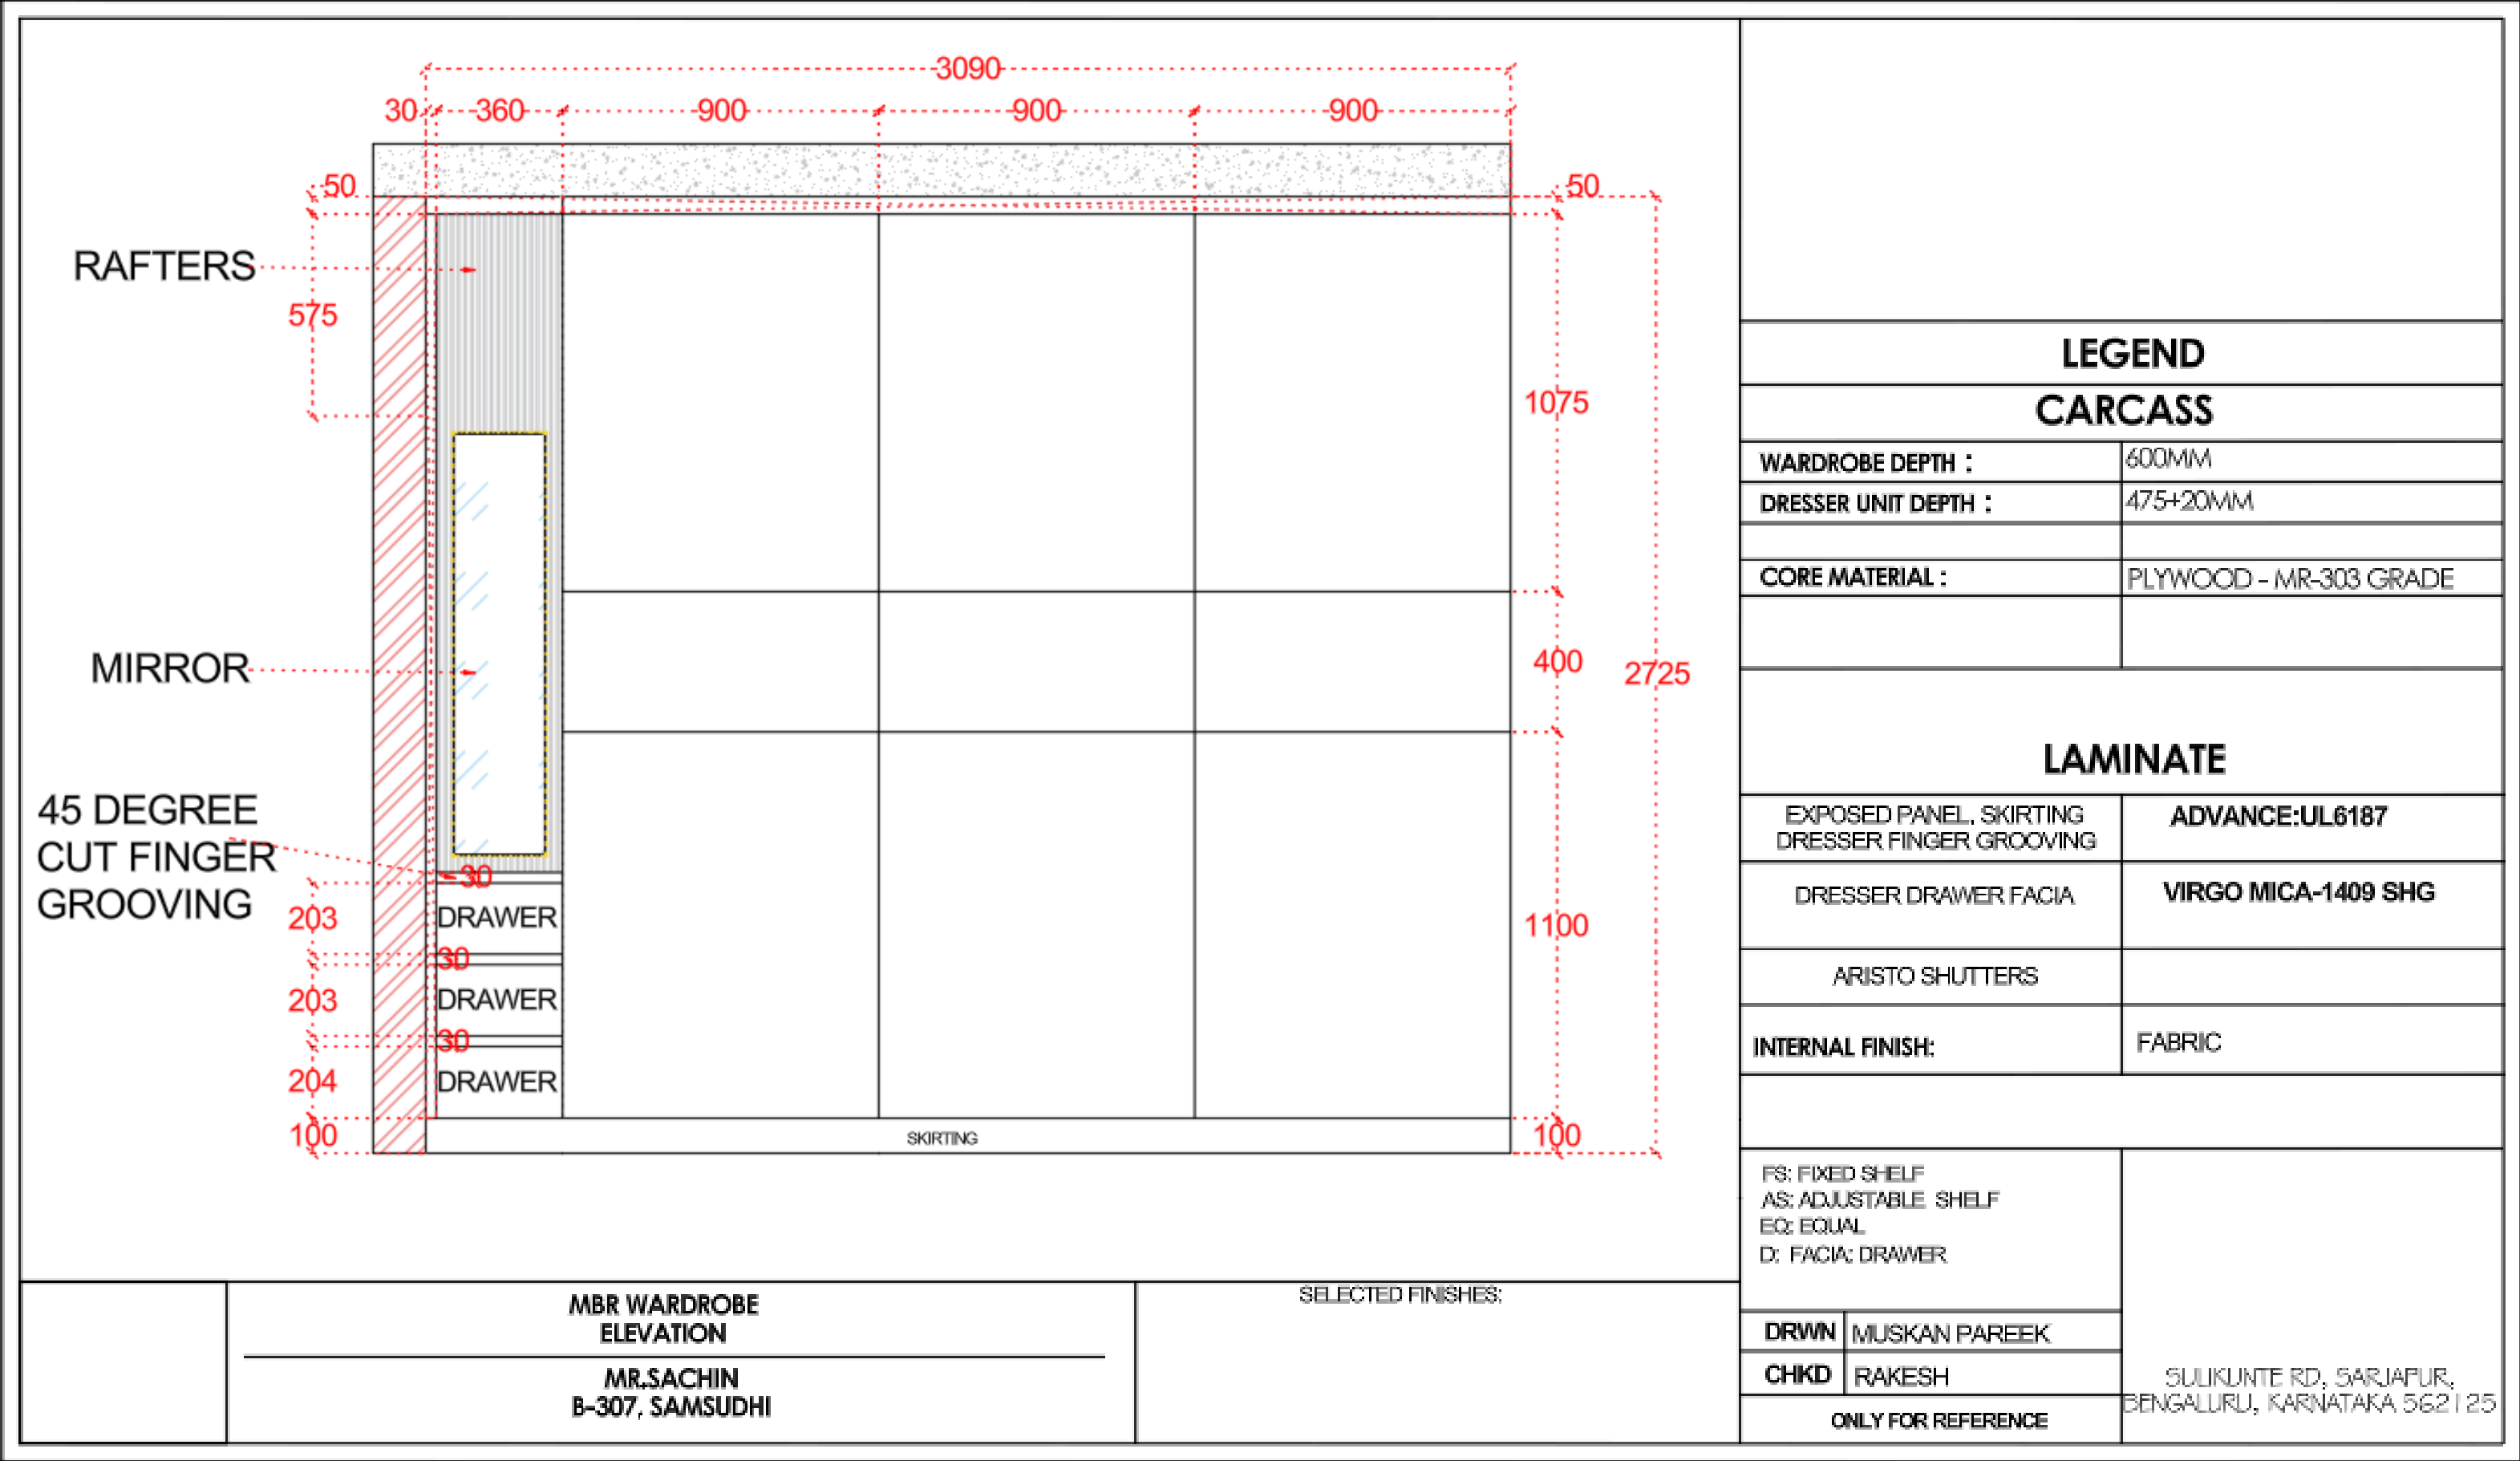


MBR WARDROBE INTERNAL:

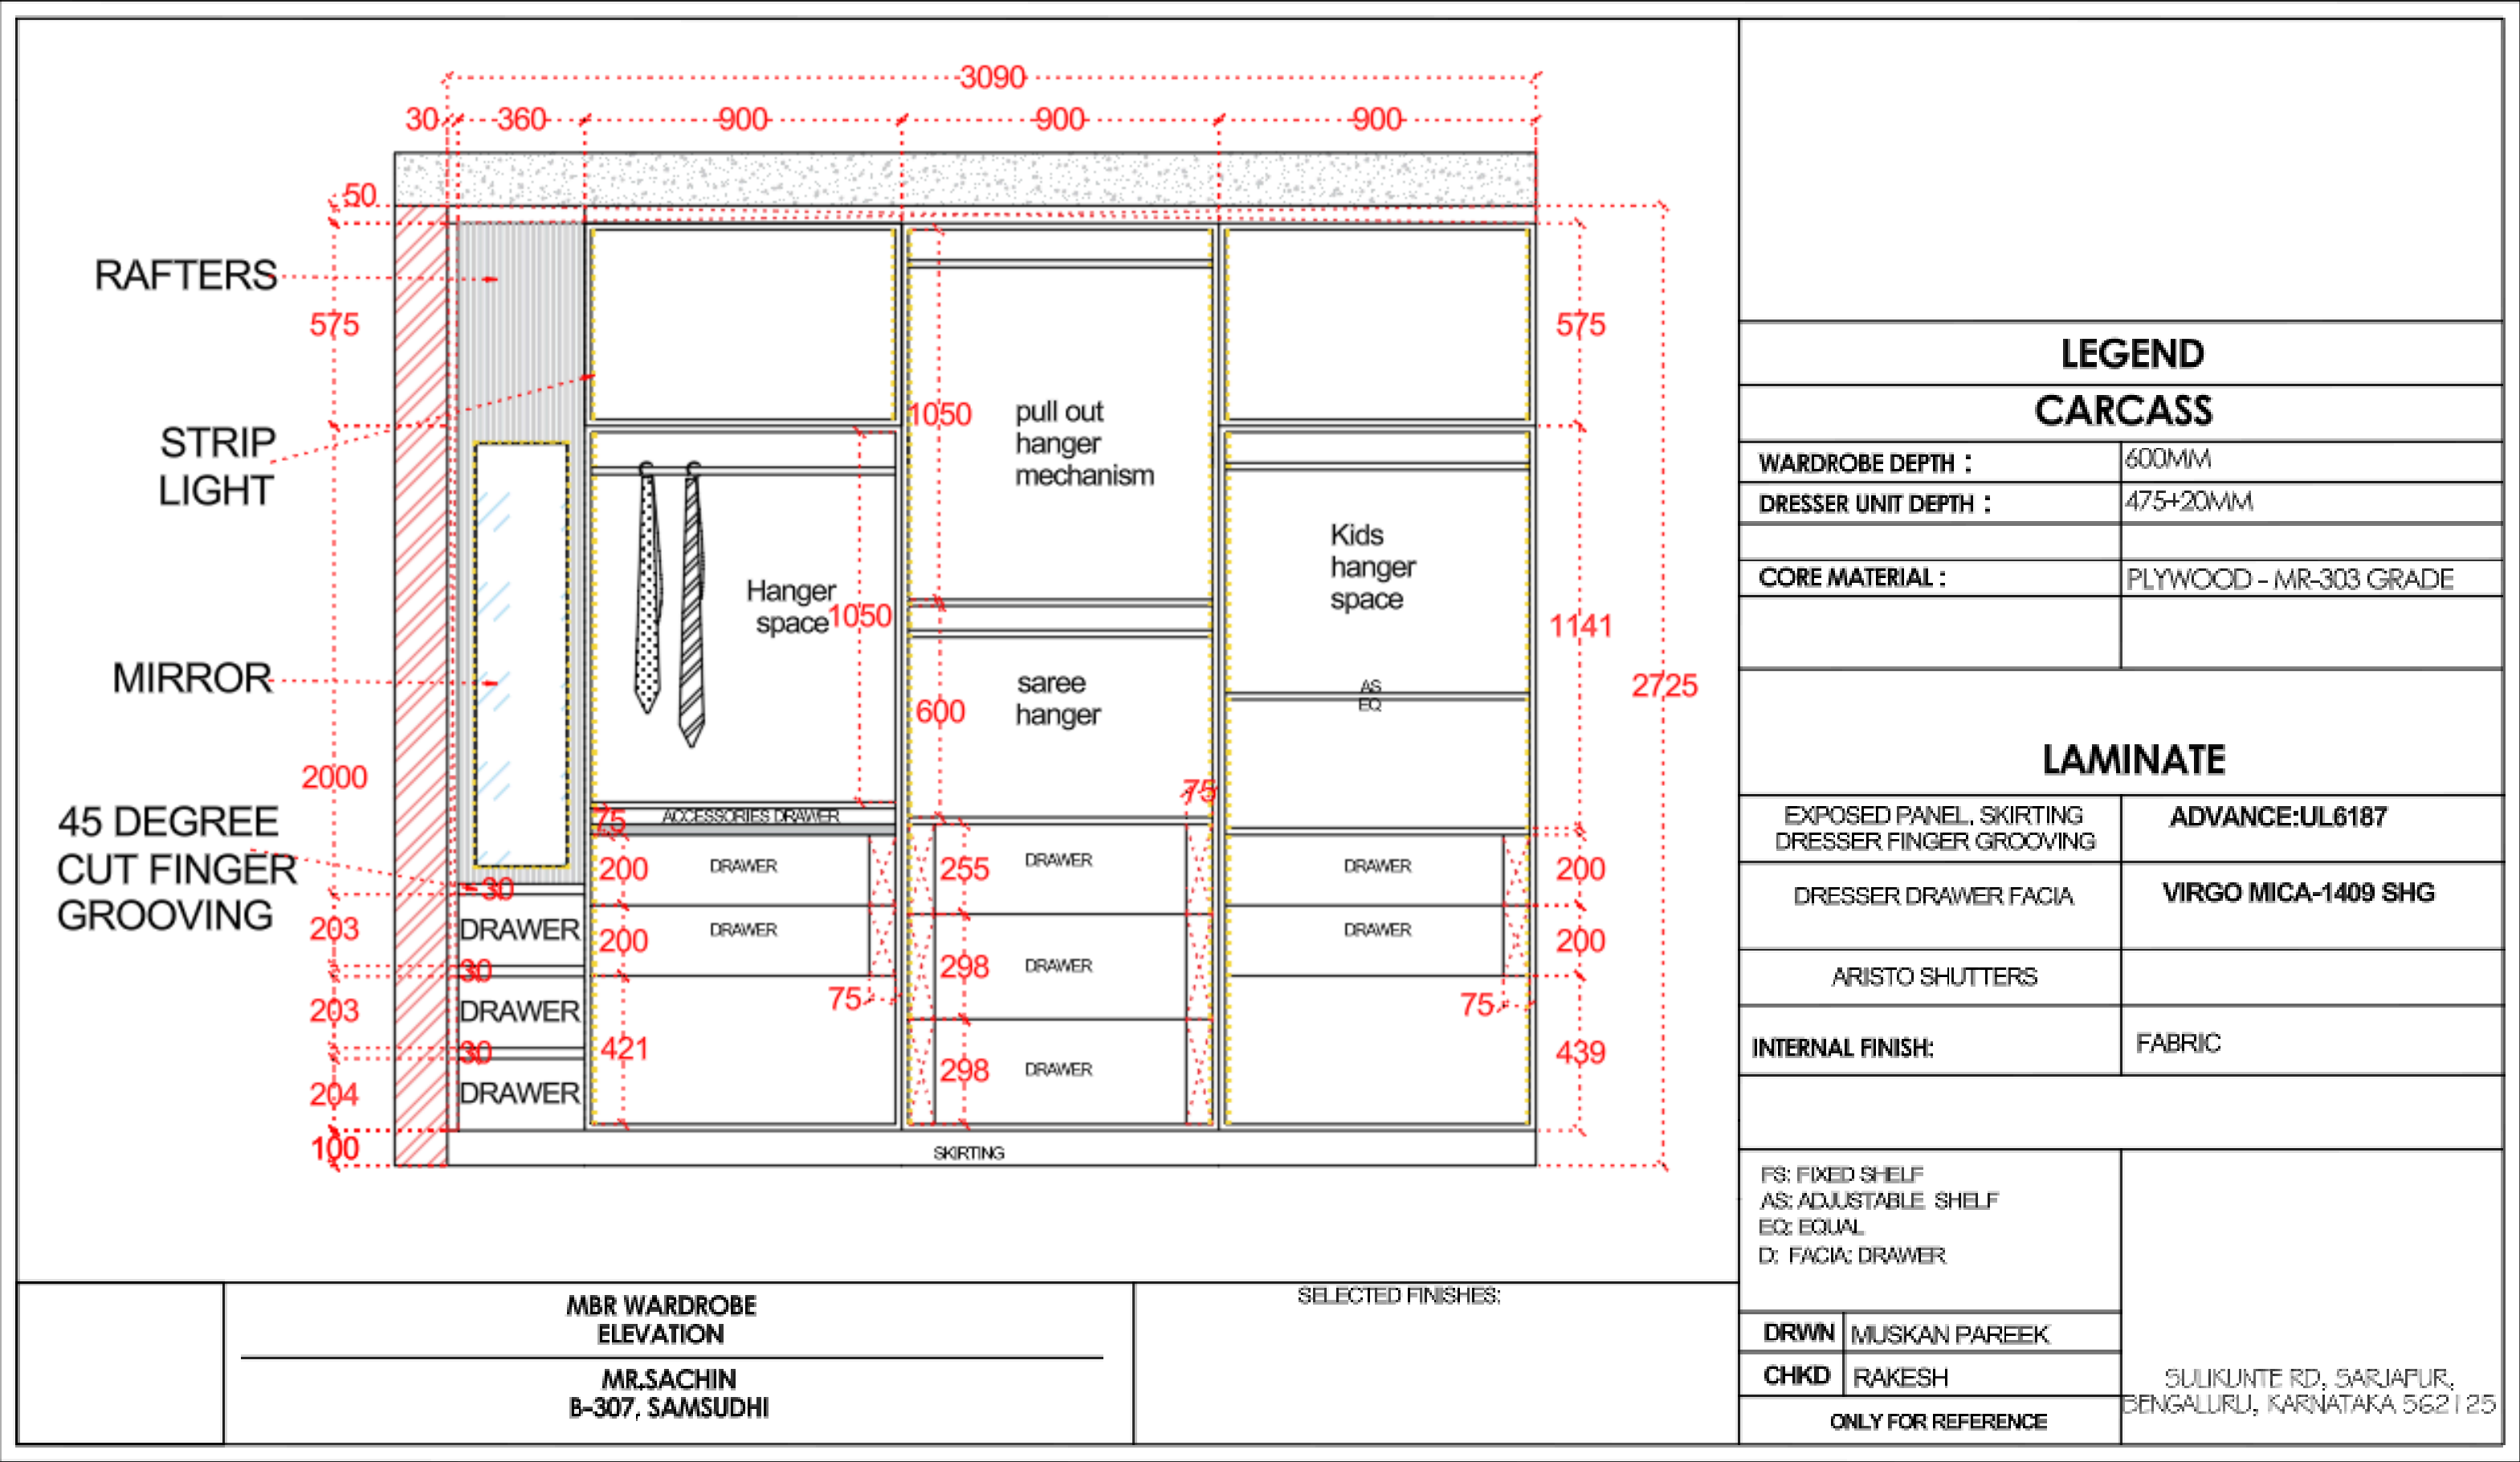


MBR STUDY TABLE:

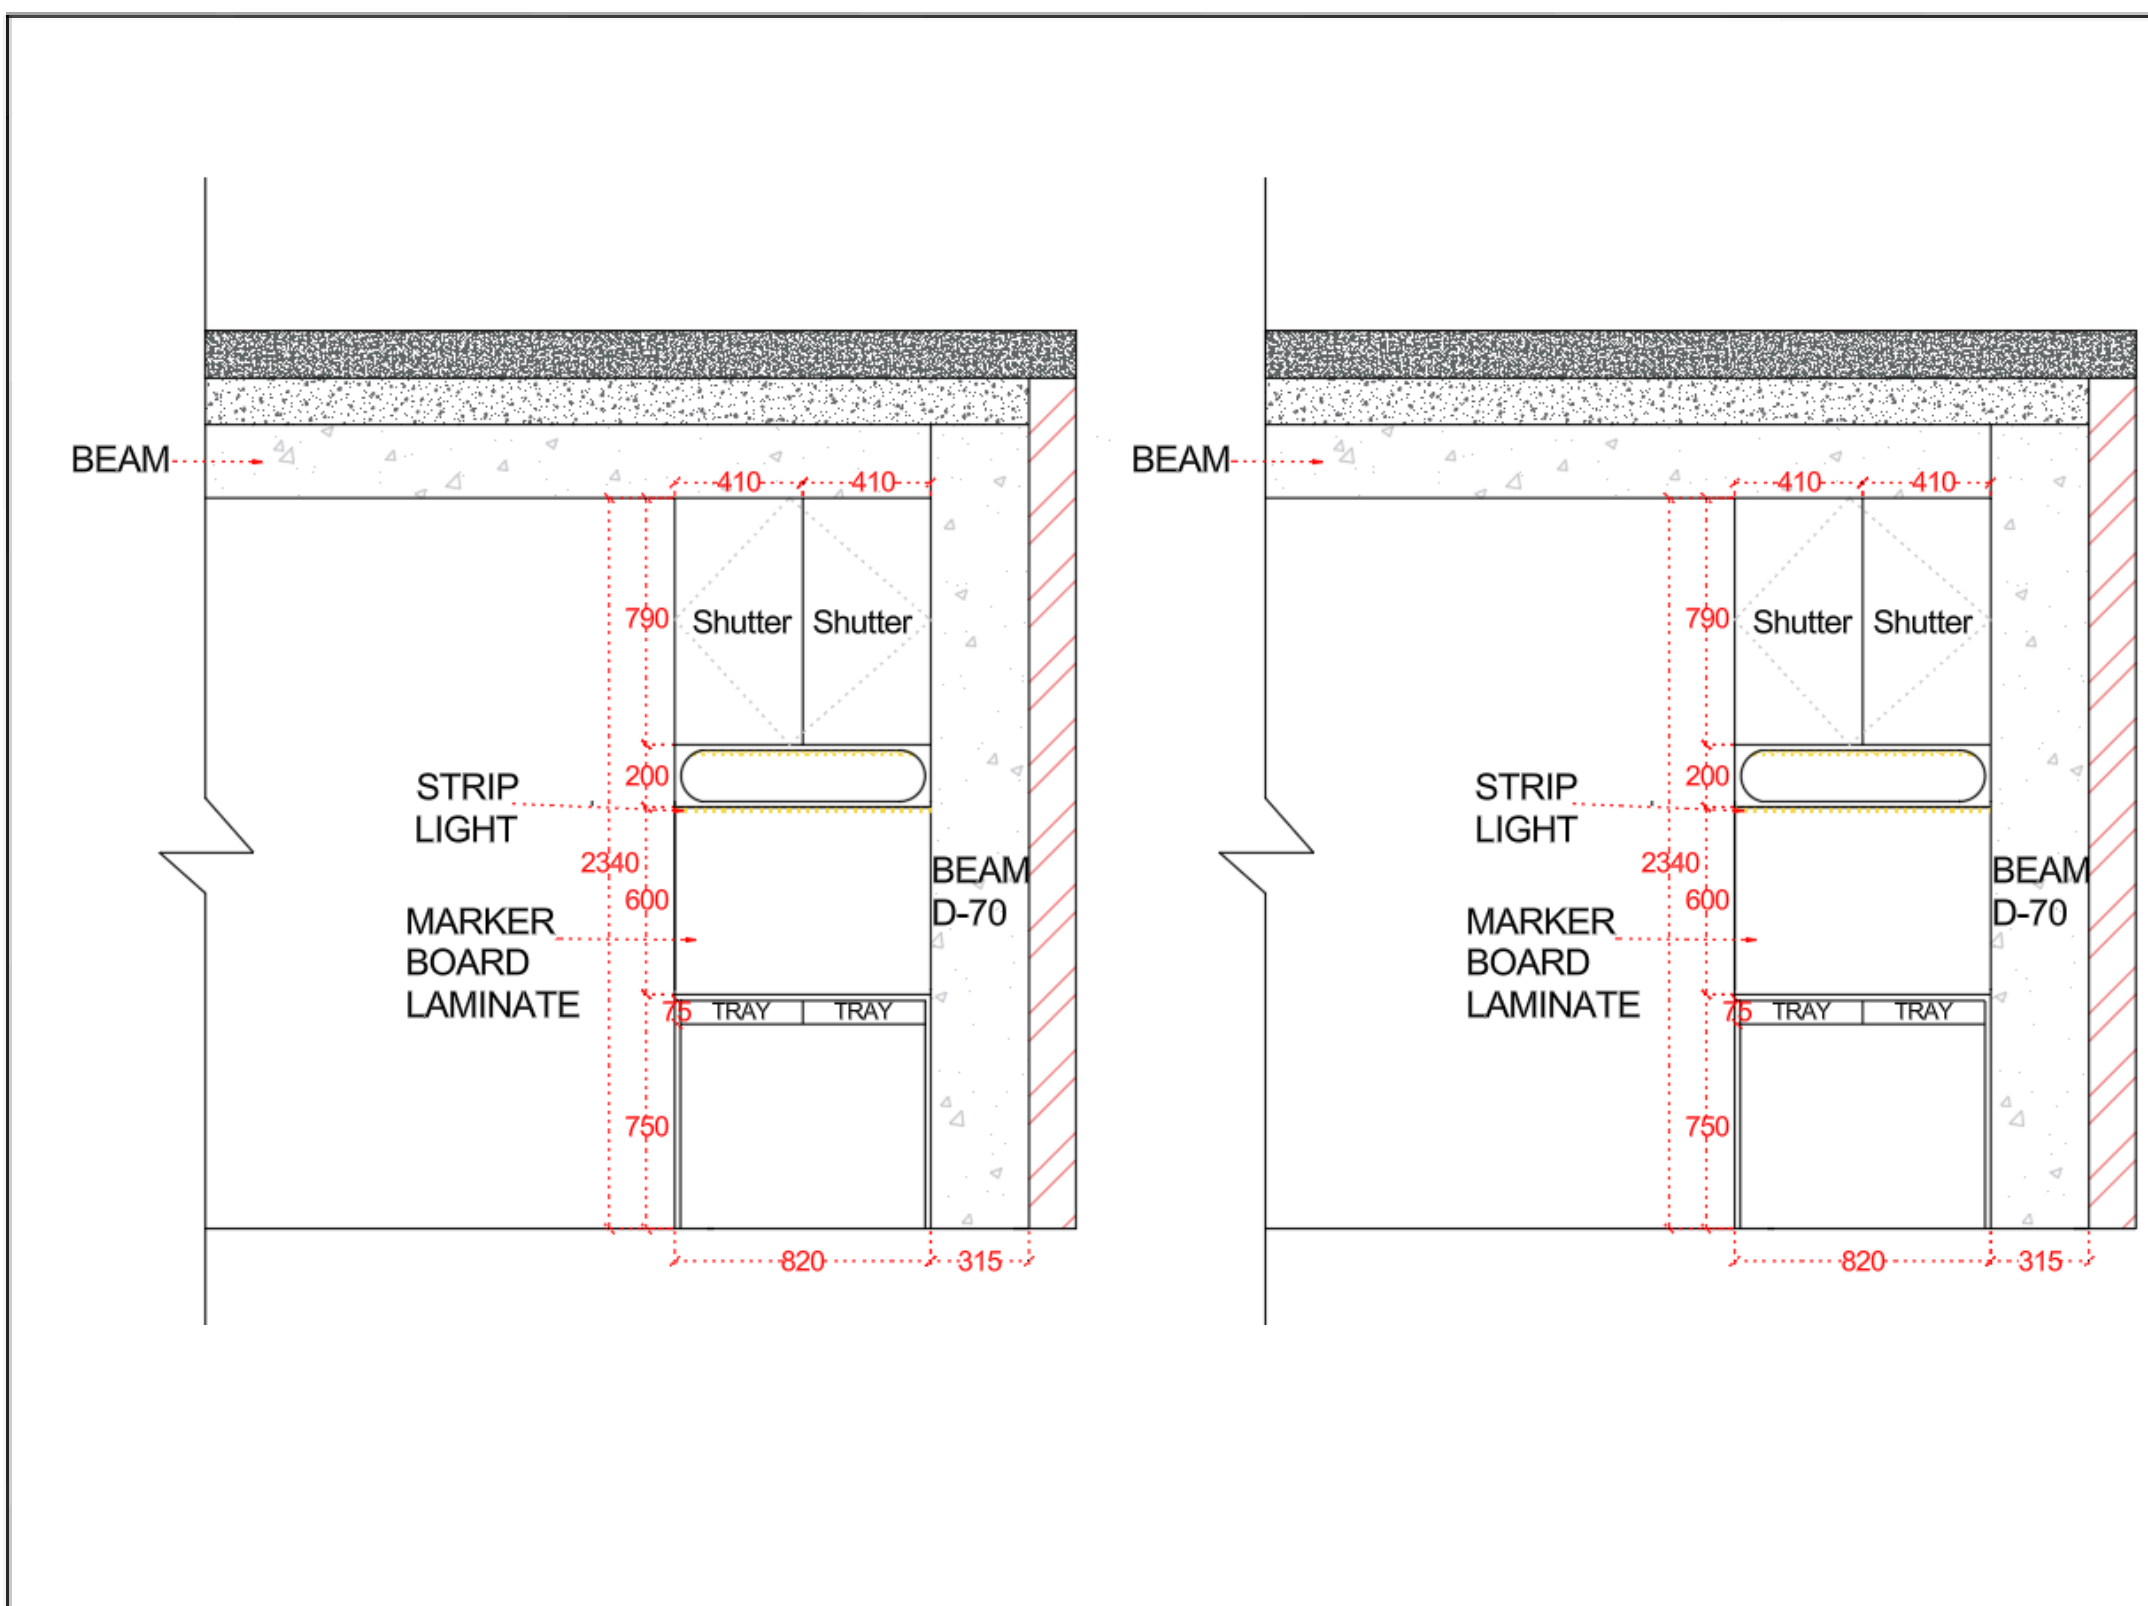		<table><tr><th colspan="2">LEGEND</th></tr><tr><th colspan="2">CARCASS</th></tr><tr><td>STUDY BASE UNIT DEPTH:</td><td>600MM</td></tr><tr><td>STUDY WALL UNIT DEPTH:</td><td>300+20MM</td></tr><tr><td>CORE MATERIAL :</td><td>PLYWOOD - MR-303 GRADE</td></tr><tr><th colspan="2">LAMINATE</th></tr><tr><td>EXPOSED PANEL, OPEN UNIT</td><td>ADVANCE:UL6187</td></tr><tr><td>WALL UNIT SHUTTERS & STUDY TABLE</td><td>VIRGO MICA-1409 SHG</td></tr><tr><td>INTERNAL FINISH:</td><td>FABRIC</td></tr><tr><td colspan="2">FS: FIXED SHELF AS: ADJUSTABLE SHELF EQ: EQUAL D: FACIA: DRAWER</td></tr><tr><td>DRWN</td><td>MUSKAN PAREEK</td></tr><tr><td>CHKD</td><td>RAKESH</td></tr><tr><td colspan="2">ONLY FOR REFERENCE</td></tr></table>		LEGEND		CARCASS		STUDY BASE UNIT DEPTH:	600MM	STUDY WALL UNIT DEPTH:	300+20MM	CORE MATERIAL :	PLYWOOD - MR-303 GRADE	LAMINATE		EXPOSED PANEL, OPEN UNIT	ADVANCE:UL6187	WALL UNIT SHUTTERS & STUDY TABLE	VIRGO MICA-1409 SHG	INTERNAL FINISH:	FABRIC	FS: FIXED SHELF AS: ADJUSTABLE SHELF EQ: EQUAL D: FACIA: DRAWER		DRWN	MUSKAN PAREEK	CHKD	RAKESH	ONLY FOR REFERENCE	
LEGEND																													
CARCASS																													
STUDY BASE UNIT DEPTH:	600MM																												
STUDY WALL UNIT DEPTH:	300+20MM																												
CORE MATERIAL :	PLYWOOD - MR-303 GRADE																												
LAMINATE																													
EXPOSED PANEL, OPEN UNIT	ADVANCE:UL6187																												
WALL UNIT SHUTTERS & STUDY TABLE	VIRGO MICA-1409 SHG																												
INTERNAL FINISH:	FABRIC																												
FS: FIXED SHELF AS: ADJUSTABLE SHELF EQ: EQUAL D: FACIA: DRAWER																													
DRWN	MUSKAN PAREEK																												
CHKD	RAKESH																												
ONLY FOR REFERENCE																													
MBR STUDY ELEVATION MR.SACHIN B-307, SAMSUDHI		SELECTED FINISHES: SULIKUNTE RD, SARJAPUR, BENGALURU, KARNATAKA 562125																											

MBR VANITY:

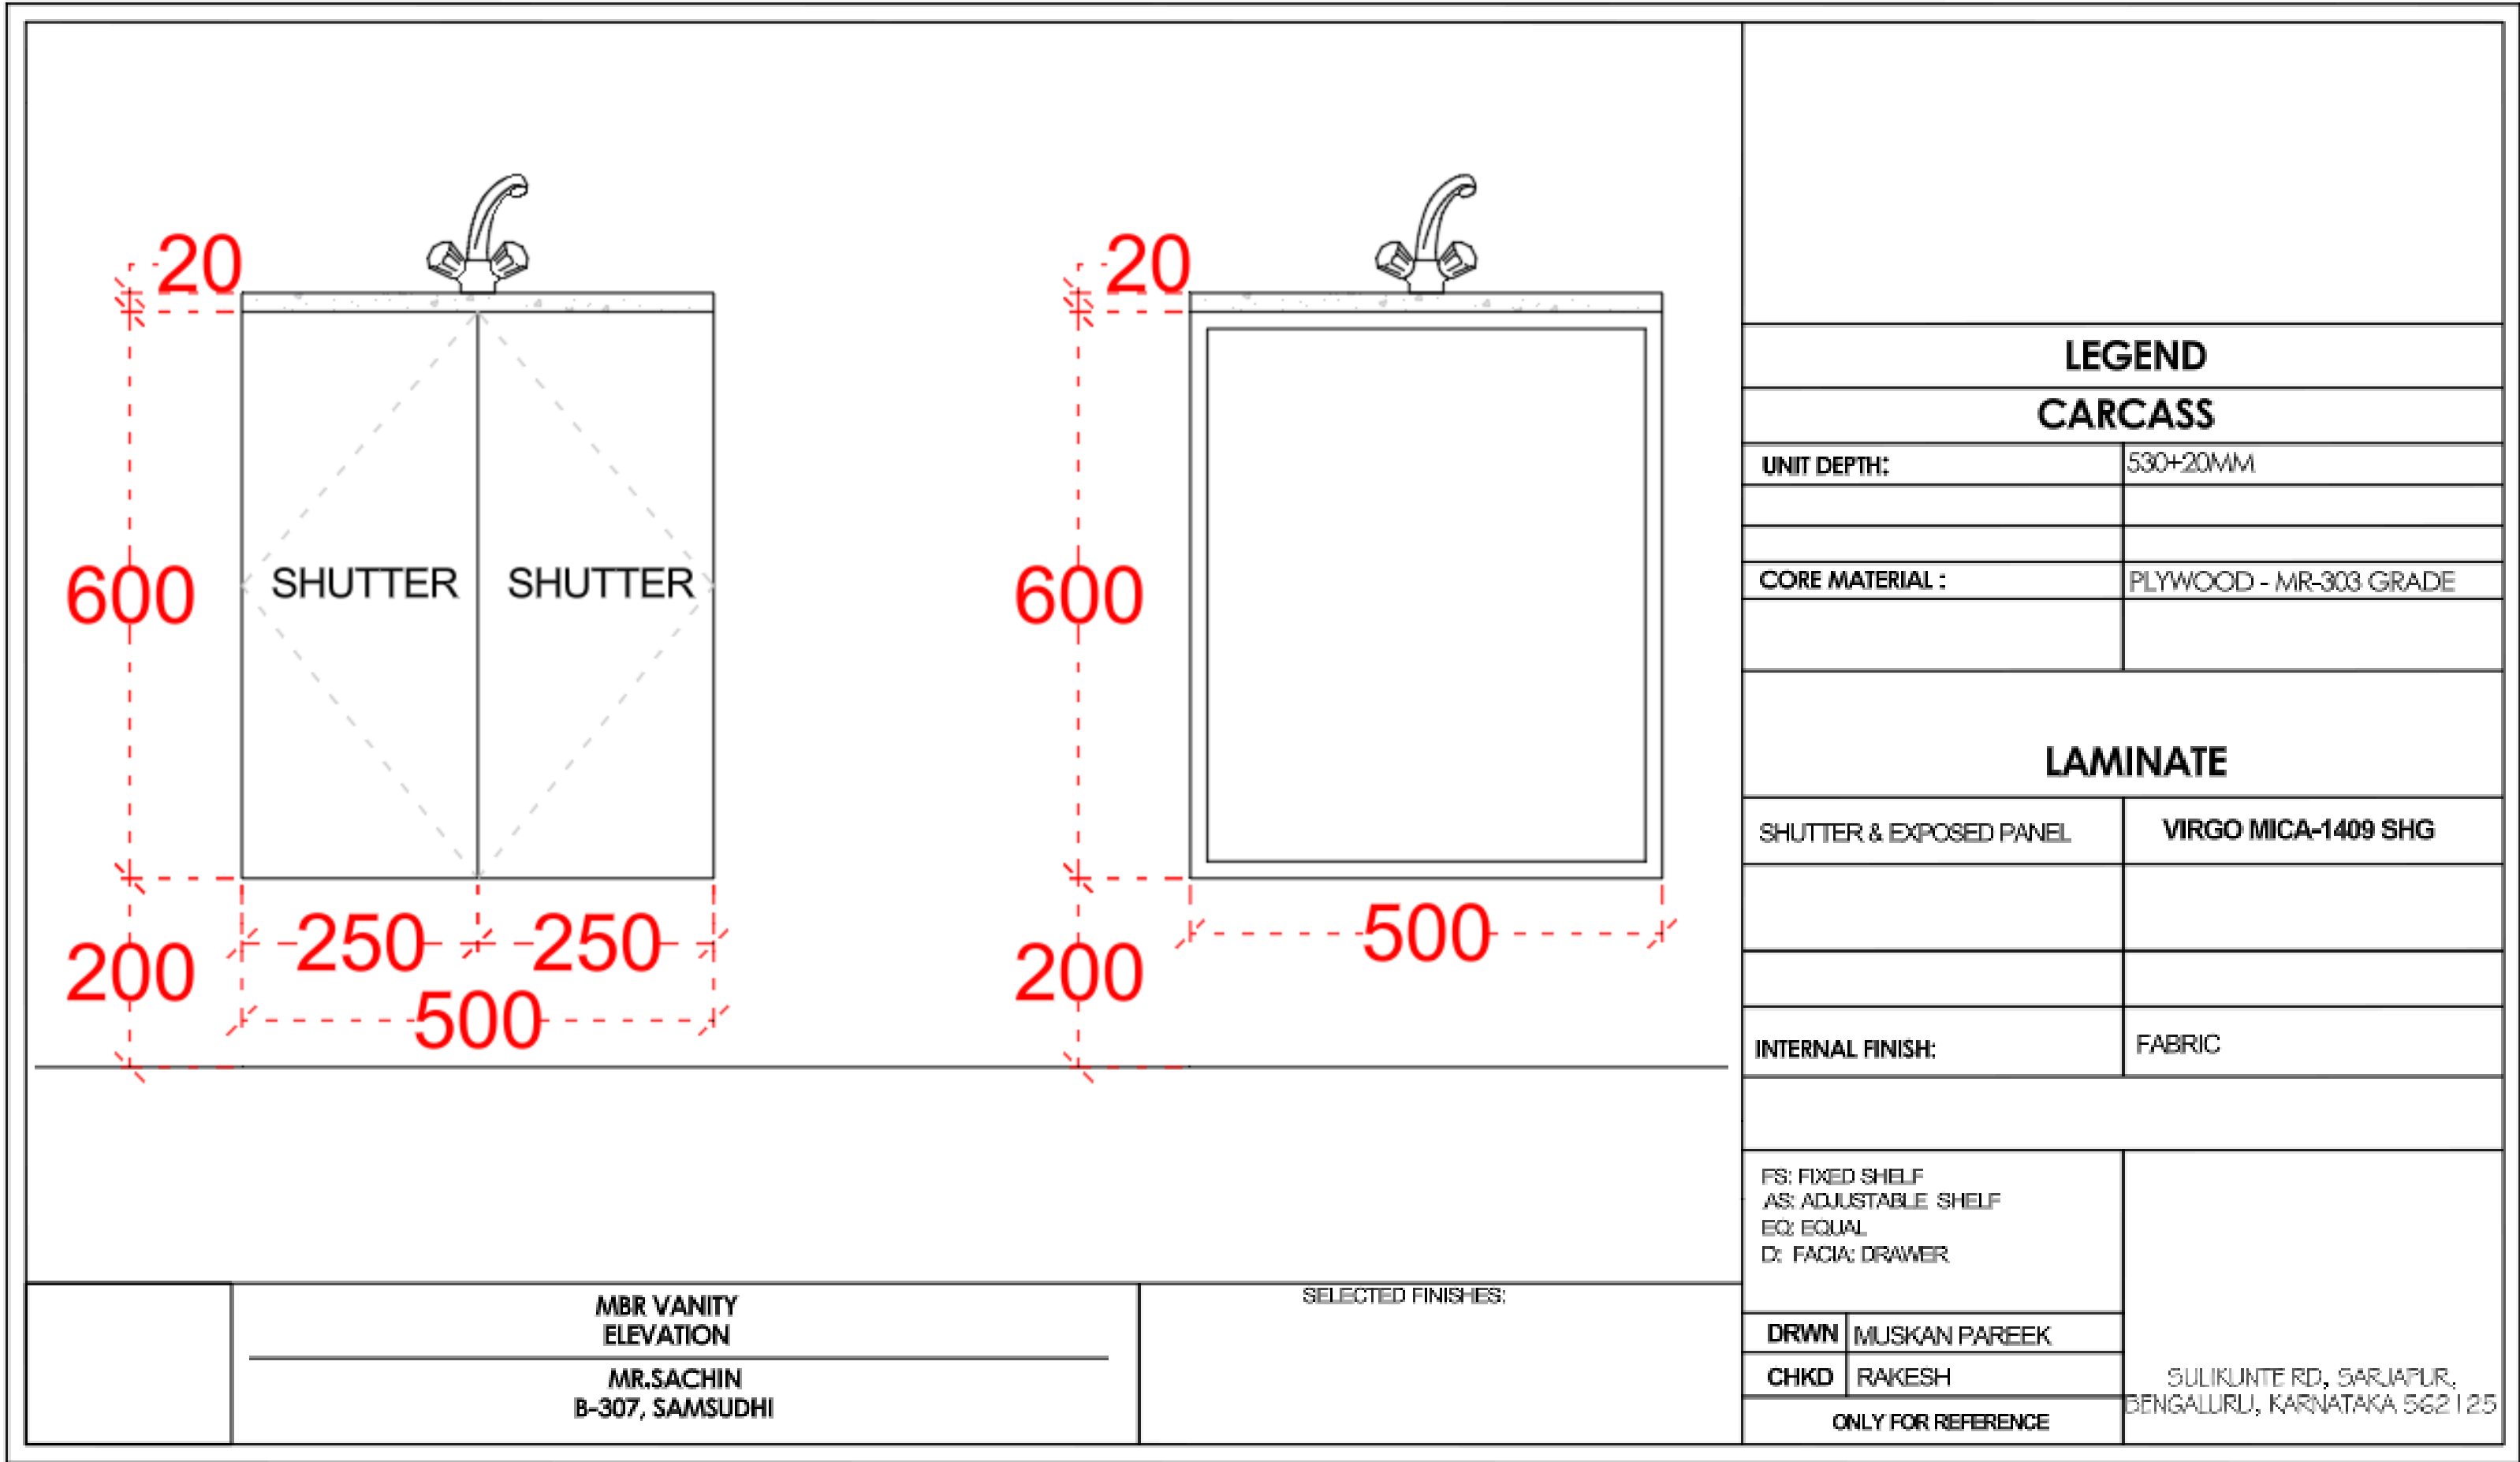


MBR :

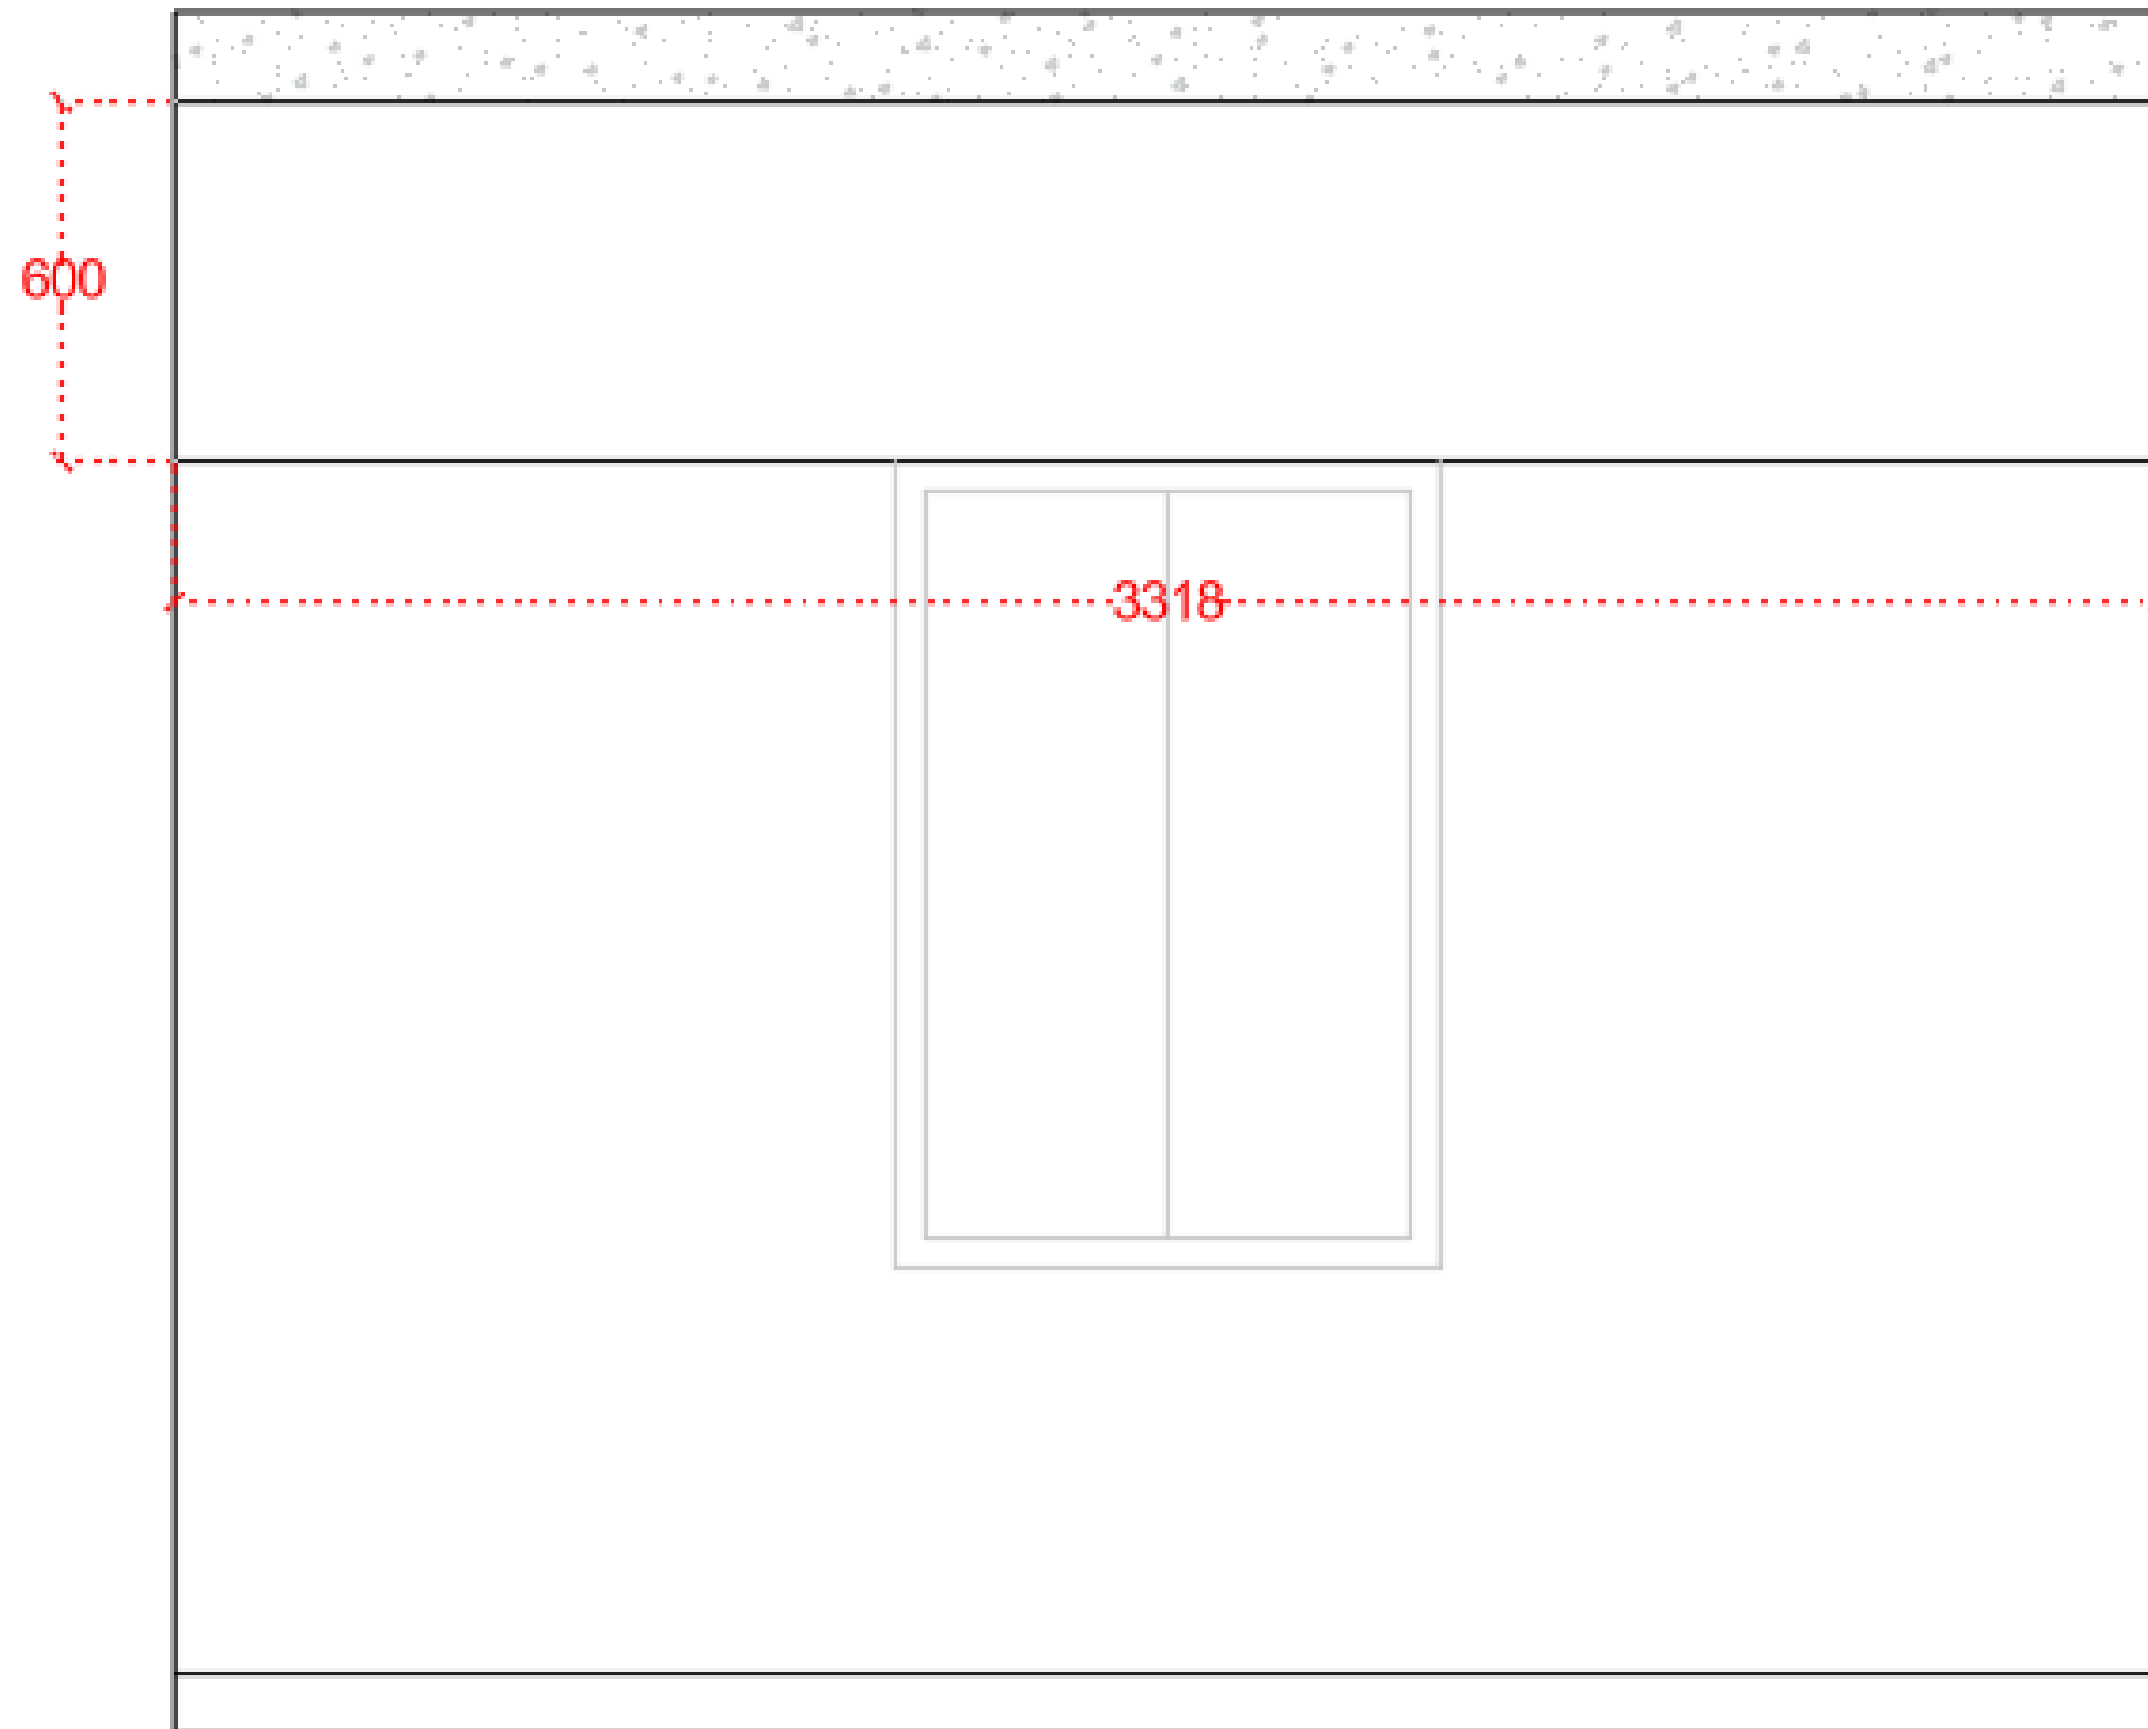

PELMET DEPTH:
150MM

GBR WARDROBE EXTERNAL

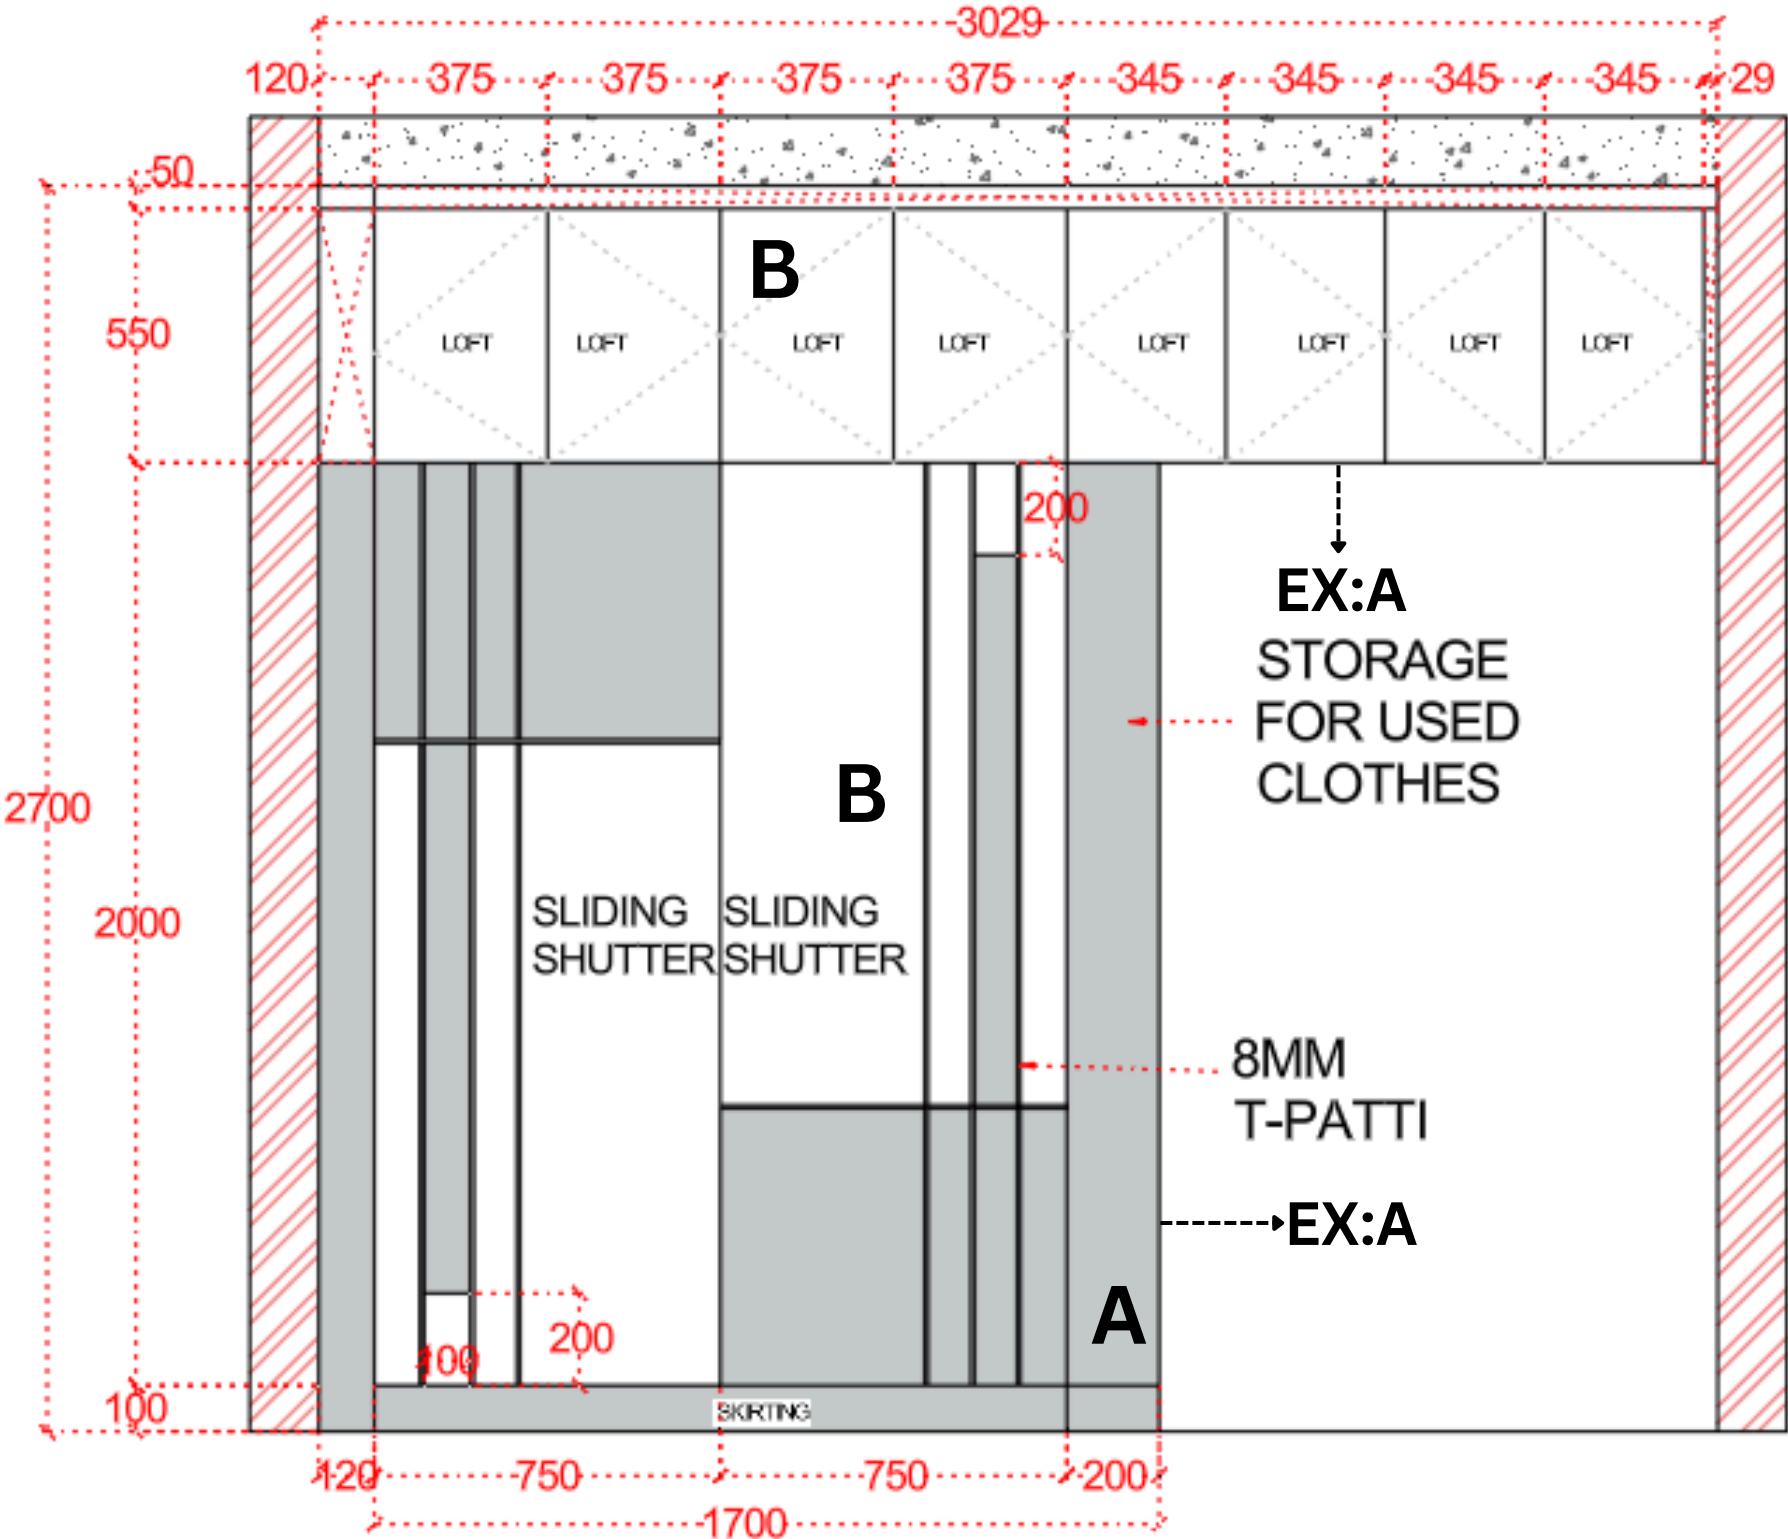

LEGEND

CARCASS

UNIT DEPTH :	580+20MM
CORE MATERIAL :	PLYWOOD - MR 303 GRADE

LAMINATE

WARDROBE SHUTTERS EXPOSED PANEL- A	VIGRO: 1937 SHG
WARDROBE SHUTTER& LOFT SHUTTER-B	VIGRO: 1409 SHG

INTERNAL FINISH:	0.72MM OFF WHITE LAMINATE
------------------	---------------------------

FS: FIXED SHELF
AS: ADJUSTABLE SHELF
EQ: EQUAL
D: FACIA: DRAWER



DRWN	MUSKAN PAREEK
CHKD	RAKESH

ONLY FOR REFERENCE


SULKUNTE RD, SARJAPUR,
BENGALURU, KARNATAKA 562 125

GBR
ELEVATION


MR.SACHIN & SAMMITHA

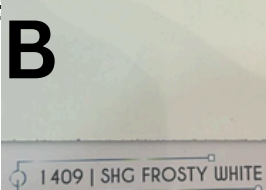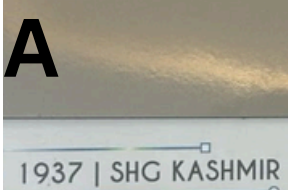


GBR WARDROBE INTERNAL

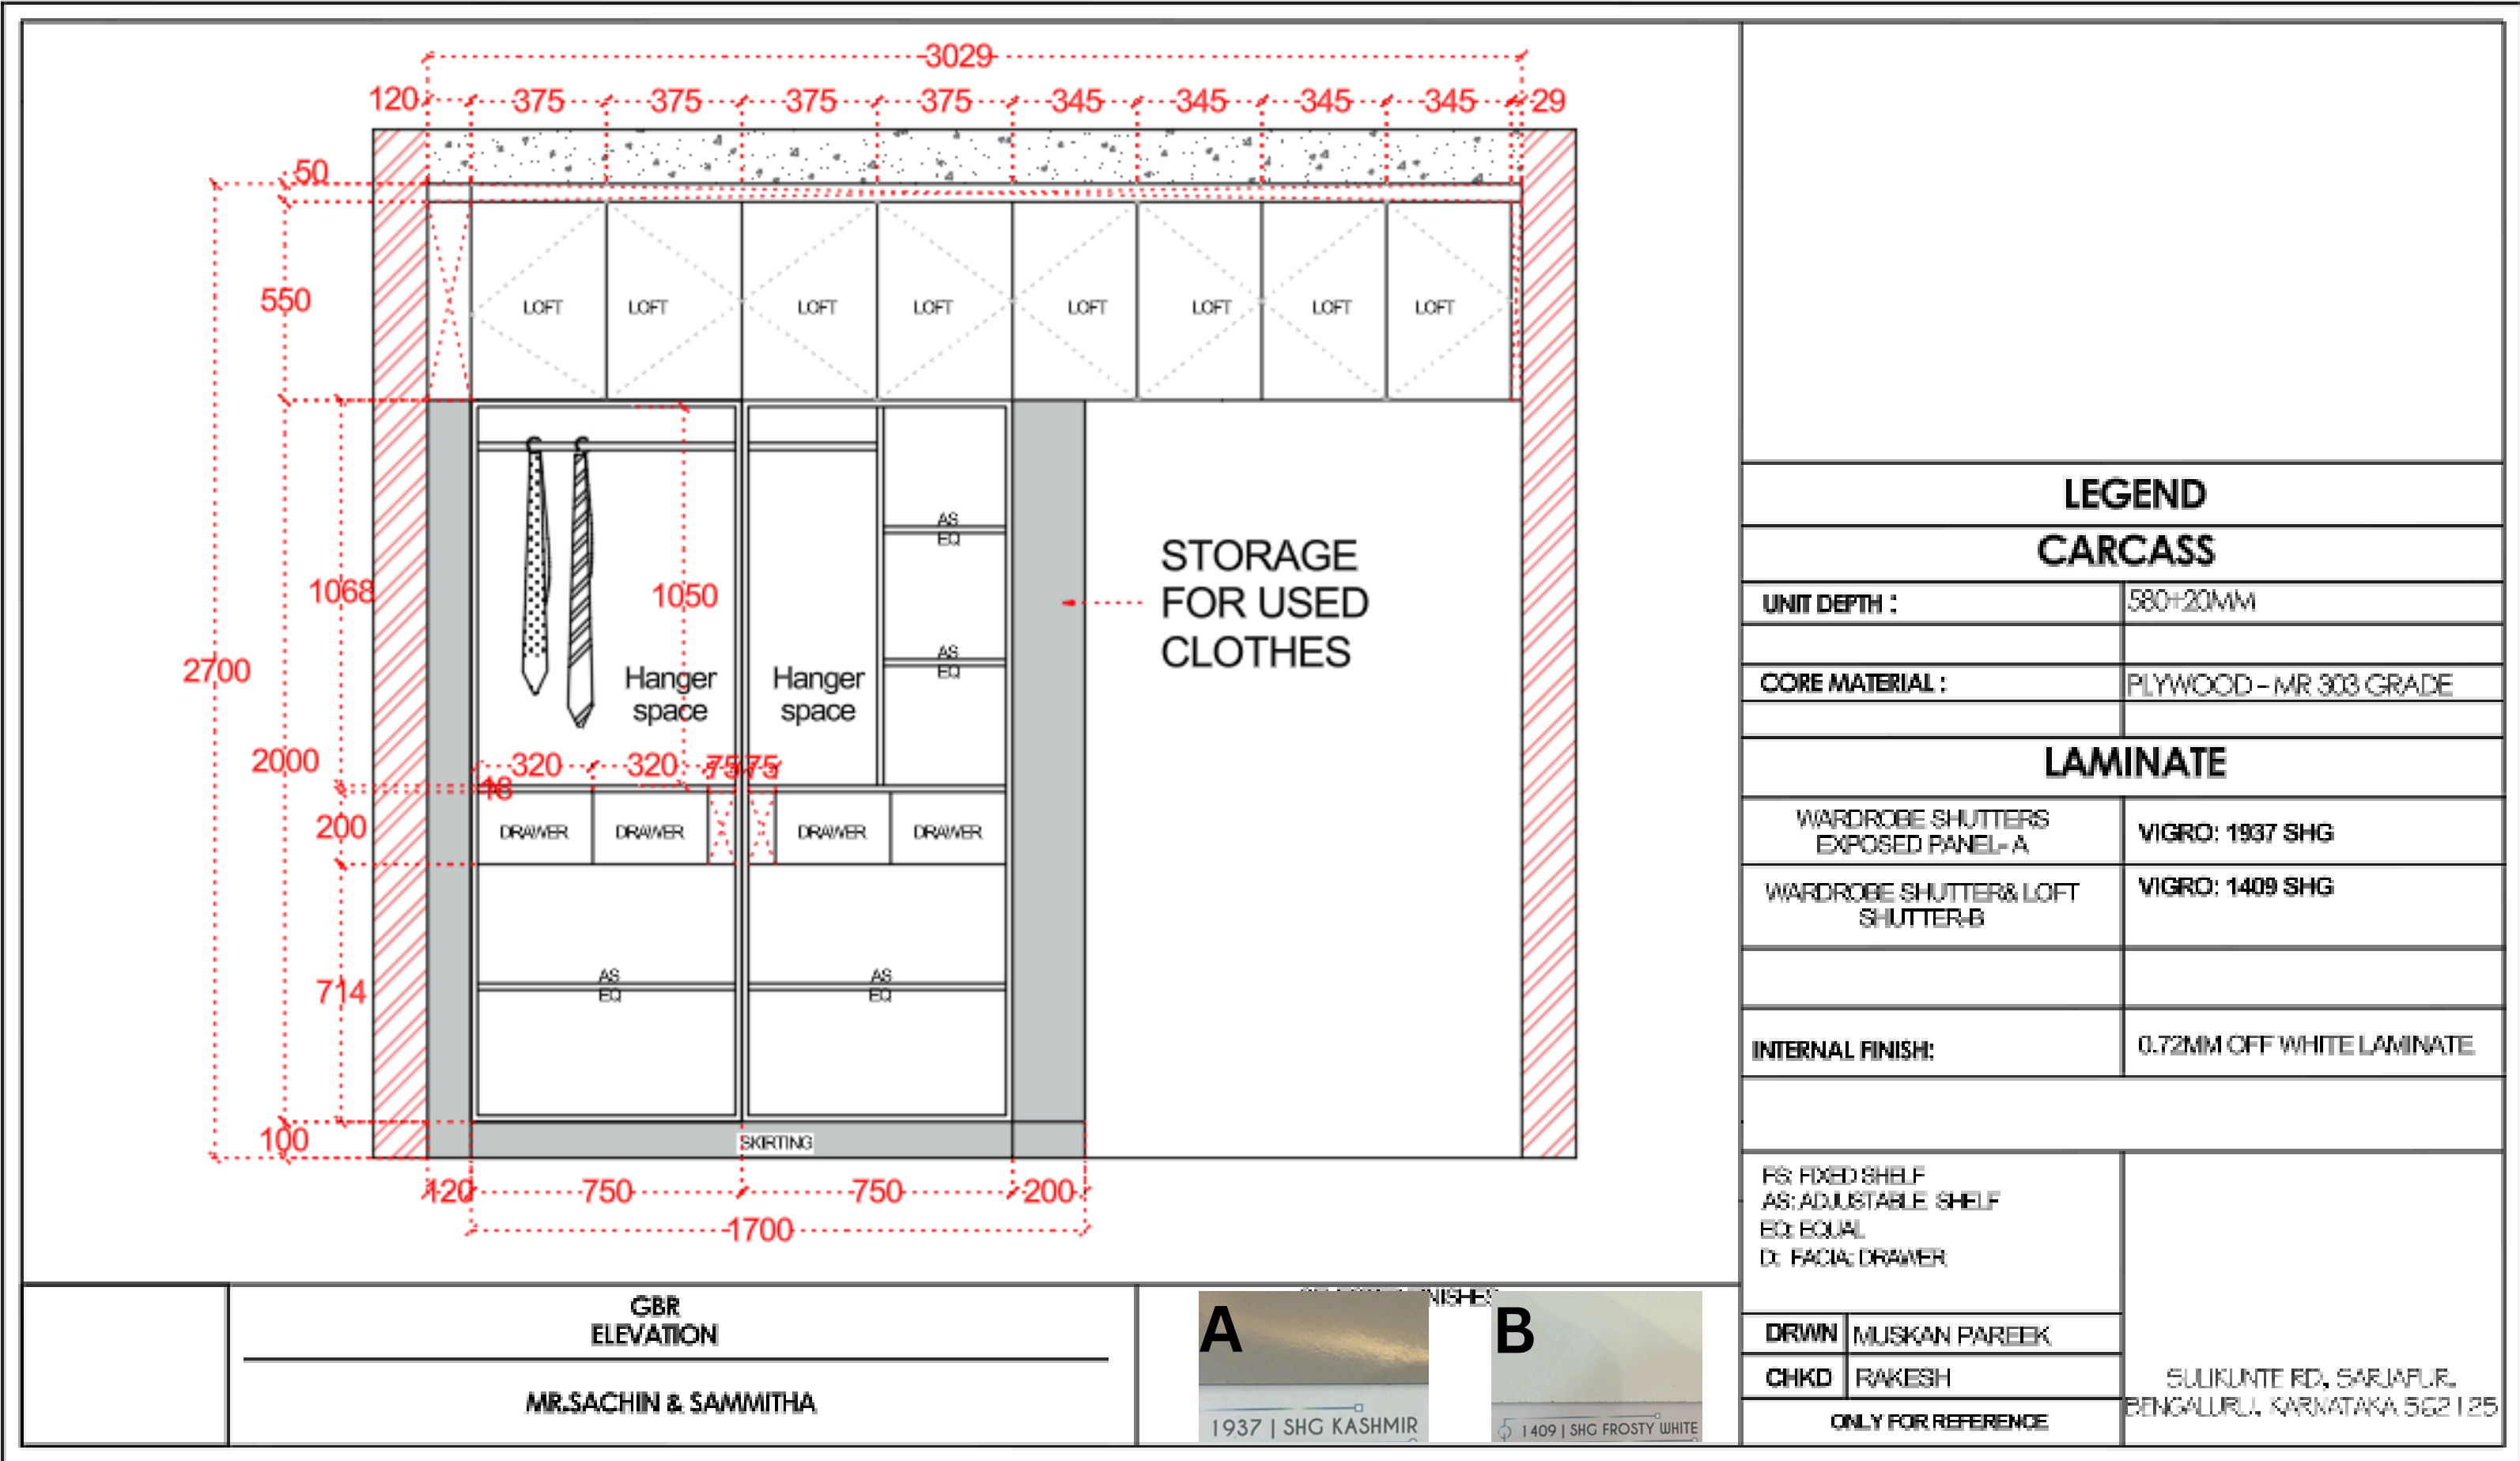


GBR STORAGE UNIT :

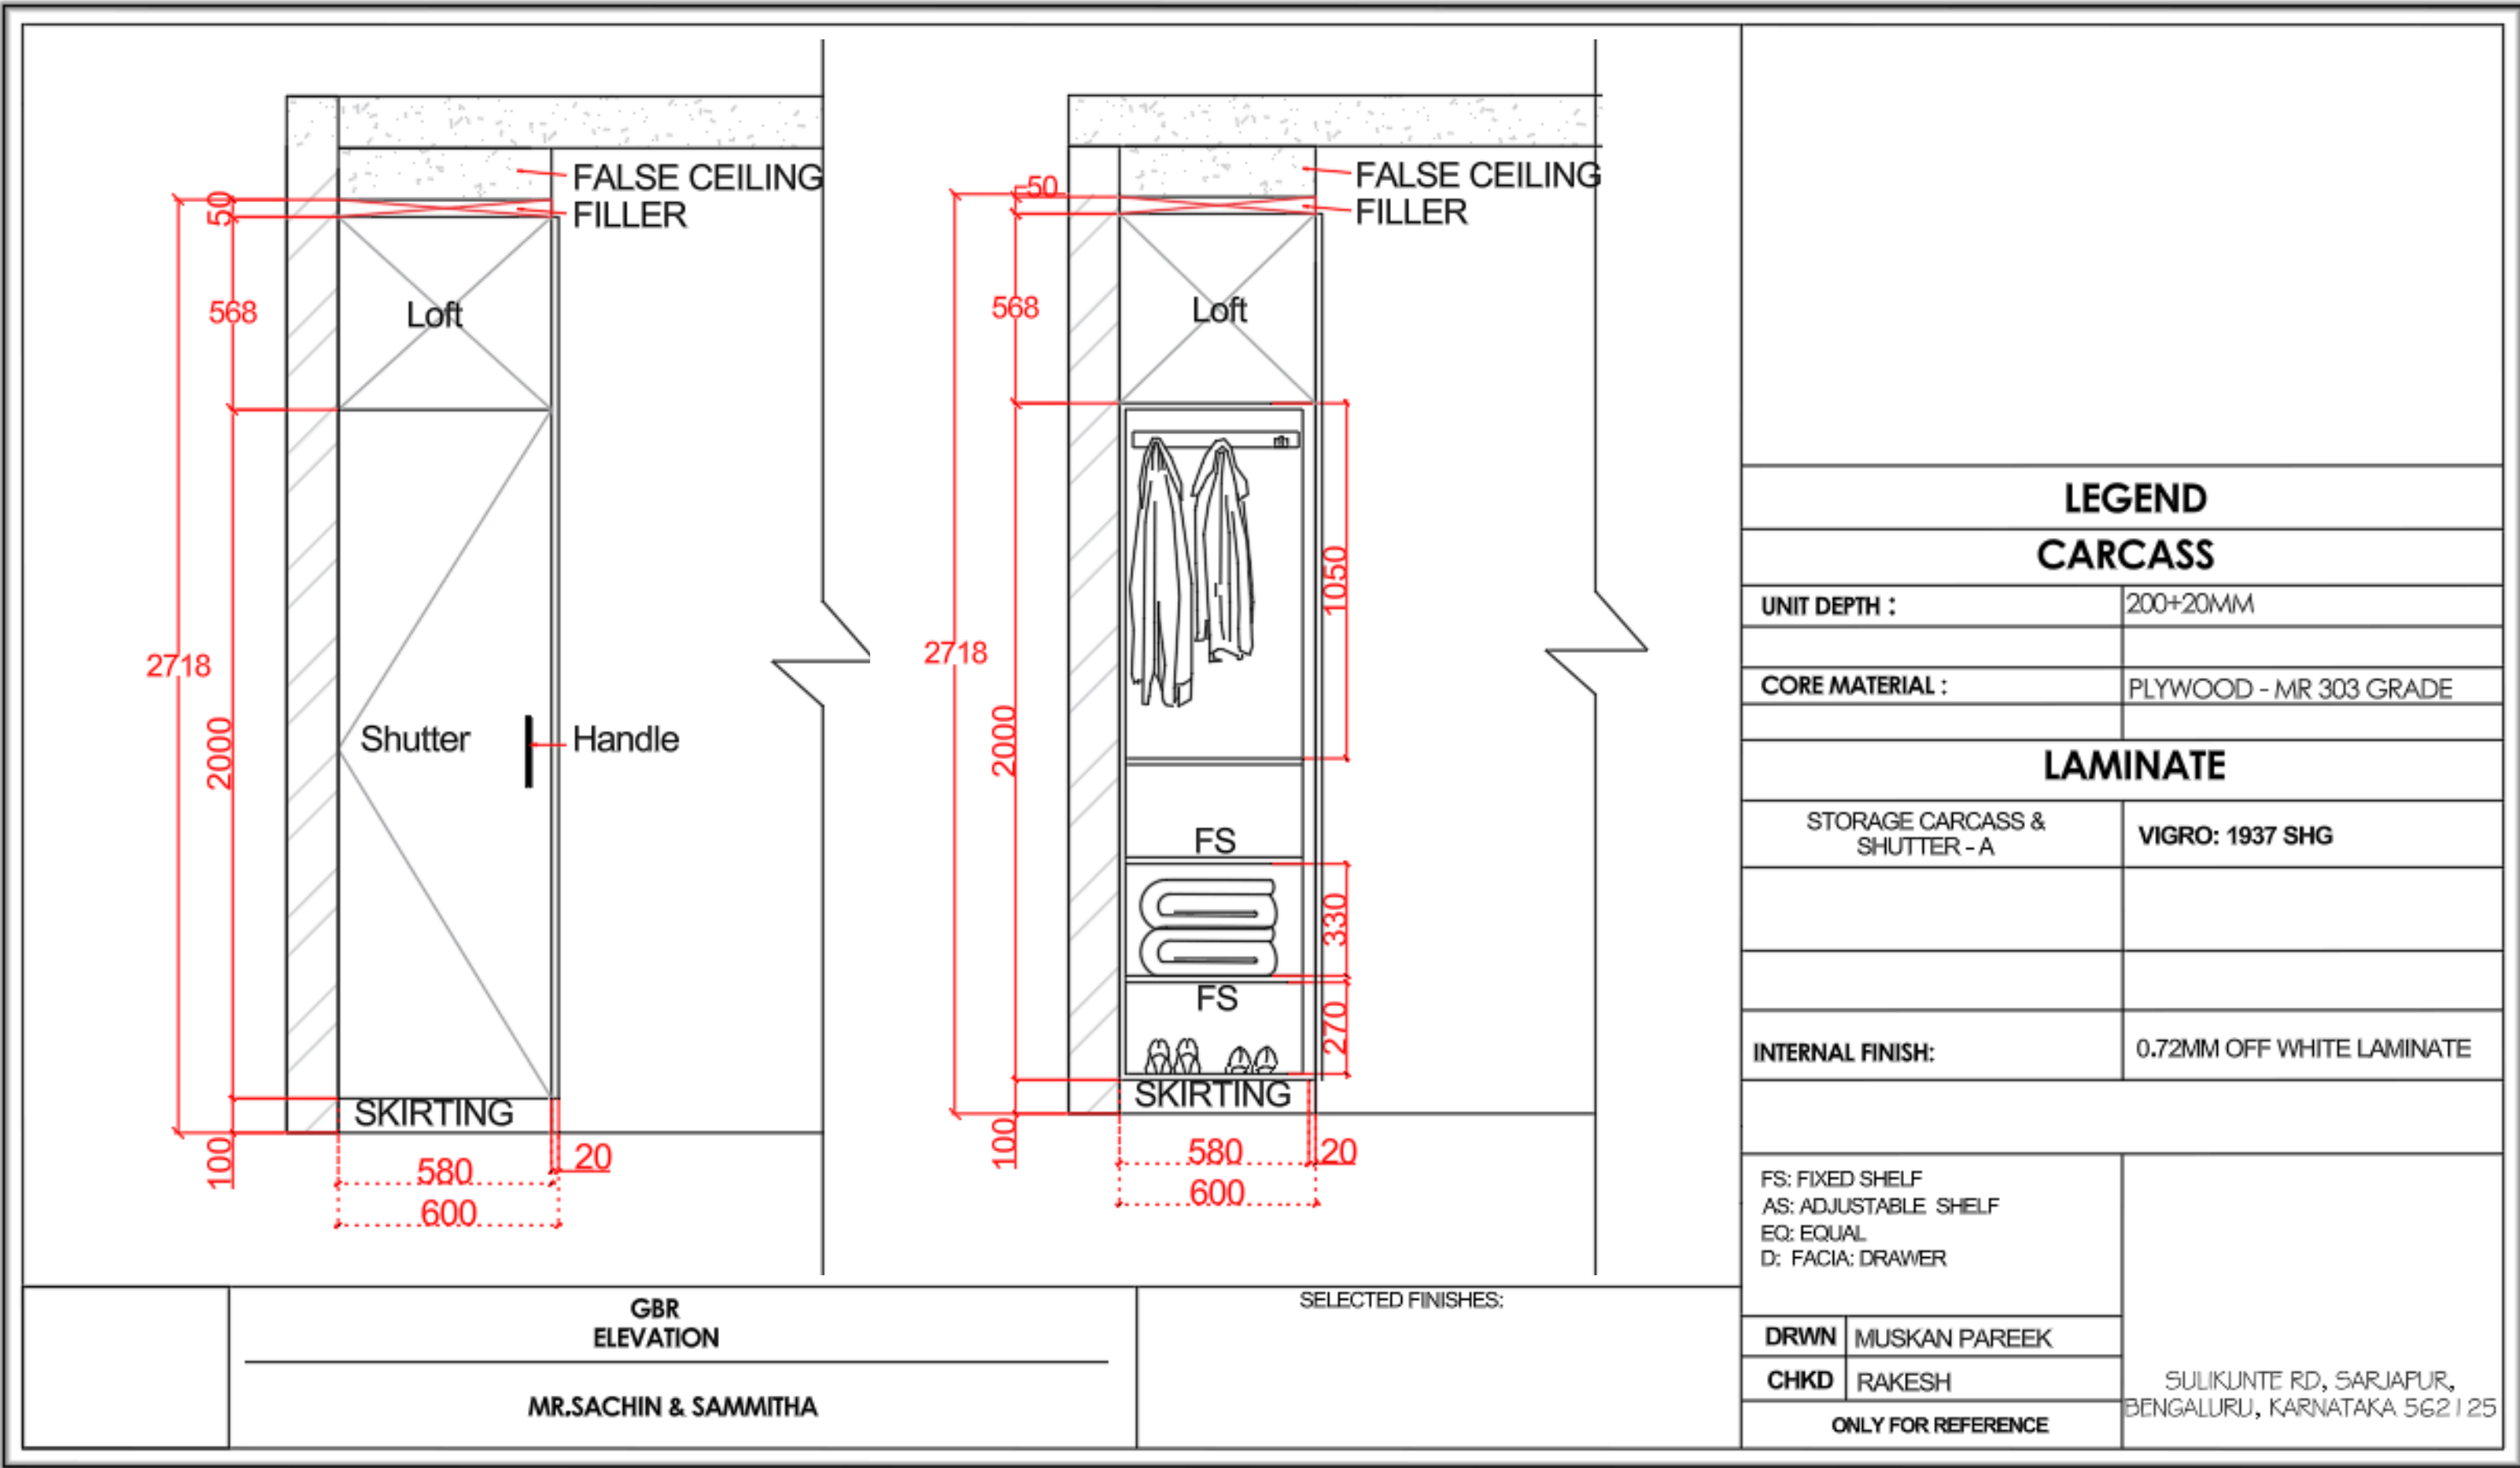



KBR WARDROBE EXTERNAL

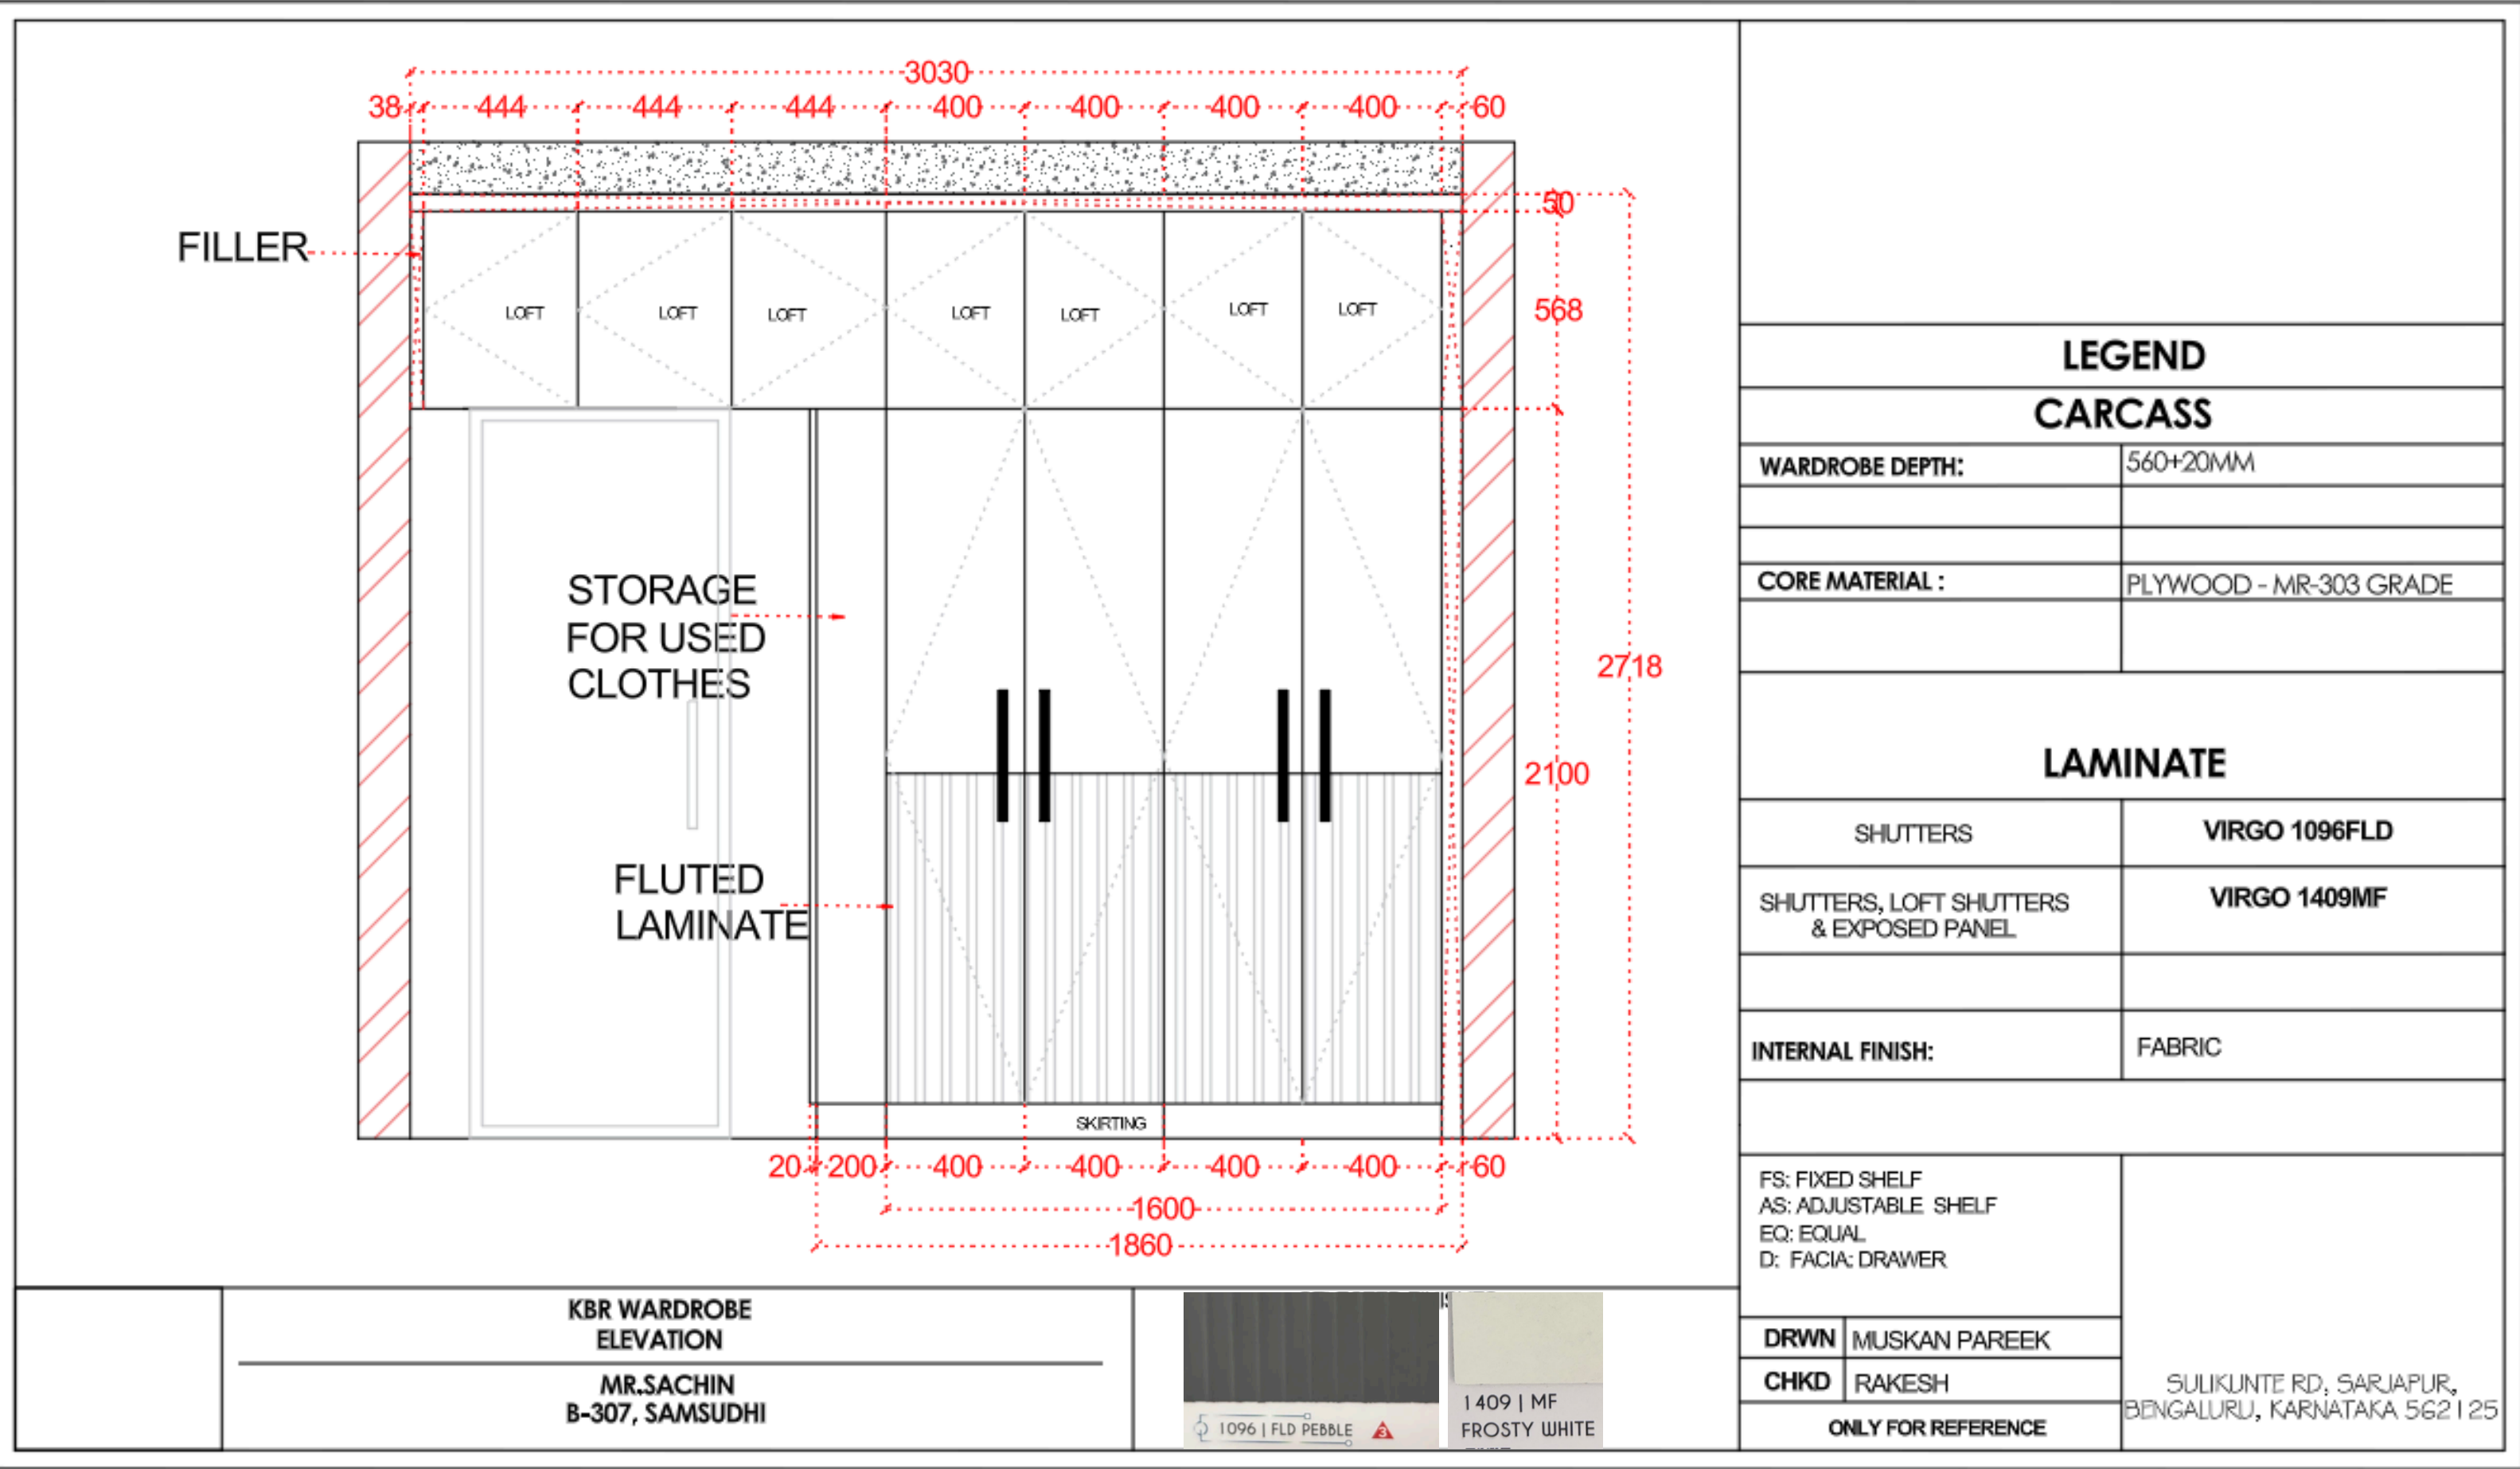


KBR WARDROBE INTERNAL:

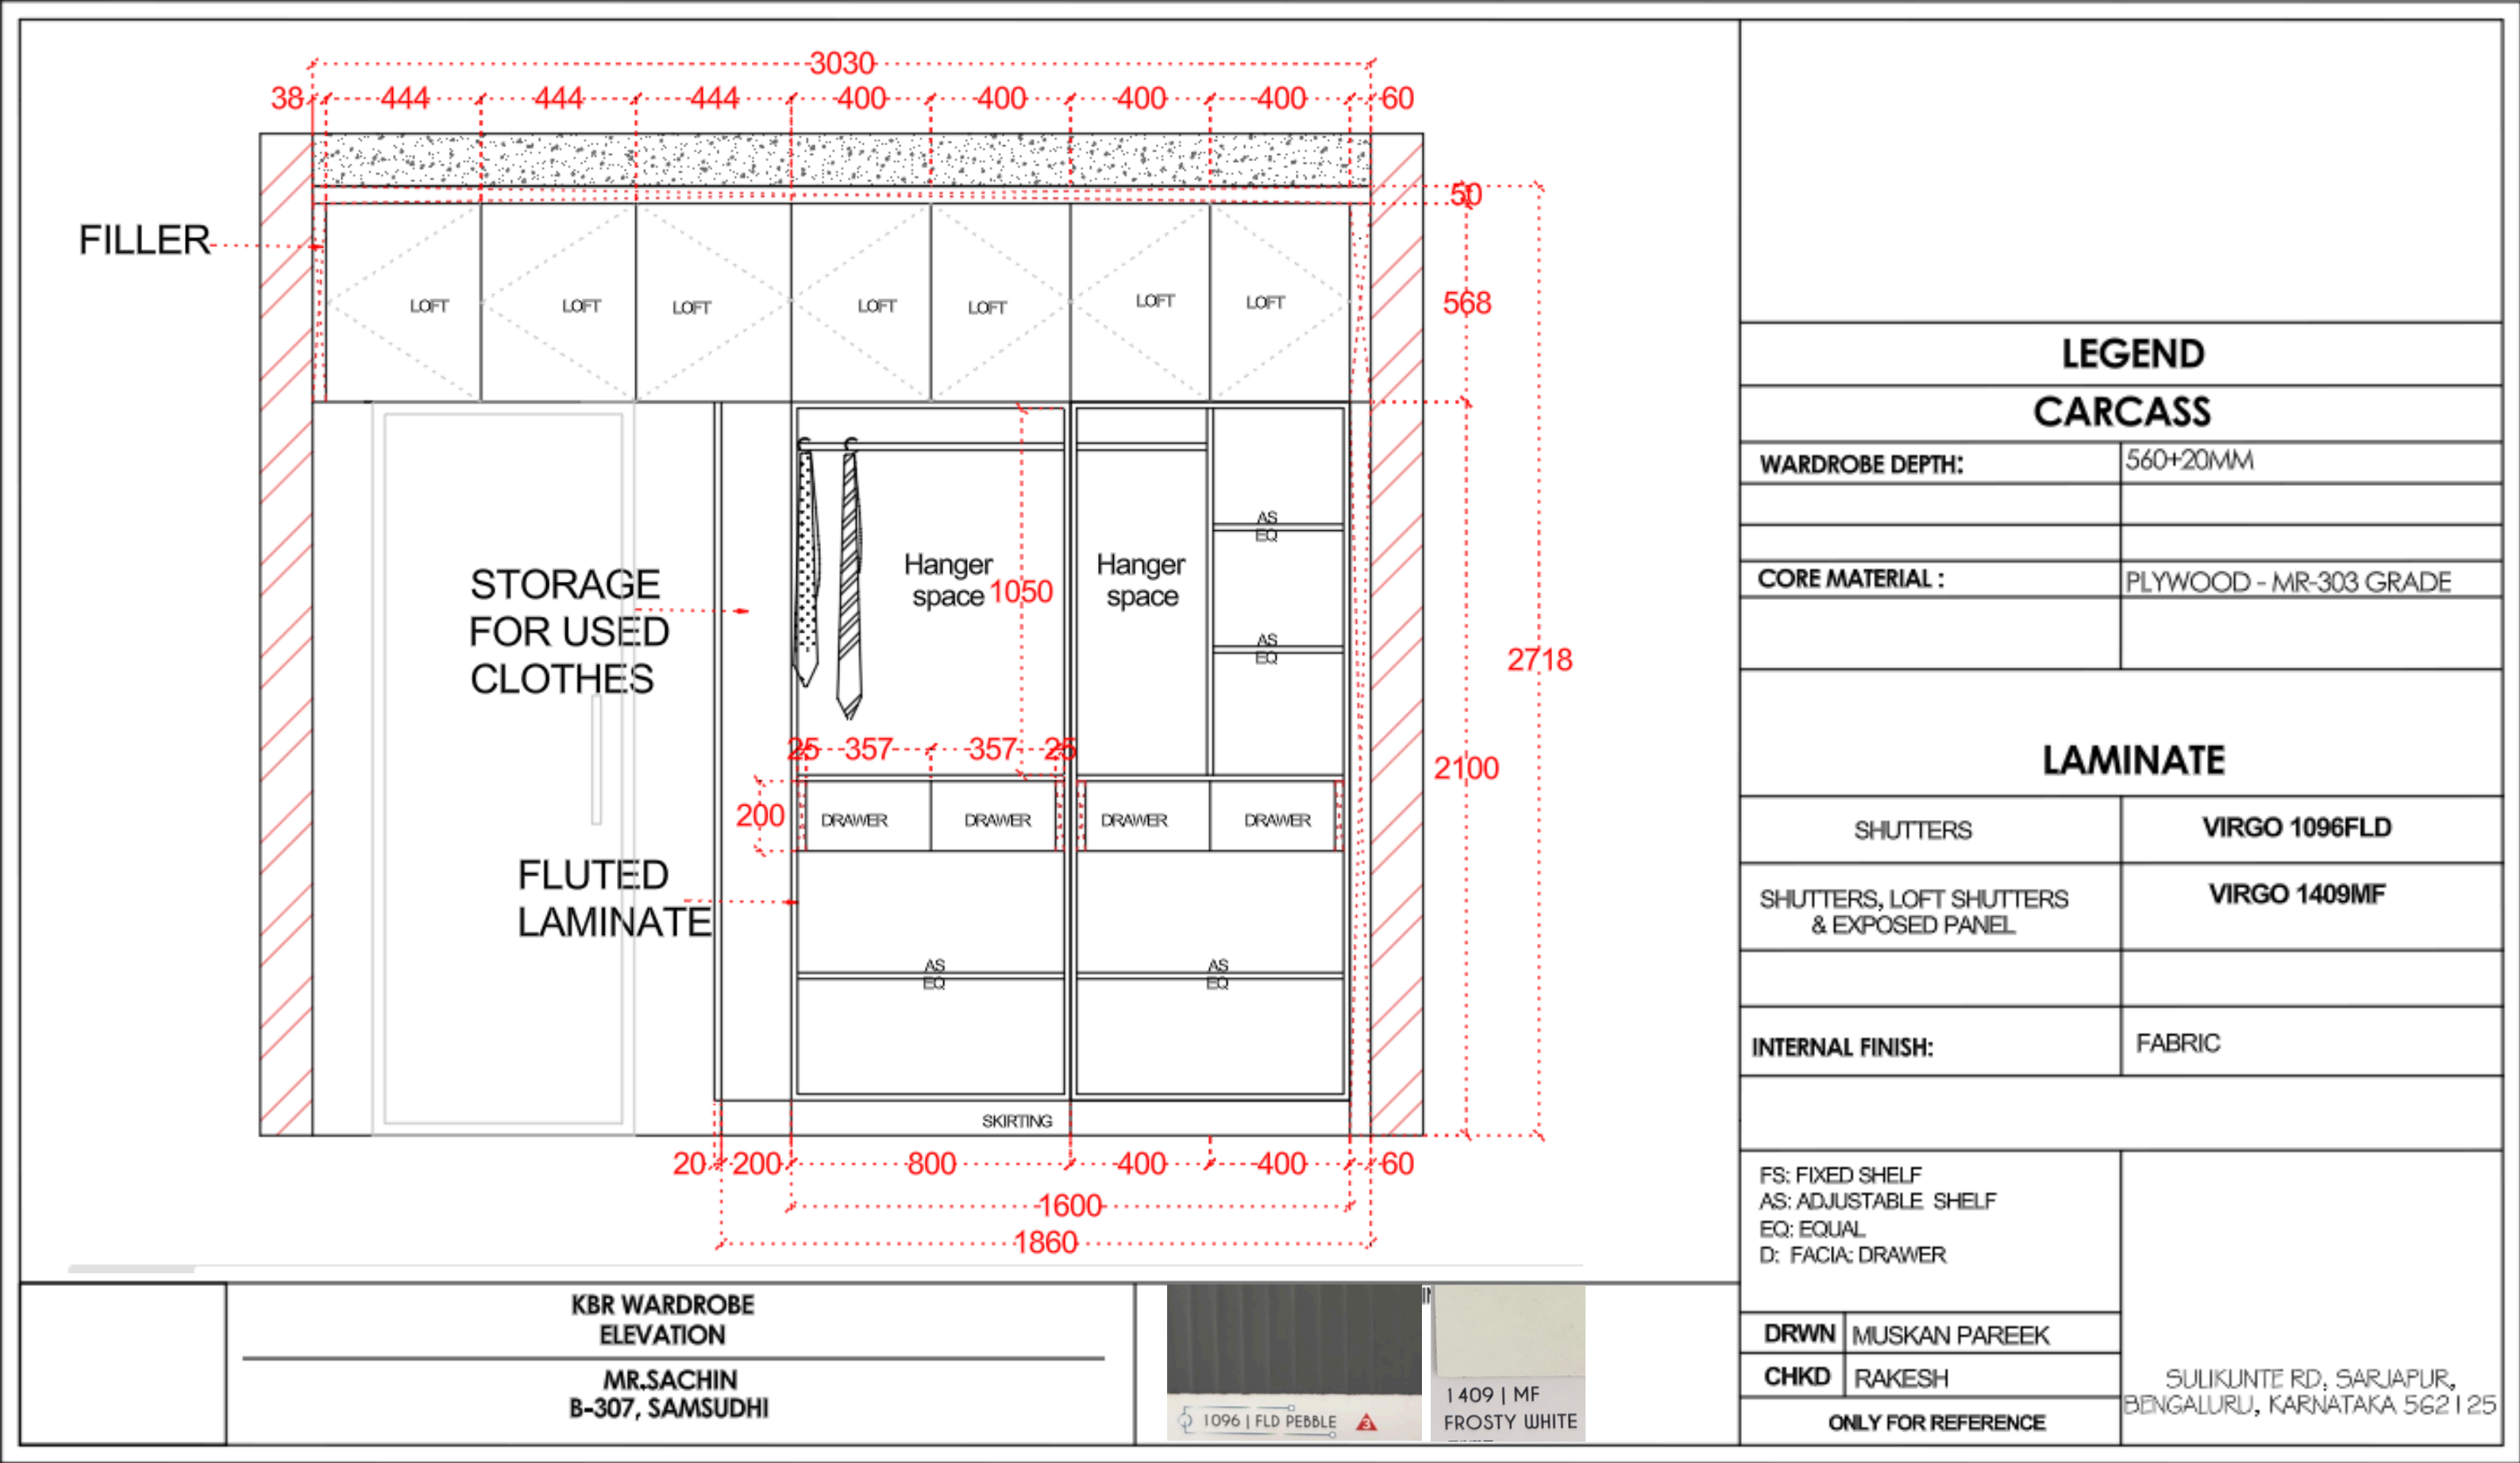

KBR STORAGE UNIT :

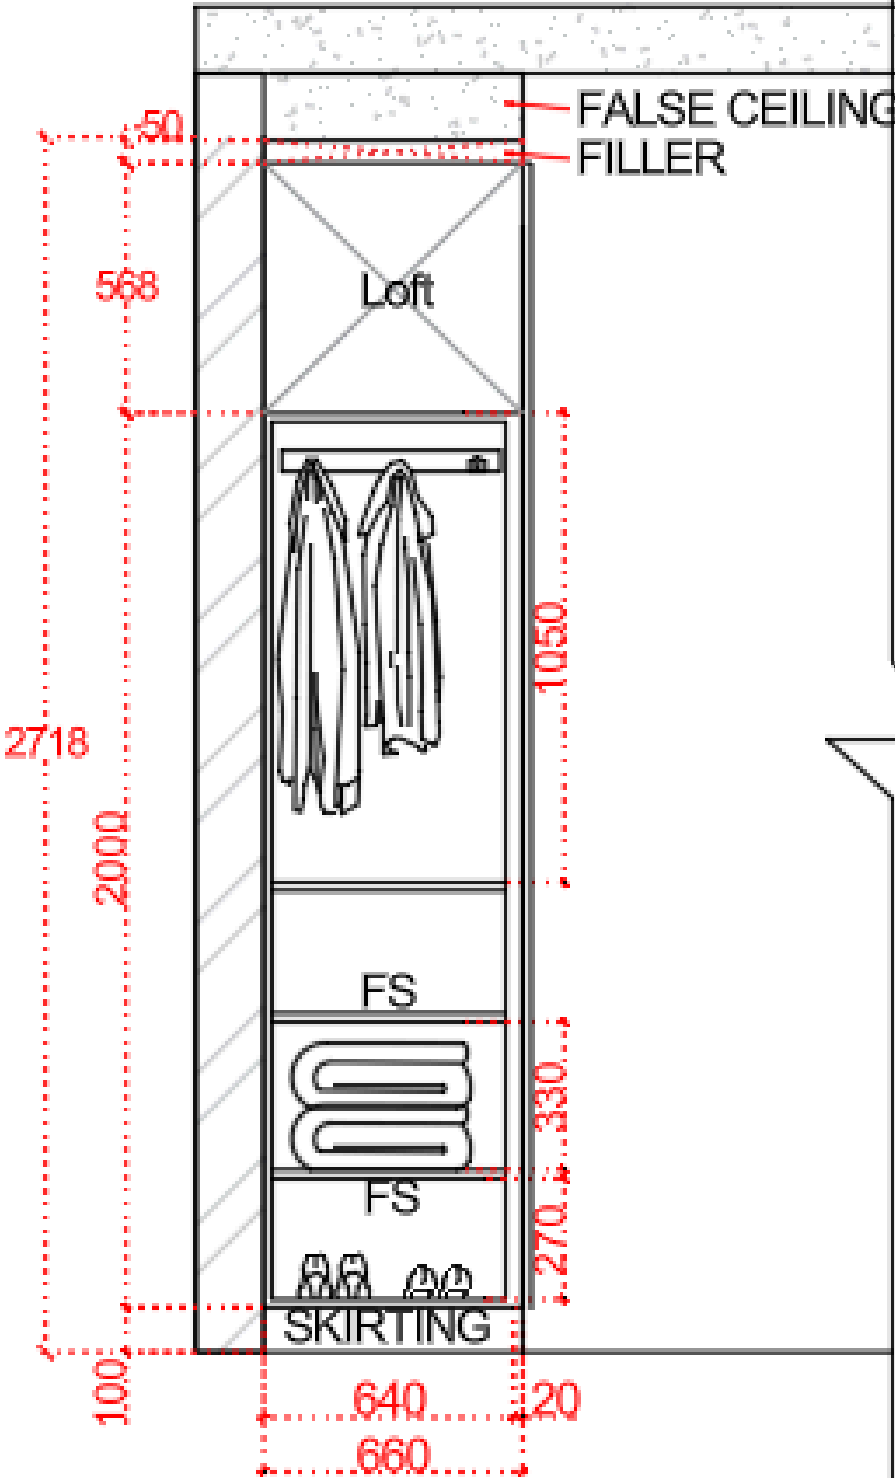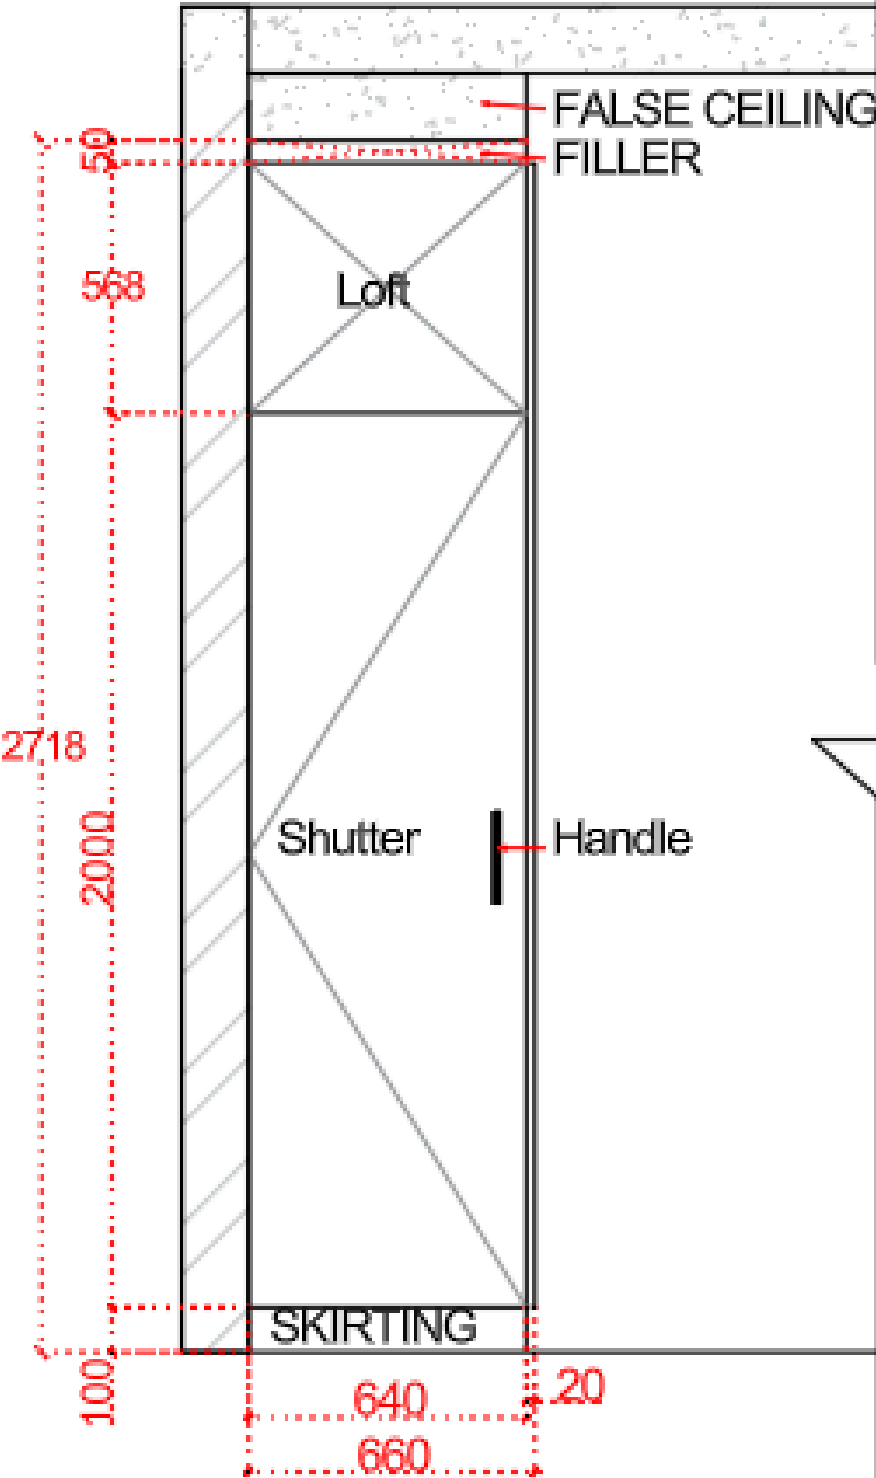

WARDROBE DEPTH:
540+20
STORAGE WEIDTH: 660

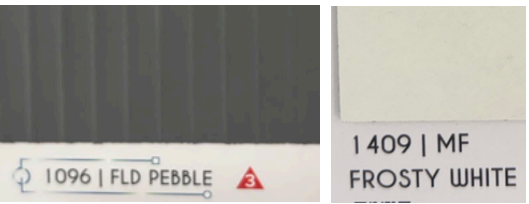

THANK YOU