


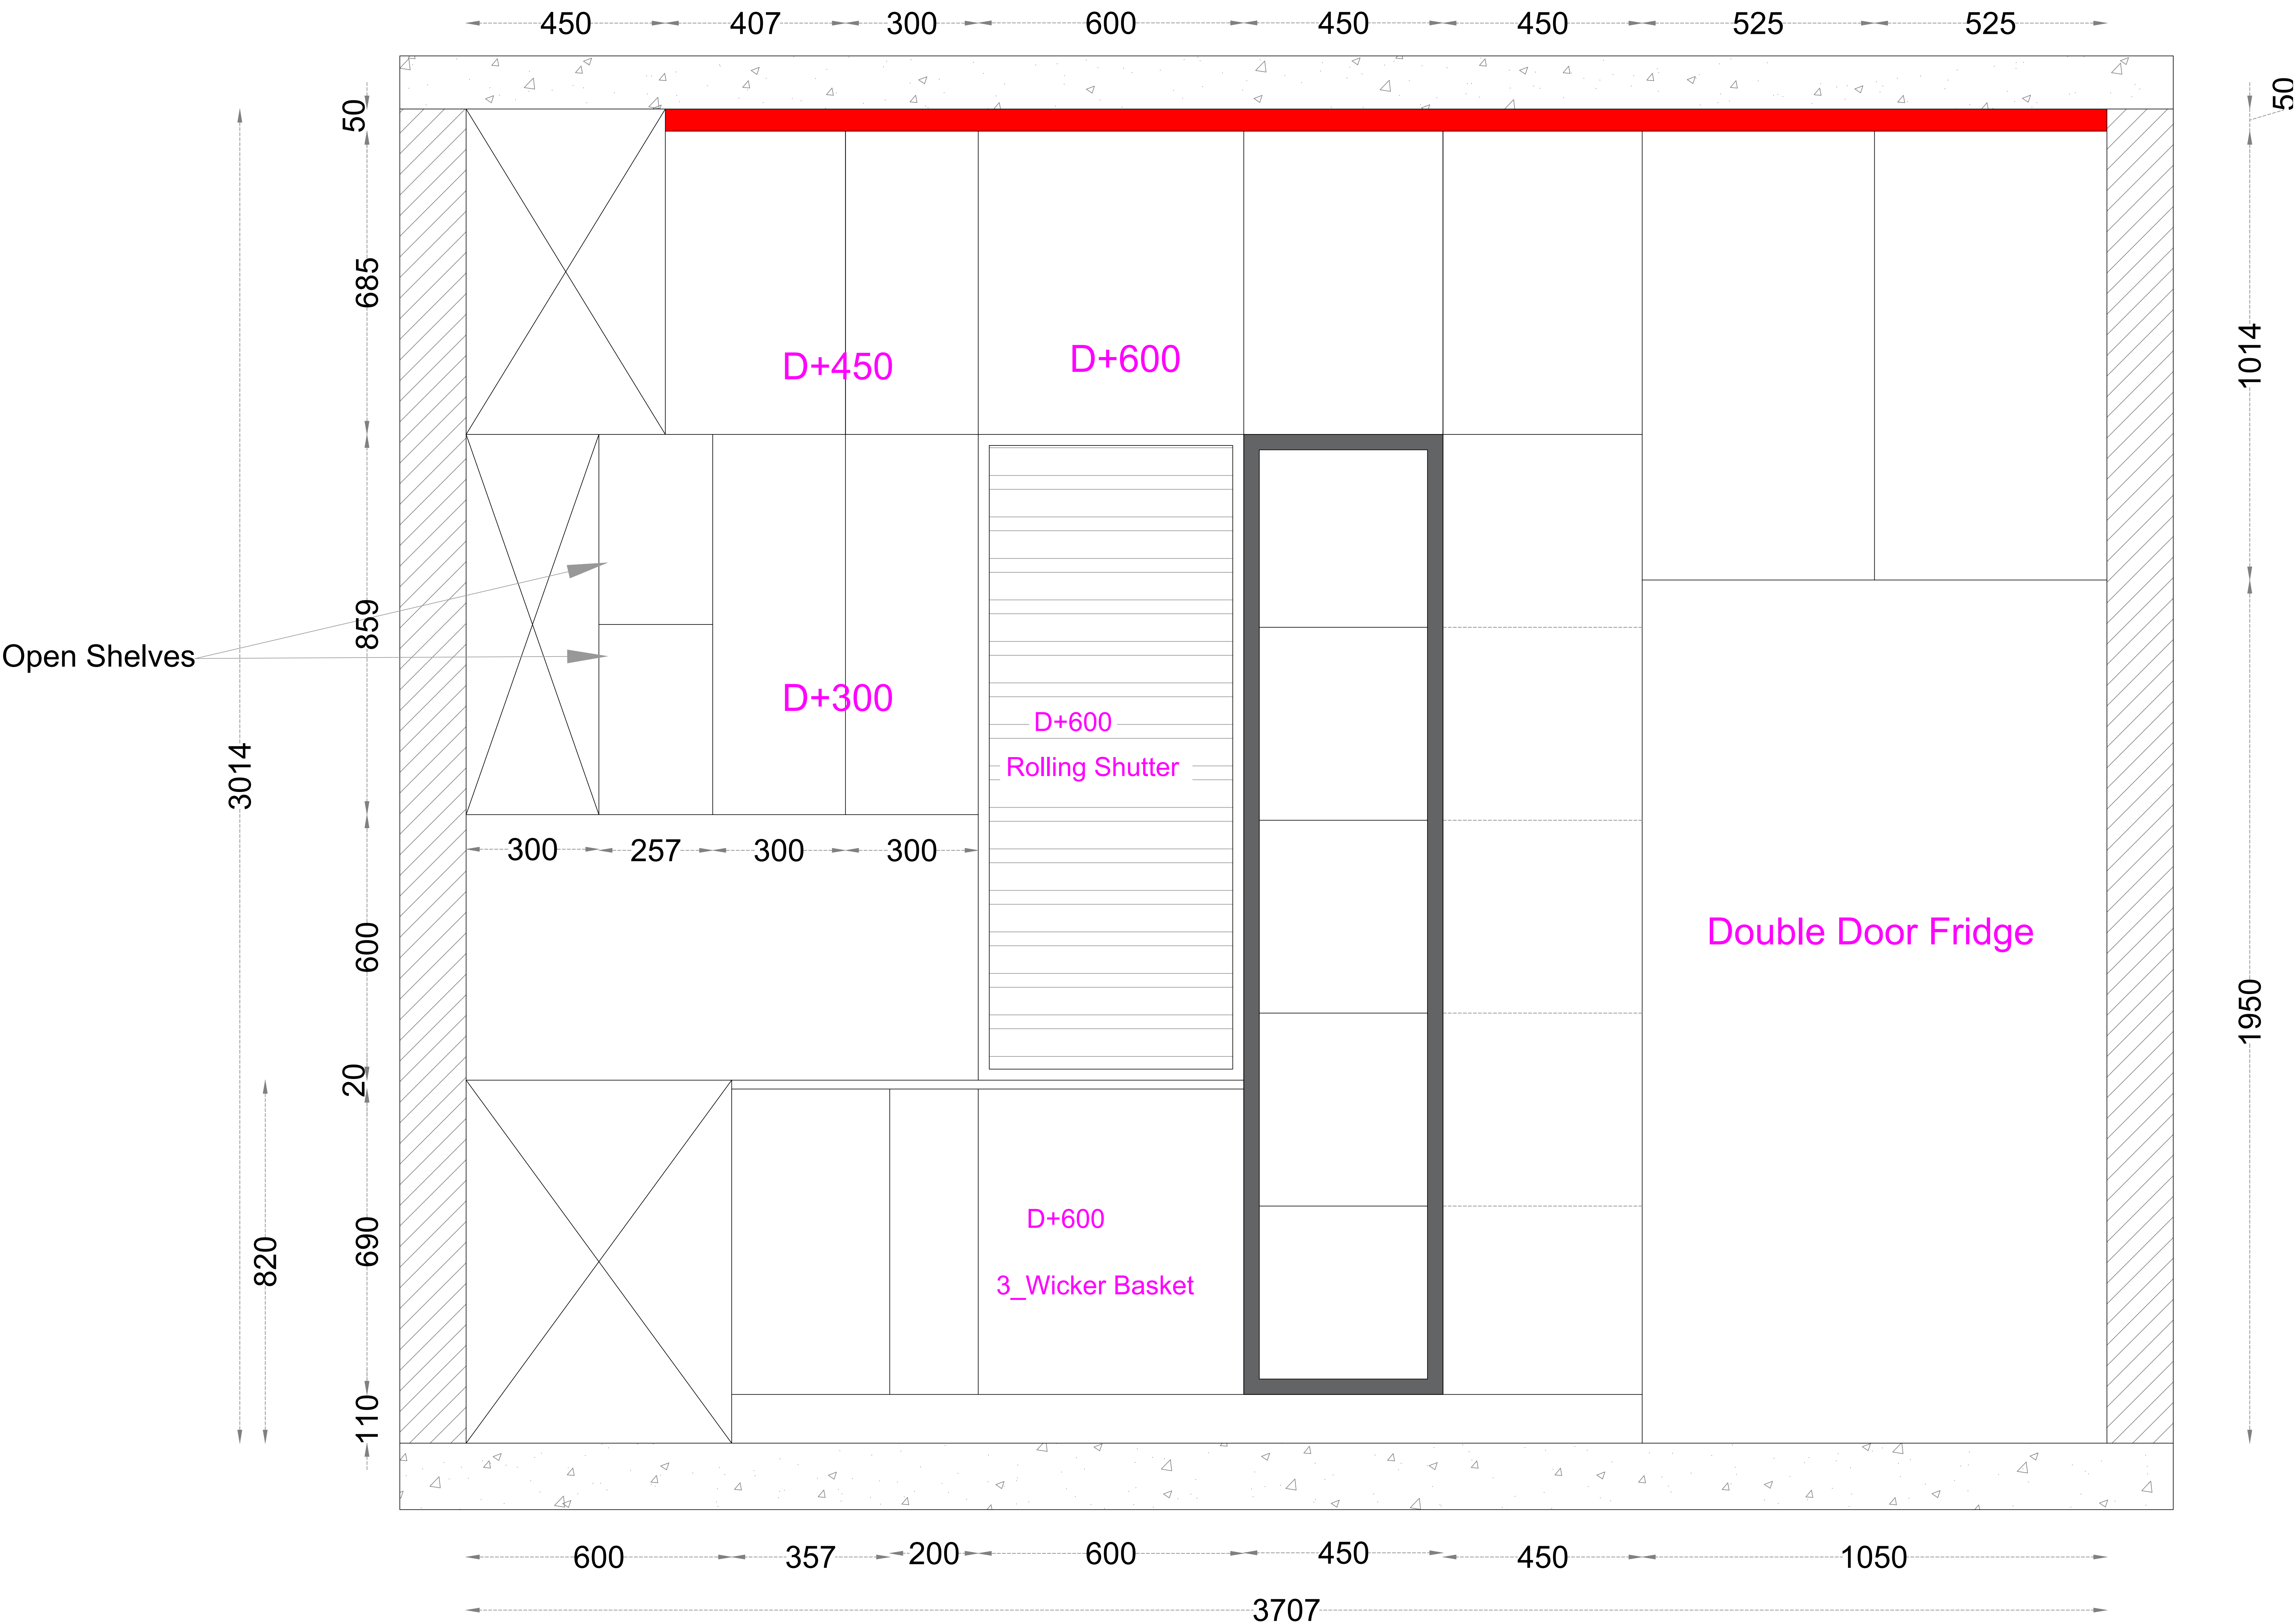

Kitchen_A

ALL DIMENSIONS ARE IN MILLIMETERS .
CONTRACTOR HAS TO CHECK & VERIFY ALL LEVELS, DATUM & DIMENSIONS ON SITE AND SHALL REPORT ANY DISCREPANCIES OR OMISSIONS ON SITE THIS OFFICE PRIOR TO THE START OF WORK & DURING THE CONSTRUCTION PHASE.
THIS DRAWING HAS TO BE READ & UNDERSTOOD IN CONJUNCTION WITH STRUCTURAL, MECHANICAL, ELECTRICAL AND/OR ANY OTHER CONSULTANT/S DOCUMENTATION, AS MAY BE APPLICABLE TO THE PROJECT PRIOR TO START OF WORK & IT'S DURATION.

TECHNICAL NOTE :
PROVIDED AS PER STRUCTURAL DRAWINGS & DETAILS.
ANY DISCREPENCY RELATED TO THIS DRAWING SHALL BE BROUGHT TO THE NOTICE OF THE CONCERNED PROJECT ARCHITECTS IMMEDIATELY BEFORE THE EXECUTION OF WORK.
LVLS MENTIONED IN THE DRAWING REFERS TO THE UNFINISHED LEVELS ON THE SITE.

COMPANY NAME
SPACICOUS VENTURE
Address:
Address: Candeur Landmark Liberty blockD903
Varthur, Bengaluru, Karnataka 560087

CLIENT NAME :
Mr.

PROJECT NAME :
INCOR_C1301

DRAWING TITLE :
Kitchen_A

DRAWING NO :


SHEET NO	:000
SCALE	: N.T.S
TEAM	Woodpeckers
DRAWN	: Mohd Arfath
CHECKED	: Syedfareed
DESIGNED	: Syedfareed
DATE	: 14-12-2025

ARCHITECTURAL DRAWING

NOTE :
THIS DRAWING IS THE EXCLUSIVE PROPERTY OF "SPACICOUS VENTURE". AND THE REPRODUCTION OF ANY PART WITHOUT PRIOR WRITTEN CONSENT FROM THIS OFFICE IS A VIOLATION OF APPLICABLE LAWS.

Open Shelves

Open Shelves

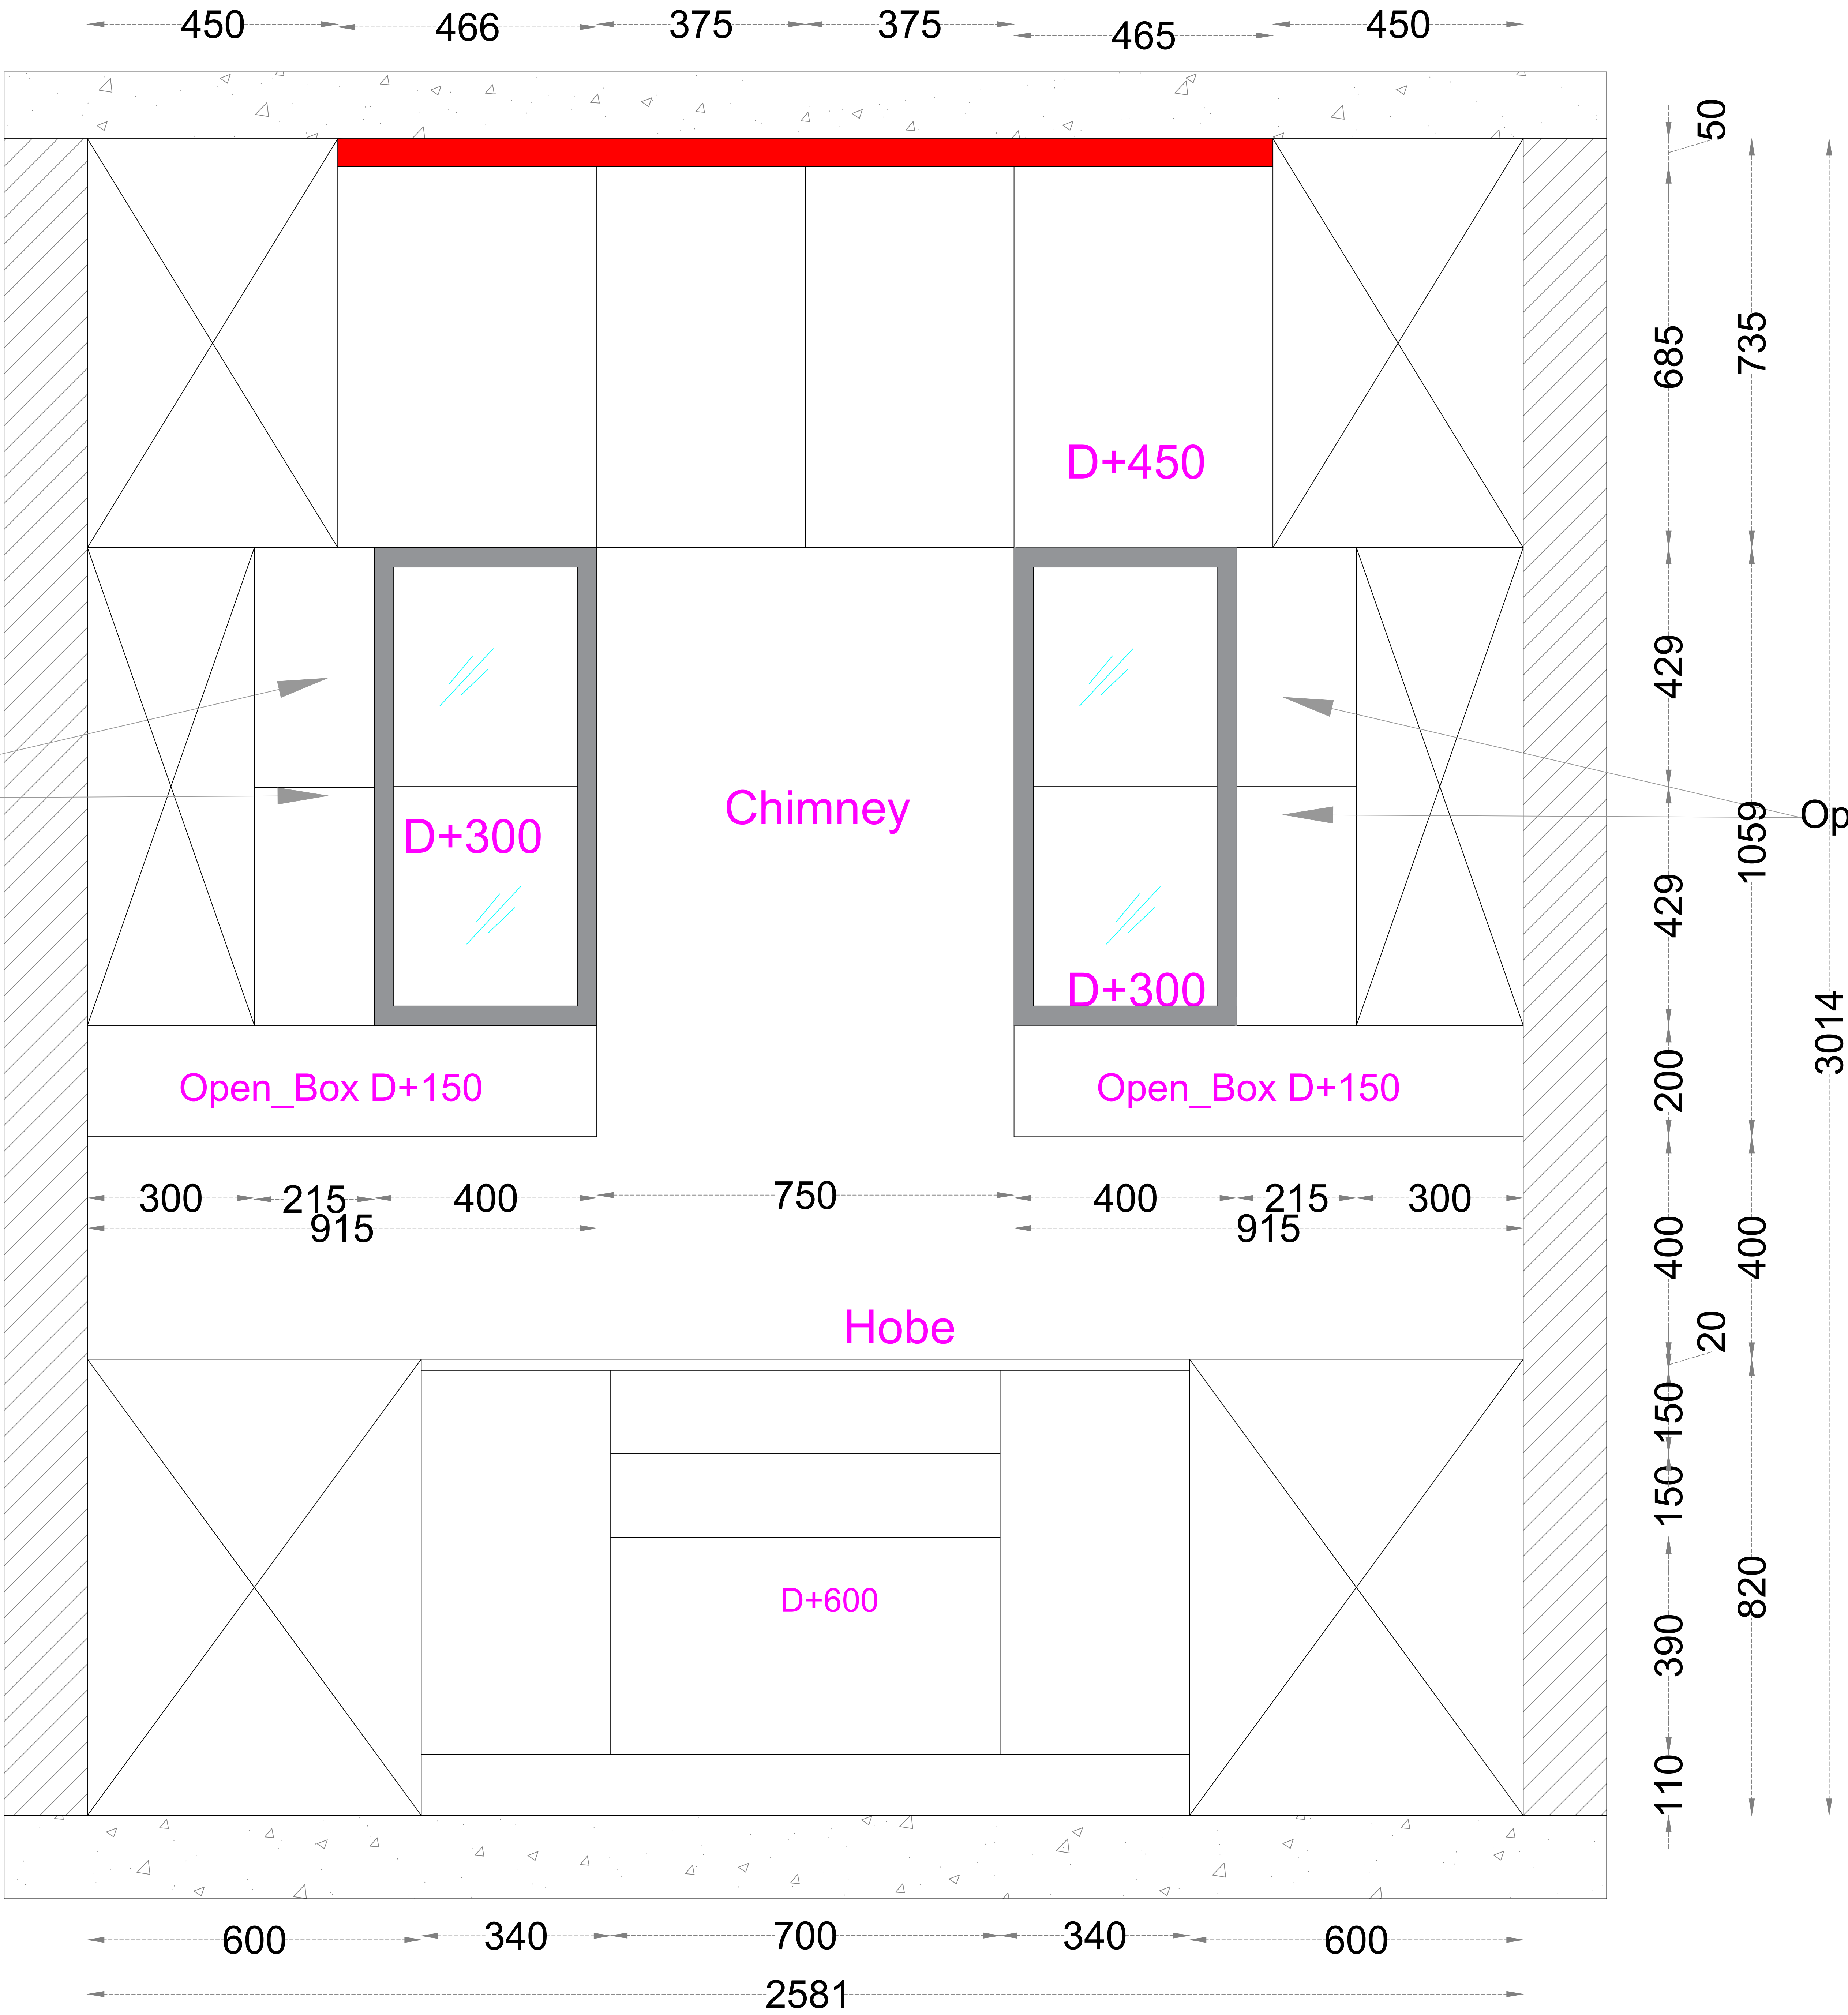

ALL DIMENSIONS ARE IN MILLIMETERS .
CONTRACTOR HAS TO CHECK & VERIFY ALL LEVELS, DATUM & DIMENSIONS ON SITE AND SHALL REPORT ANY DISCREPANCIES OR OMISSIONS ON SITE THIS OFFICE PRIOR TO THE START OF WORK & DURING THE CONSTRUCTION PHASE.
THIS DRAWING HAS TO BE READ & UNDERSTOOD IN CONJUNCTION WITH STRUCTURAL, MECHANICAL, ELECTRICAL AND/OR ANY OTHER CONSULTANT/S DOCUMENTATION, AS MAY BE APPLICABLE TO THE PROJECT PRIOR TO START OF WORK & IT'S DURATION.

TECHNICAL NOTE :
PROVIDED AS PER STRUCTURAL DRAWINGS & DETAILS.
ANY DISCREPENCY RELATED TO THIS DRAWING SHALL BE BROUGHT TO THE NOTICE OF THE CONCERNED PROJECT ARCHITECTS IMMEDIATELY BEFORE THE EXECUTION OF WORK.
LVLS MENTIONED IN THE DRAWING REFERS TO THE UNFINISHED LEVELS ON THE SITE.

COMPANY NAME
SPACICIOUS VENTURE
Address:
Address: Candeur Landmark Liberty blockD903
Varthur, Bengaluru, Karnataka 560087

CLIENT NAME :
Mr.

PROJECT NAME :
INCOR_C1301

DRAWING TITLE :
Kitchen_B

DRAWING NO :

SHEET NO :000

SCALE : N.T.S

TEAM Woodpeckers

DRAWN : Mohd Arfath

CHECKED : Syedfareed

DESIGNED : Syedfareed


DATE : 14-12-2025

ARCHITECTURAL DRAWING

NOTE :
THIS DRAWING IS THE EXCLUSIVE PROPERTY OF "SPACICIOUS VENTURE". AND THE REPRODUCTION OF ANY PART WITHOUT PRIOR WRITTEN CONSENT FROM THIS OFFICE IS A VIOLATION OF APPLICABLE LAWS.



NOTE :
THIS DRAWING IS THE EXCLUSIVE PROPERTY OF
"SPACICOUS VENTURE". AND THE
REPRODUCTION OF ANY PART WITHOUT PRIOR WRITTEN CONSENT
FROM THIS OFFICE IS A VIOLATION OF APPLICABLE LAWS.

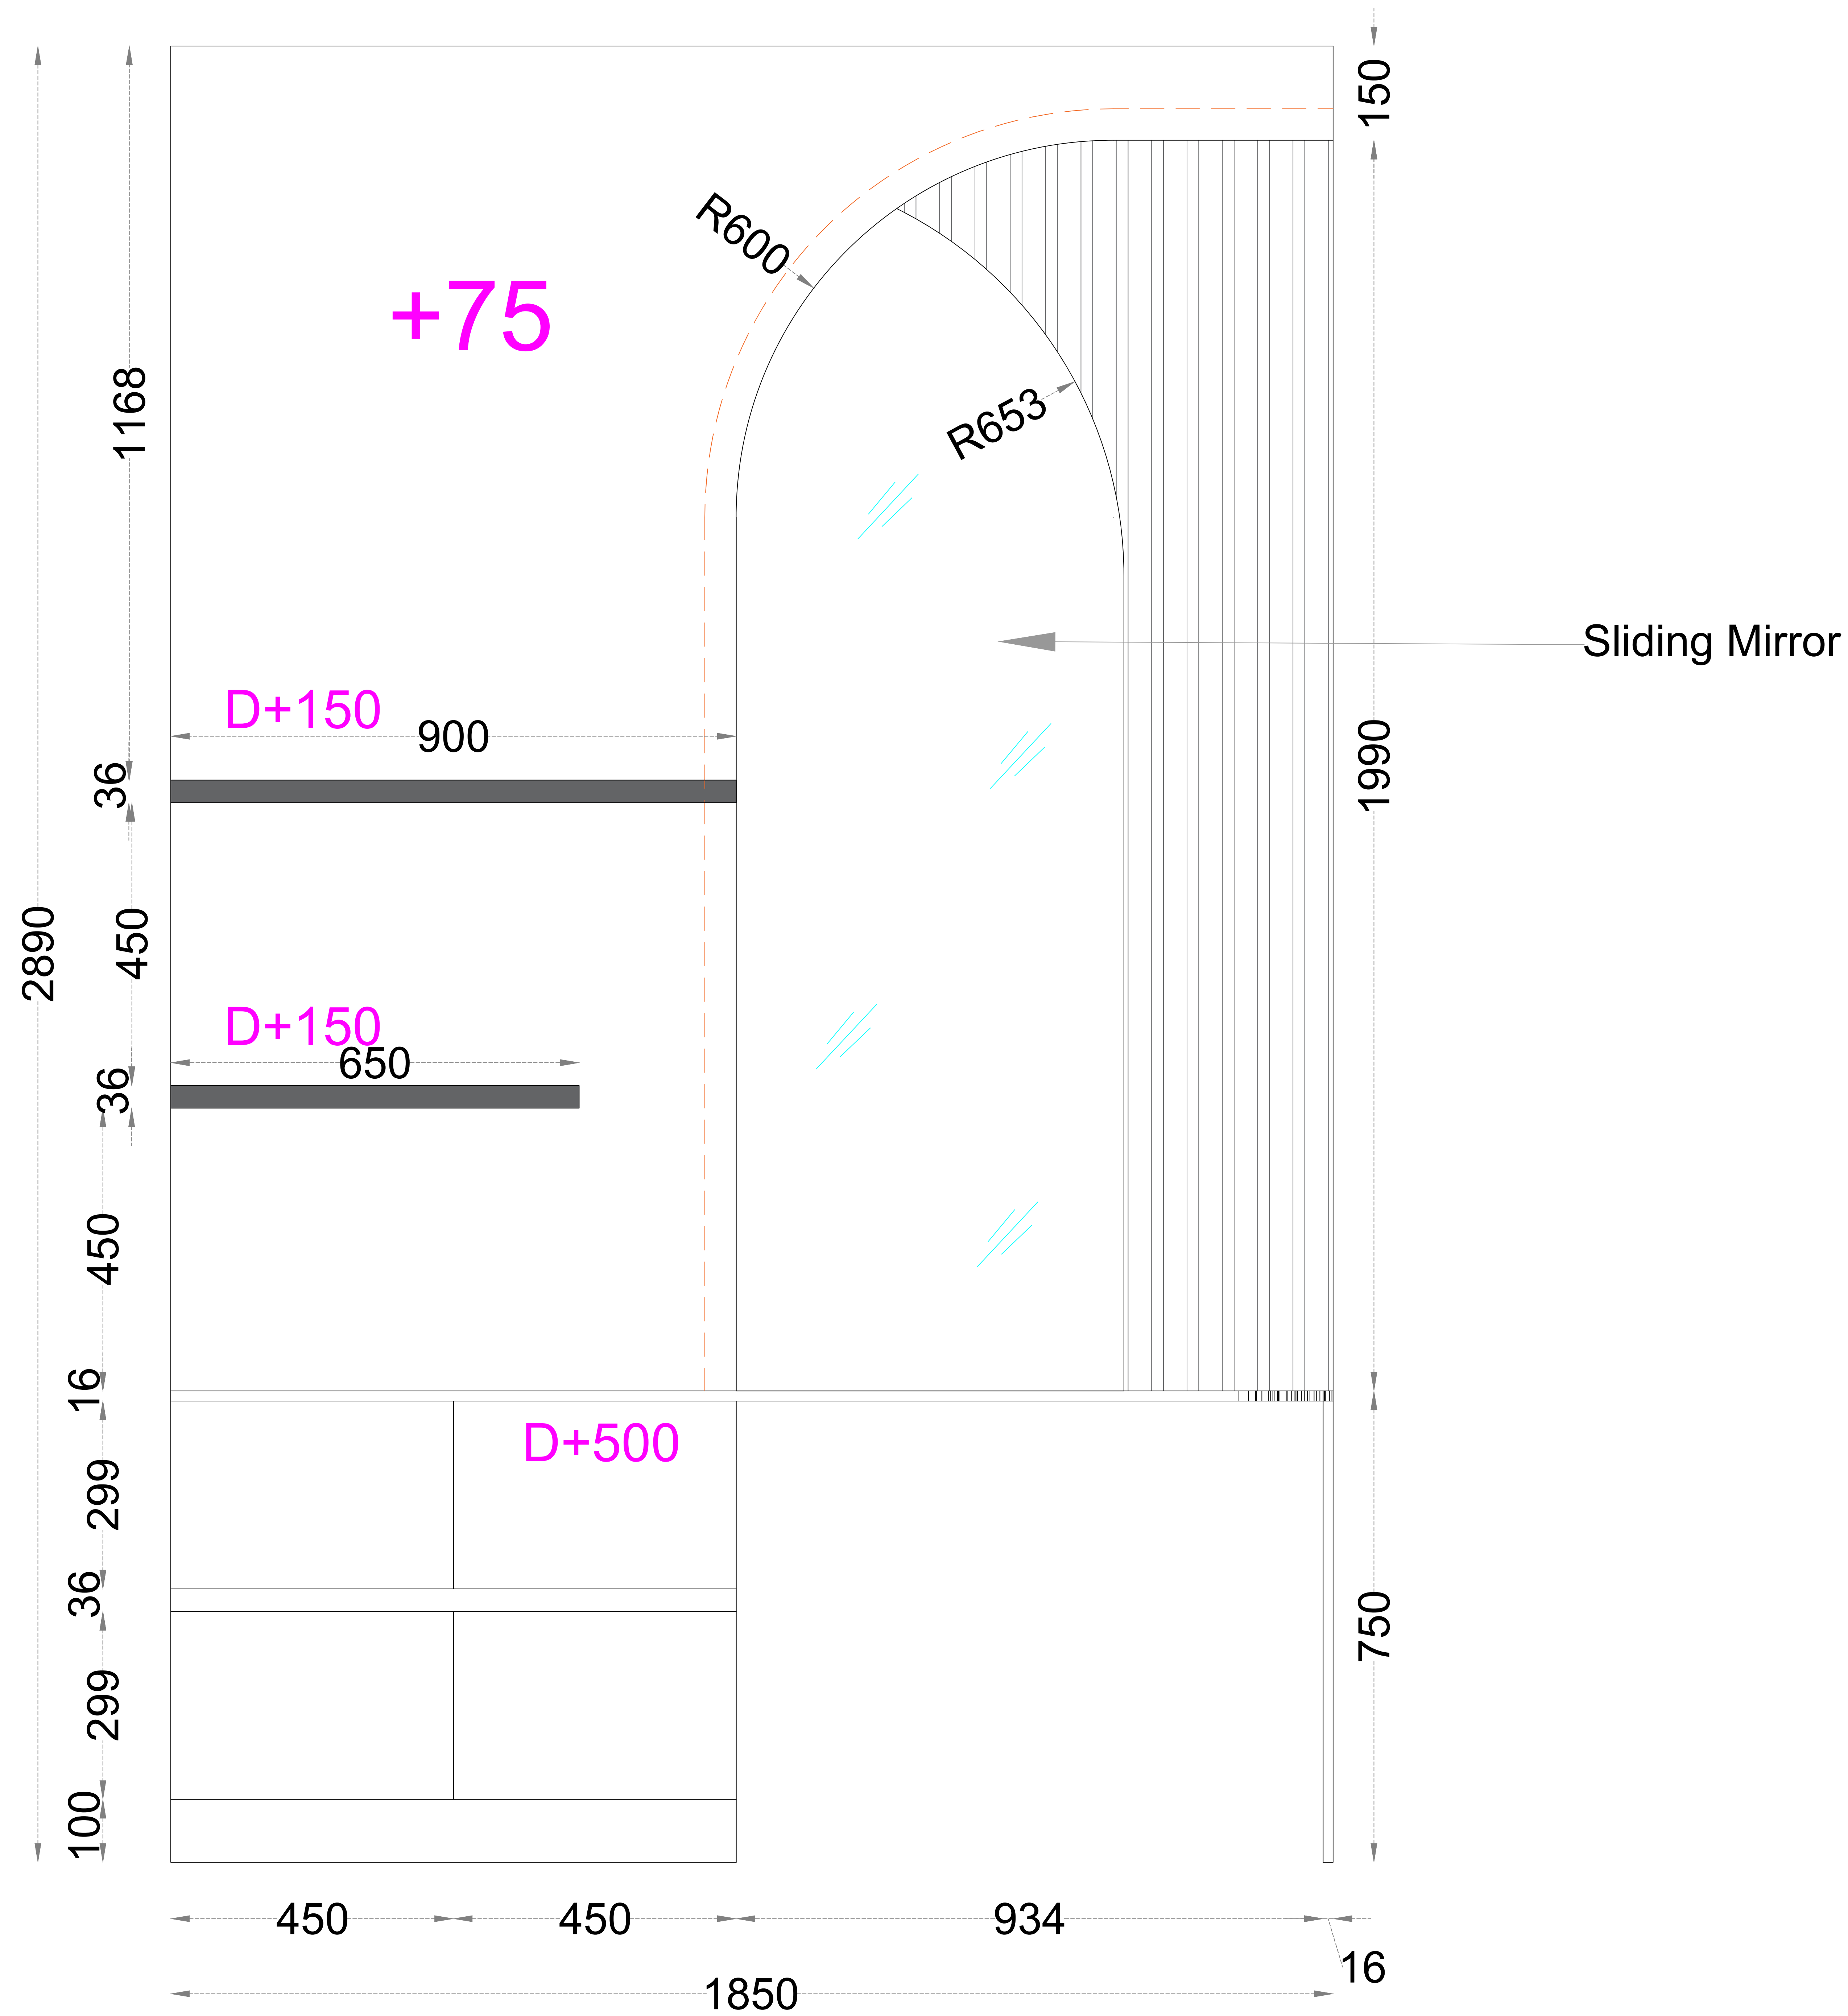

ALL DIMENSIONS ARE IN MILLIMETERS .
CONTRACTOR HAS TO CHECK & VERIFY ALL LEVELS,
DATUM & DIMENSIONS ON SITE AND SHALL REPORT ANY
DISCREPANCIES OR OMISSIONS ON SITE THIS OFFICE PRIOR TO THE
START OF WORK & DURING THE CONSTRUCTION PHASE.

THIS DRAWING HAS TO BE READ & UNDERSTOOD IN CONJUNCTION
WITH STRUCTURAL, MECHANICAL, ELECTRICAL AND/OR ANY OTHER
CONSULTANT/S DOCUMENTATION, AS MAY BE APPLICABLE TO THE
PROJECT PRIOR TO START OF WORK & IT'S DURATION.

TECHNICAL NOTE :

PROVIDED AS PER STRUCTURAL DRAWINGS & DETAILS.

ANY DISCREPANCY RELATED TO THIS DRAWING SHALL BE BROUGHT TO THE NOTICE OF THE CONCERNED PROJECT ARCHITECTS IMMEDIATELY BEFORE THE EXECUTION OF WORK.

LVLS MENTIONED IN THE DRAWING REFERS TO THE UNFINISHED LEVELS ON THE SITE.

COMPANY NAME

SPACIOUS VENTURE

Address:
Address: Candeur Landmark Liberty blockD903
Varthur, Bengaluru, Karnataka 560087

CLIENT NAME :

Mr.

PROJECT NAME :

INCOR_C1301

DRAWING TITLE :

MBR_Dressing

DRAWING NO :

SHEET NO	:000
----------	------

SCALE	: N.T.S
-------	---------

TEAM	Woodpeckers
------	-------------

DRAWN	: Mohd Arfath
-------	---------------


CHECKED	: Syedfareed
---------	--------------

DESIGNED	: Syedfareed
----------	--------------

DATE	: 14-12-2025
------	--------------

ARCHITECTURAL DRAWING

NOTE :
THIS DRAWING IS THE EXCLUSIVE PROPERTY OF
"SPACICIOUS VENTURE". AND THE
REPRODUCTION OF ANY PART WITHOUT PRIOR WRITTEN CONSENT
FROM THIS OFFICE IS A VIOLATION OF APPLICABLE LAWS.

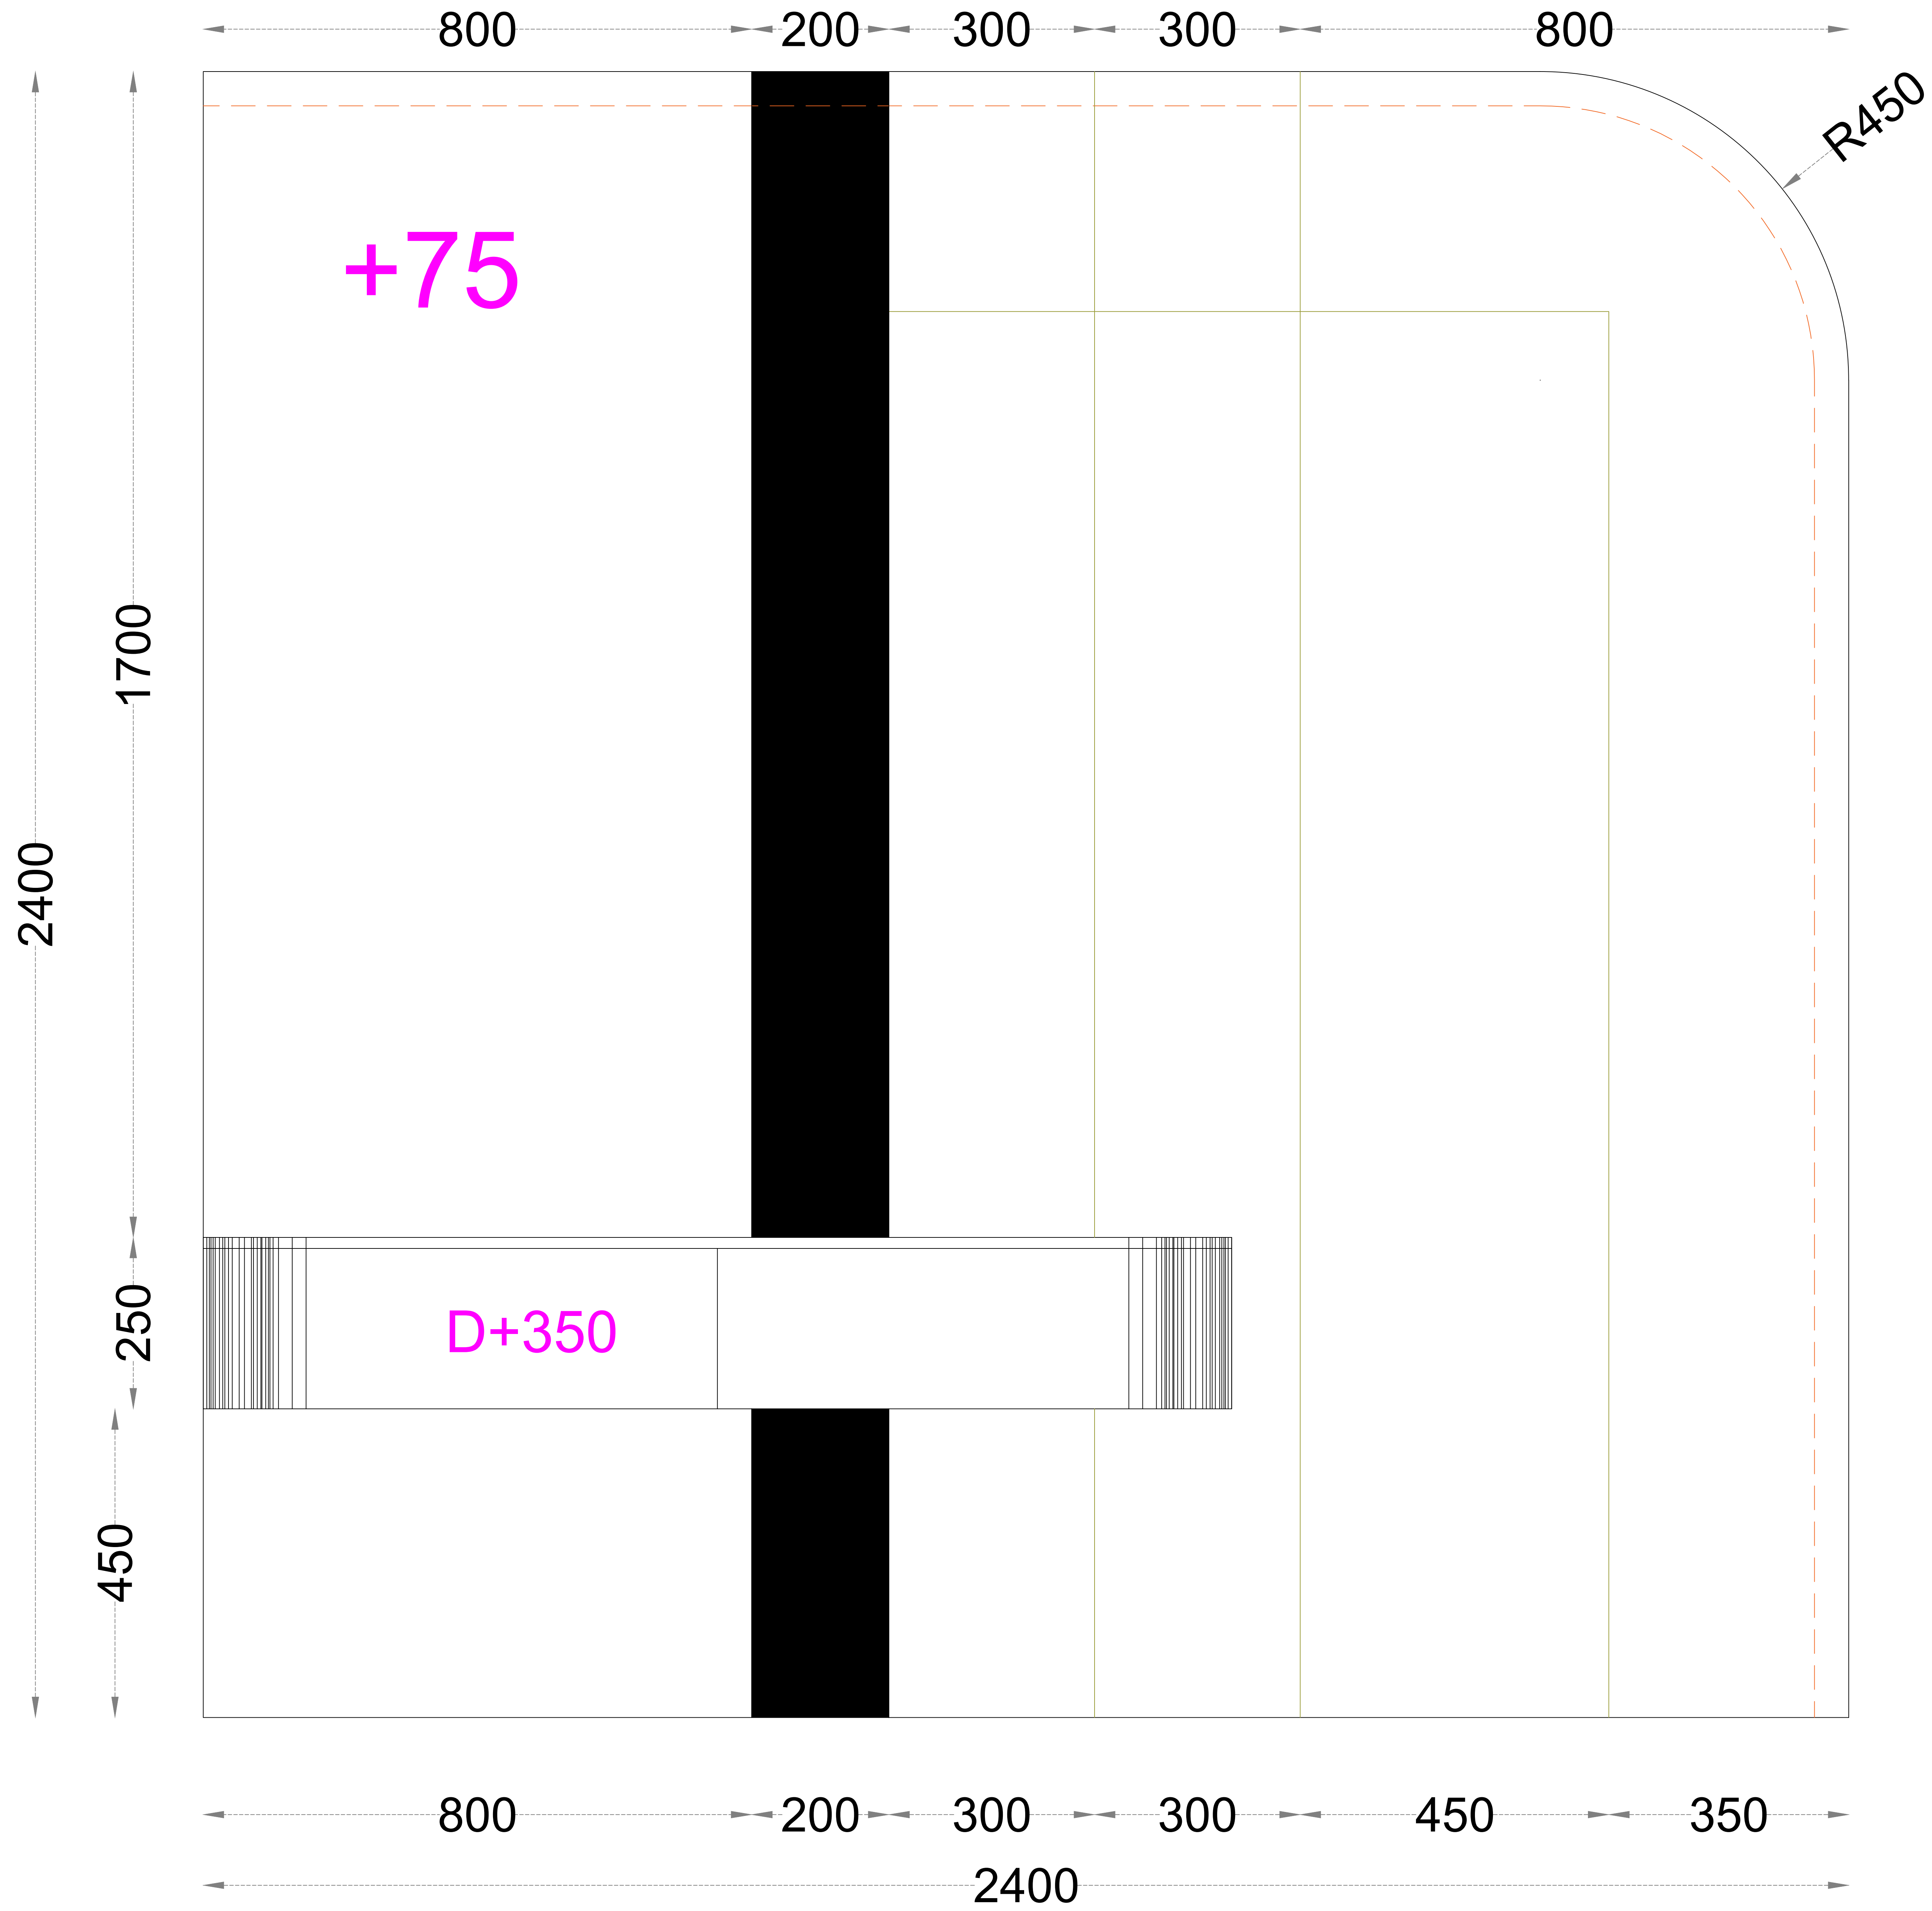

MBR_TV

ALL DIMENSIONS ARE IN MILLIMETERS .
CONTRACTOR HAS TO CHECK & VERIFY ALL LEVELS, DATUM & DIMENSIONS ON SITE AND SHALL REPORT ANY DISCREPANCIES OR OMISSIONS ON SITE THIS OFFICE PRIOR TO THE START OF WORK & DURING THE CONSTRUCTION PHASE.

THIS DRAWING HAS TO BE READ & UNDERSTOOD IN CONJUNCTION WITH STRUCTURAL, MECHANICAL, ELECTRICAL AND/OR ANY OTHER CONSULTANT/S DOCUMENTATION, AS MAY BE APPLICABLE TO THE PROJECT PRIOR TO START OF WORK & IT'S DURATION.

TECHNICAL NOTE :

PROVIDED AS PER STRUCTURAL DRAWINGS & DETAILS.

ANY DISCREPENCY RELATED TO THIS DRAWING SHALL BE BROUGHT TO THE NOTICE OF THE CONCERNED PROJECT ARCHITECTS IMMEDIATELY BEFORE THE EXECUTION OF WORK.

LVLS MENTIONED IN THE DRAWING REFERS TO THE UNFINISHED LEVELS ON THE SITE.

COMPANY NAME
SPACICOUS VENTURE

Address:
Address: Candeur Landmark Liberty blockD903
Varthur, Bengaluru, Karnataka 560087

CLIENT NAME :

Mr.

PROJECT NAME :

INCOR_C1301

DRAWING TITLE :

MBR_Tv Unit

DRAWING NO :

SHEET NO :000

SCALE : N.T.S

TEAM Woodpeckers

DRAWN : Mohd Arfath


CHECKED : Syedfareed


DESIGNED : Syedfareed

DATE : 14-12-2025

ARCHITECTURAL DRAWING

NOTE :
THIS DRAWING IS THE EXCLUSIVE PROPERTY OF "SPACICOUS VENTURE". AND THE REPRODUCTION OF ANY PART WITHOUT PRIOR WRITTEN CONSENT FROM THIS OFFICE IS A VIOLATION OF APPLICABLE LAWS.

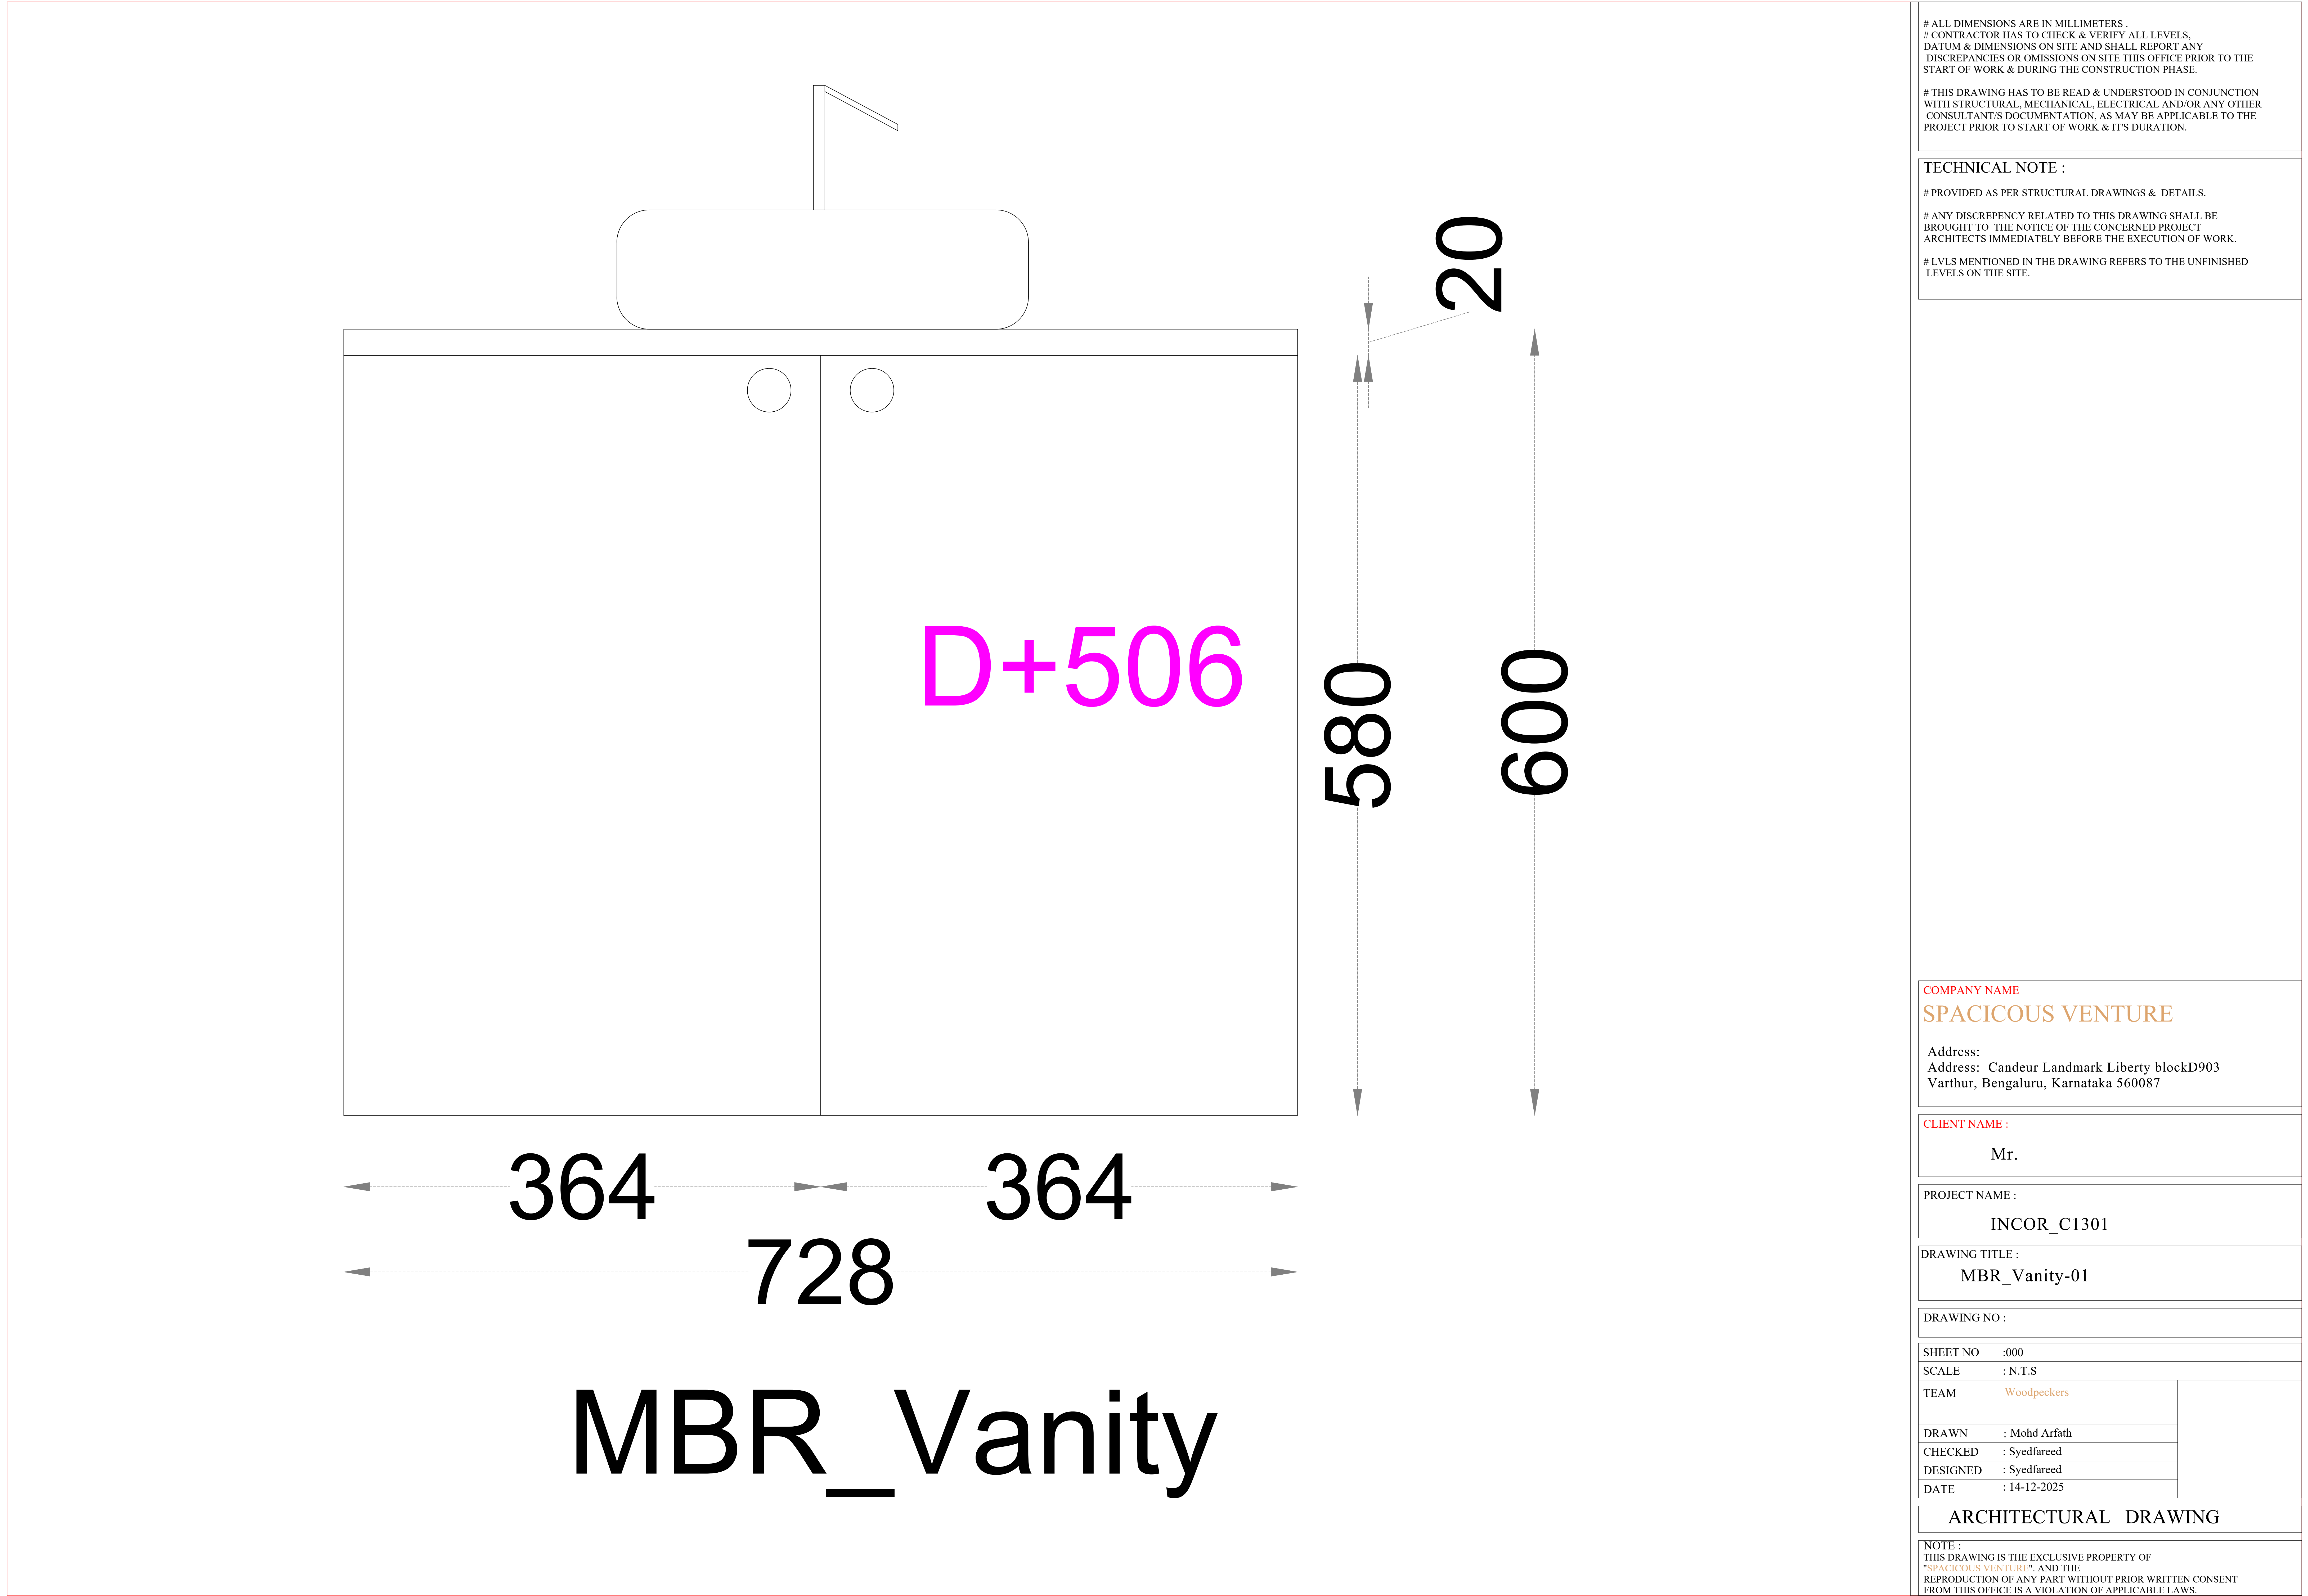

 

ALL DIMENSIONS ARE IN MILLIMETERS .
CONTRACTOR HAS TO CHECK & VERIFY ALL LEVELS, DATUM & DIMENSIONS ON SITE AND SHALL REPORT ANY DISCREPANCIES OR OMISSIONS ON SITE THIS OFFICE PRIOR TO THE START OF WORK & DURING THE CONSTRUCTION PHASE.

THIS DRAWING HAS TO BE READ & UNDERSTOOD IN CONJUNCTION WITH STRUCTURAL, MECHANICAL, ELECTRICAL AND/OR ANY OTHER CONSULTANT/S DOCUMENTATION, AS MAY BE APPLICABLE TO THE PROJECT PRIOR TO START OF WORK & IT'S DURATION.

TECHNICAL NOTE :

PROVIDED AS PER STRUCTURAL DRAWINGS & DETAILS.

ANY DISCREPENCY RELATED TO THIS DRAWING SHALL BE BROUGHT TO THE NOTICE OF THE CONCERNED PROJECT ARCHITECTS IMMEDIATELY BEFORE THE EXECUTION OF WORK.

LVLS MENTIONED IN THE DRAWING REFERS TO THE UNFINISHED LEVELS ON THE SITE.

COMPANY NAME
SPACICOUS VENTURE

Address:
Address: Candeur Landmark Liberty blockD903
Varthur, Bengaluru, Karnataka 560087

CLIENT NAME :

Mr.

PROJECT NAME :

INCOR_C1301

DRAWING TITLE :

MBR_Vanity-02


DRAWING NO :

SHEET NO :000
SCALE : N.T.S

TEAM	Woodpeckers	
DRAWN	: Mohd Arfath	
CHECKED	: Syedfareed	
DESIGNED	: Syedfareed	
DATE	: 14-12-2025	

ARCHITECTURAL DRAWING

NOTE :
THIS DRAWING IS THE EXCLUSIVE PROPERTY OF "SPACICOUS VENTURE". AND THE REPRODUCTION OF ANY PART WITHOUT PRIOR WRITTEN CONSENT FROM THIS OFFICE IS A VIOLATION OF APPLICABLE LAWS.

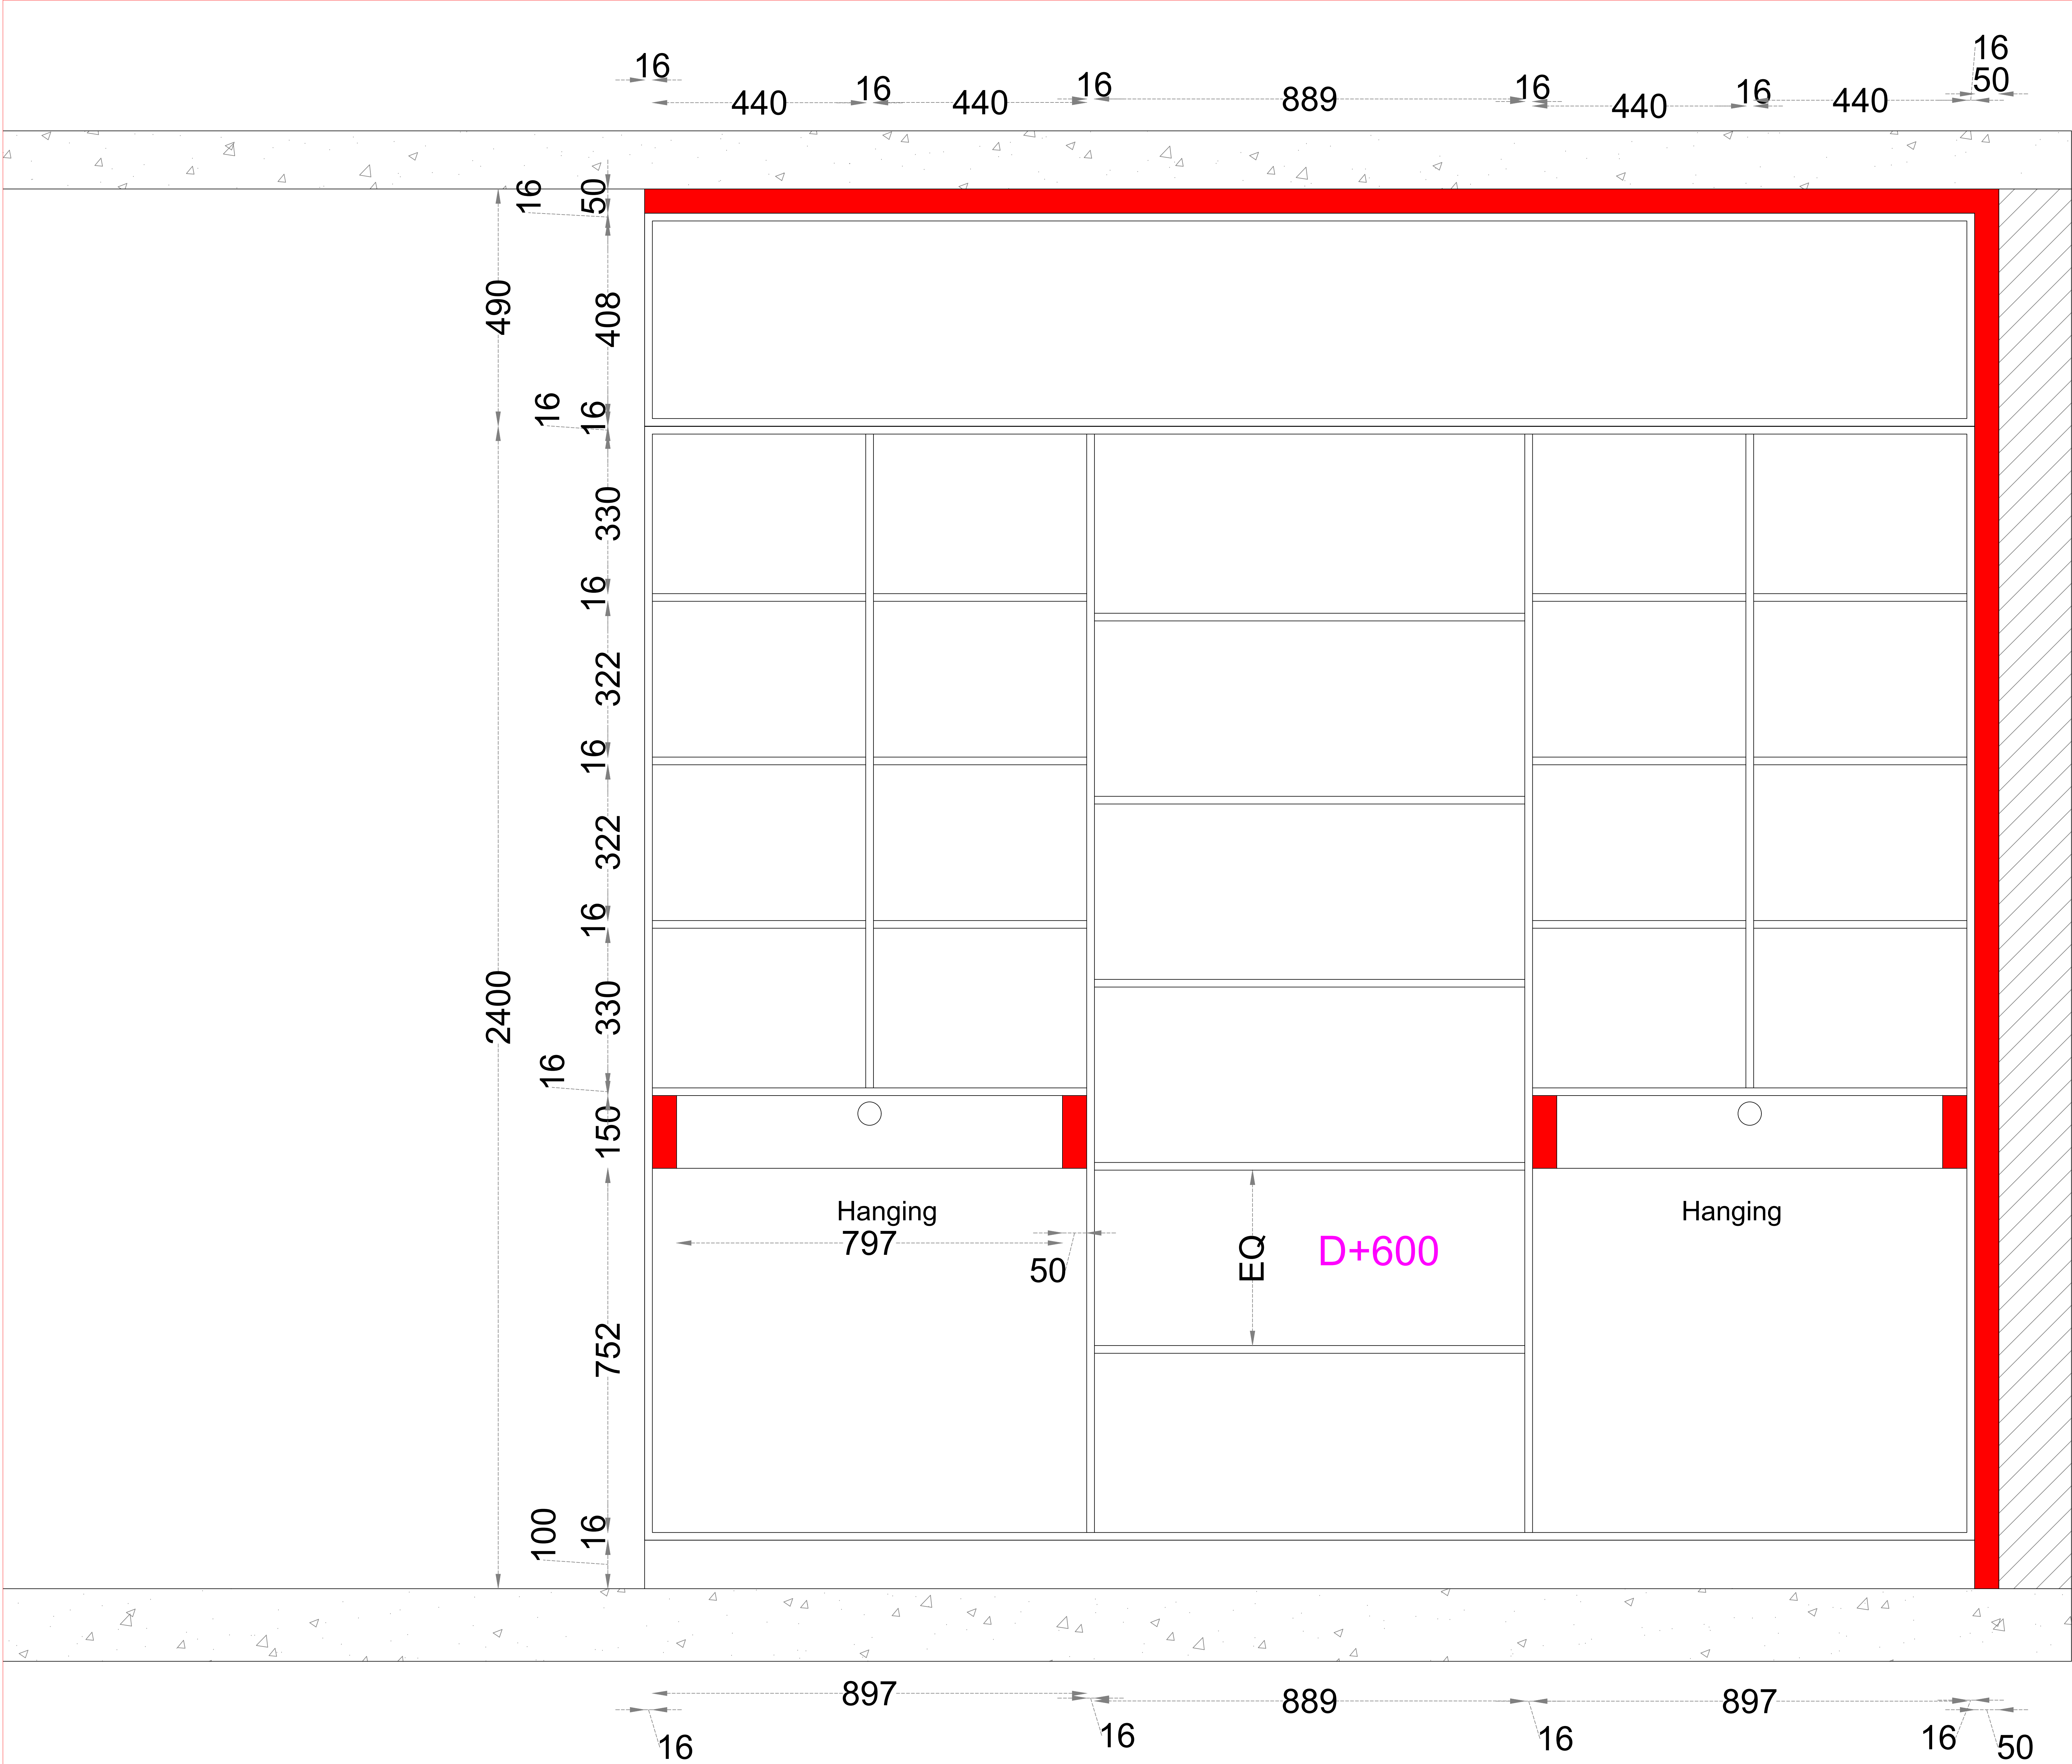

ALL DIMENSIONS ARE IN MILLIMETERS .
CONTRACTOR HAS TO CHECK & VERIFY ALL LEVELS, DATUM & DIMENSIONS ON SITE AND SHALL REPORT ANY DISCREPANCIES OR OMISSIONS ON SITE THIS OFFICE PRIOR TO THE START OF WORK & DURING THE CONSTRUCTION PHASE.
THIS DRAWING HAS TO BE READ & UNDERSTOOD IN CONJUNCTION WITH STRUCTURAL, MECHANICAL, ELECTRICAL AND/OR ANY OTHER CONSULTANT/S DOCUMENTATION, AS MAY BE APPLICABLE TO THE PROJECT PRIOR TO START OF WORK & IT'S DURATION.

TECHNICAL NOTE :
PROVIDED AS PER STRUCTURAL DRAWINGS & DETAILS.
ANY DISCREPENCY RELATED TO THIS DRAWING SHALL BE BROUGHT TO THE NOTICE OF THE CONCERNED PROJECT ARCHITECTS IMMEDIATELY BEFORE THE EXECUTION OF WORK.
LVLS MENTIONED IN THE DRAWING REFERS TO THE UNFINISHED LEVELS ON THE SITE.

COMPANY NAME
SPACICOUS VENTURE
Address:
Address: Candeur Landmark Liberty blockD903
Varthur, Bengaluru, Karnataka 560087

CLIENT NAME :
Mr.

PROJECT NAME :
INCOR_C1301

DRAWING TITLE :
MBR_WRD-_Internal


DRAWING NO :

SHEET NO	:000
SCALE	: N.T.S
TEAM	Woodpeckers
DRAWN	: Mohd Arfath
CHECKED	: Syedfareed
DESIGNED	: Syedfareed
DATE	: 14-12-2025

ARCHITECTURAL DRAWING

NOTE :
THIS DRAWING IS THE EXCLUSIVE PROPERTY OF "SPACICOUS VENTURE". AND THE REPRODUCTION OF ANY PART WITHOUT PRIOR WRITTEN CONSENT FROM THIS OFFICE IS A VIOLATION OF APPLICABLE LAWS.

MBR_Internal

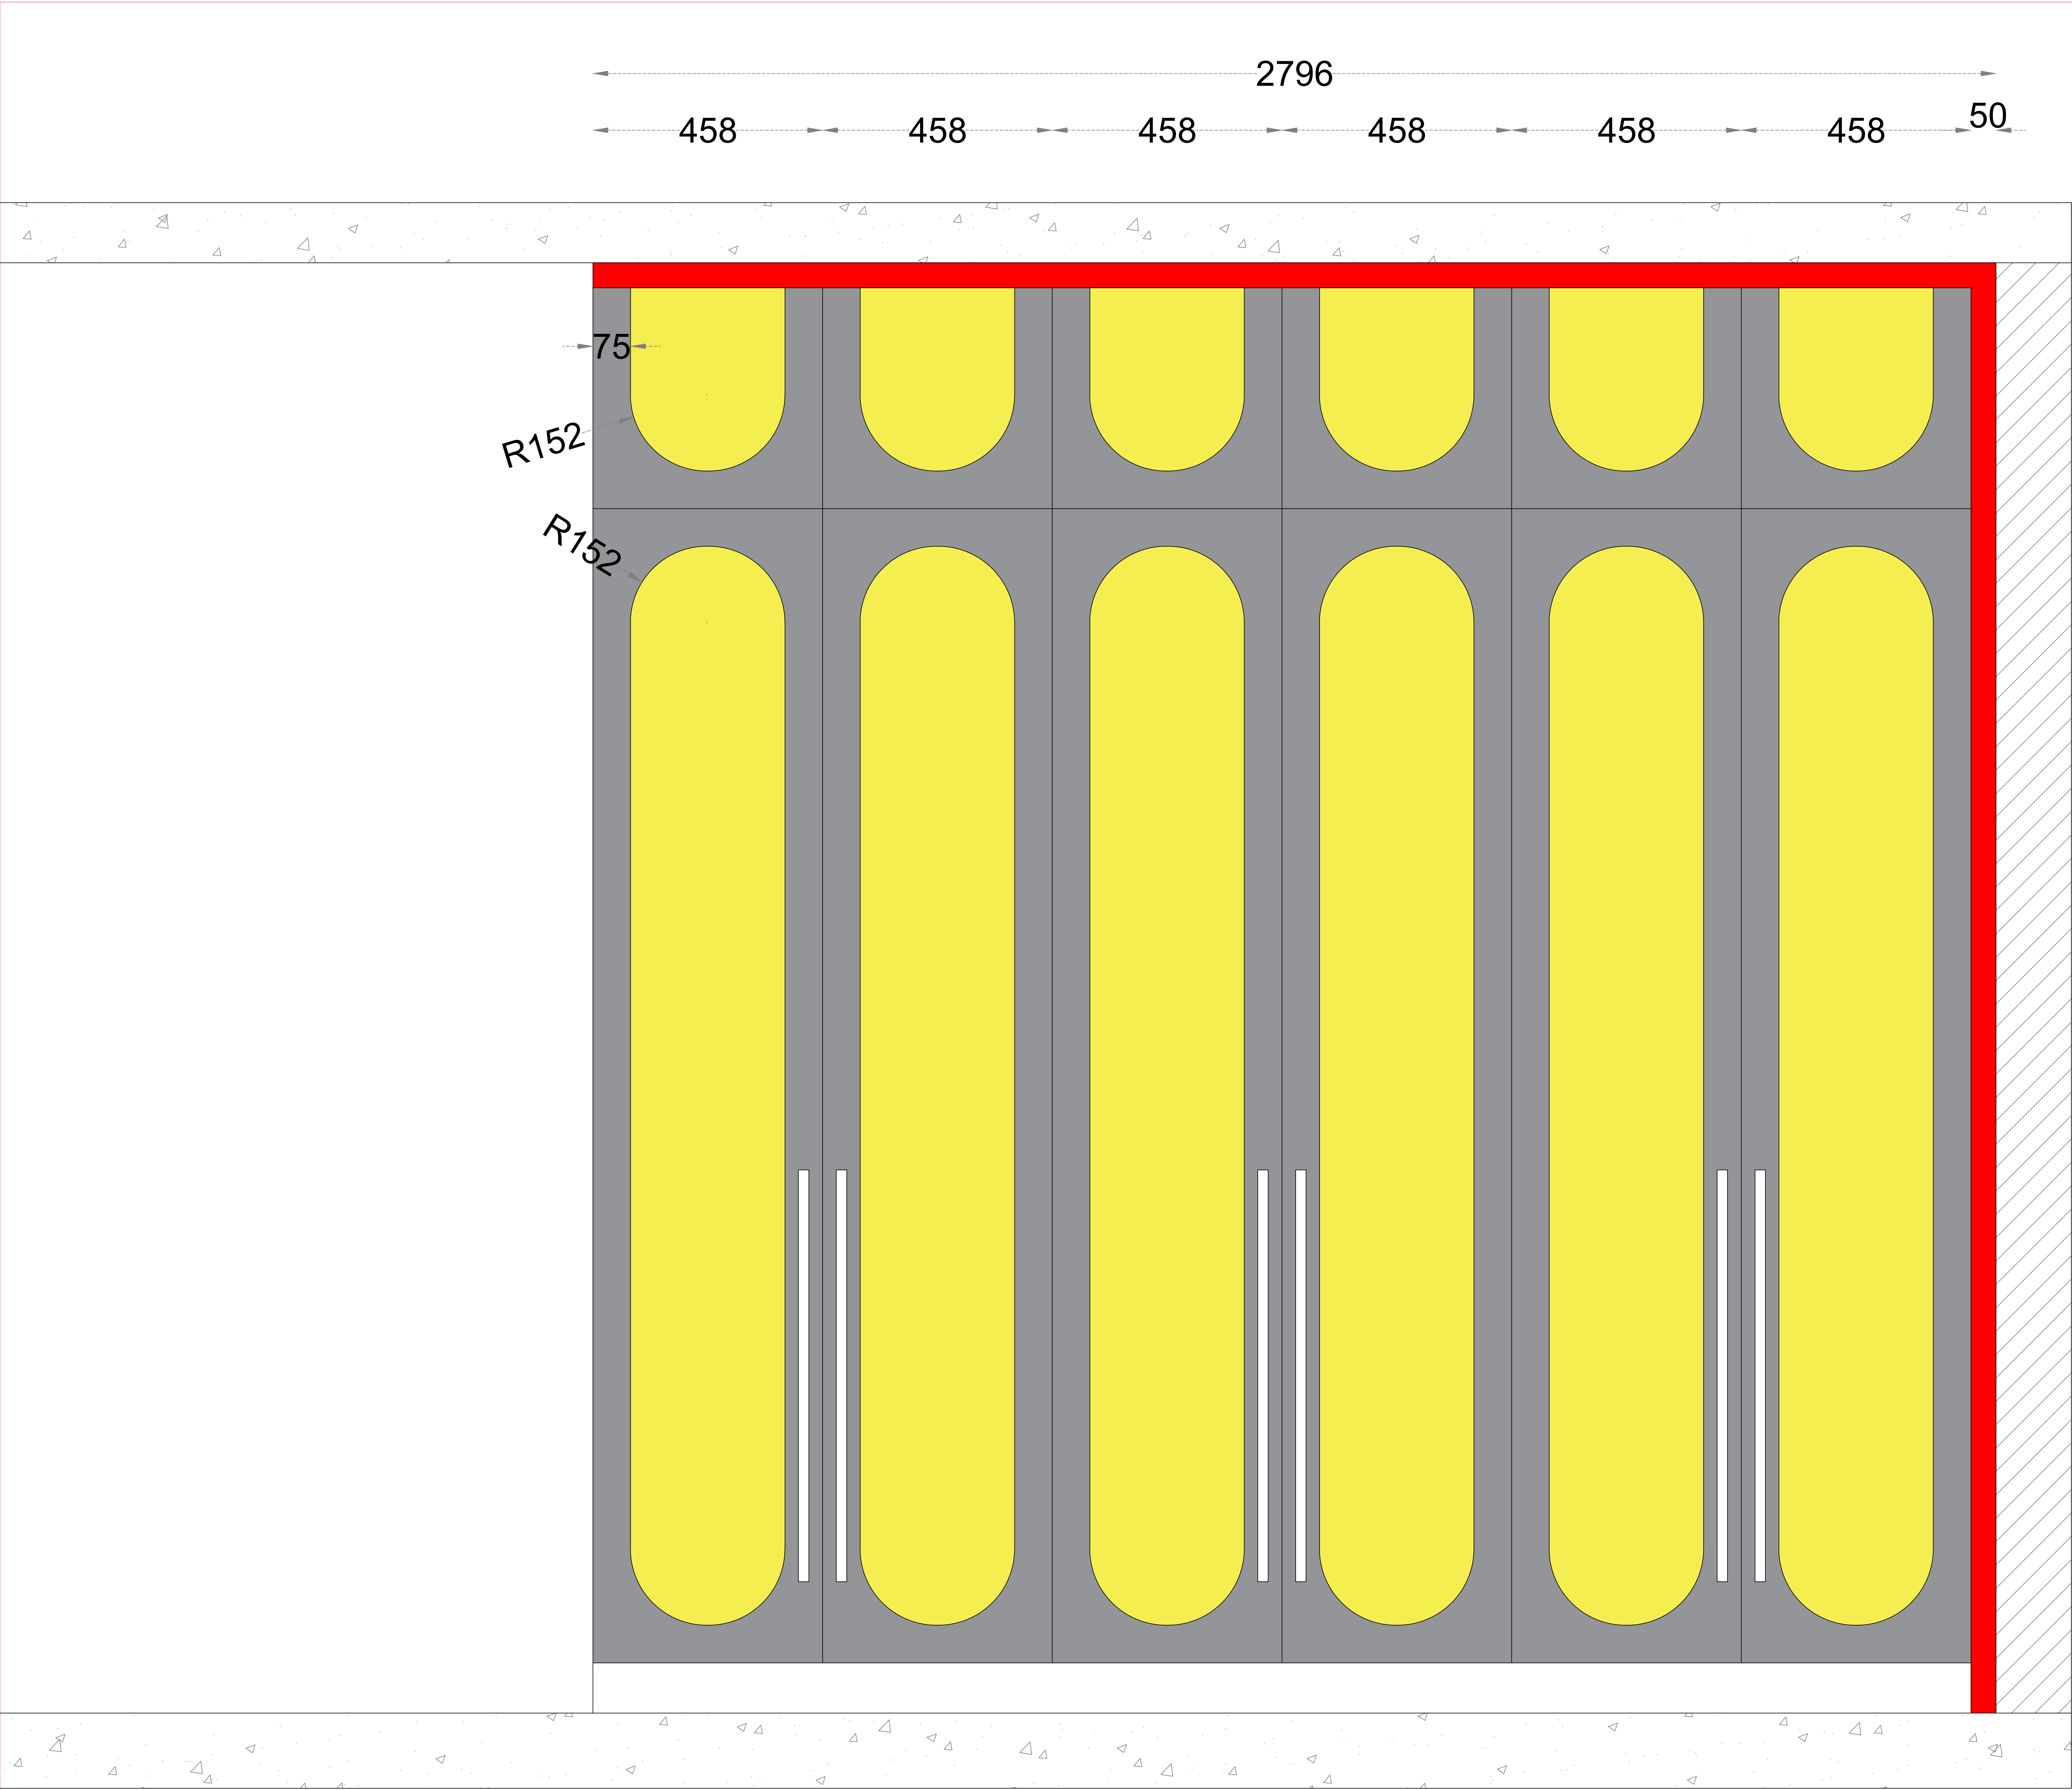

MBR_External

ALL DIMENSIONS ARE IN MILLIMETERS .
CONTRACTOR HAS TO CHECK & VERIFY ALL LEVELS, DATUM & DIMENSIONS ON SITE AND SHALL REPORT ANY DISCREPANCIES OR OMISSIONS ON SITE THIS OFFICE PRIOR TO THE START OF WORK & DURING THE CONSTRUCTION PHASE.

THIS DRAWING HAS TO BE READ & UNDERSTOOD IN CONJUNCTION WITH STRUCTURAL, MECHANICAL, ELECTRICAL AND/OR ANY OTHER CONSULTANT/S DOCUMENTATION, AS MAY BE APPLICABLE TO THE PROJECT PRIOR TO START OF WORK & IT'S DURATION.

TECHNICAL NOTE :

PROVIDED AS PER STRUCTURAL DRAWINGS & DETAILS.

ANY DISCREPENCY RELATED TO THIS DRAWING SHALL BE BROUGHT TO THE NOTICE OF THE CONCERNED PROJECT ARCHITECTS IMMEDIATELY BEFORE THE EXECUTION OF WORK.

LVL'S MENTIONED IN THE DRAWING REFERS TO THE UNFINISHED LEVELS ON THE SITE.

COMPANY NAME
SPACICOUS VENTURE

Address:
Address: Candeur Landmark Liberty blockD903
Varthur, Bengaluru, Karnataka 560087

CLIENT NAME :

Mr.

PROJECT NAME :

INCOR_C1301

DRAWING TITLE :

MBR_WRD-_External

DRAWING NO :

SHEET NO :000

SCALE : N.T.S

TEAM Woodpeckers

DRAWN	: Mohd Arfath
CHECKED	: Syedfareed
DESIGNED	: Syedfareed
DATE	: 14-12-2025

ARCHITECTURAL DRAWING

NOTE :
THIS DRAWING IS THE EXCLUSIVE PROPERTY OF "SPACICOUS VENTURE". AND THE REPRODUCTION OF ANY PART WITHOUT PRIOR WRITTEN CONSENT FROM THIS OFFICE IS A VIOLATION OF APPLICABLE LAWS.

ALL DIMENSIONS ARE IN MILLIMETERS .
CONTRACTOR HAS TO CHECK & VERIFY ALL LEVELS, DATUM & DIMENSIONS ON SITE AND SHALL REPORT ANY DISCREPANCIES OR OMISSIONS ON SITE THIS OFFICE PRIOR TO THE START OF WORK & DURING THE CONSTRUCTION PHASE.

THIS DRAWING HAS TO BE READ & UNDERSTOOD IN CONJUNCTION WITH STRUCTURAL, MECHANICAL, ELECTRICAL AND/OR ANY OTHER CONSULTANT/S DOCUMENTATION, AS MAY BE APPLICABLE TO THE PROJECT PRIOR TO START OF WORK & IT'S DURATION.

TECHNICAL NOTE :

PROVIDED AS PER STRUCTURAL DRAWINGS & DETAILS.

ANY DISCREPENCY RELATED TO THIS DRAWING SHALL BE BROUGHT TO THE NOTICE OF THE CONCERNED PROJECT ARCHITECTS IMMEDIATELY BEFORE THE EXECUTION OF WORK.

LVLS MENTIONED IN THE DRAWING REFERS TO THE UNFINISHED LEVELS ON THE SITE.

COMPANY NAME
SPACICOUS VENTURE

Address:
Address: Candeur Landmark Liberty blockD903
Varthur, Bengaluru, Karnataka 560087

CLIENT NAME :

Mr.

PROJECT NAME :

INCOR_C1301

DRAWING TITLE :

CBR_Low Seating

DRAWING NO :

SHEET NO :000

SCALE : N.T.S

TEAM Woodpeckers

DRAWN : Mohd Arfath


CHECKED : Syedfareed


DESIGNED : Syedfareed

DATE : 14-12-2025

ARCHITECTURAL DRAWING

NOTE :
THIS DRAWING IS THE EXCLUSIVE PROPERTY OF "SPACICOUS VENTURE". AND THE REPRODUCTION OF ANY PART WITHOUT PRIOR WRITTEN CONSENT FROM THIS OFFICE IS A VIOLATION OF APPLICABLE LAWS.

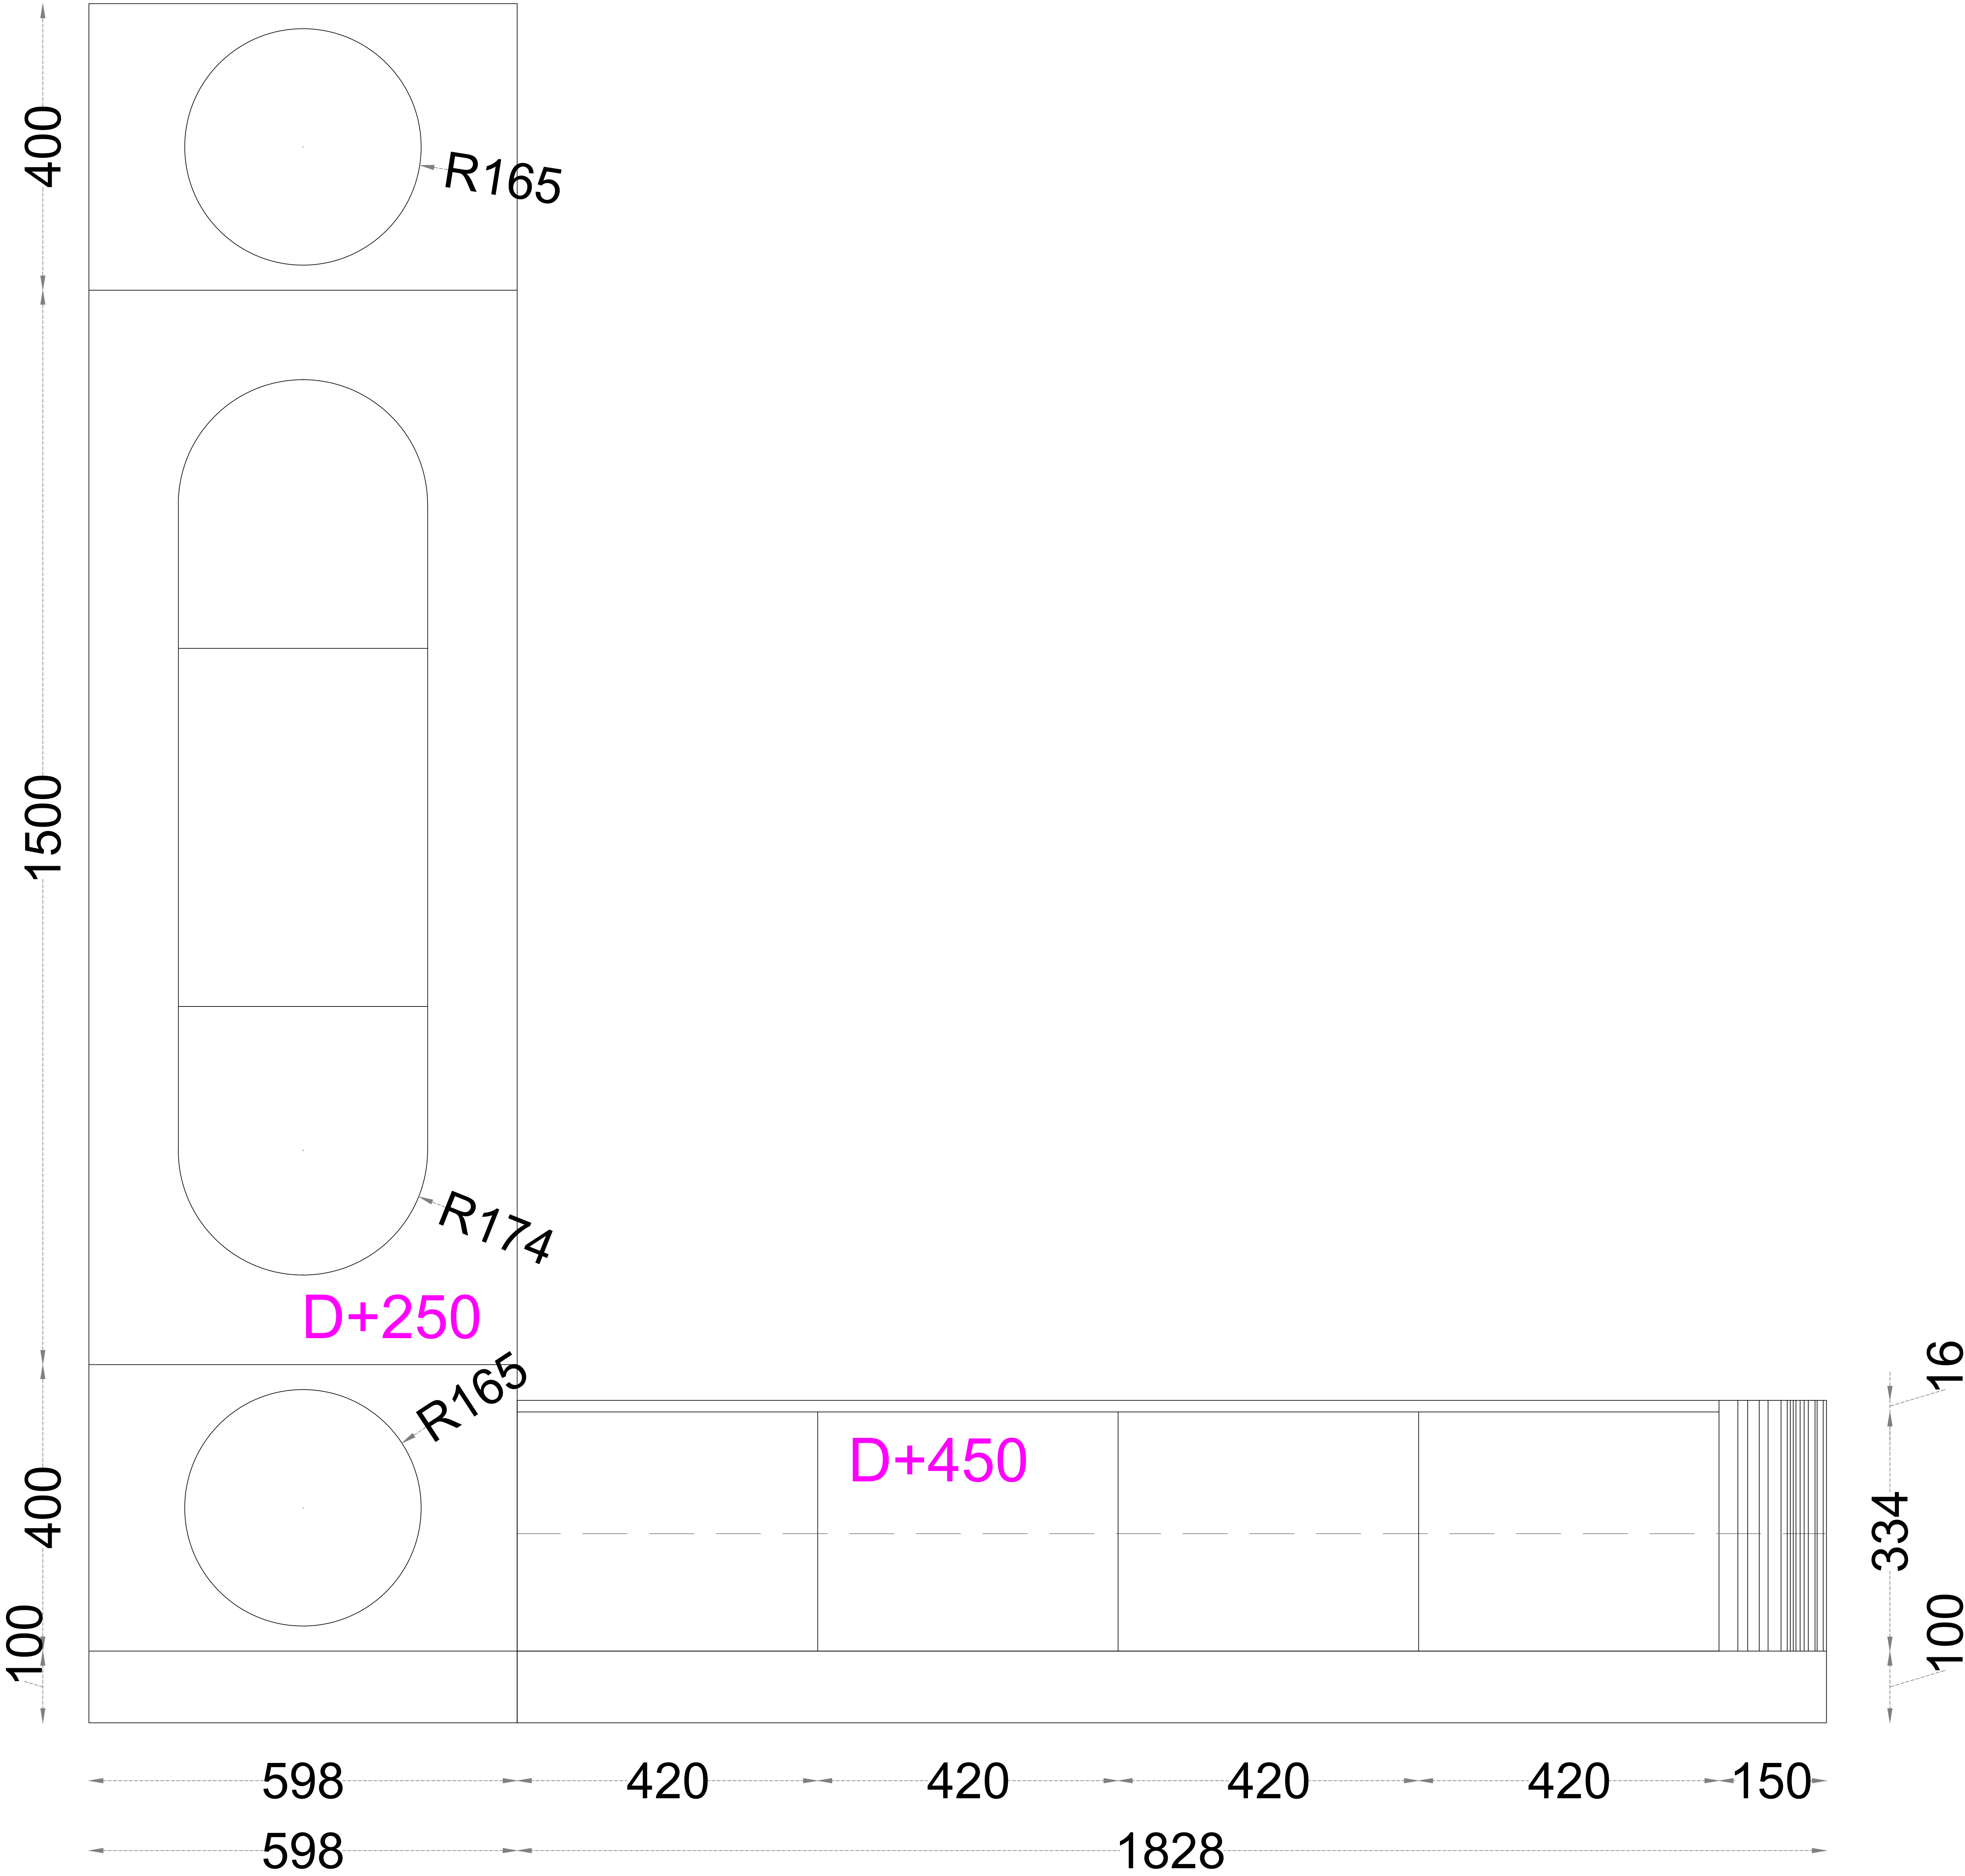

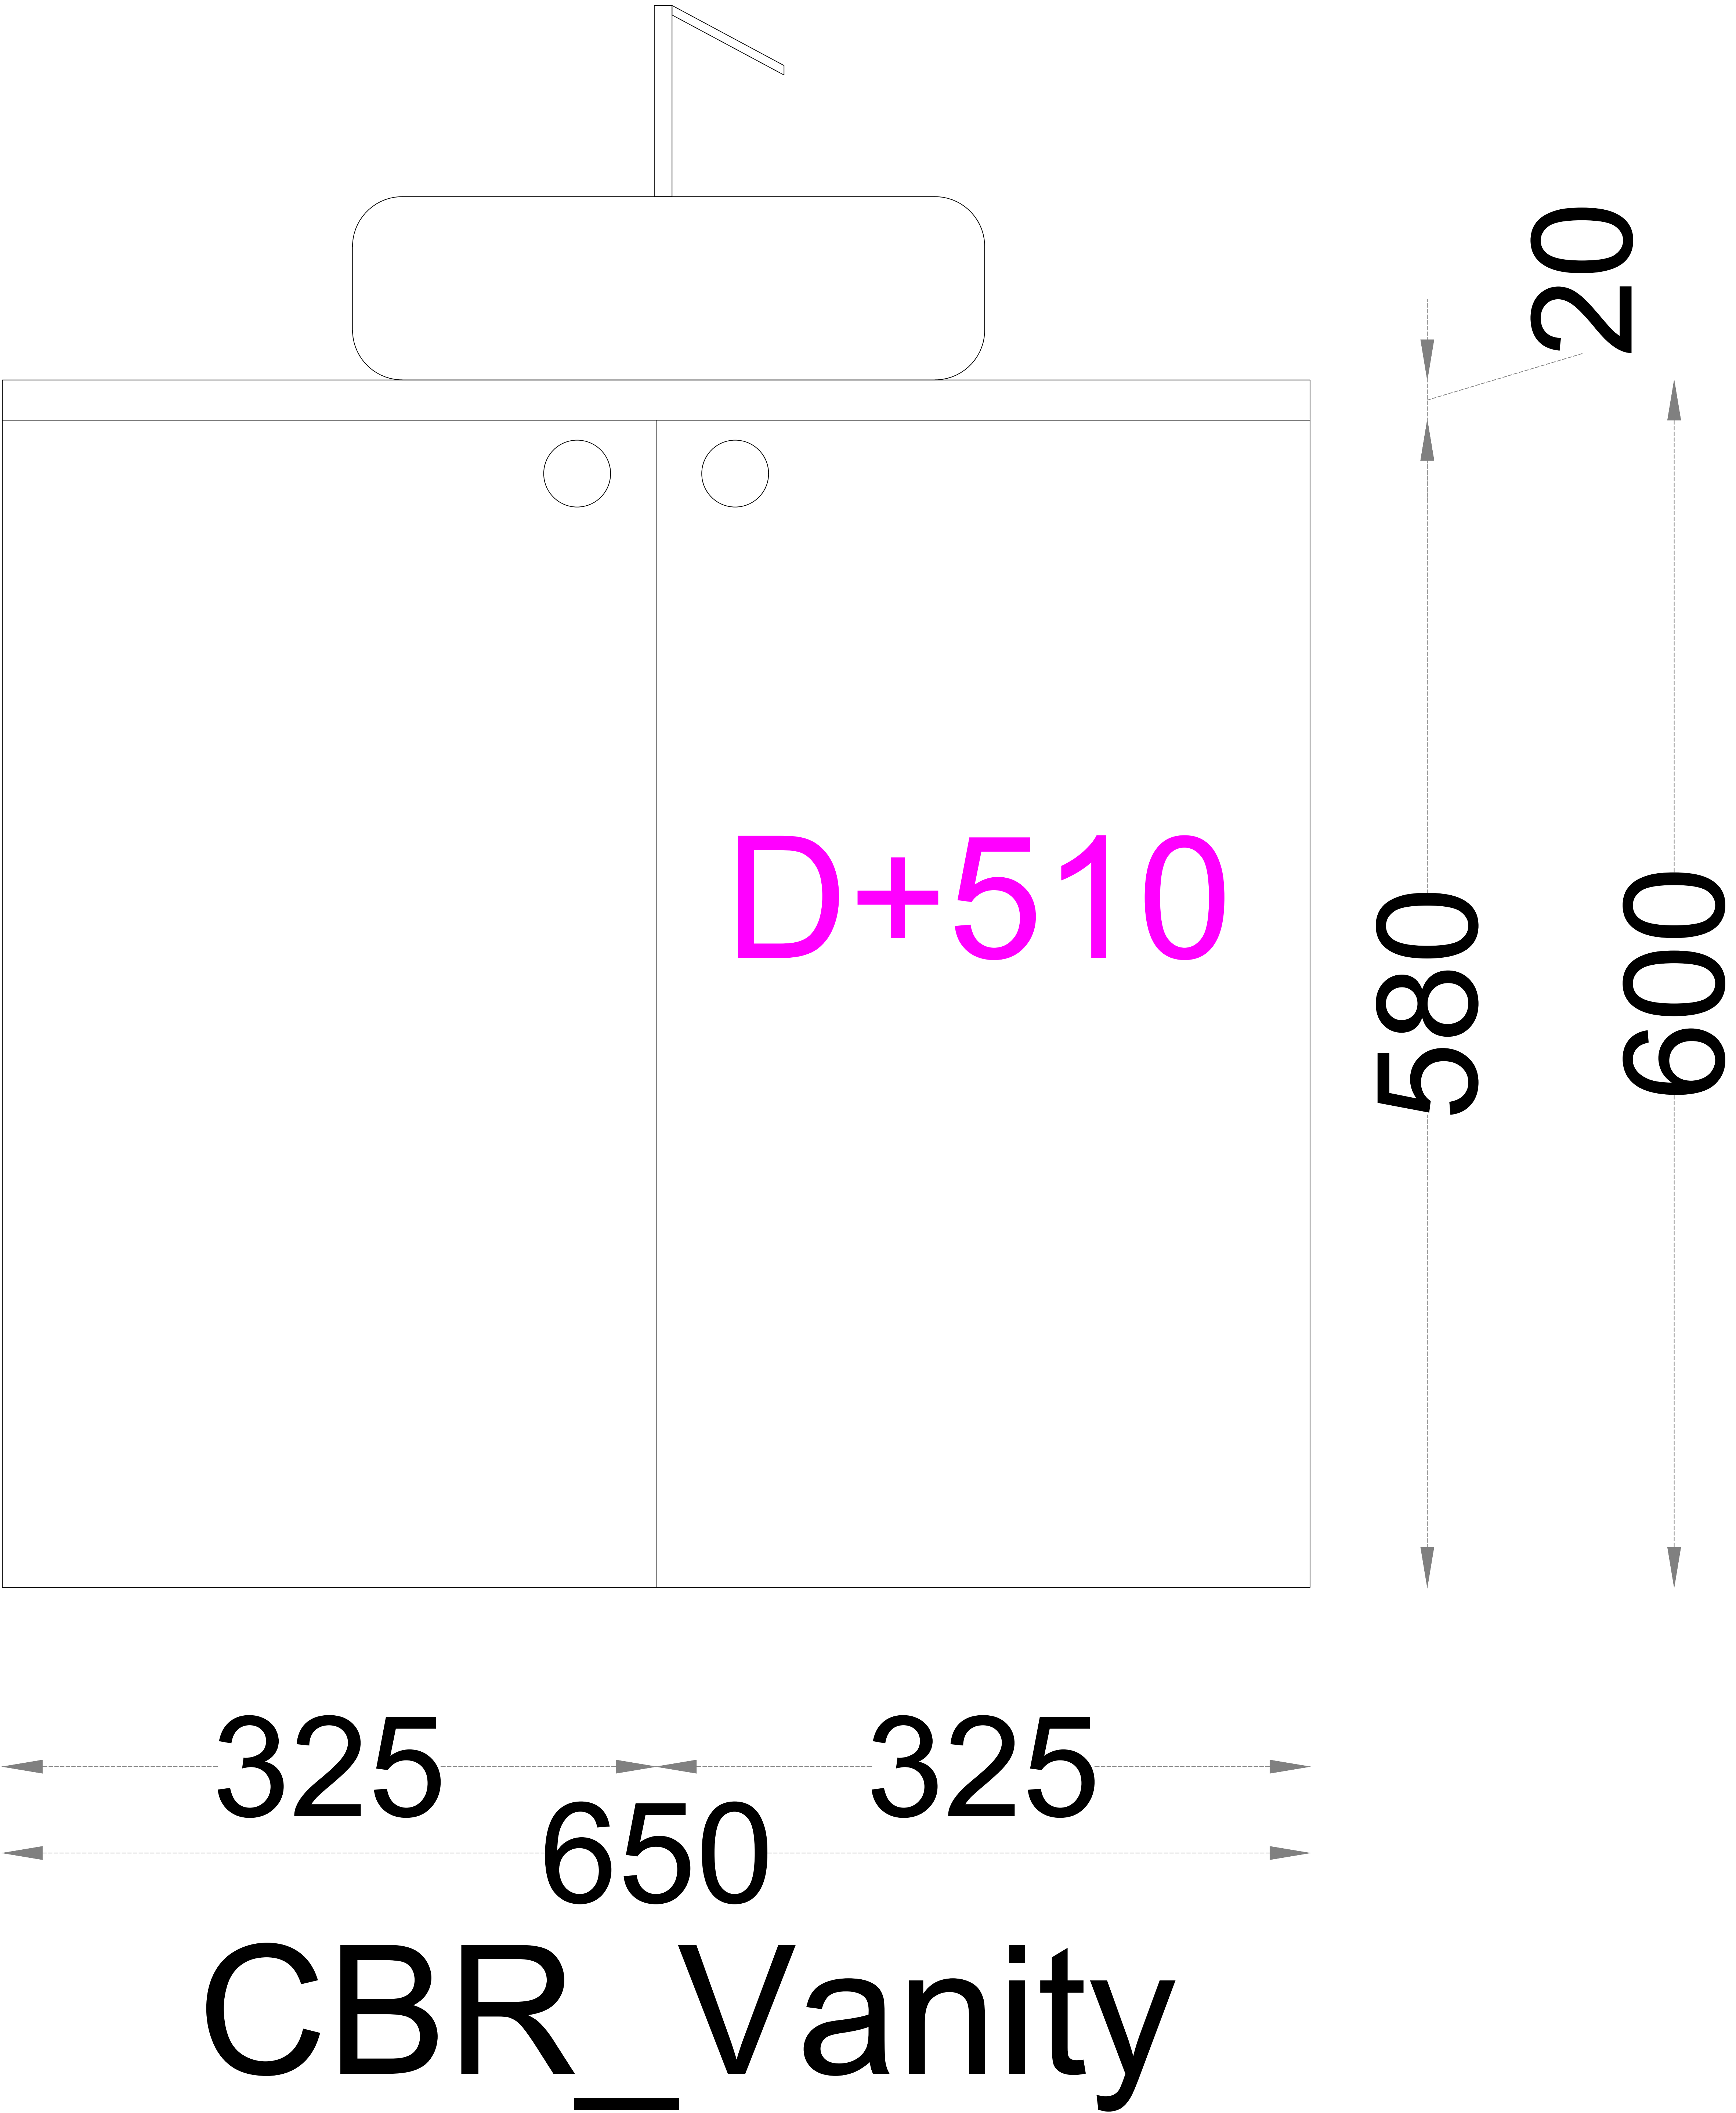

ALL DIMENSIONS ARE IN MILLIMETERS .
CONTRACTOR HAS TO CHECK & VERIFY ALL LEVELS, DATUM & DIMENSIONS ON SITE AND SHALL REPORT ANY DISCREPANCIES OR OMISSIONS ON SITE THIS OFFICE PRIOR TO THE START OF WORK & DURING THE CONSTRUCTION PHASE.
THIS DRAWING HAS TO BE READ & UNDERSTOOD IN CONJUNCTION WITH STRUCTURAL, MECHANICAL, ELECTRICAL AND/OR ANY OTHER CONSULTANT/S DOCUMENTATION, AS MAY BE APPLICABLE TO THE PROJECT PRIOR TO START OF WORK & IT'S DURATION.

TECHNICAL NOTE :
PROVIDED AS PER STRUCTURAL DRAWINGS & DETAILS.
ANY DISCREPENCY RELATED TO THIS DRAWING SHALL BE BROUGHT TO THE NOTICE OF THE CONCERNED PROJECT ARCHITECTS IMMEDIATELY BEFORE THE EXECUTION OF WORK.
LVLS MENTIONED IN THE DRAWING REFERS TO THE UNFINISHED LEVELS ON THE SITE.

COMPANY NAME
SPACICOUS VENTURE
Address:
Address: Candeur Landmark Liberty blockD903
Varthur, Bengaluru, Karnataka 560087

CLIENT NAME :
Mr.

PROJECT NAME :
INCOR_C1301

DRAWING TITLE :
CBR_Vanity-01

DRAWING NO :

SHEET NO :000
SCALE : N.T.S

TEAM Woodpeckers

DRAWN : Mohd Arfath
CHECKED : Syedfareed
DESIGNED : Syedfareed
DATE : 14-12-2025

ARCHITECTURAL DRAWING

NOTE :
THIS DRAWING IS THE EXCLUSIVE PROPERTY OF "SPACICOUS VENTURE". AND THE REPRODUCTION OF ANY PART WITHOUT PRIOR WRITTEN CONSENT FROM THIS OFFICE IS A VIOLATION OF APPLICABLE LAWS.

1539

1356

D=198

ALL DIMENSIONS ARE IN MILLIMETERS .
CONTRACTOR HAS TO CHECK & VERIFY ALL LEVELS, DATUM & DIMENSIONS ON SITE AND SHALL REPORT ANY DISCREPANCIES OR OMISSIONS ON SITE THIS OFFICE PRIOR TO THE START OF WORK & DURING THE CONSTRUCTION PHASE.

THIS DRAWING HAS TO BE READ & UNDERSTOOD IN CONJUNCTION WITH STRUCTURAL, MECHANICAL, ELECTRICAL AND/OR ANY OTHER CONSULTANT/S DOCUMENTATION, AS MAY BE APPLICABLE TO THE PROJECT PRIOR TO START OF WORK & IT'S DURATION.

TECHNICAL NOTE :

PROVIDED AS PER STRUCTURAL DRAWINGS & DETAILS.

ANY DISCREPENCY RELATED TO THIS DRAWING SHALL BE BROUGHT TO THE NOTICE OF THE CONCERNED PROJECT ARCHITECTS IMMEDIATELY BEFORE THE EXECUTION OF WORK.

LVLS MENTIONED IN THE DRAWING REFERS TO THE UNFINISHED LEVELS ON THE SITE.

COMPANY NAME
SPACICOUS VENTURE

Address:
Address: Candeur Landmark Liberty blockD903
Varthur, Bengaluru, Karnataka 560087

CLIENT NAME :

Mr.

PROJECT NAME :

INCOR_C1301

DRAWING TITLE :

CBR_Vanity-02


DRAWING NO :

SHEET NO :000
SCALE : N.T.S

TEAM	Woodpeckers	
DRAWN	: Mohd Arfath	
CHECKED	: Syedfareed	
DESIGNED	: Syedfareed	
DATE	: 14-12-2025	

ARCHITECTURAL DRAWING

NOTE :
THIS DRAWING IS THE EXCLUSIVE PROPERTY OF "SPACICOUS VENTURE". AND THE REPRODUCTION OF ANY PART WITHOUT PRIOR WRITTEN CONSENT FROM THIS OFFICE IS A VIOLATION OF APPLICABLE LAWS.

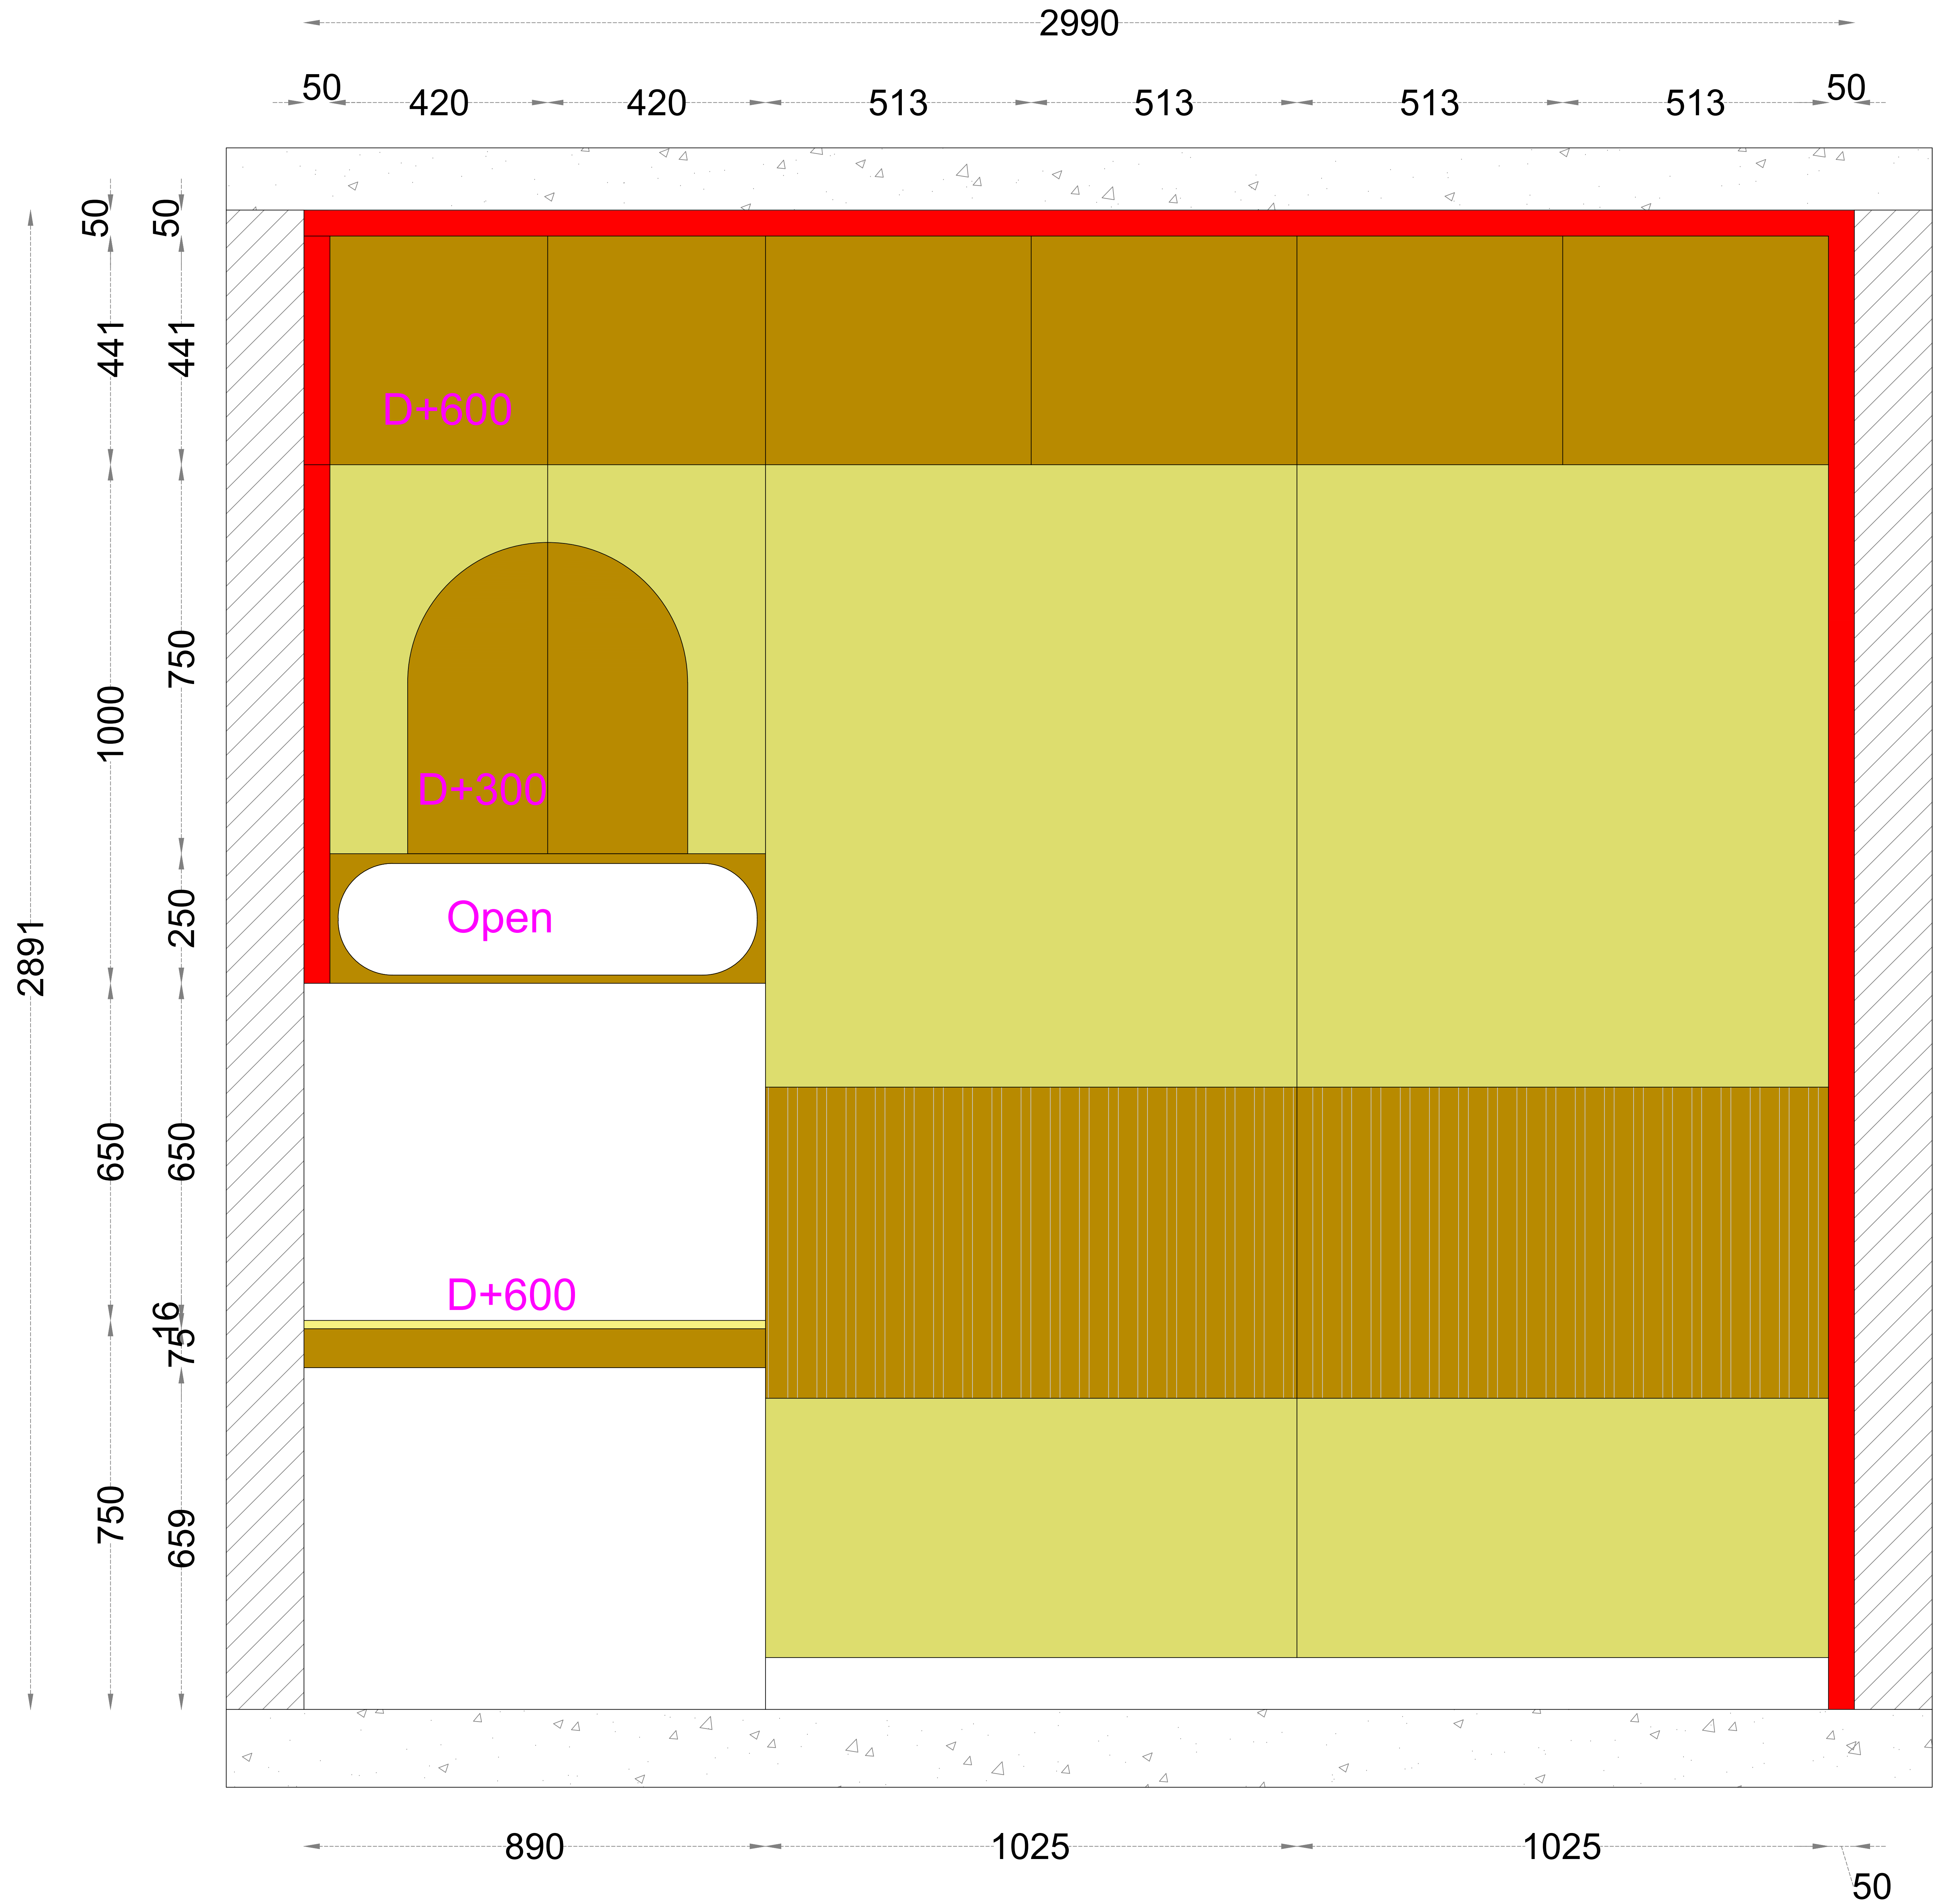

CBR_External

ALL DIMENSIONS ARE IN MILLIMETERS .
CONTRACTOR HAS TO CHECK & VERIFY ALL LEVELS, DATUM & DIMENSIONS ON SITE AND SHALL REPORT ANY DISCREPANCIES OR OMISSIONS ON SITE THIS OFFICE PRIOR TO THE START OF WORK & DURING THE CONSTRUCTION PHASE.

THIS DRAWING HAS TO BE READ & UNDERSTOOD IN CONJUNCTION WITH STRUCTURAL, MECHANICAL, ELECTRICAL AND/OR ANY OTHER CONSULTANT/S DOCUMENTATION, AS MAY BE APPLICABLE TO THE PROJECT PRIOR TO START OF WORK & IT'S DURATION.

TECHNICAL NOTE :

PROVIDED AS PER STRUCTURAL DRAWINGS & DETAILS.

ANY DISCREPENCY RELATED TO THIS DRAWING SHALL BE BROUGHT TO THE NOTICE OF THE CONCERNED PROJECT ARCHITECTS IMMEDIATELY BEFORE THE EXECUTION OF WORK.

LVLS MENTIONED IN THE DRAWING REFERS TO THE UNFINISHED LEVELS ON THE SITE.

COMPANY NAME
SPACICOUS VENTURE

Address:
Address: Candeur Landmark Liberty blockD903
Varthur, Bengaluru, Karnataka 560087

CLIENT NAME :

Mr.

PROJECT NAME :

INCOR_C1301

DRAWING TITLE :

CBR_WRD-_External

DRAWING NO :

SHEET NO :000

SCALE : N.T.S

TEAM Woodpeckers

DRAWN : Mohd Arfath


CHECKED : Syedfareed

DESIGNED : Syedfareed

DATE : 14-12-2025

ARCHITECTURAL DRAWING

NOTE :
THIS DRAWING IS THE EXCLUSIVE PROPERTY OF "SPACICOUS VENTURE". AND THE REPRODUCTION OF ANY PART WITHOUT PRIOR WRITTEN CONSENT FROM THIS OFFICE IS A VIOLATION OF APPLICABLE LAWS.

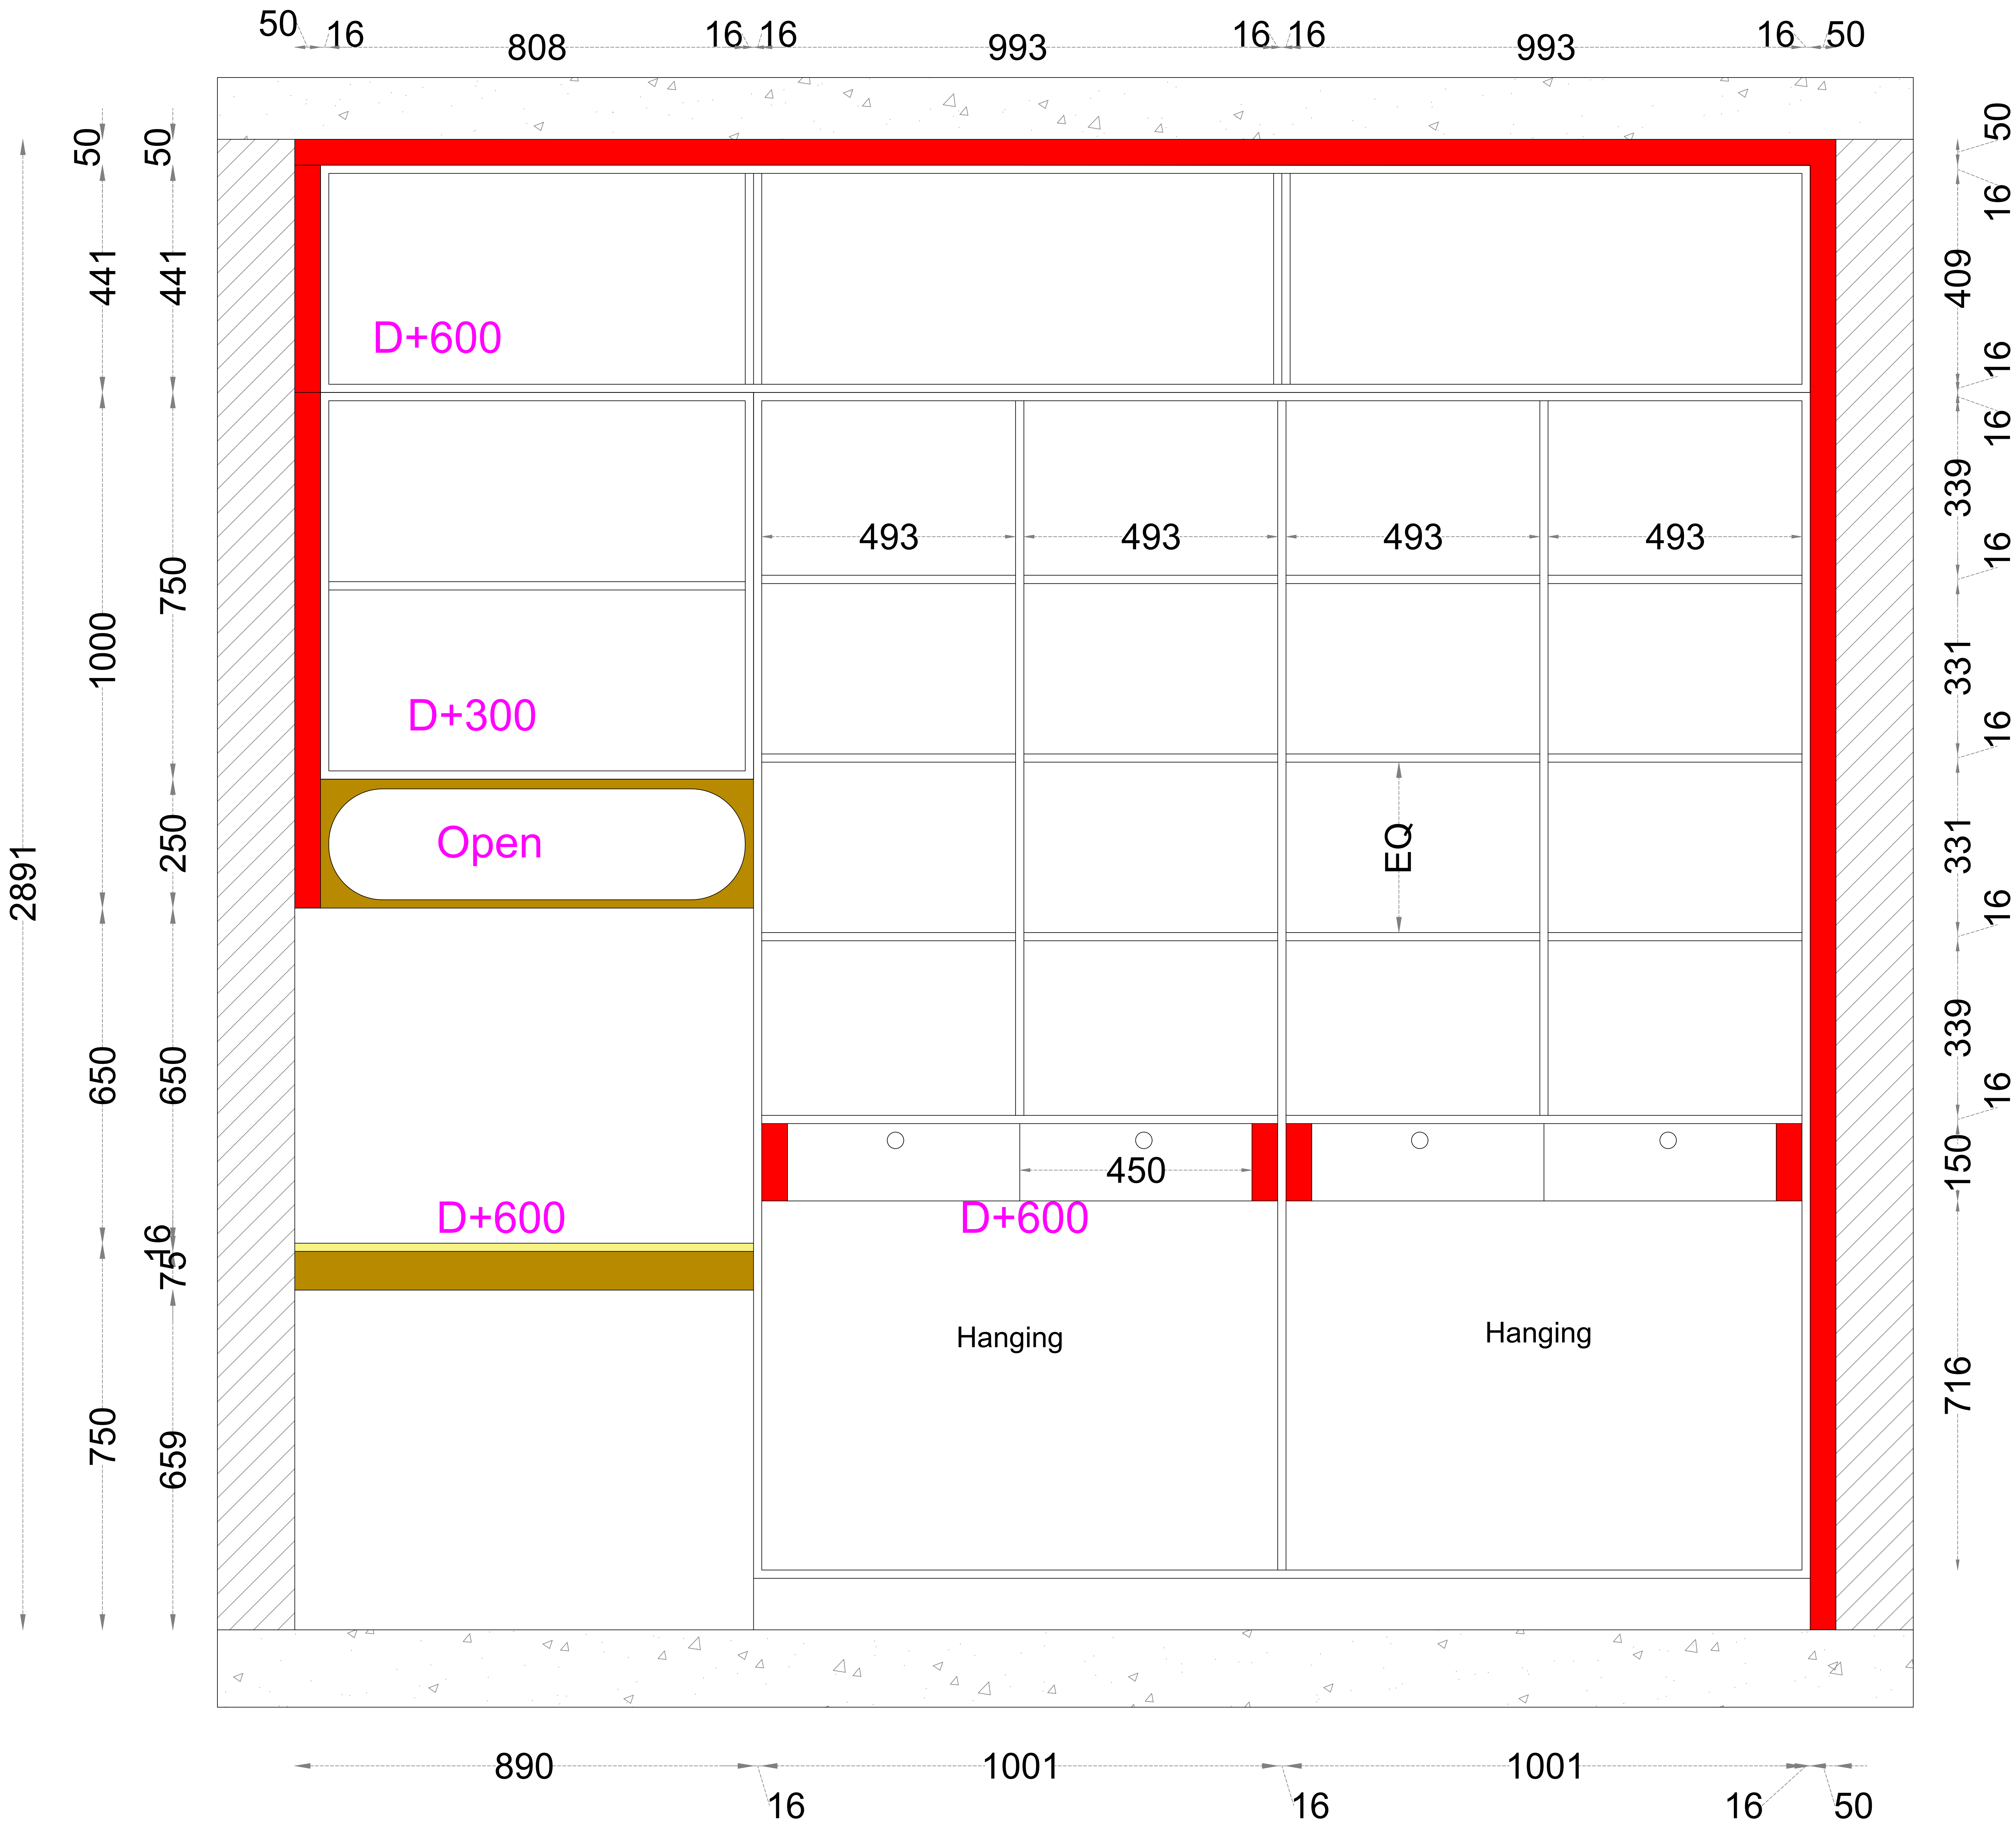

CBR_Internal

ALL DIMENSIONS ARE IN MILLIMETERS .
CONTRACTOR HAS TO CHECK & VERIFY ALL LEVELS, DATUM & DIMENSIONS ON SITE AND SHALL REPORT ANY DISCREPANCIES OR OMISSIONS ON SITE THIS OFFICE PRIOR TO THE START OF WORK & DURING THE CONSTRUCTION PHASE.

THIS DRAWING HAS TO BE READ & UNDERSTOOD IN CONJUNCTION WITH STRUCTURAL, MECHANICAL, ELECTRICAL AND/OR ANY OTHER CONSULTANT/S DOCUMENTATION, AS MAY BE APPLICABLE TO THE PROJECT PRIOR TO START OF WORK & IT'S DURATION.

TECHNICAL NOTE :

PROVIDED AS PER STRUCTURAL DRAWINGS & DETAILS.

ANY DISCREPENCY RELATED TO THIS DRAWING SHALL BE BROUGHT TO THE NOTICE OF THE CONCERNED PROJECT ARCHITECTS IMMEDIATELY BEFORE THE EXECUTION OF WORK.

LVLS MENTIONED IN THE DRAWING REFERS TO THE UNFINISHED LEVELS ON THE SITE.

COMPANY NAME
SPACICOUS VENTURE

Address:
Address: Candeur Landmark Liberty blockD903
Varthur, Bengaluru, Karnataka 560087

CLIENT NAME :

Mr.

PROJECT NAME :

INCOR_C1301

DRAWING TITLE :


CBR_WRD-_Internal

DRAWING NO :

SHEET NO	:000
SCALE	: N.T.S
TEAM	Woodpeckers
DRAWN	: Mohd Arfath
CHECKED	: Syedfareed
DESIGNED	: Syedfareed
DATE	: 14-12-2025

ARCHITECTURAL DRAWING

NOTE :
THIS DRAWING IS THE EXCLUSIVE PROPERTY OF "SPACICOUS VENTURE". AND THE REPRODUCTION OF ANY PART WITHOUT PRIOR WRITTEN CONSENT FROM THIS OFFICE IS A VIOLATION OF APPLICABLE LAWS.

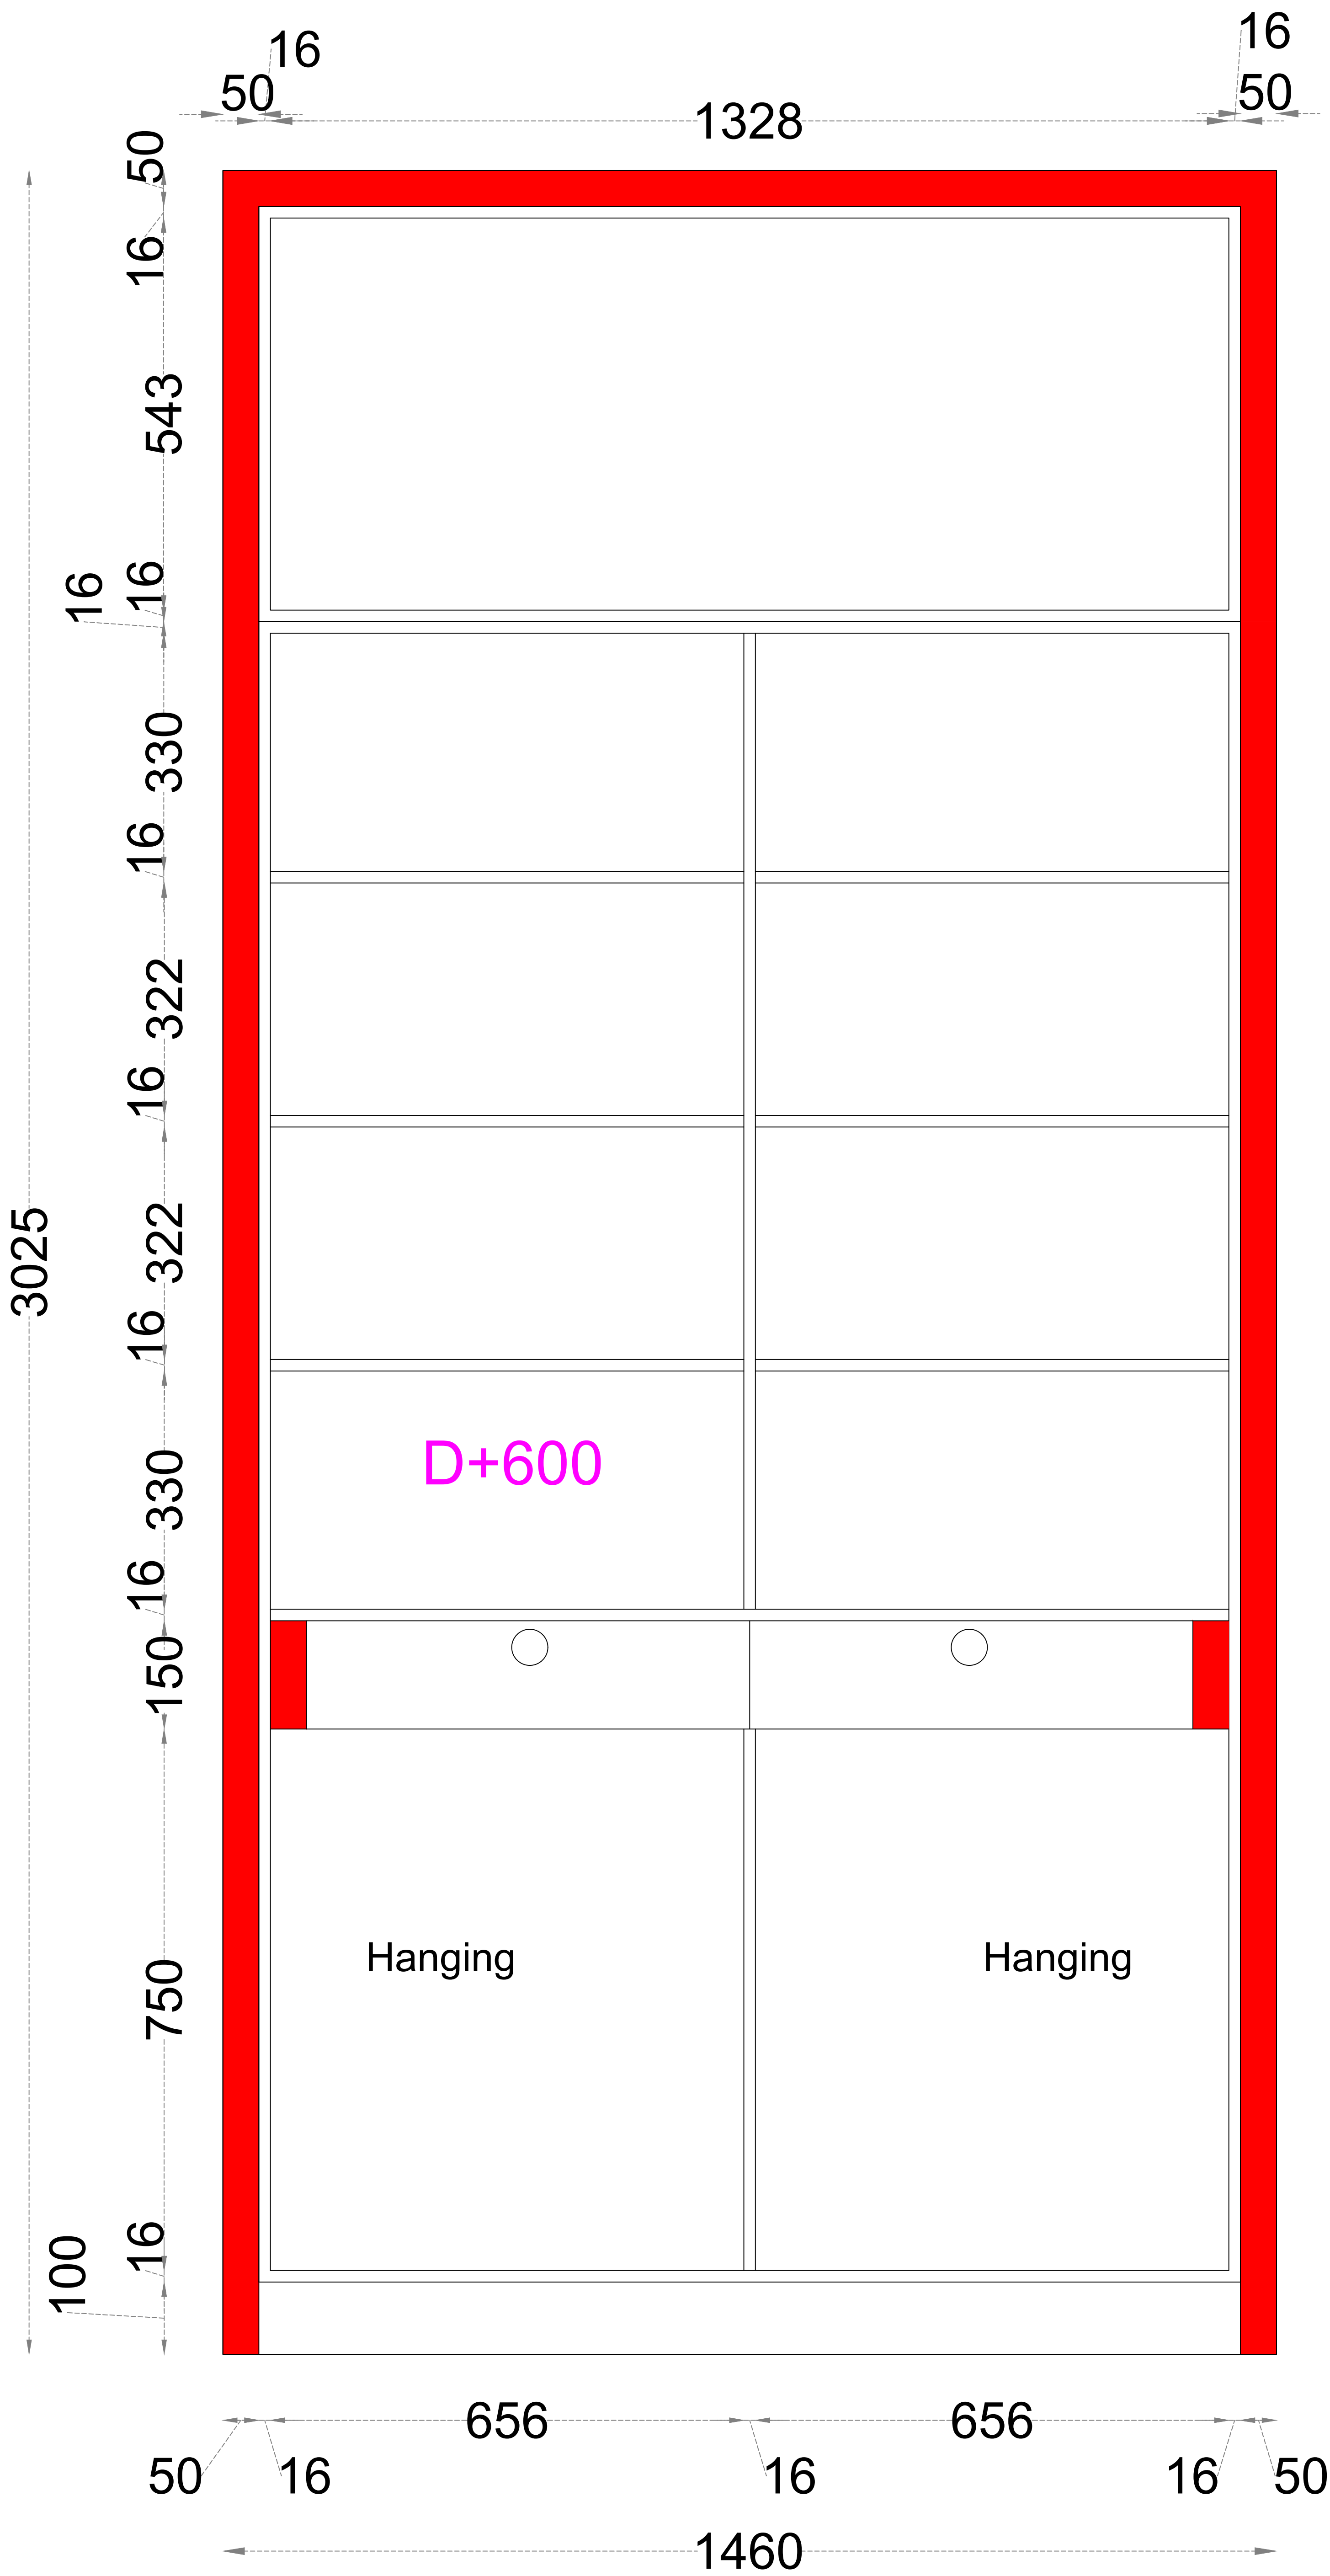

Dining Area WRD-01

ALL DIMENSIONS ARE IN MILLIMETERS .
CONTRACTOR HAS TO CHECK & VERIFY ALL LEVELS, DATUM & DIMENSIONS ON SITE AND SHALL REPORT ANY DISCREPANCIES OR OMISSIONS ON SITE THIS OFFICE PRIOR TO THE START OF WORK & DURING THE CONSTRUCTION PHASE.
THIS DRAWING HAS TO BE READ & UNDERSTOOD IN CONJUNCTION WITH STRUCTURAL, MECHANICAL, ELECTRICAL AND/OR ANY OTHER CONSULTANT/S DOCUMENTATION, AS MAY BE APPLICABLE TO THE PROJECT PRIOR TO START OF WORK & IT'S DURATION.

TECHNICAL NOTE :
PROVIDED AS PER STRUCTURAL DRAWINGS & DETAILS.
ANY DISCREPENCY RELATED TO THIS DRAWING SHALL BE BROUGHT TO THE NOTICE OF THE CONCERNED PROJECT ARCHITECTS IMMEDIATELY BEFORE THE EXECUTION OF WORK.
LVLS MENTIONED IN THE DRAWING REFERS TO THE UNFINISHED LEVELS ON THE SITE.

COMPANY NAME
SPACICOUS VENTURE
Address:
Address: Candeur Landmark Liberty blockD903
Varthur, Bengaluru, Karnataka 560087

CLIENT NAME :
Mr.

PROJECT NAME :
INCOR_C1301

DRAWING TITLE :
Dining Area WRD-01

DRAWING NO :

SHEET NO :000

SCALE : N.T.S

TEAM Woodpeckers

DRAWN : Mohd Arfath


CHECKED : Syedfareed

DESIGNED : Syedfareed

DATE : 14-12-2025

ARCHITECTURAL DRAWING

NOTE :
THIS DRAWING IS THE EXCLUSIVE PROPERTY OF "SPACICOUS VENTURE". AND THE REPRODUCTION OF ANY PART WITHOUT PRIOR WRITTEN CONSENT FROM THIS OFFICE IS A VIOLATION OF APPLICABLE LAWS.

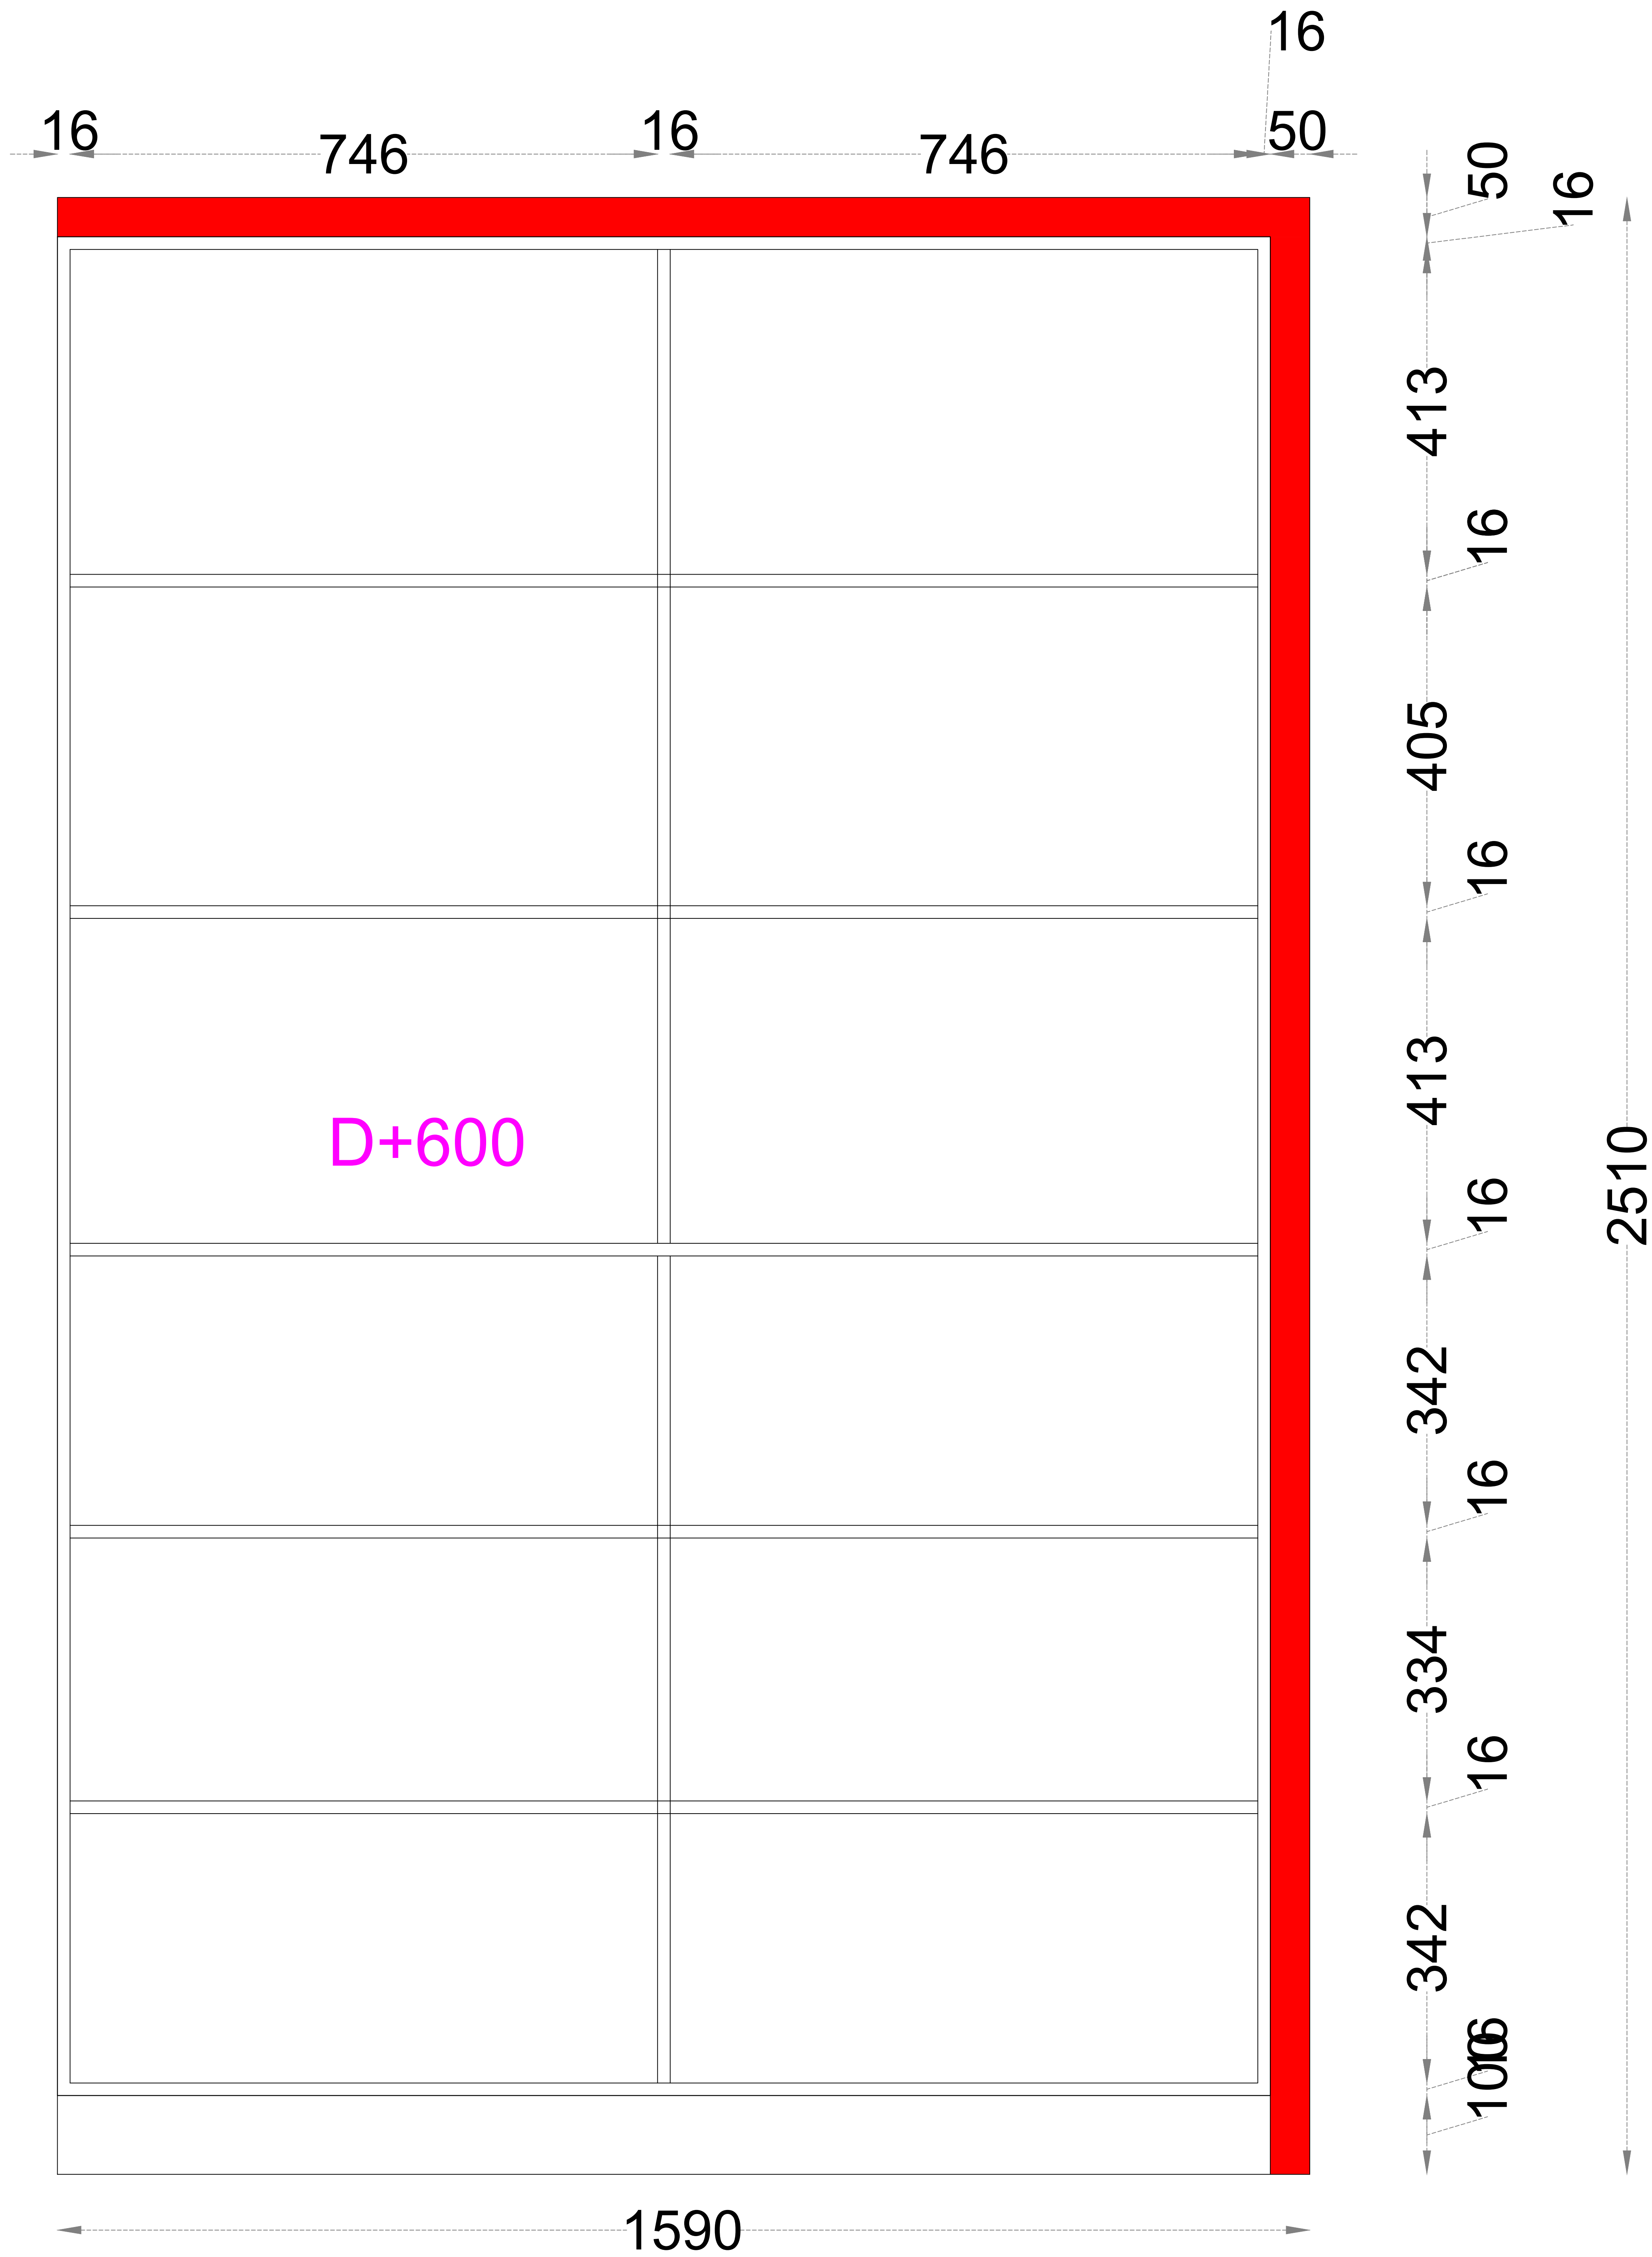

ALL DIMENSIONS ARE IN MILLIMETERS .
CONTRACTOR HAS TO CHECK & VERIFY ALL LEVELS, DATUM & DIMENSIONS ON SITE AND SHALL REPORT ANY DISCREPANCIES OR OMISSIONS ON SITE THIS OFFICE PRIOR TO THE START OF WORK & DURING THE CONSTRUCTION PHASE.
THIS DRAWING HAS TO BE READ & UNDERSTOOD IN CONJUNCTION WITH STRUCTURAL, MECHANICAL, ELECTRICAL AND/OR ANY OTHER CONSULTANT/S DOCUMENTATION, AS MAY BE APPLICABLE TO THE PROJECT PRIOR TO START OF WORK & IT'S DURATION.

TECHNICAL NOTE :
PROVIDED AS PER STRUCTURAL DRAWINGS & DETAILS.
ANY DISCREPENCY RELATED TO THIS DRAWING SHALL BE BROUGHT TO THE NOTICE OF THE CONCERNED PROJECT ARCHITECTS IMMEDIATELY BEFORE THE EXECUTION OF WORK.
LVLS MENTIONED IN THE DRAWING REFERS TO THE UNFINISHED LEVELS ON THE SITE.

COMPANY NAME
SPACICOUS VENTURE
Address:
Address: Candeur Landmark Liberty blockD903
Varthur, Bengaluru, Karnataka 560087

CLIENT NAME :
Mr.

PROJECT NAME :
INCOR_C1301

DRAWING TITLE :
Dining Area WRD-02


DRAWING NO :

SHEET NO :000
SCALE : N.T.S

TEAM	Woodpeckers	
DRAWN	: Mohd Arfath	
CHECKED	: Syedfareed	
DESIGNED	: Syedfareed	
DATE	: 14-12-2025	

ARCHITECTURAL DRAWING

NOTE :
THIS DRAWING IS THE EXCLUSIVE PROPERTY OF "SPACICOUS VENTURE". AND THE REPRODUCTION OF ANY PART WITHOUT PRIOR WRITTEN CONSENT FROM THIS OFFICE IS A VIOLATION OF APPLICABLE LAWS.

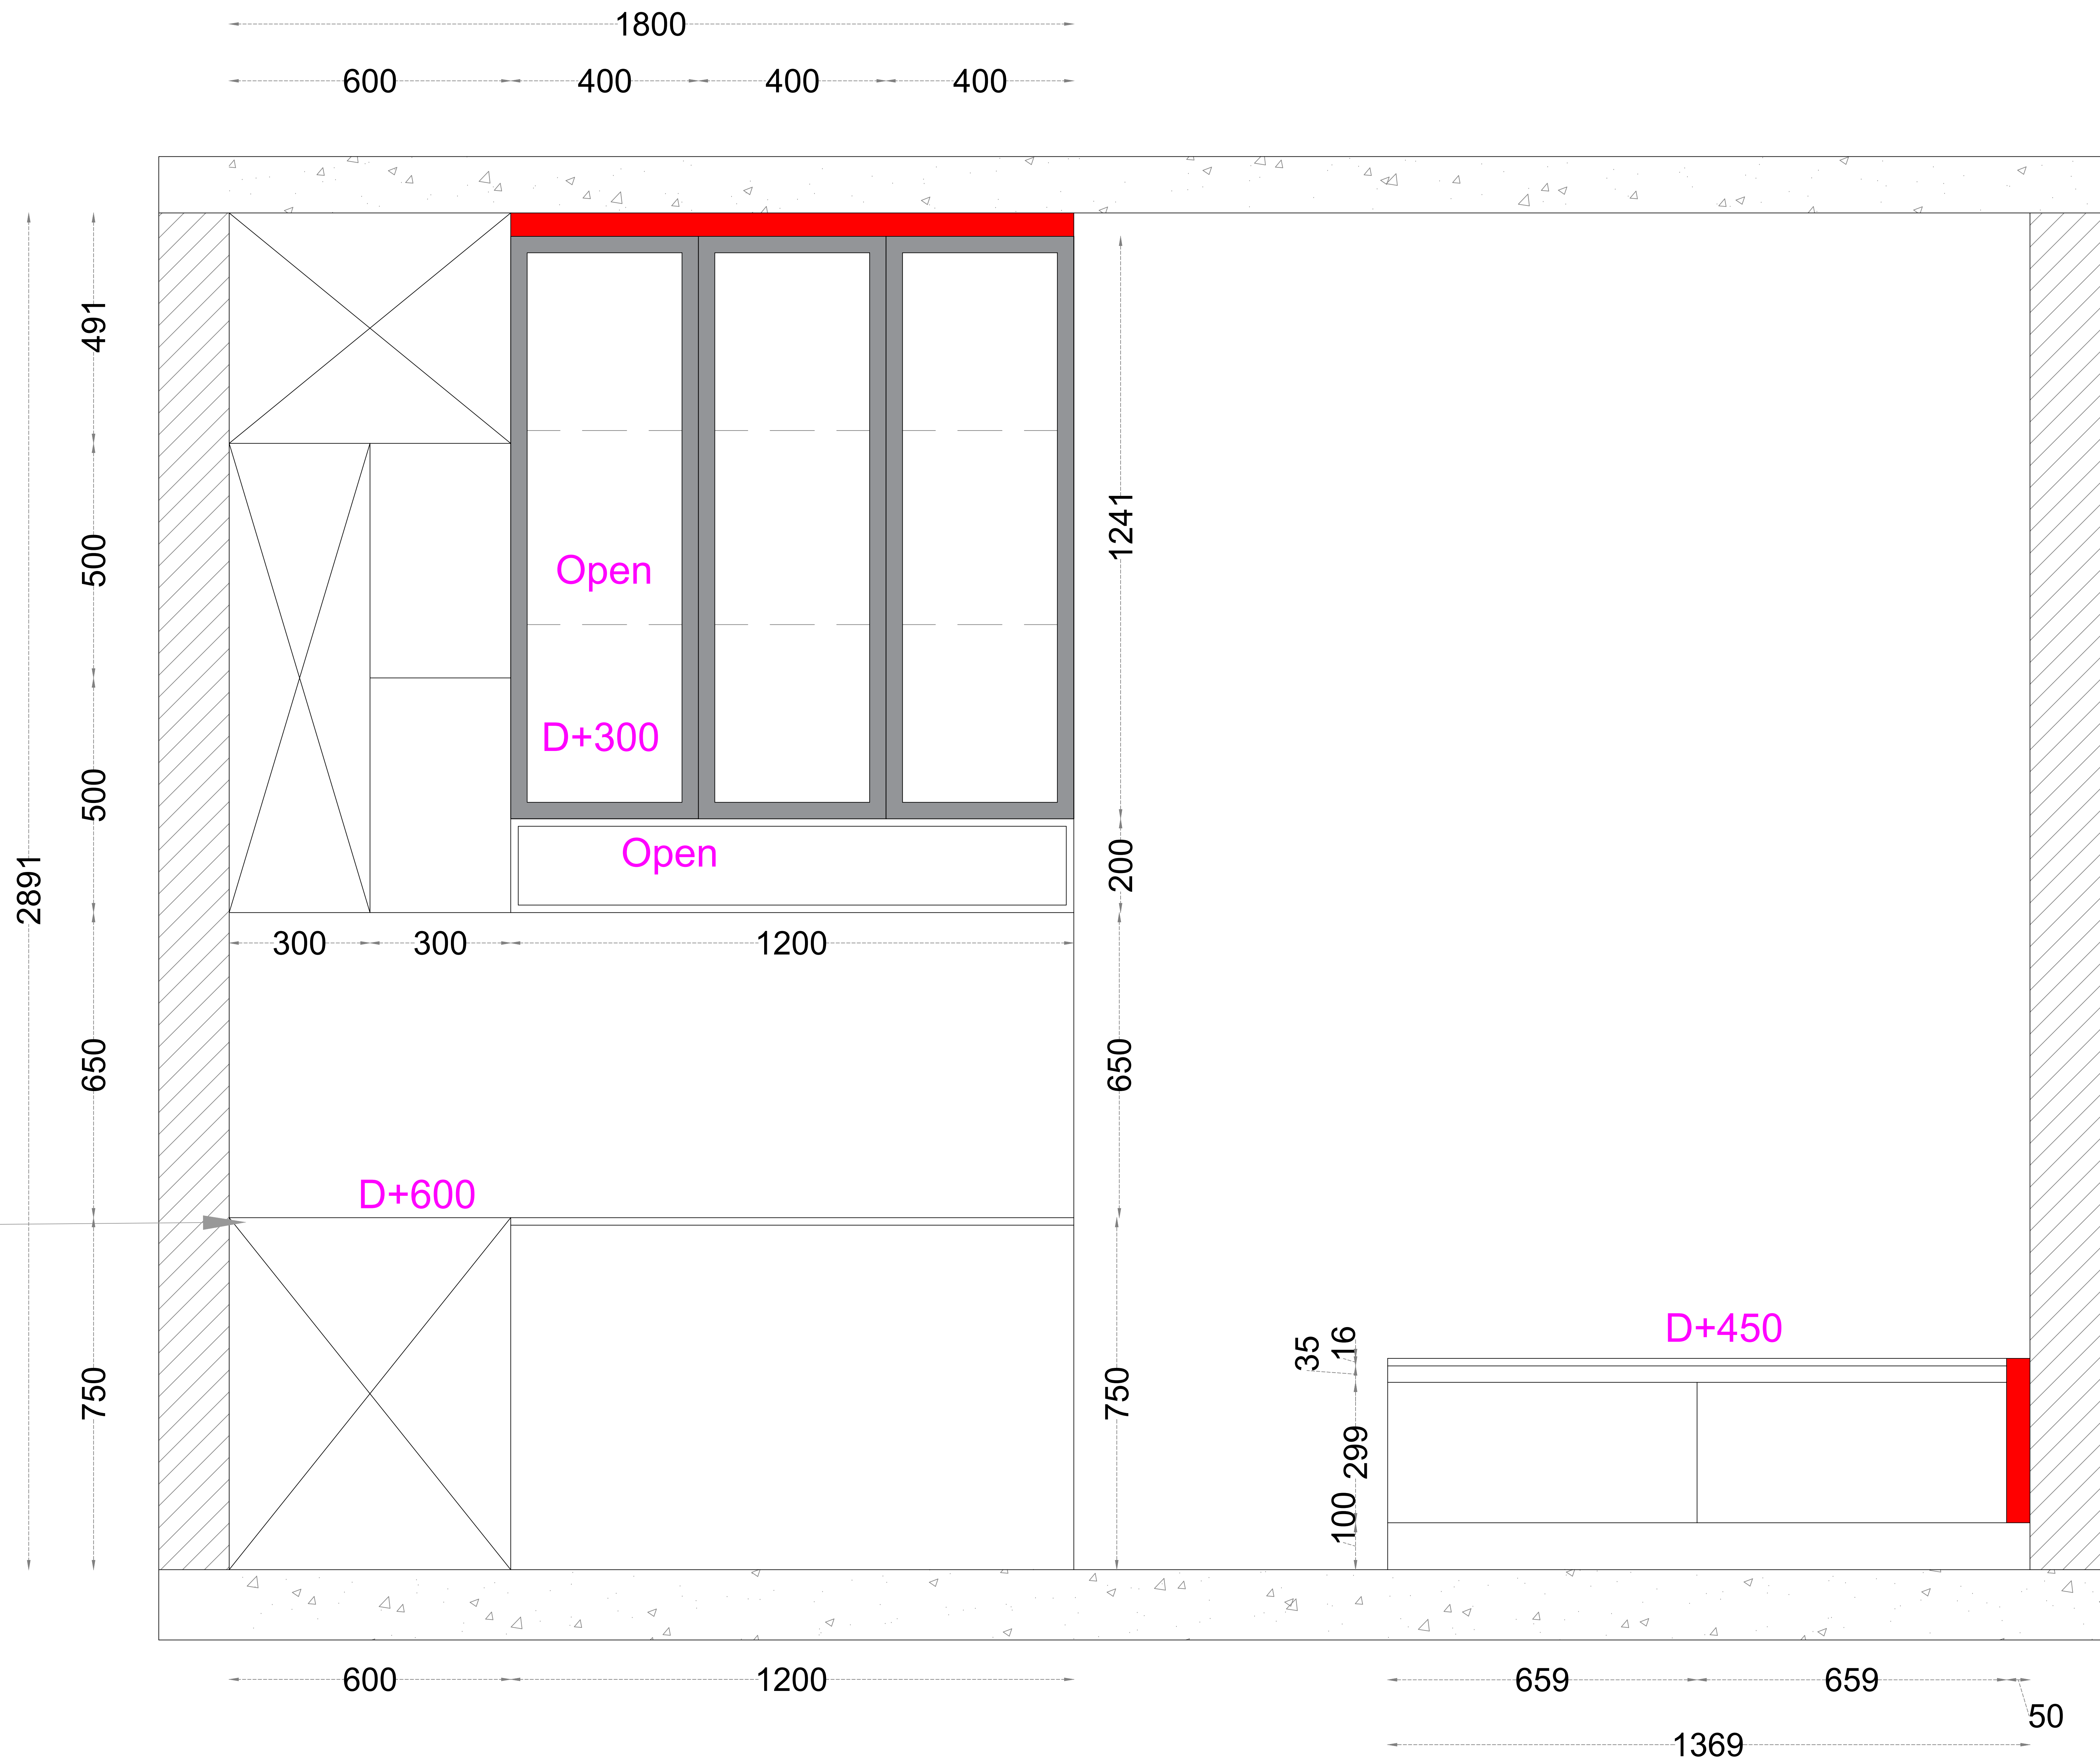

L_Shape Table

CBR_Internal

ALL DIMENSIONS ARE IN MILLIMETERS .
CONTRACTOR HAS TO CHECK & VERIFY ALL LEVELS, DATUM & DIMENSIONS ON SITE AND SHALL REPORT ANY DISCREPANCIES OR OMISSIONS ON SITE THIS OFFICE PRIOR TO THE START OF WORK & DURING THE CONSTRUCTION PHASE.
THIS DRAWING HAS TO BE READ & UNDERSTOOD IN CONJUNCTION WITH STRUCTURAL, MECHANICAL, ELECTRICAL AND/OR ANY OTHER CONSULTANT/S DOCUMENTATION, AS MAY BE APPLICABLE TO THE PROJECT PRIOR TO START OF WORK & IT'S DURATION.

TECHNICAL NOTE :
PROVIDED AS PER STRUCTURAL DRAWINGS & DETAILS.
ANY DISCREPENCY RELATED TO THIS DRAWING SHALL BE BROUGHT TO THE NOTICE OF THE CONCERNED PROJECT ARCHITECTS IMMEDIATELY BEFORE THE EXECUTION OF WORK.
LVLS MENTIONED IN THE DRAWING REFERS TO THE UNFINISHED LEVELS ON THE SITE.

COMPANY NAME
SPACICOUS VENTURE
Address:
Address: Candeur Landmark Liberty blockD903
Varthur, Bengaluru, Karnataka 560087

CLIENT NAME :
Mr.

PROJECT NAME :
INCOR_C1301


DRAWING TITLE :
GBR_Study

DRAWING NO :

SHEET NO	:000
SCALE	: N.T.S
TEAM	Woodpeckers
DRAWN	: Mohd Arfath
CHECKED	: Syedfareed
DESIGNED	: Syedfareed
DATE	: 14-12-2025

ARCHITECTURAL DRAWING

NOTE :
THIS DRAWING IS THE EXCLUSIVE PROPERTY OF "SPACICOUS VENTURE". AND THE REPRODUCTION OF ANY PART WITHOUT PRIOR WRITTEN CONSENT FROM THIS OFFICE IS A VIOLATION OF APPLICABLE LAWS.

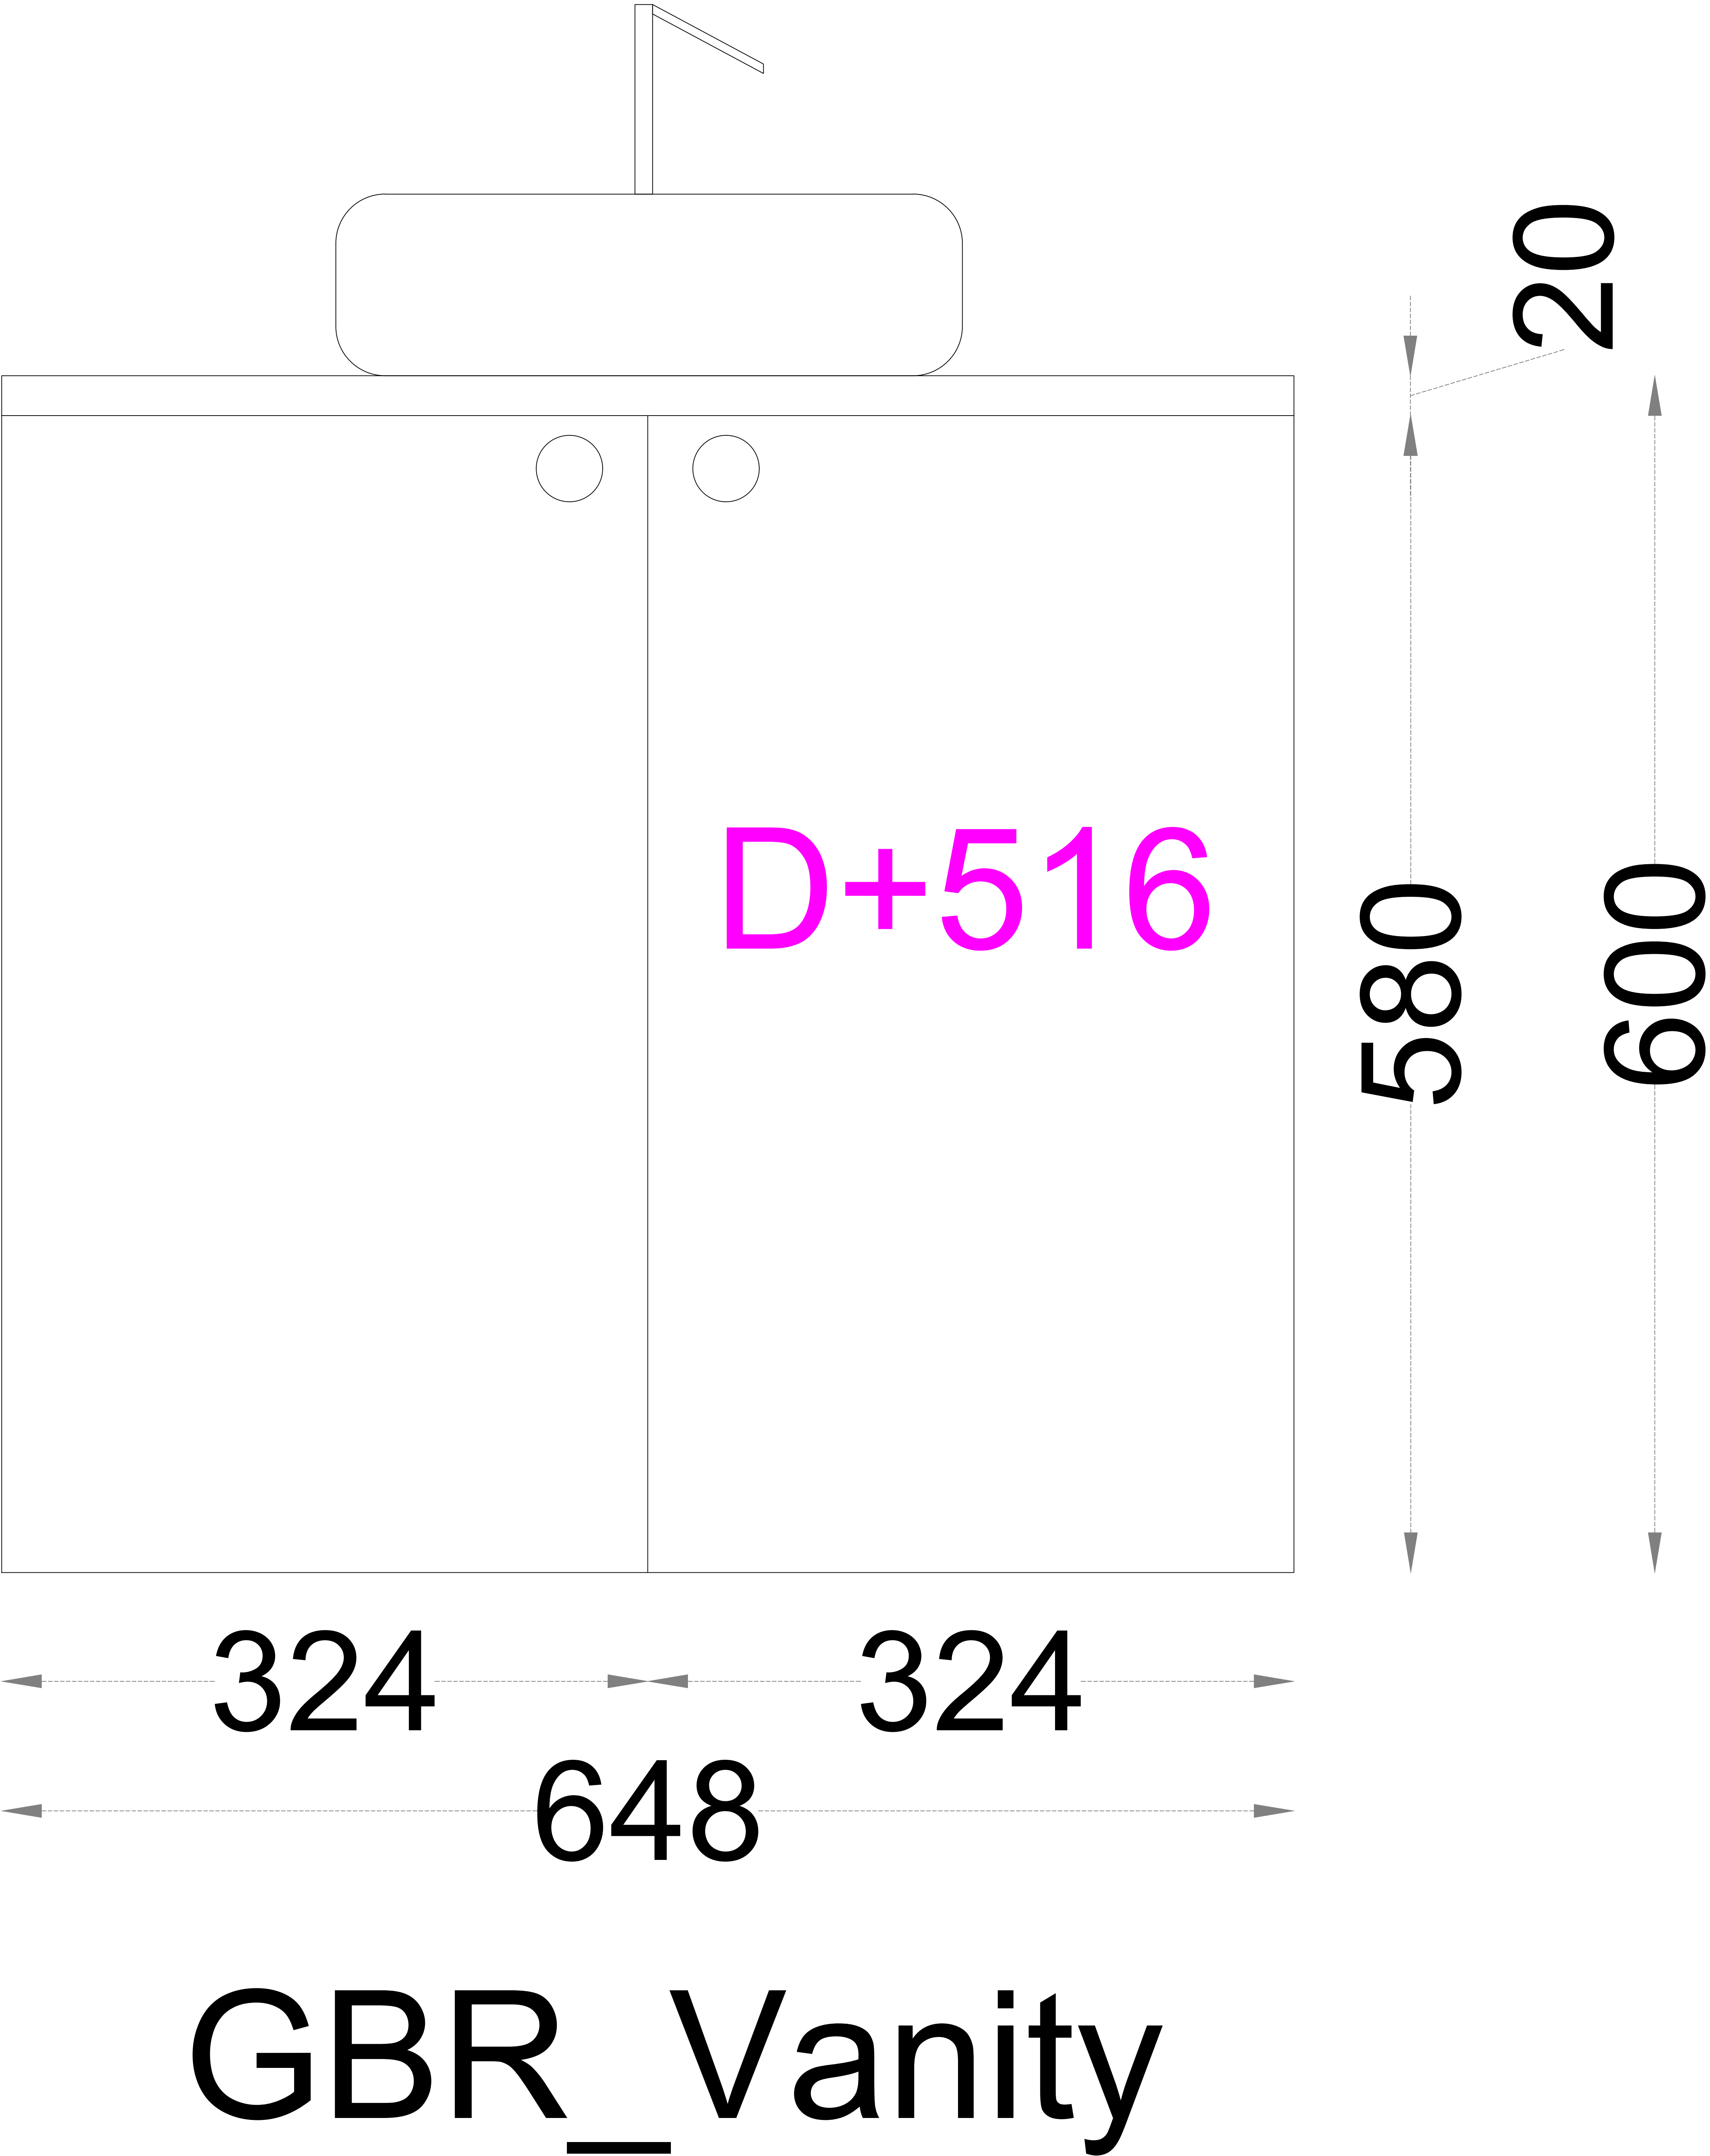

ALL DIMENSIONS ARE IN MILLIMETERS .
CONTRACTOR HAS TO CHECK & VERIFY ALL LEVELS, DATUM & DIMENSIONS ON SITE AND SHALL REPORT ANY DISCREPANCIES OR OMISSIONS ON SITE THIS OFFICE PRIOR TO THE START OF WORK & DURING THE CONSTRUCTION PHASE.

THIS DRAWING HAS TO BE READ & UNDERSTOOD IN CONJUNCTION WITH STRUCTURAL, MECHANICAL, ELECTRICAL AND/OR ANY OTHER CONSULTANT/S DOCUMENTATION, AS MAY BE APPLICABLE TO THE PROJECT PRIOR TO START OF WORK & IT'S DURATION.

TECHNICAL NOTE :

PROVIDED AS PER STRUCTURAL DRAWINGS & DETAILS.

ANY DISCREPENCY RELATED TO THIS DRAWING SHALL BE BROUGHT TO THE NOTICE OF THE CONCERNED PROJECT ARCHITECTS IMMEDIATELY BEFORE THE EXECUTION OF WORK.

LVLS MENTIONED IN THE DRAWING REFERS TO THE UNFINISHED LEVELS ON THE SITE.

COMPANY NAME
SPACICOUS VENTURE

Address:
Address: Candeur Landmark Liberty blockD903
Varthur, Bengaluru, Karnataka 560087

CLIENT NAME :

Mr.

PROJECT NAME :

INCOR_C1301

DRAWING TITLE :

GBR_Vanity-01

DRAWING NO :

SHEET NO :000
SCALE : N.T.S

TEAM	Woodpeckers	
DRAWN	: Mohd Arfath	
CHECKED	: Syedfareed	
DESIGNED	: Syedfareed	
DATE	: 14-12-2025	

ARCHITECTURAL DRAWING

NOTE :
THIS DRAWING IS THE EXCLUSIVE PROPERTY OF "SPACICOUS VENTURE". AND THE REPRODUCTION OF ANY PART WITHOUT PRIOR WRITTEN CONSENT FROM THIS OFFICE IS A VIOLATION OF APPLICABLE LAWS.

ALL DIMENSIONS ARE IN MILLIMETERS .
CONTRACTOR HAS TO CHECK & VERIFY ALL LEVELS,
DATUM & DIMENSIONS ON SITE AND SHALL REPORT ANY
DISCREPANCIES OR OMISSIONS ON SITE THIS OFFICE PRIOR TO THE
START OF WORK & DURING THE CONSTRUCTION PHASE.

THIS DRAWING HAS TO BE READ & UNDERSTOOD IN CONJUNCTION
WITH STRUCTURAL, MECHANICAL, ELECTRICAL AND/OR ANY OTHER
CONSULTANT/S DOCUMENTATION, AS MAY BE APPLICABLE TO THE
PROJECT PRIOR TO START OF WORK & IT'S DURATION.

TECHNICAL NOTE :

PROVIDED AS PER STRUCTURAL DRAWINGS & DETAILS.

ANY DISCREPANCY RELATED TO THIS DRAWING SHALL BE
BROUGHT TO THE NOTICE OF THE CONCERNED PROJECT
ARCHITECTS IMMEDIATELY BEFORE THE EXECUTION OF WORK.

LVLS MENTIONED IN THE DRAWING REFERS TO THE UNFINISHED LEVELS ON THE SITE.

COMPANY NAME

SPACIOUS VENTURE

Address:
Address: Candeur Landmark Liberty blockD903
Varthur, Bengaluru, Karnataka 560087

CLIENT NAME :

Mr.

PROJECT NAME :

INCOR_C1301

DRAWING TITLE :

GBR_Vanity-02

DRAWING NO :

SHEET NO :000

SCALE	: N.T.S
-------	---------

TEAM Woodpeckers

DRAWN : Mohd Arfath

CHECKED : Syedfareed

DESIGNED : Syedfareed

DATE	: 14-12-2025
------	--------------

ARCHITECTURAL DRAWING


NOTE :
THIS DRAWING IS THE EXCLUSIVE PROPERTY OF
"SPACICIOUS VENTURE". AND THE
REPRODUCTION OF ANY PART WITHOUT PRIOR WRITTEN CONSENT
FROM THIS OFFICE IS A VIOLATION OF APPLICABLE LAWS.

1512

D=220

1493

GBR

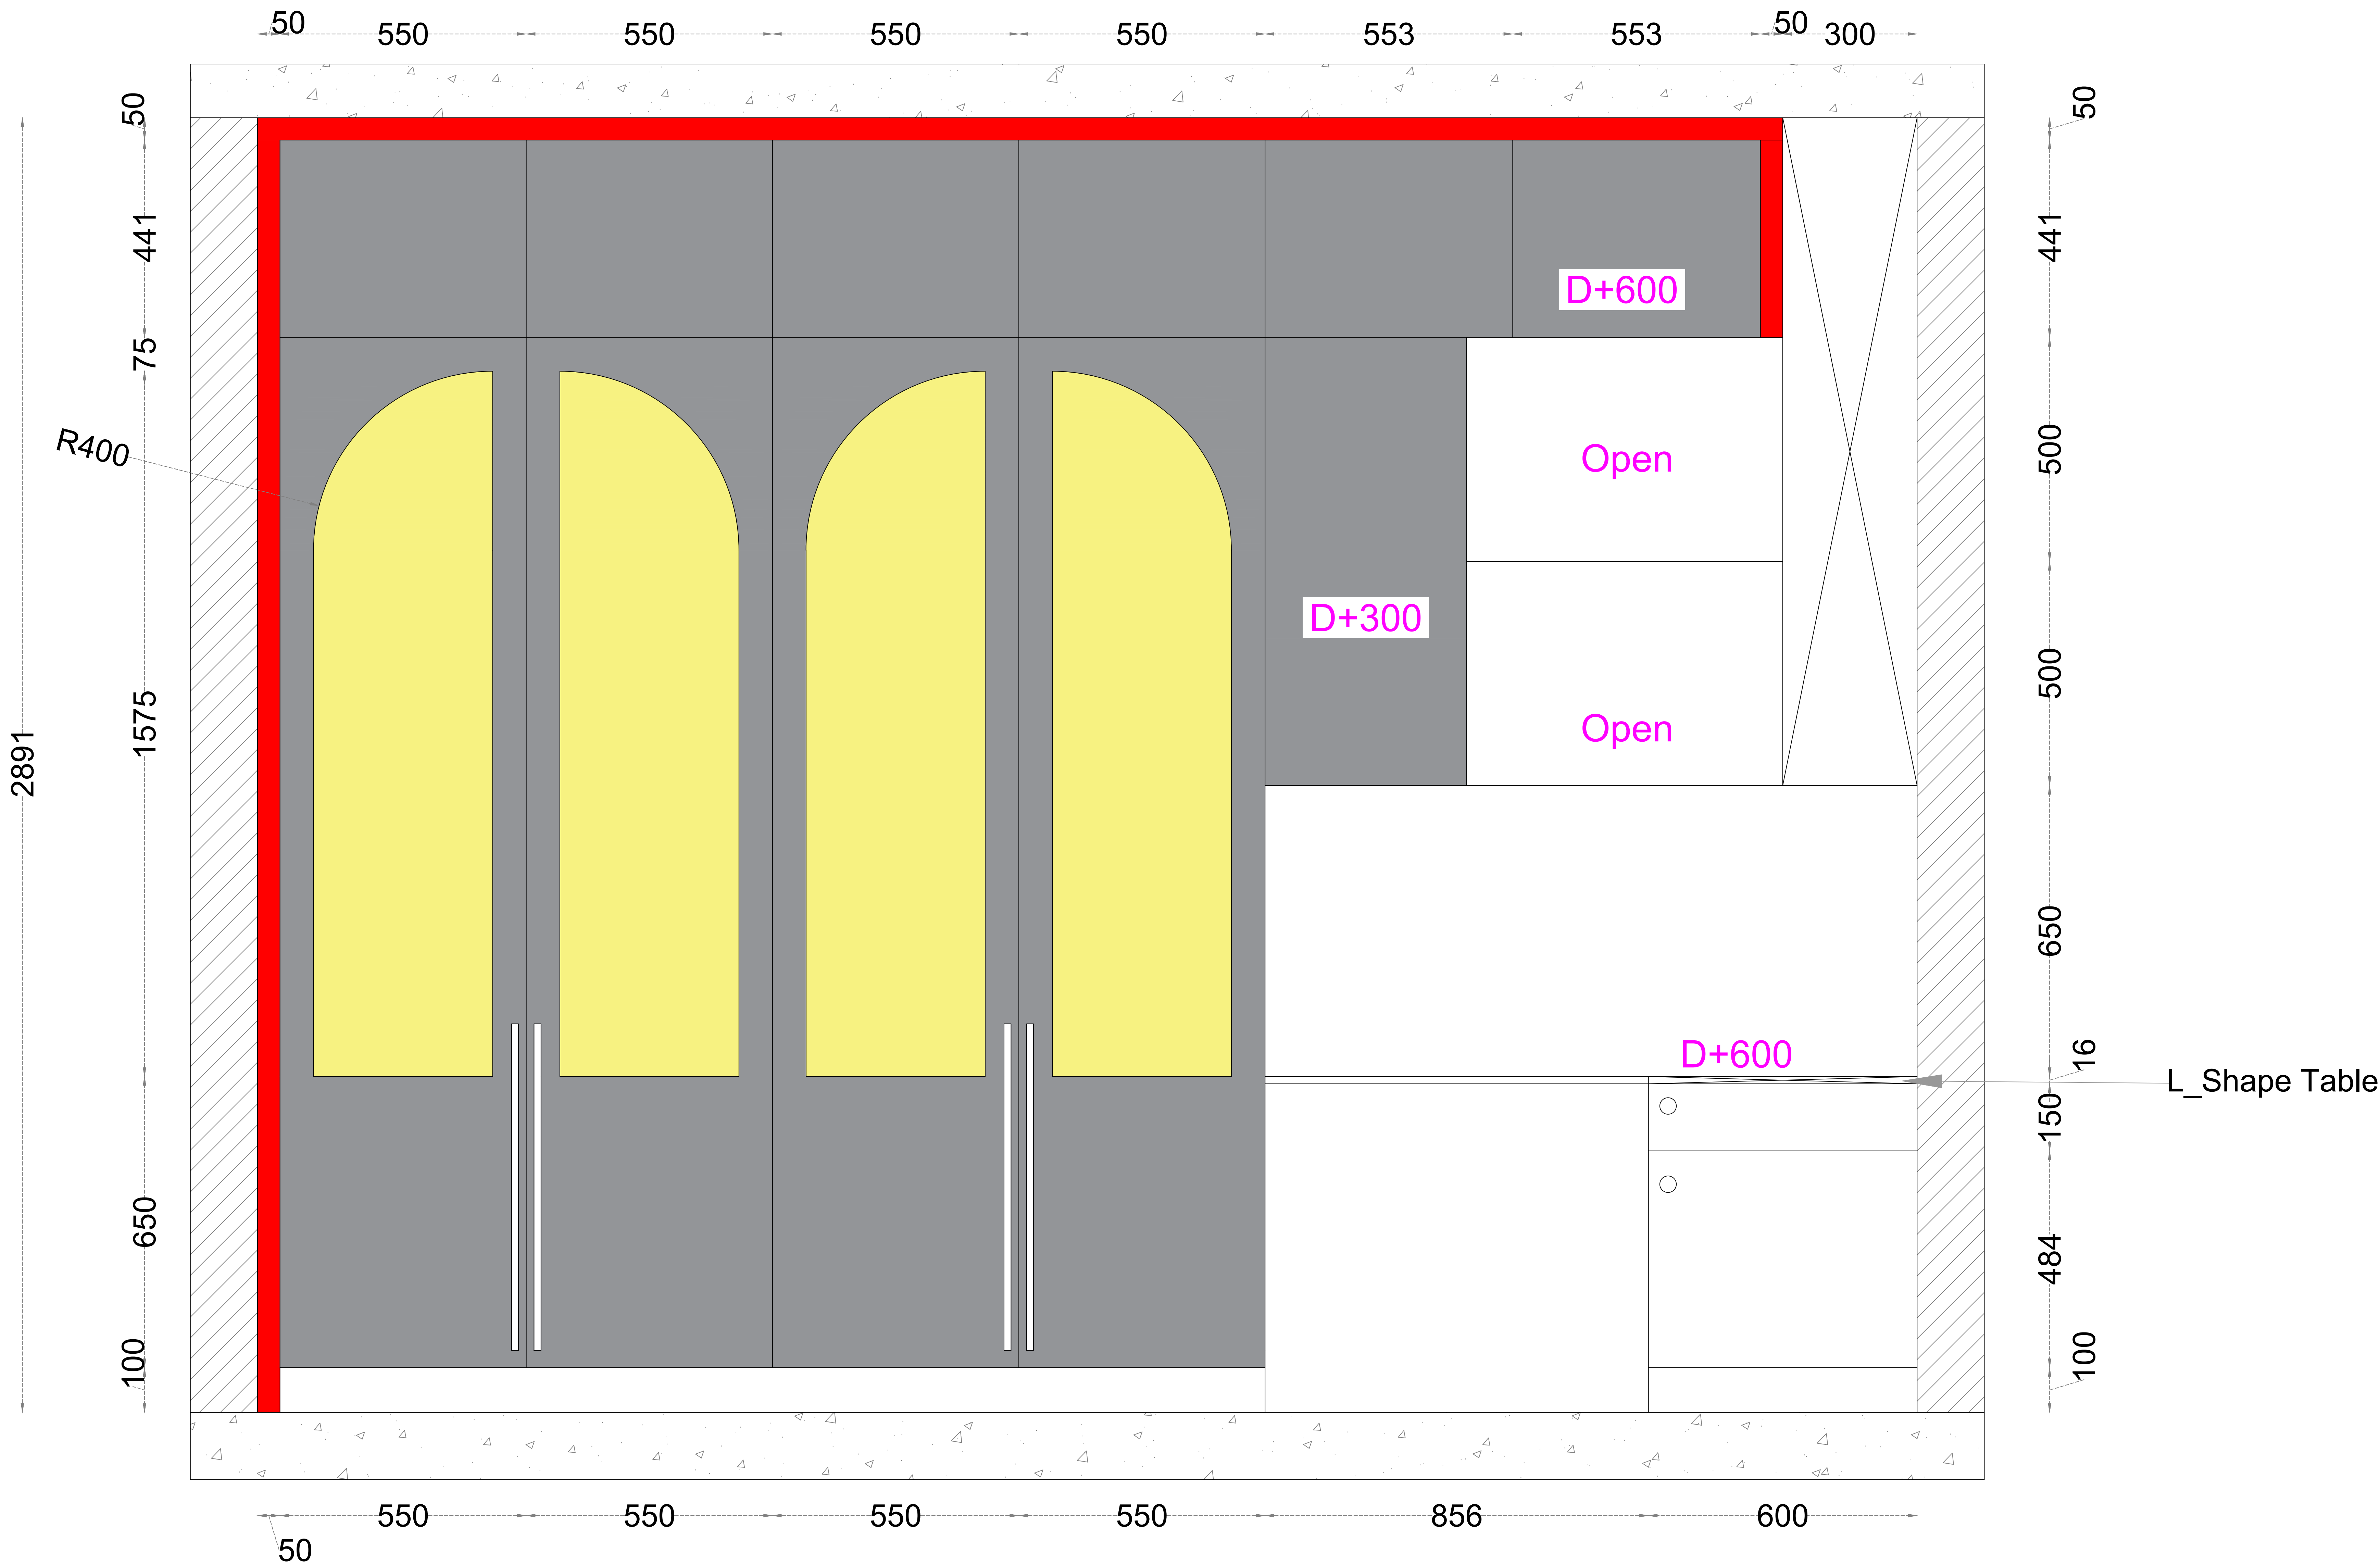

CBR_External

ALL DIMENSIONS ARE IN MILLIMETERS .
CONTRACTOR HAS TO CHECK & VERIFY ALL LEVELS, DATUM & DIMENSIONS ON SITE AND SHALL REPORT ANY DISCREPANCIES OR OMISSIONS ON SITE THIS OFFICE PRIOR TO THE START OF WORK & DURING THE CONSTRUCTION PHASE.
THIS DRAWING HAS TO BE READ & UNDERSTOOD IN CONJUNCTION WITH STRUCTURAL, MECHANICAL, ELECTRICAL AND/OR ANY OTHER CONSULTANT/S DOCUMENTATION, AS MAY BE APPLICABLE TO THE PROJECT PRIOR TO START OF WORK & IT'S DURATION.

TECHNICAL NOTE :
PROVIDED AS PER STRUCTURAL DRAWINGS & DETAILS.
ANY DISCREPENCY RELATED TO THIS DRAWING SHALL BE BROUGHT TO THE NOTICE OF THE CONCERNED PROJECT ARCHITECTS IMMEDIATELY BEFORE THE EXECUTION OF WORK.
LVLS MENTIONED IN THE DRAWING REFERS TO THE UNFINISHED LEVELS ON THE SITE.

COMPANY NAME
SPACICIOUS VENTURE
Address:
Address: Candeur Landmark Liberty blockD903
Varthur, Bengaluru, Karnataka 560087

CLIENT NAME :
Mr.

PROJECT NAME :
INCOR_C1301

DRAWING TITLE :
GBR_WRD- _External

DRAWING NO :

SHEET NO :000

SCALE : N.T.S

TEAM **Woodpeckers**

DRAWN : Mohd Arfath


CHECKED : Syedfareed

DESIGNED : Syedfareed

DATE : 14-12-2025

ARCHITECTURAL DRAWING

NOTE :
THIS DRAWING IS THE EXCLUSIVE PROPERTY OF "SPACICIOUS VENTURE". AND THE REPRODUCTION OF ANY PART WITHOUT PRIOR WRITTEN CONSENT FROM THIS OFFICE IS A VIOLATION OF APPLICABLE LAWS.

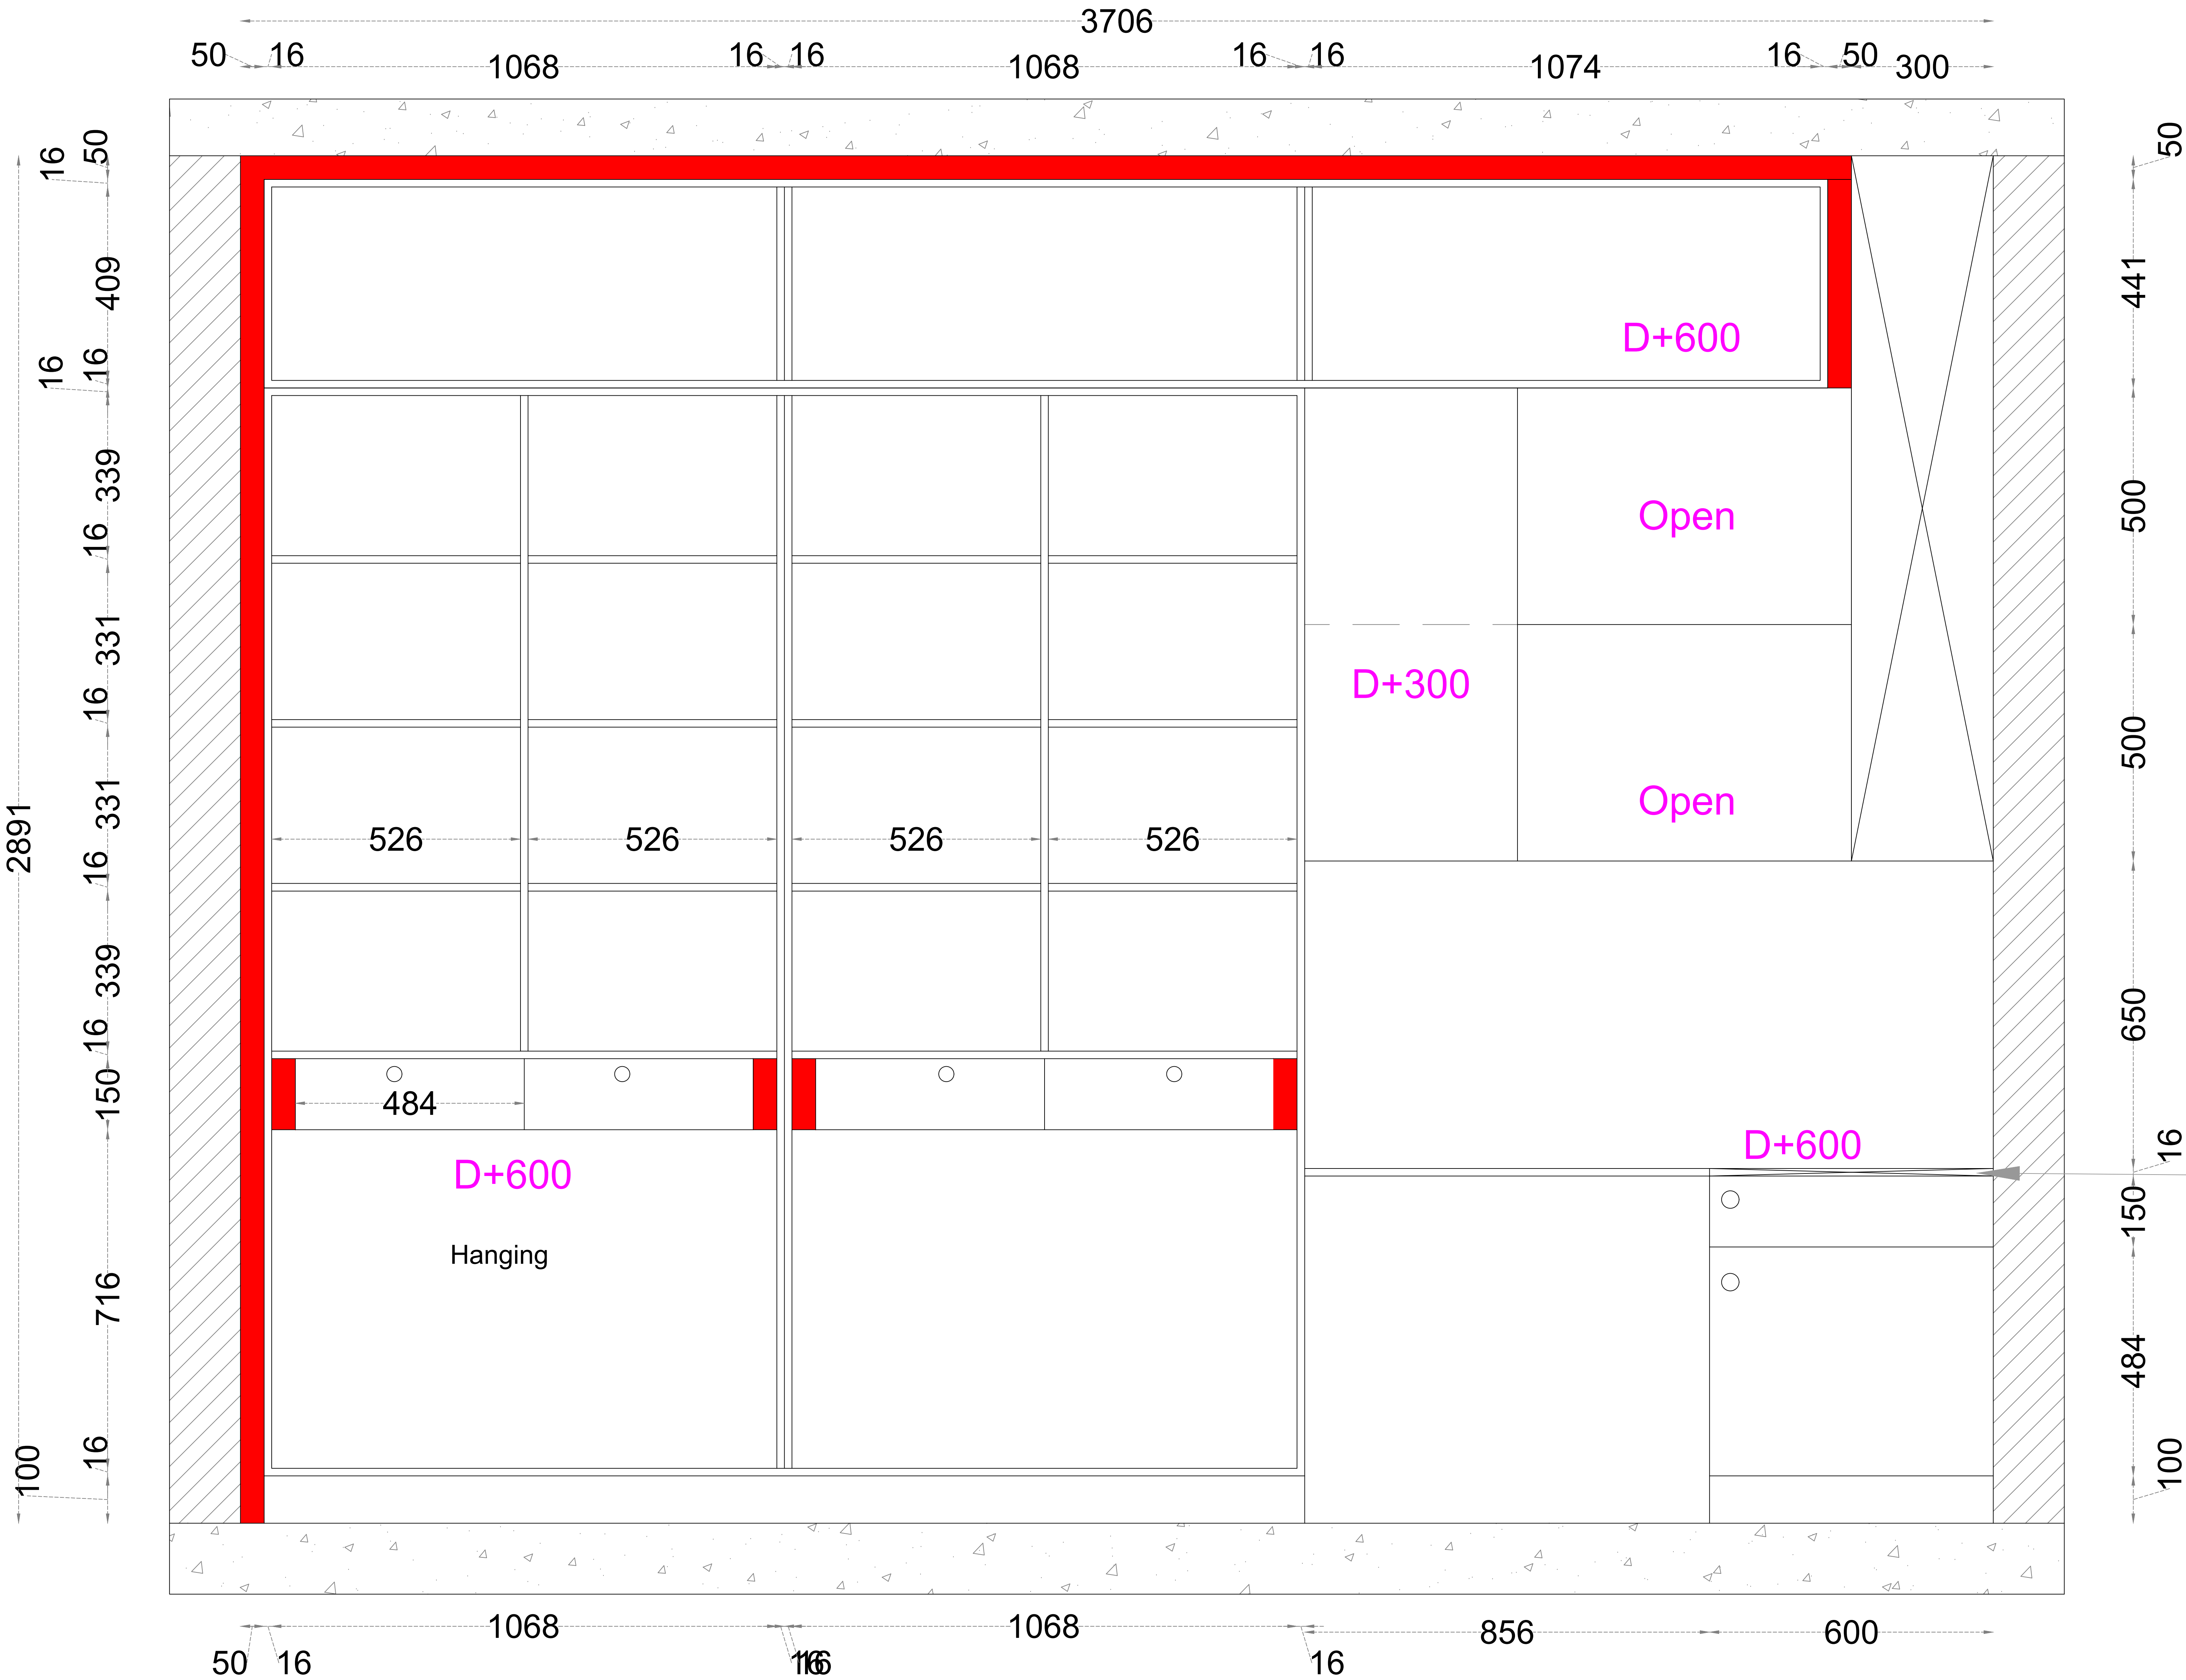

CBR_Internal

ALL DIMENSIONS ARE IN MILLIMETERS .
CONTRACTOR HAS TO CHECK & VERIFY ALL LEVELS, DATUM & DIMENSIONS ON SITE AND SHALL REPORT ANY DISCREPANCIES OR OMISSIONS ON SITE THIS OFFICE PRIOR TO THE START OF WORK & DURING THE CONSTRUCTION PHASE.
THIS DRAWING HAS TO BE READ & UNDERSTOOD IN CONJUNCTION WITH STRUCTURAL, MECHANICAL, ELECTRICAL AND/OR ANY OTHER CONSULTANT/S DOCUMENTATION, AS MAY BE APPLICABLE TO THE PROJECT PRIOR TO START OF WORK & IT'S DURATION.

TECHNICAL NOTE :
PROVIDED AS PER STRUCTURAL DRAWINGS & DETAILS.
ANY DISCREPENCY RELATED TO THIS DRAWING SHALL BE BROUGHT TO THE NOTICE OF THE CONCERNED PROJECT ARCHITECTS IMMEDIATELY BEFORE THE EXECUTION OF WORK.
LVLS MENTIONED IN THE DRAWING REFERS TO THE UNFINISHED LEVELS ON THE SITE.

COMPANY NAME
SPACICOUS VENTURE
Address:
Address: Candeur Landmark Liberty blockD903
Varthur, Bengaluru, Karnataka 560087

CLIENT NAME :
Mr.

PROJECT NAME :
INCOR_C1301


DRAWING TITLE :
GBR_WRD- _Internal

DRAWING NO :

SHEET NO	:000
SCALE	: N.T.S
TEAM	Woodpeckers
DRAWN	: Mohd Arfath
CHECKED	: Syedfareed
DESIGNED	: Syedfareed
DATE	: 14-12-2025

ARCHITECTURAL DRAWING

NOTE :
THIS DRAWING IS THE EXCLUSIVE PROPERTY OF "SPACICOUS VENTURE". AND THE REPRODUCTION OF ANY PART WITHOUT PRIOR WRITTEN CONSENT FROM THIS OFFICE IS A VIOLATION OF APPLICABLE LAWS.

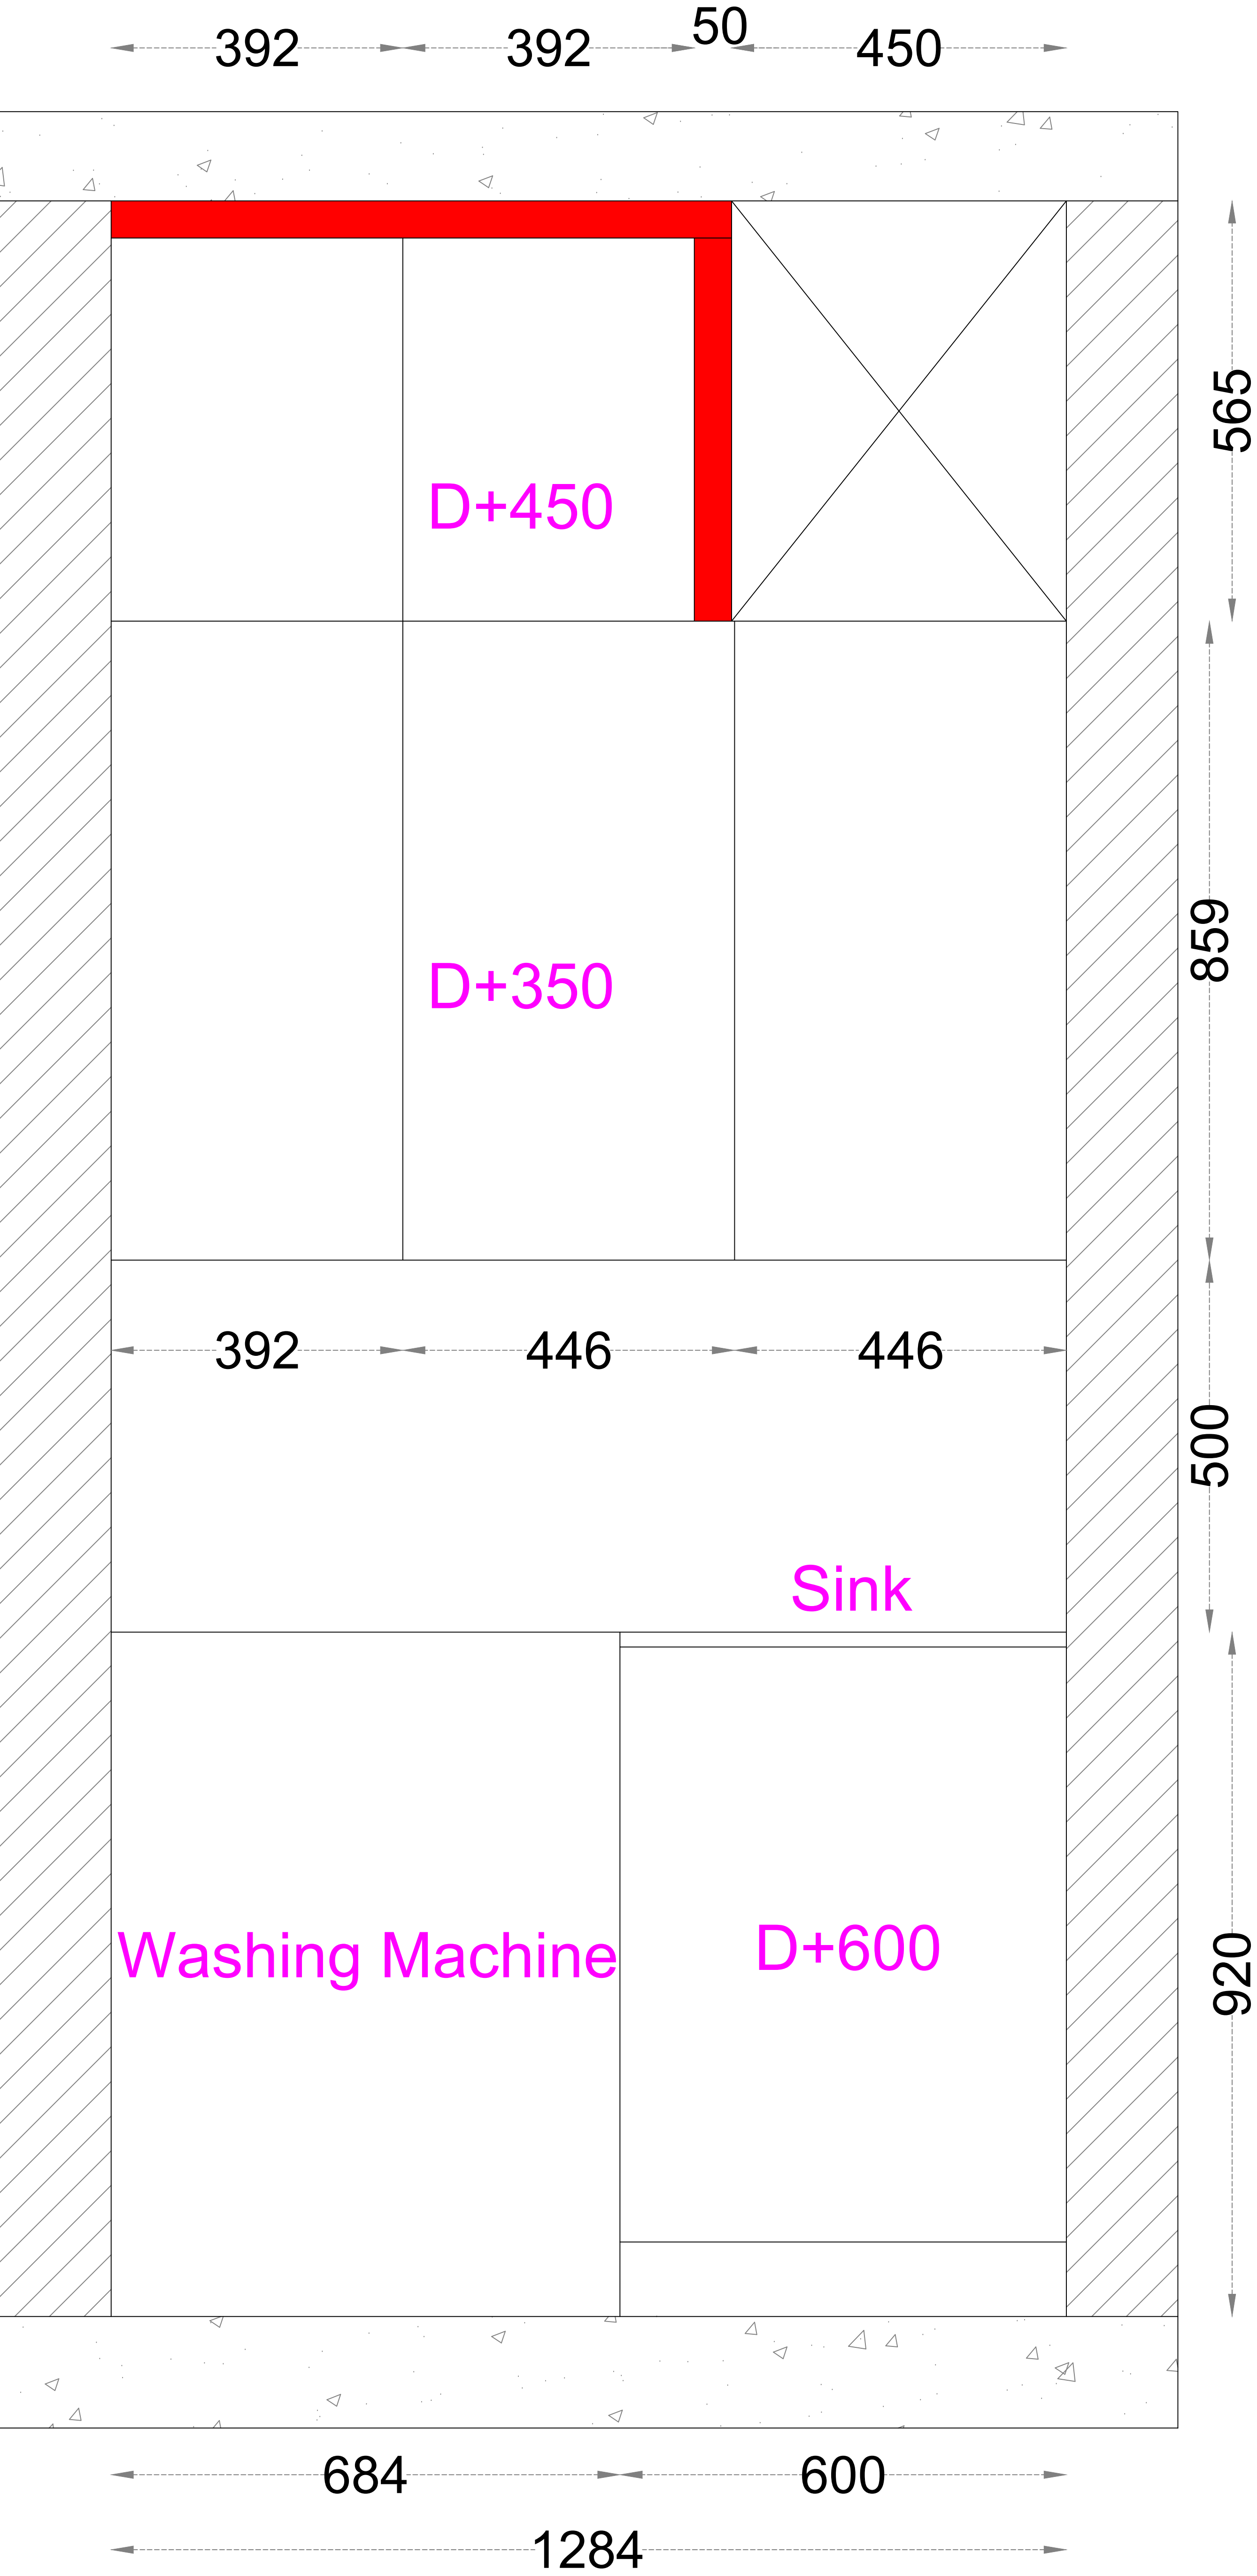

Utility

ALL DIMENSIONS ARE IN MILLIMETERS .
CONTRACTOR HAS TO CHECK & VERIFY ALL LEVELS, DATUM & DIMENSIONS ON SITE AND SHALL REPORT ANY DISCREPANCIES OR OMISSIONS ON SITE THIS OFFICE PRIOR TO THE START OF WORK & DURING THE CONSTRUCTION PHASE.

THIS DRAWING HAS TO BE READ & UNDERSTOOD IN CONJUNCTION WITH STRUCTURAL, MECHANICAL, ELECTRICAL AND/OR ANY OTHER CONSULTANT/S DOCUMENTATION, AS MAY BE APPLICABLE TO THE PROJECT PRIOR TO START OF WORK & IT'S DURATION.

TECHNICAL NOTE :

PROVIDED AS PER STRUCTURAL DRAWINGS & DETAILS.

ANY DISCREPENCY RELATED TO THIS DRAWING SHALL BE BROUGHT TO THE NOTICE OF THE CONCERNED PROJECT ARCHITECTS IMMEDIATELY BEFORE THE EXECUTION OF WORK.

LVLS MENTIONED IN THE DRAWING REFERS TO THE UNFINISHED LEVELS ON THE SITE.

COMPANY NAME
SPACICOUS VENTURE

Address:
Address: Candeur Landmark Liberty blockD903
Varthur, Bengaluru, Karnataka 560087

CLIENT NAME :

Mr.

PROJECT NAME :

INCOR_C1301

DRAWING TITLE :


Utility

DRAWING NO :

SHEET NO	:000
SCALE	: N.T.S
TEAM	Woodpeckers
DRAWN	: Mohd Arfath
CHECKED	: Syedfareed
DESIGNED	: Syedfareed
DATE	: 14-12-2025

ARCHITECTURAL DRAWING

NOTE :
THIS DRAWING IS THE EXCLUSIVE PROPERTY OF "SPACICOUS VENTURE". AND THE REPRODUCTION OF ANY PART WITHOUT PRIOR WRITTEN CONSENT FROM THIS OFFICE IS A VIOLATION OF APPLICABLE LAWS.

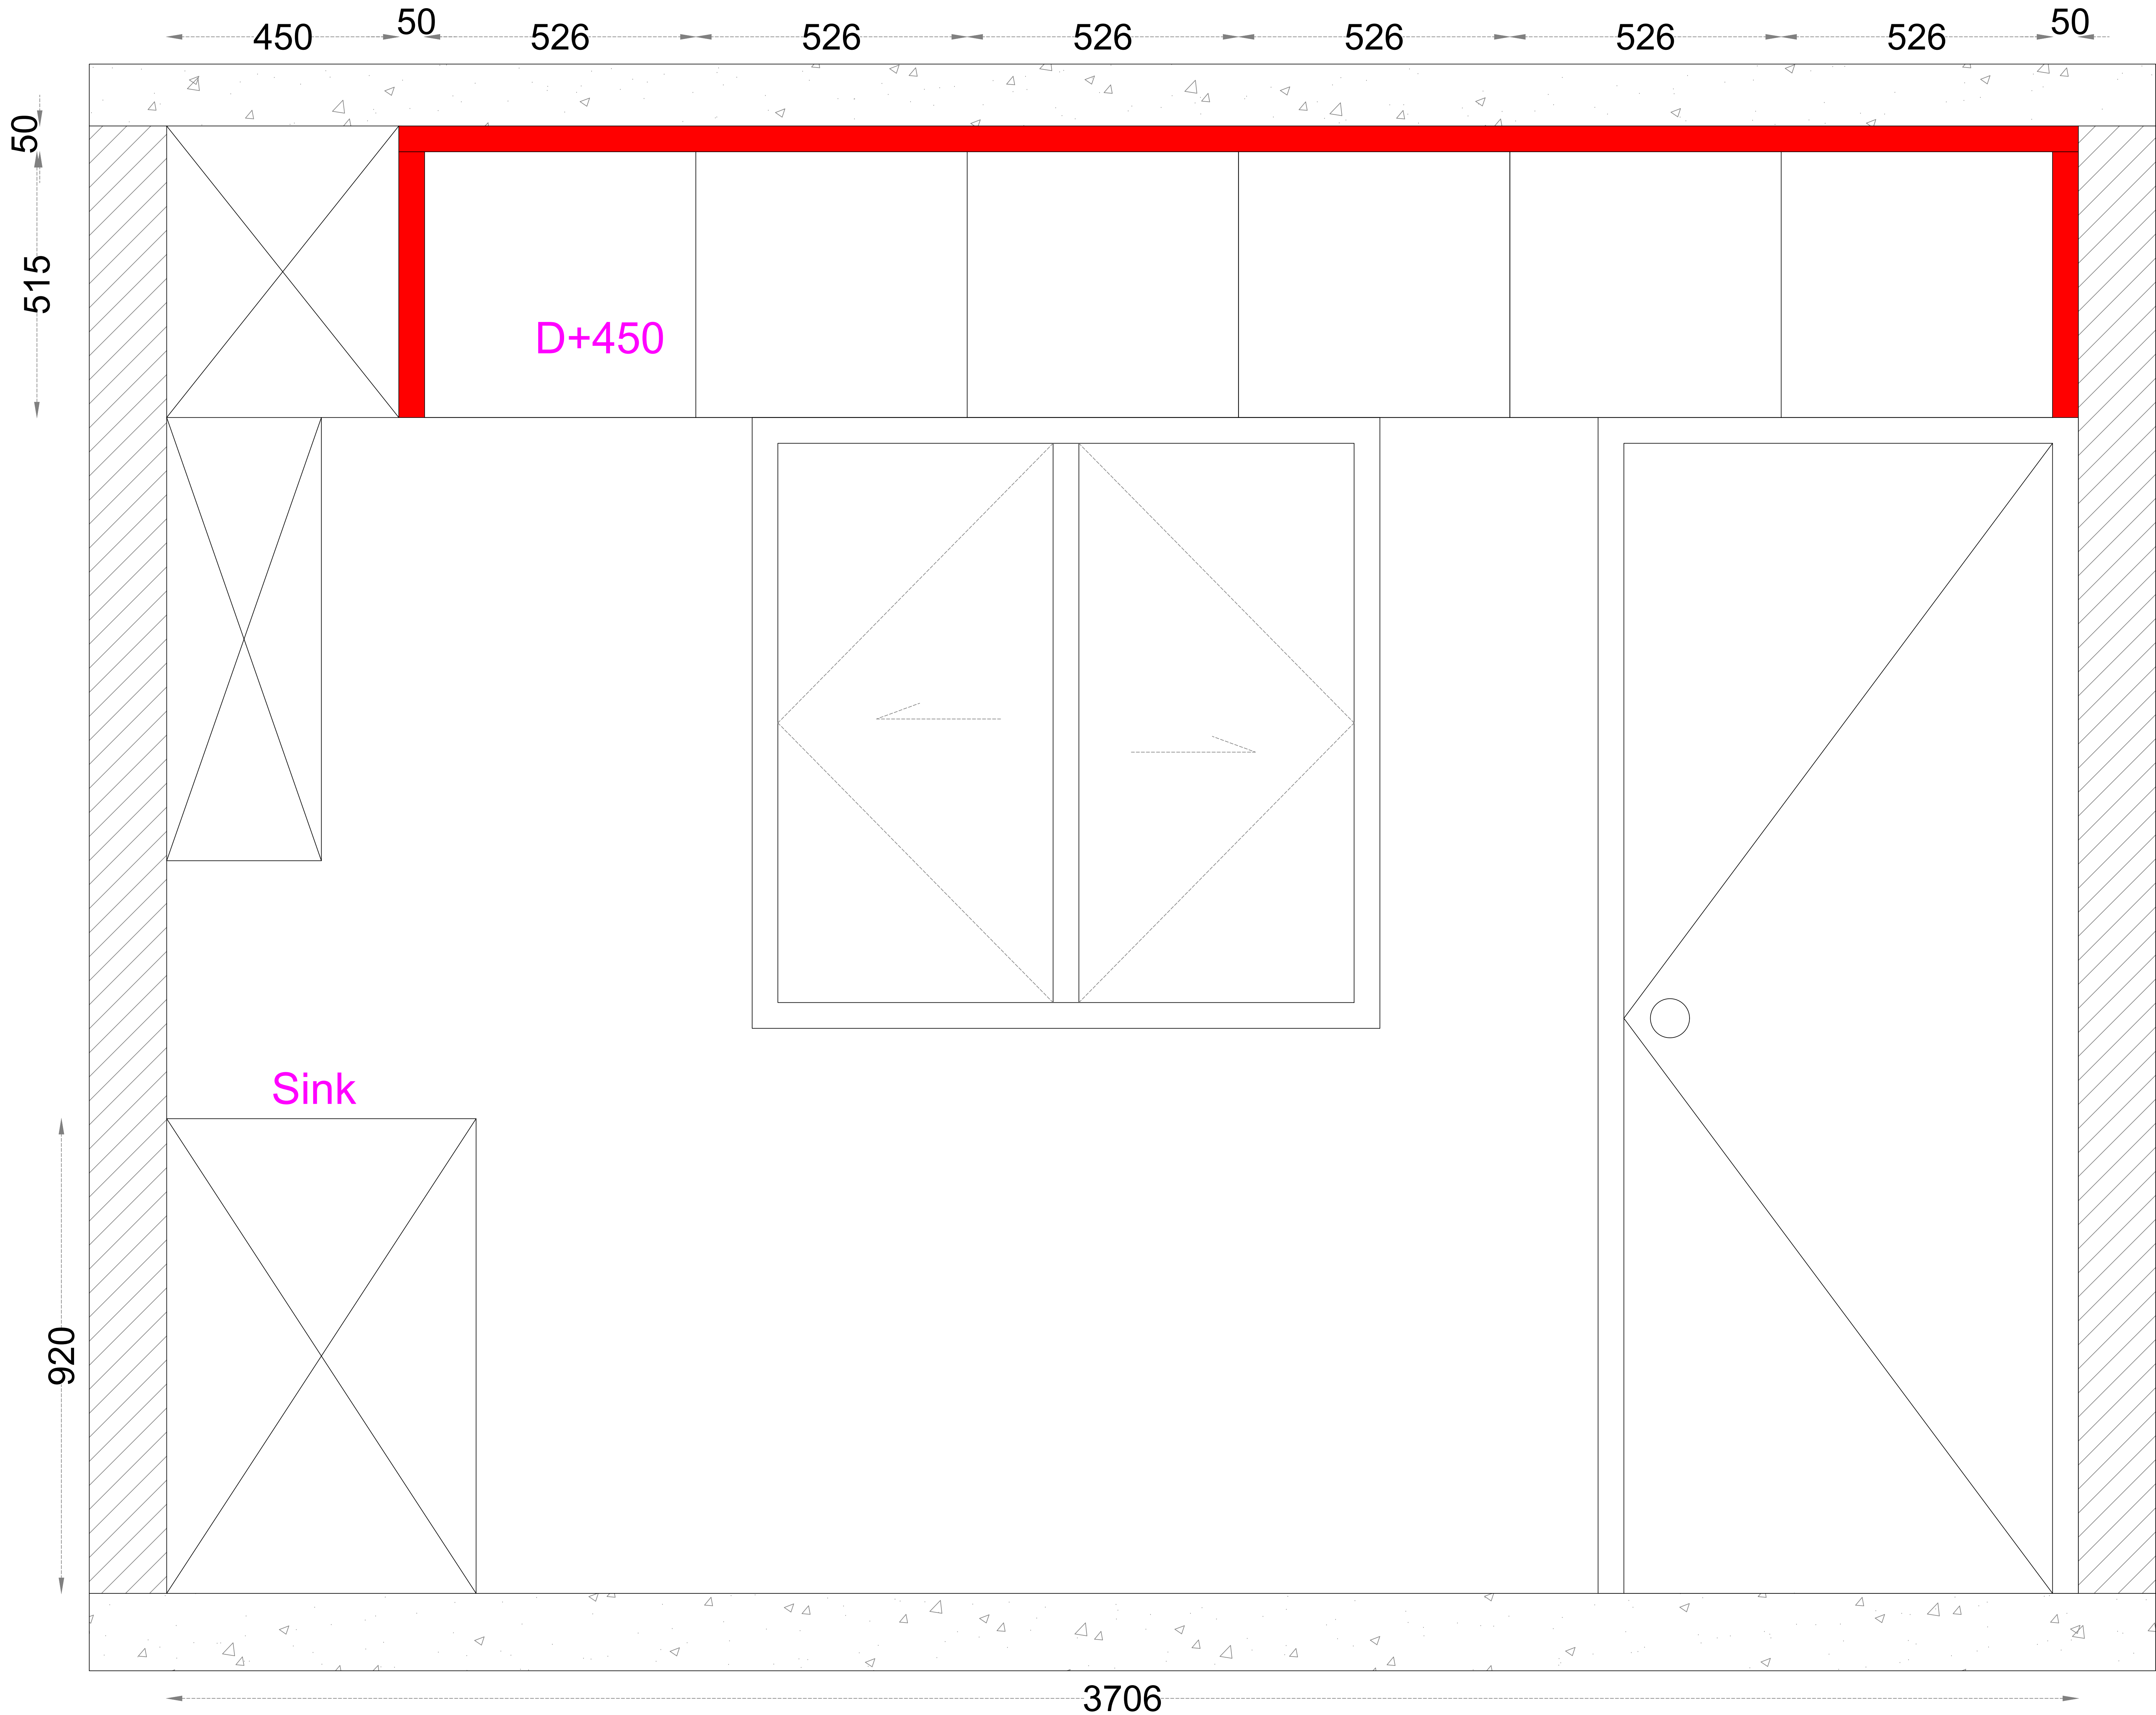

ALL DIMENSIONS ARE IN MILLIMETERS .
CONTRACTOR HAS TO CHECK & VERIFY ALL LEVELS, DATUM & DIMENSIONS ON SITE AND SHALL REPORT ANY DISCREPANCIES OR OMISSIONS ON SITE THIS OFFICE PRIOR TO THE START OF WORK & DURING THE CONSTRUCTION PHASE.
THIS DRAWING HAS TO BE READ & UNDERSTOOD IN CONJUNCTION WITH STRUCTURAL, MECHANICAL, ELECTRICAL AND/OR ANY OTHER CONSULTANT/S DOCUMENTATION, AS MAY BE APPLICABLE TO THE PROJECT PRIOR TO START OF WORK & IT'S DURATION.

TECHNICAL NOTE :
PROVIDED AS PER STRUCTURAL DRAWINGS & DETAILS.
ANY DISCREPENCY RELATED TO THIS DRAWING SHALL BE BROUGHT TO THE NOTICE OF THE CONCERNED PROJECT ARCHITECTS IMMEDIATELY BEFORE THE EXECUTION OF WORK.
LVLS MENTIONED IN THE DRAWING REFERS TO THE UNFINISHED LEVELS ON THE SITE.

COMPANY NAME
SPACICOUS VENTURE
Address:
Address: Candeur Landmark Liberty blockD903
Varthur, Bengaluru, Karnataka 560087

CLIENT NAME :
Mr.

PROJECT NAME :
INCOR_C1301


DRAWING TITLE :
Utility_Loft

DRAWING NO :

SHEET NO	:000
SCALE	: N.T.S
TEAM	Woodpeckers
DRAWN	: Mohd Arfath
CHECKED	: Syedfareed
DESIGNED	: Syedfareed
DATE	: 14-12-2025

ARCHITECTURAL DRAWING

NOTE :
THIS DRAWING IS THE EXCLUSIVE PROPERTY OF "SPACICOUS VENTURE". AND THE REPRODUCTION OF ANY PART WITHOUT PRIOR WRITTEN CONSENT FROM THIS OFFICE IS A VIOLATION OF APPLICABLE LAWS.

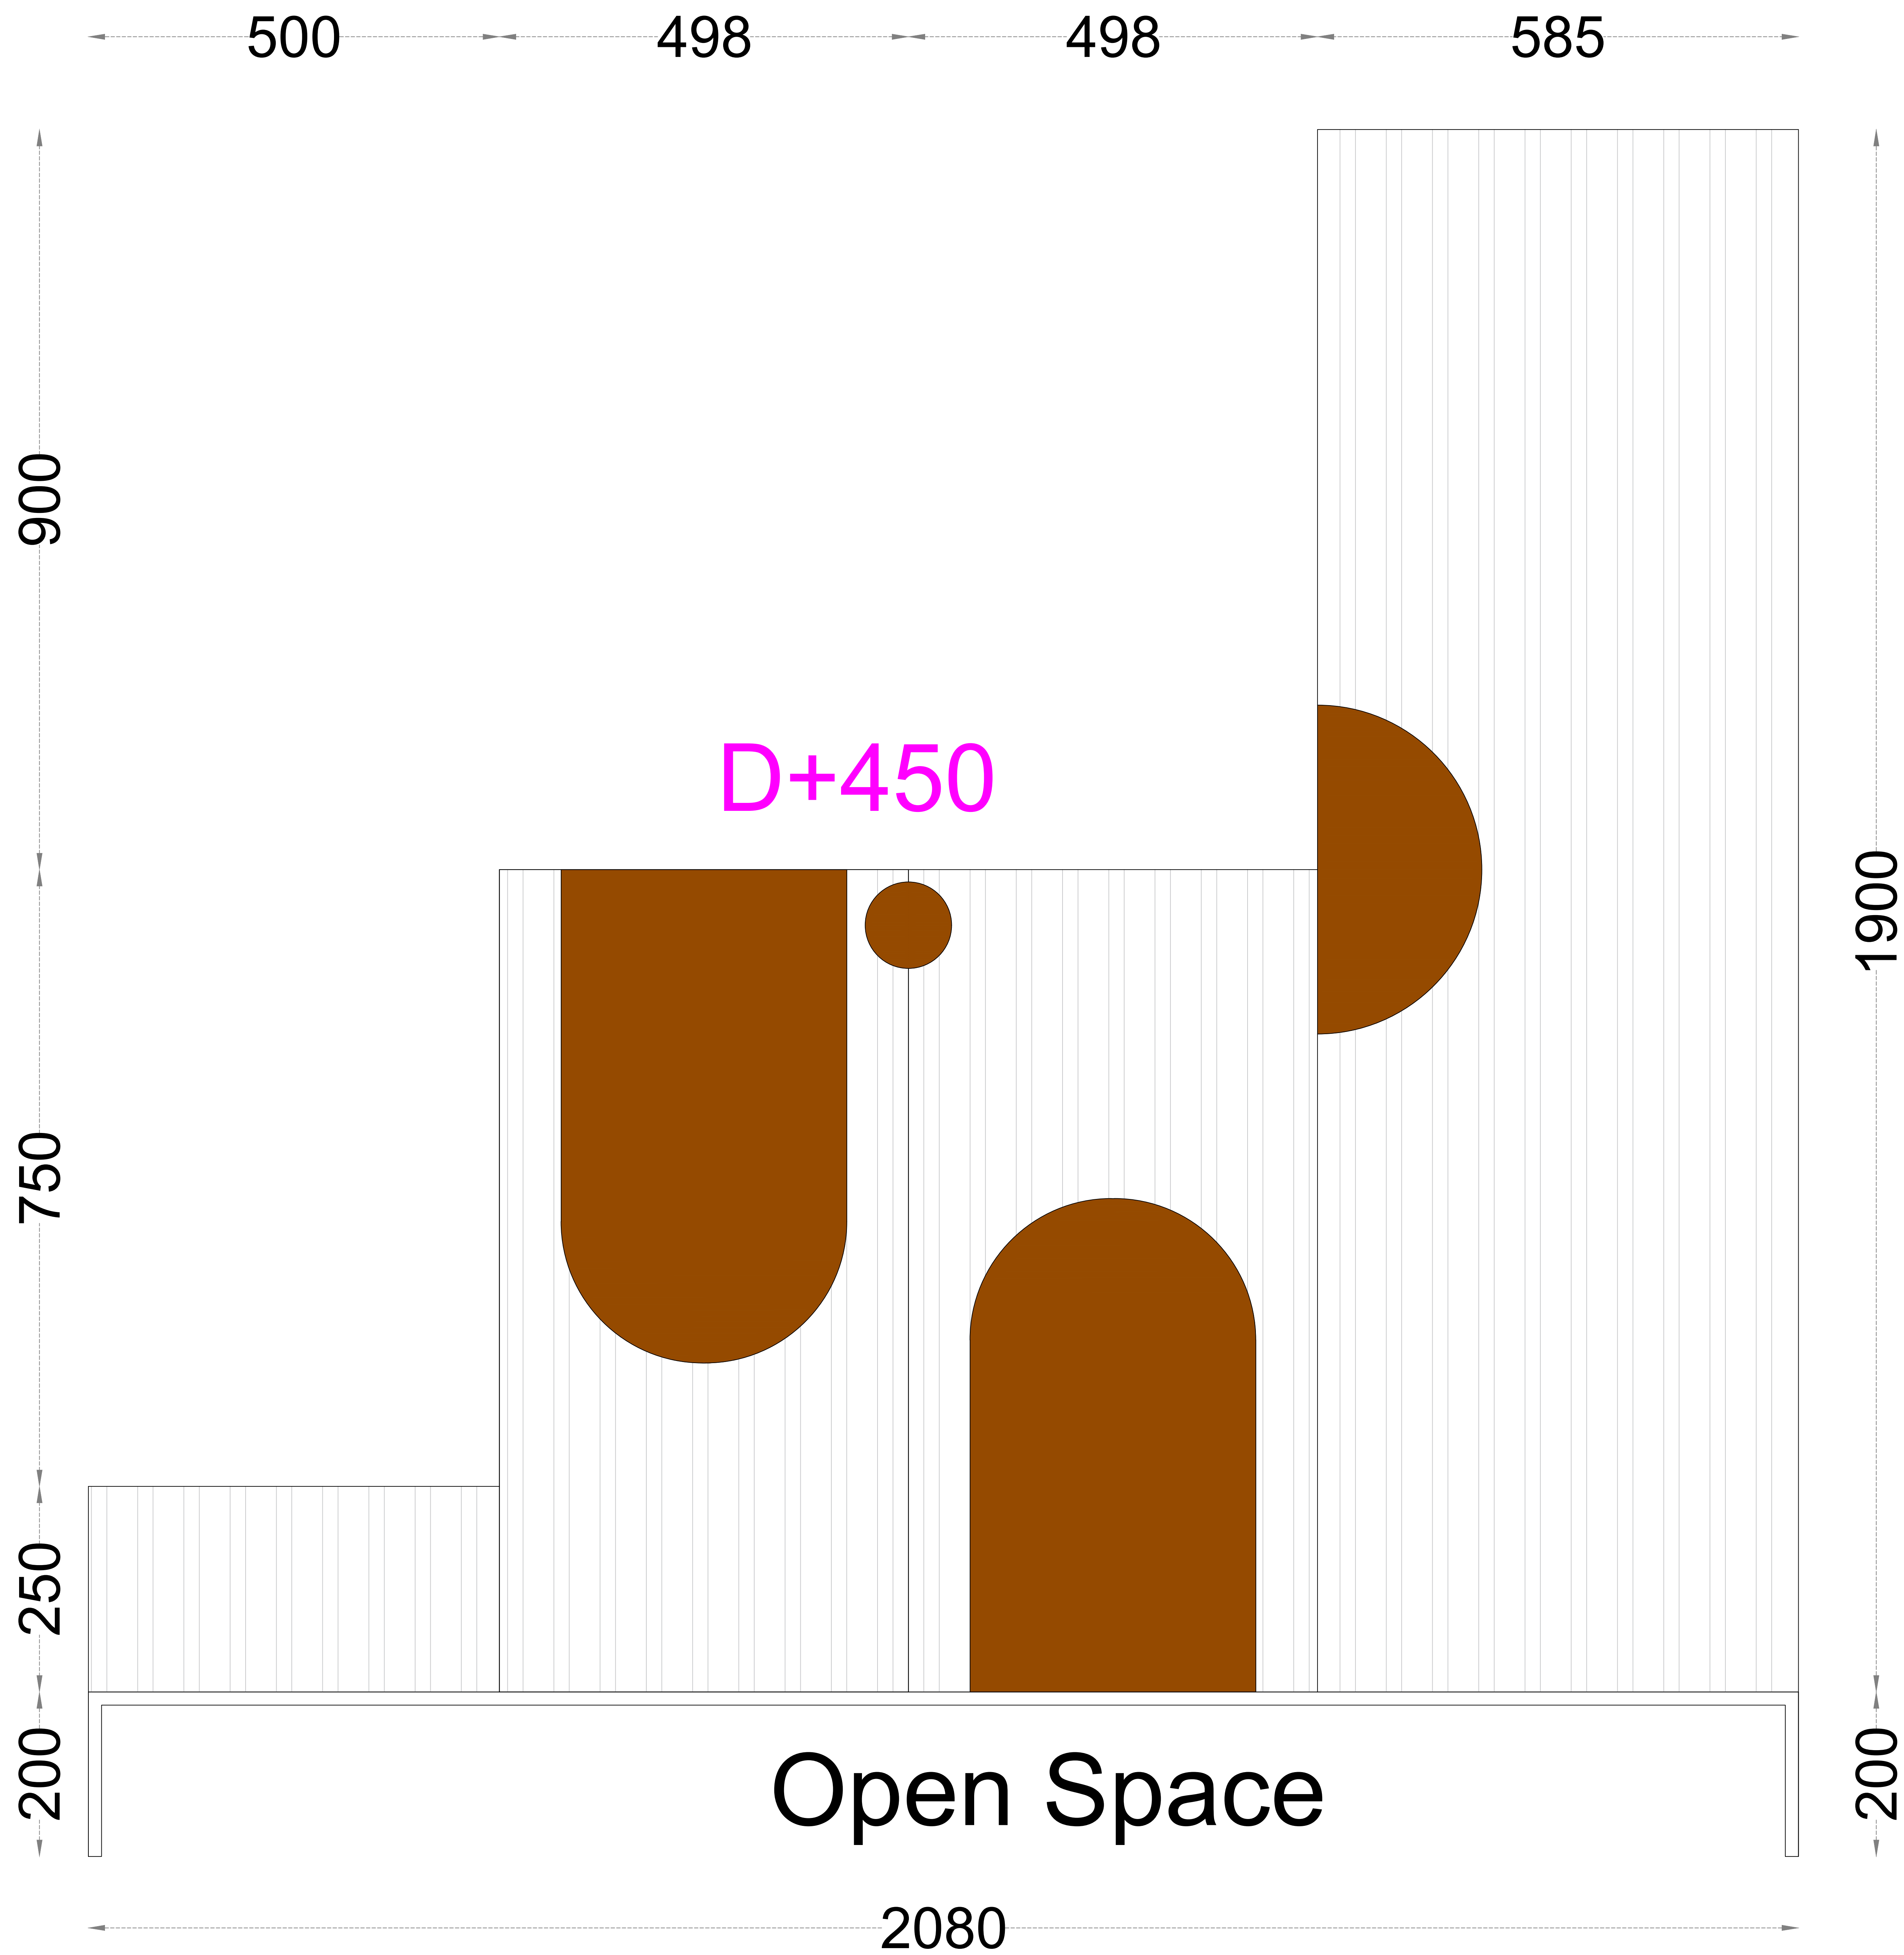

ALL DIMENSIONS ARE IN MILLIMETERS .
CONTRACTOR HAS TO CHECK & VERIFY ALL LEVELS, DATUM & DIMENSIONS ON SITE AND SHALL REPORT ANY DISCREPANCIES OR OMISSIONS ON SITE THIS OFFICE PRIOR TO THE START OF WORK & DURING THE CONSTRUCTION PHASE.

THIS DRAWING HAS TO BE READ & UNDERSTOOD IN CONJUNCTION WITH STRUCTURAL, MECHANICAL, ELECTRICAL AND/OR ANY OTHER CONSULTANT/S DOCUMENTATION, AS MAY BE APPLICABLE TO THE PROJECT PRIOR TO START OF WORK & IT'S DURATION.

TECHNICAL NOTE :

PROVIDED AS PER STRUCTURAL DRAWINGS & DETAILS.

ANY DISCREPENCY RELATED TO THIS DRAWING SHALL BE BROUGHT TO THE NOTICE OF THE CONCERNED PROJECT ARCHITECTS IMMEDIATELY BEFORE THE EXECUTION OF WORK.

LVLS MENTIONED IN THE DRAWING REFERS TO THE UNFINISHED LEVELS ON THE SITE.

COMPANY NAME
SPACICOUS VENTURE

Address:
Address: Candeur Landmark Liberty blockD903
Varthur, Bengaluru, Karnataka 560087

CLIENT NAME :

Mr.

PROJECT NAME :

INCOR_C1301

DRAWING TITLE :

Shoe Rack

DRAWING NO :

SHEET NO :000

SCALE : N.T.S

TEAM Woodpeckers

DRAWN : Mohd Arfath
CHECKED : Syedfareed
DESIGNED : Syedfareed
DATE : 14-12-2025

ARCHITECTURAL DRAWING

NOTE :
THIS DRAWING IS THE EXCLUSIVE PROPERTY OF "SPACICOUS VENTURE". AND THE REPRODUCTION OF ANY PART WITHOUT PRIOR WRITTEN CONSENT FROM THIS OFFICE IS A VIOLATION OF APPLICABLE LAWS.