


2D ELEVATIONS

DESIGNER NAME	MUSKAN PAREEK
---------------	---------------



TV UNIT

DEPTH - 430 + 20

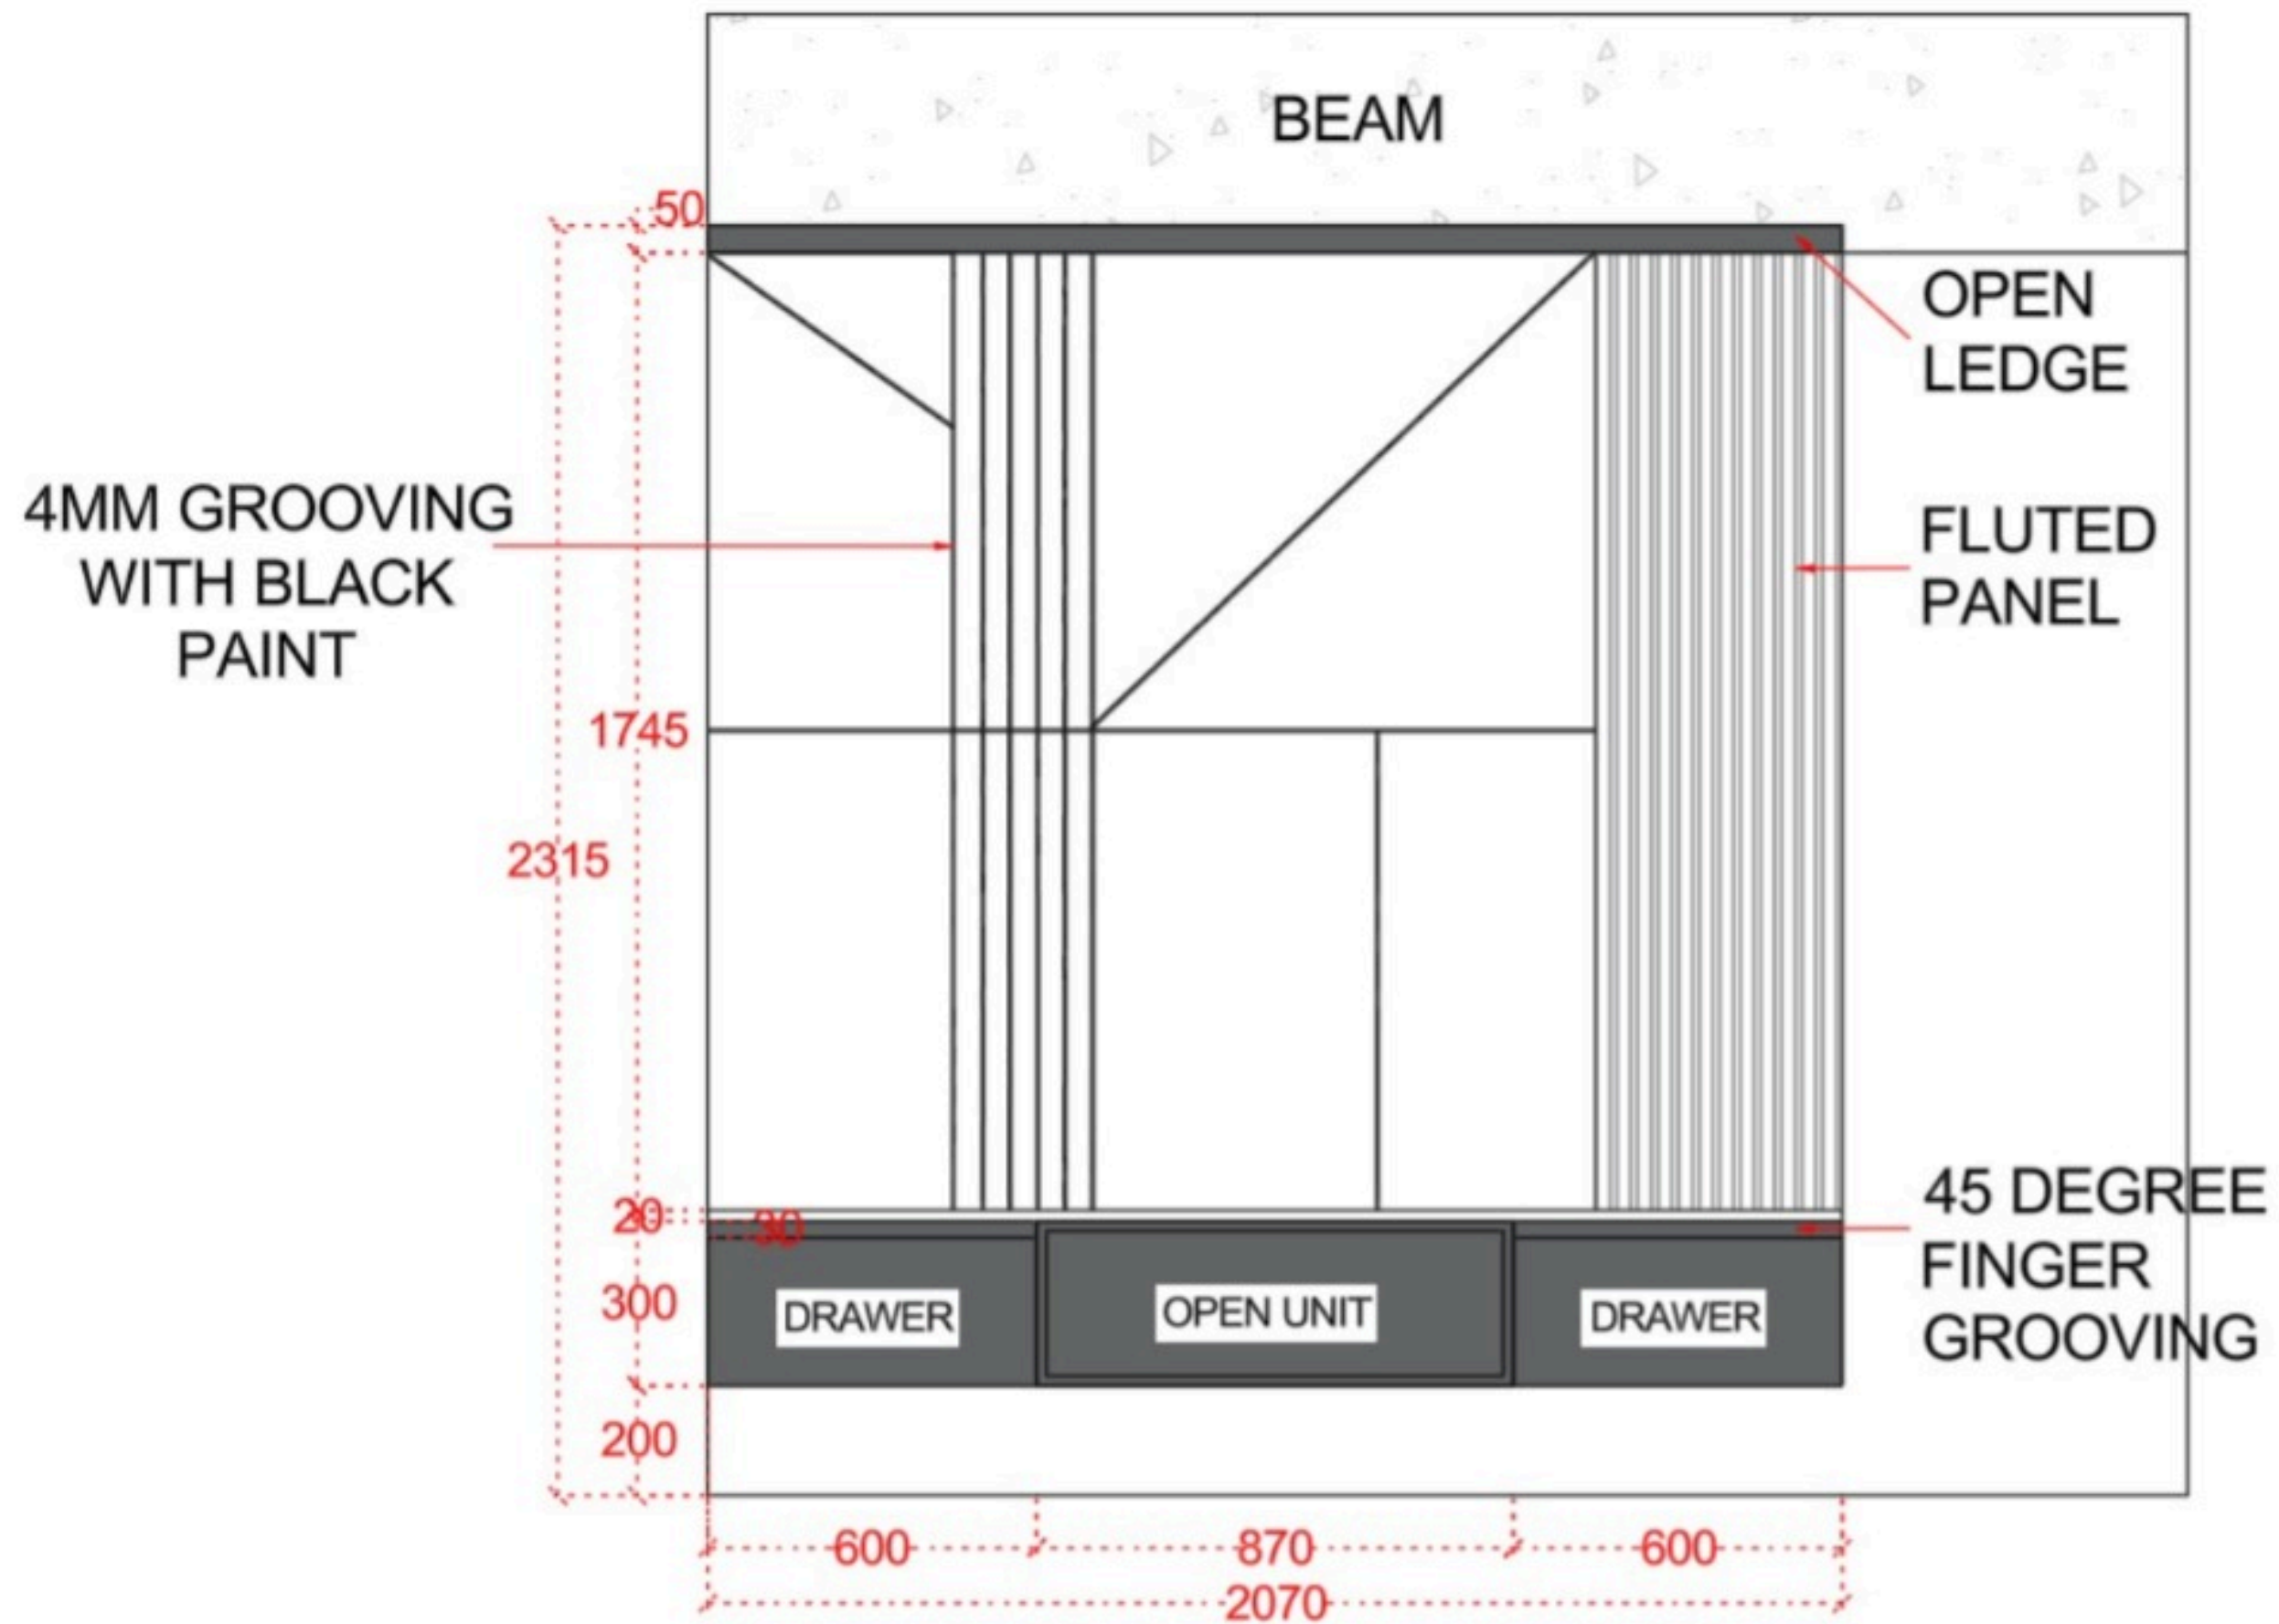



CROKERY - EXTERNAL

DEPTH - 400+ 20

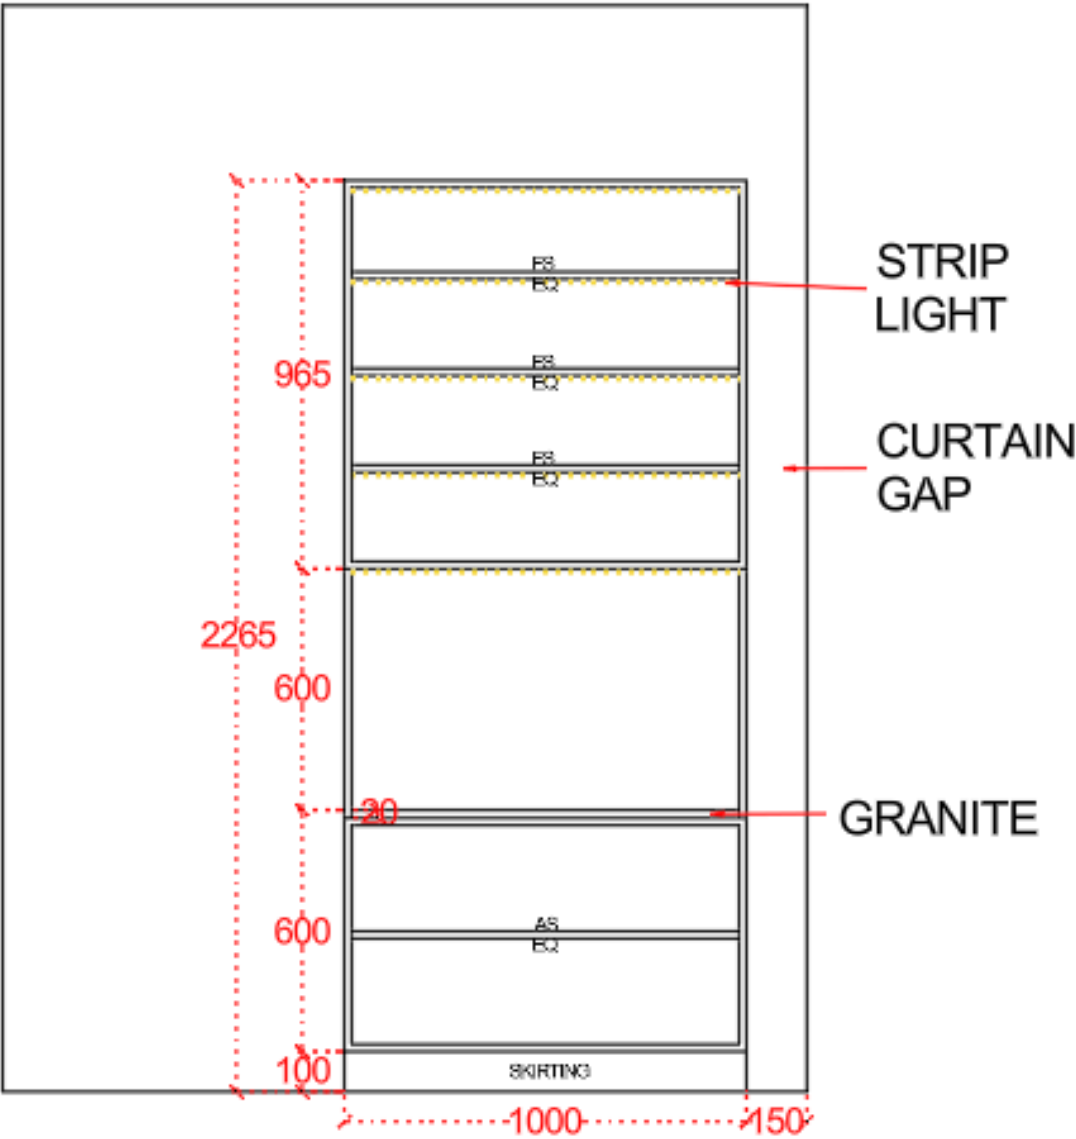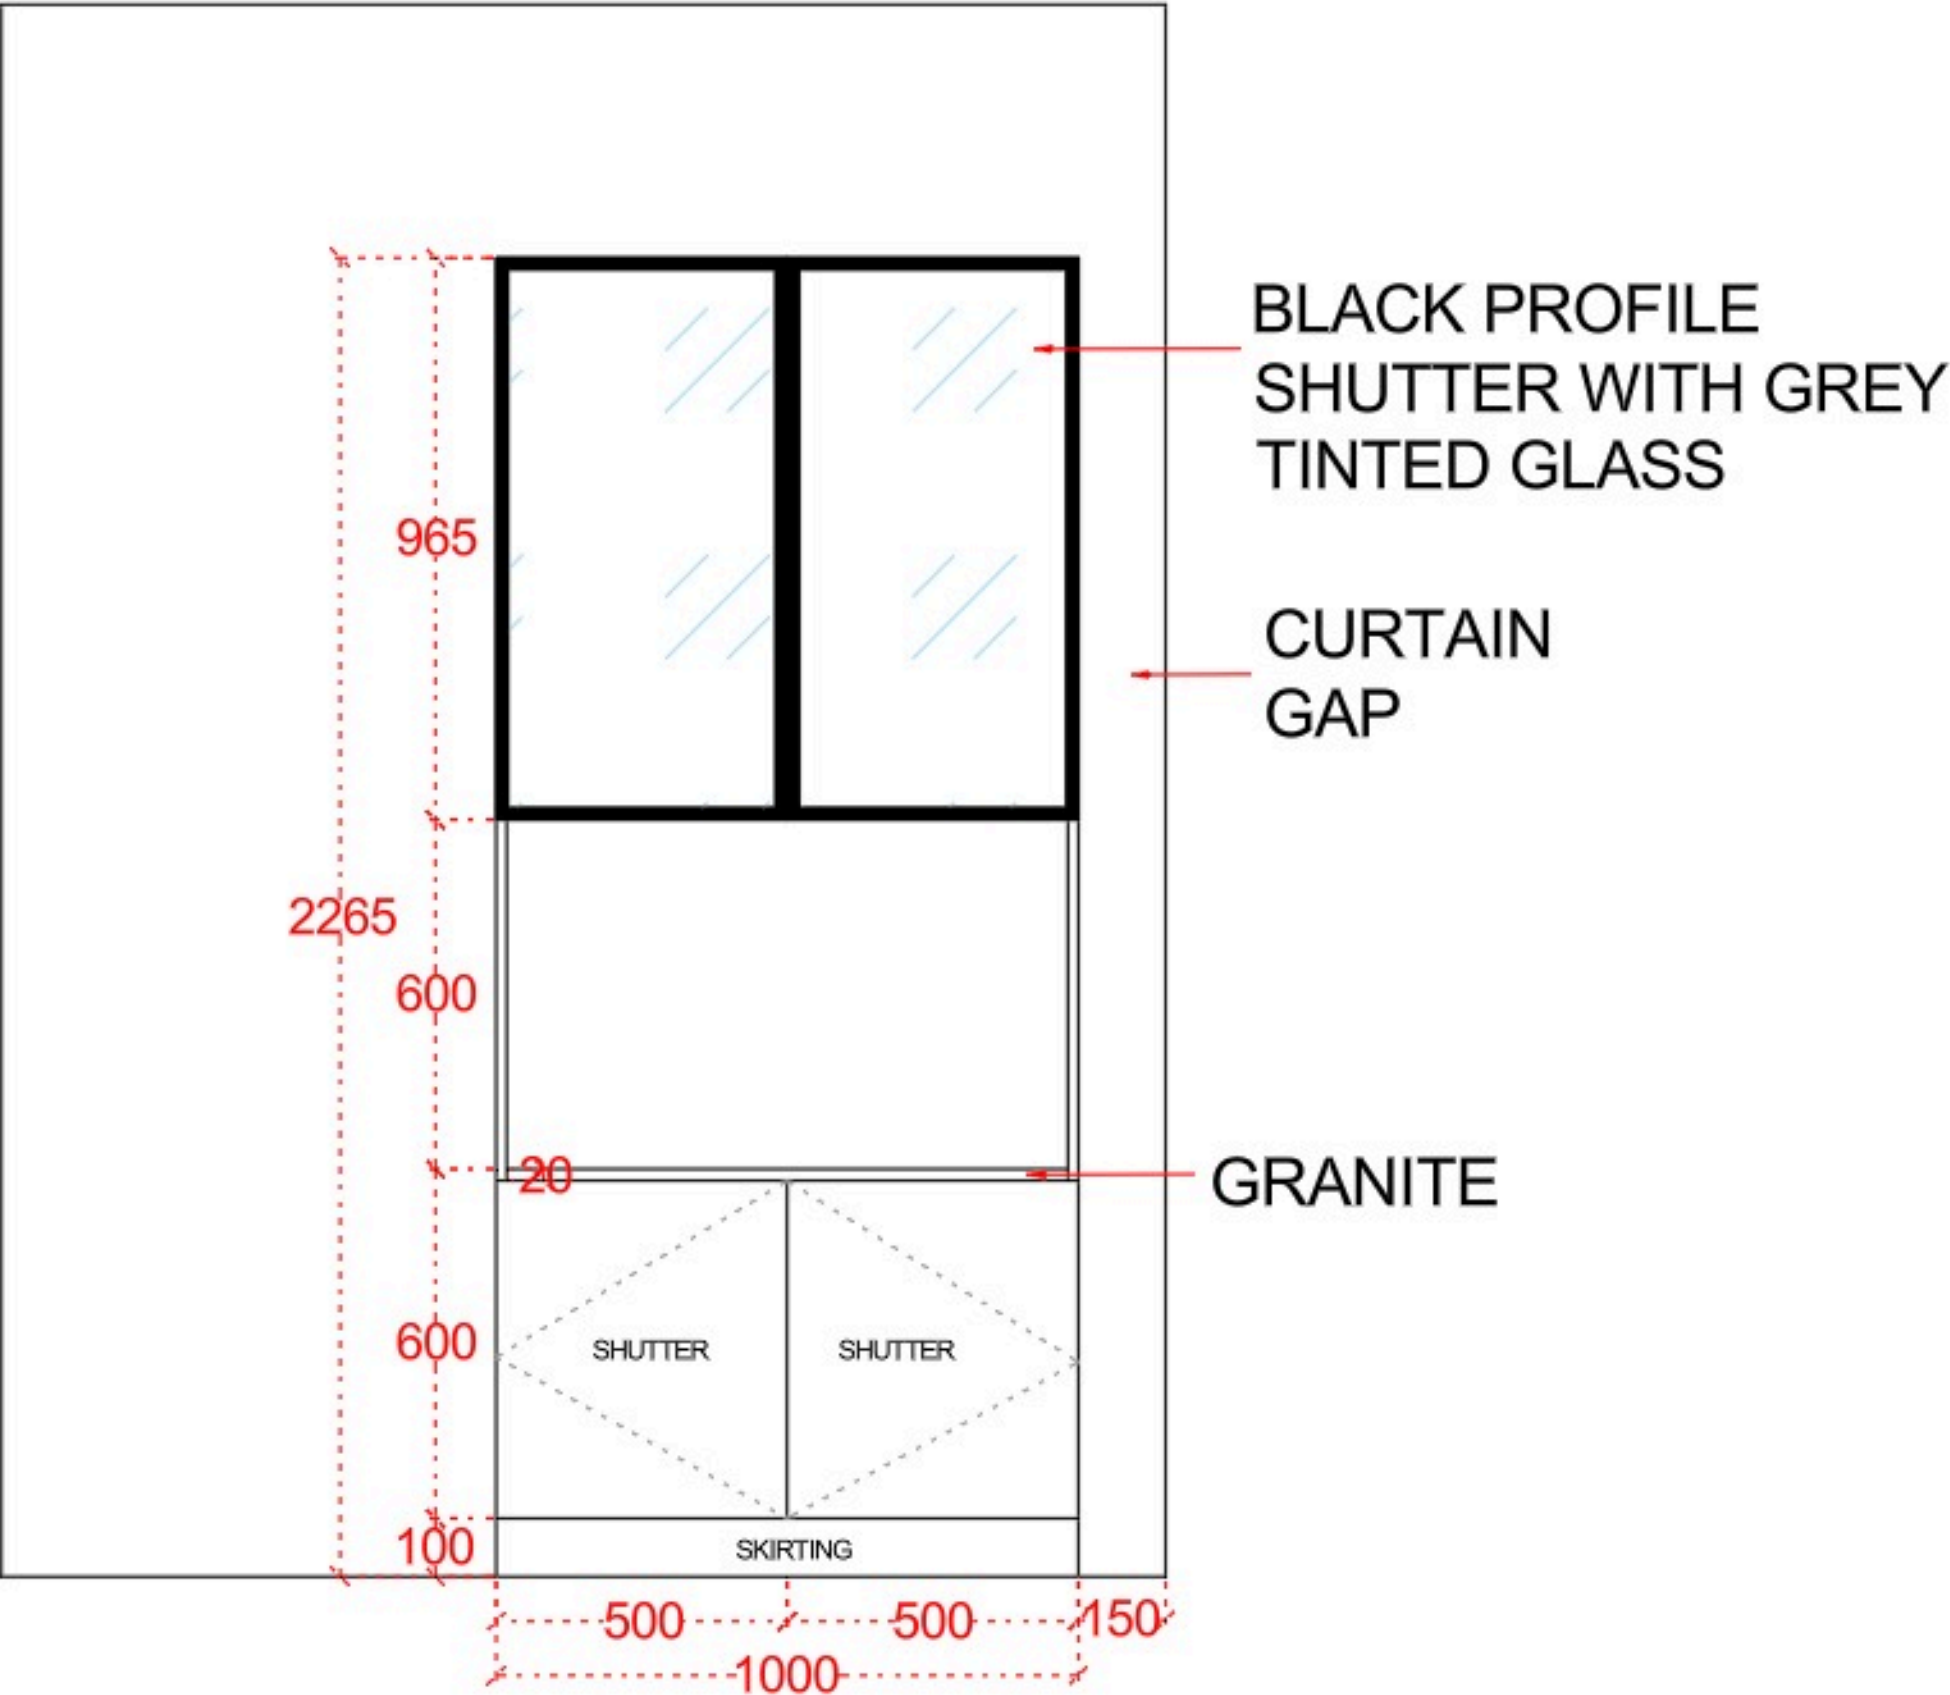



COMMON WASHROOM

DEPTH – 100 + 20

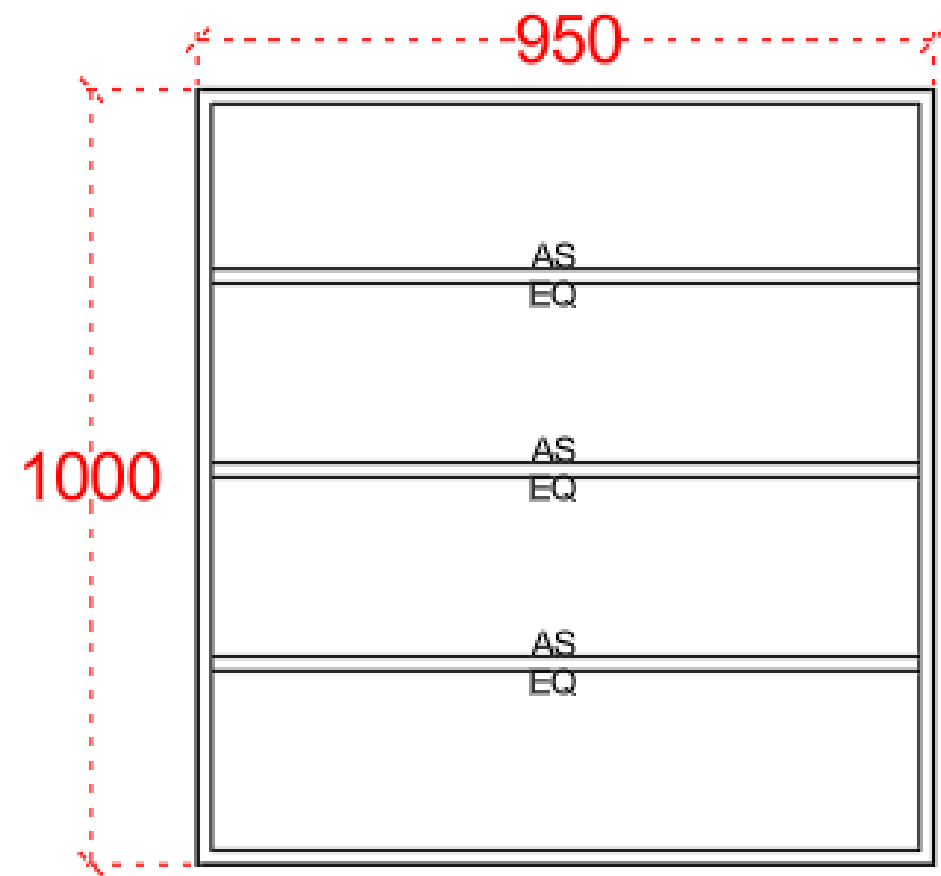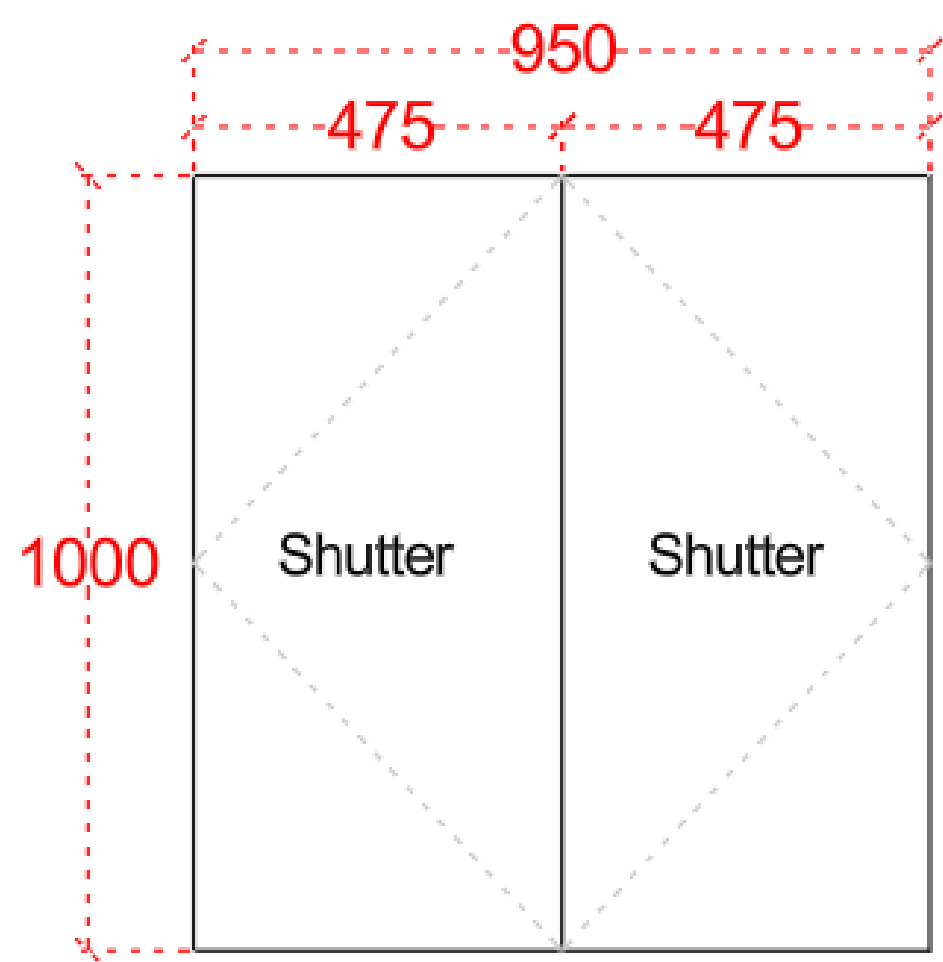


POOJA UNIT

DEPTH - 430 + 20

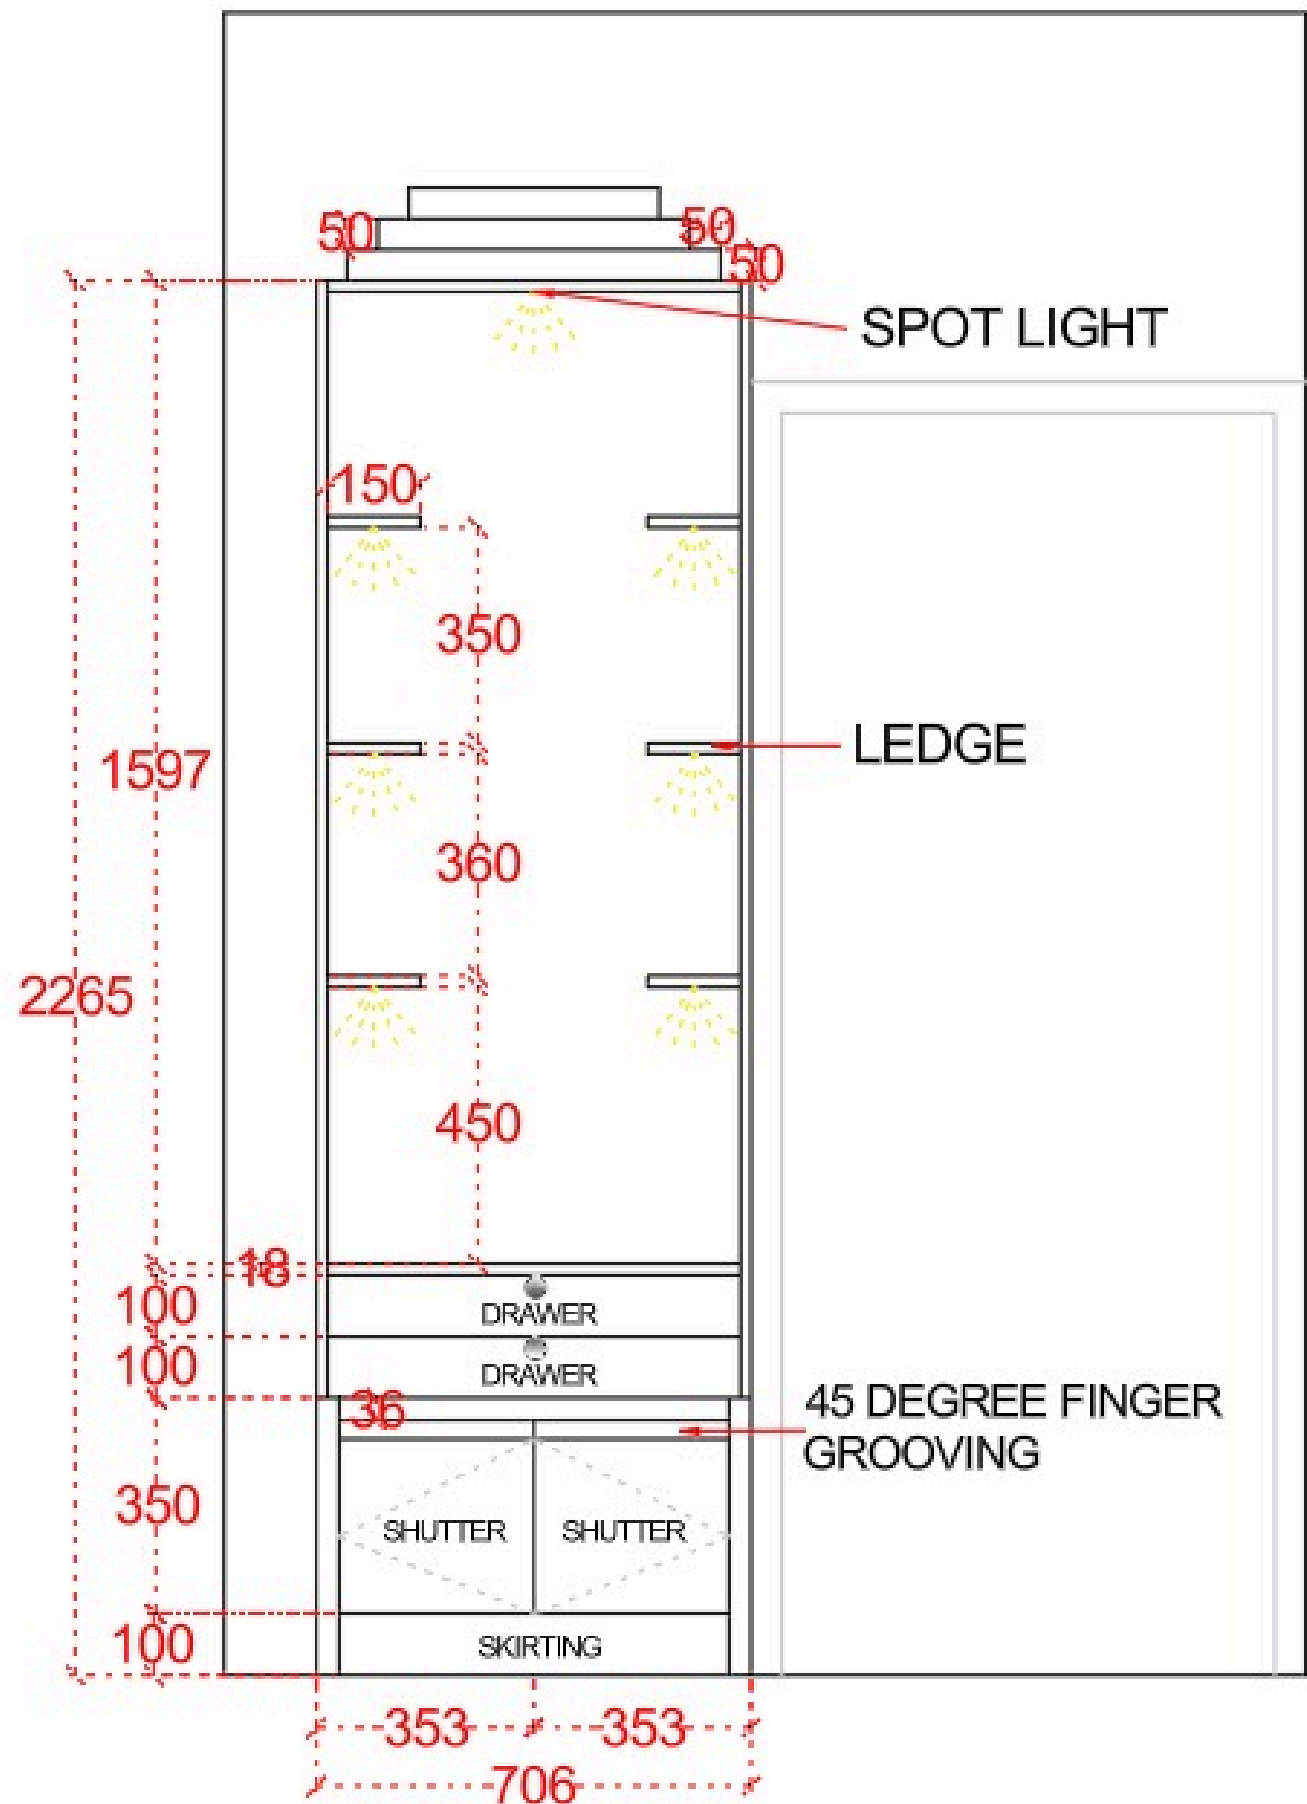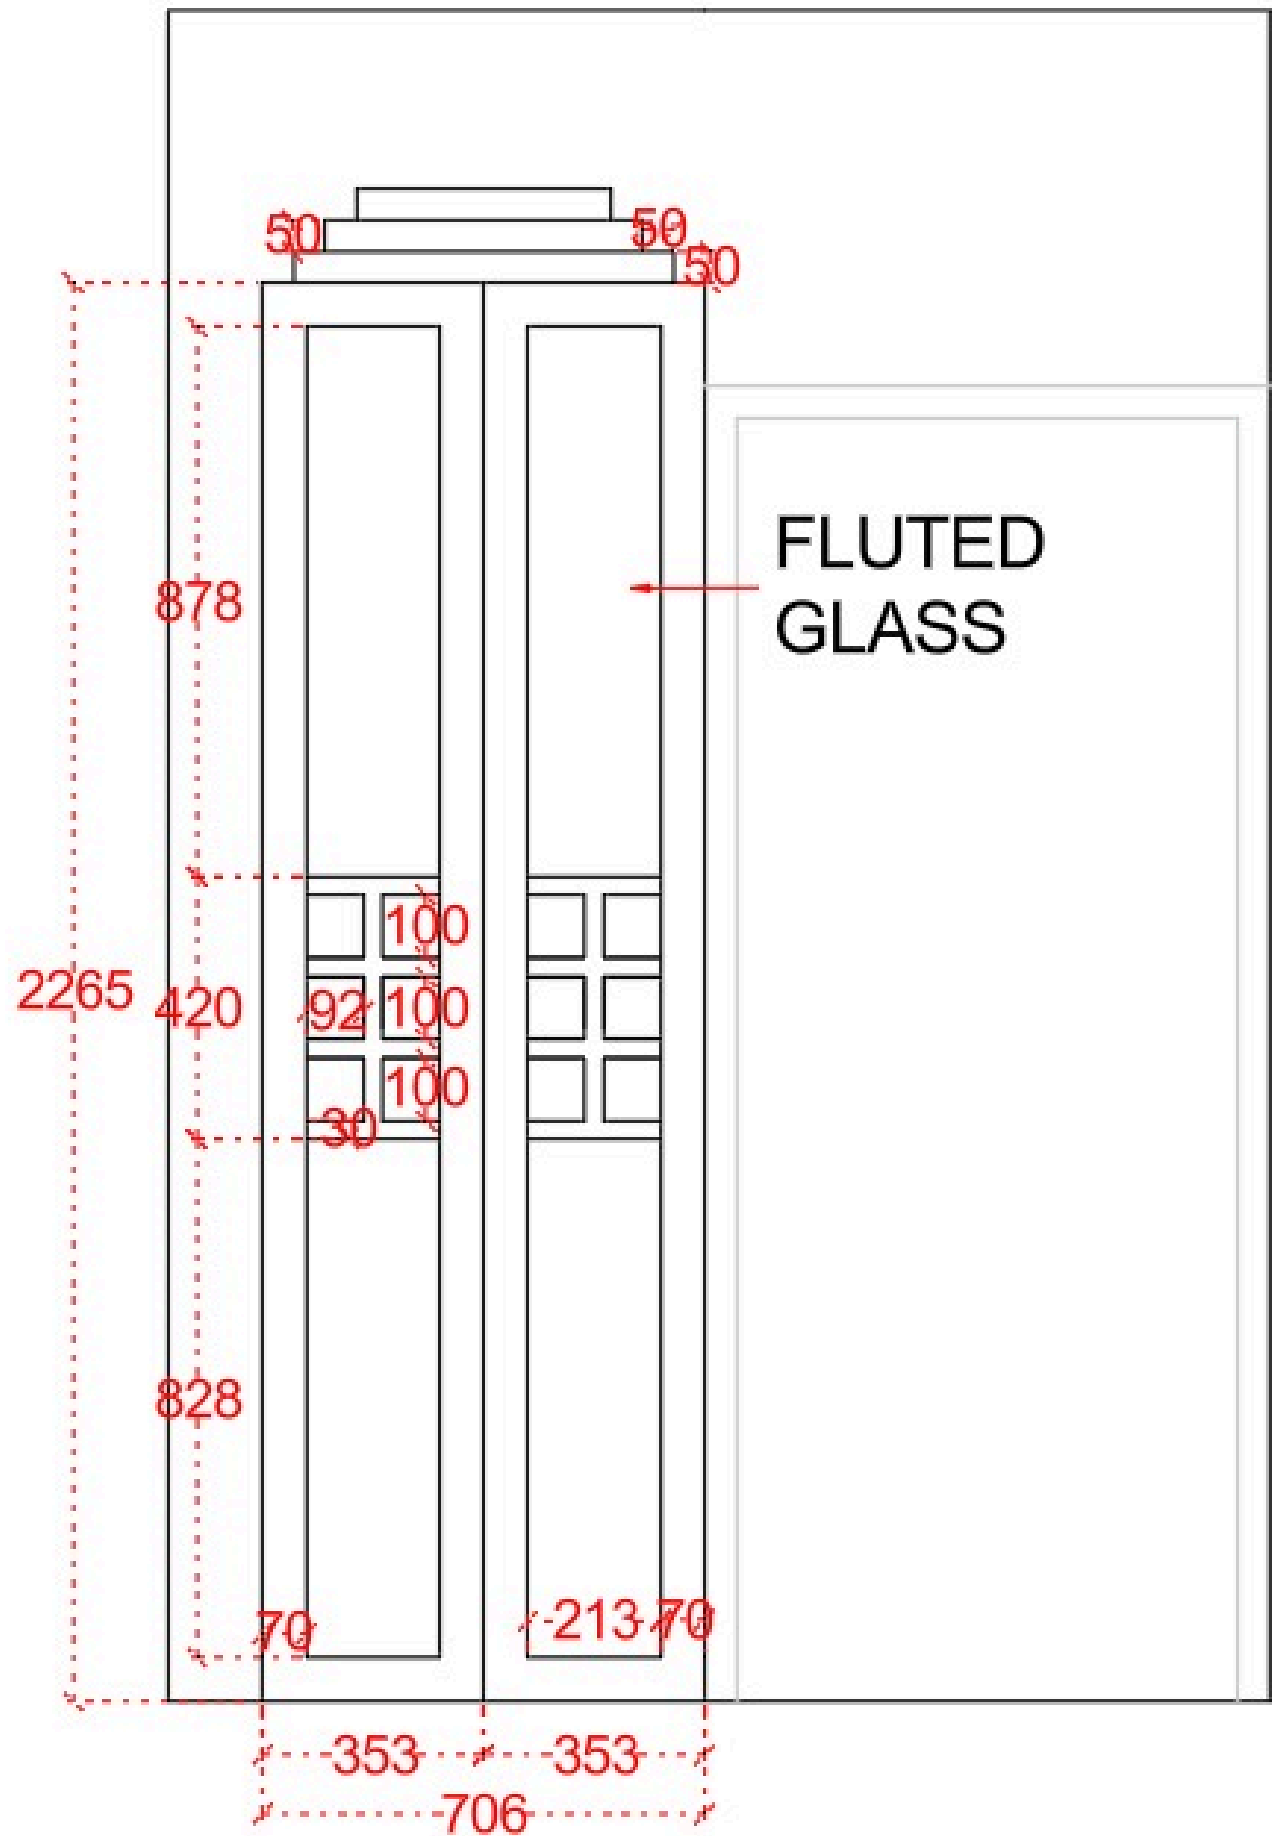

KITCHEN WALL A EXTERNAL

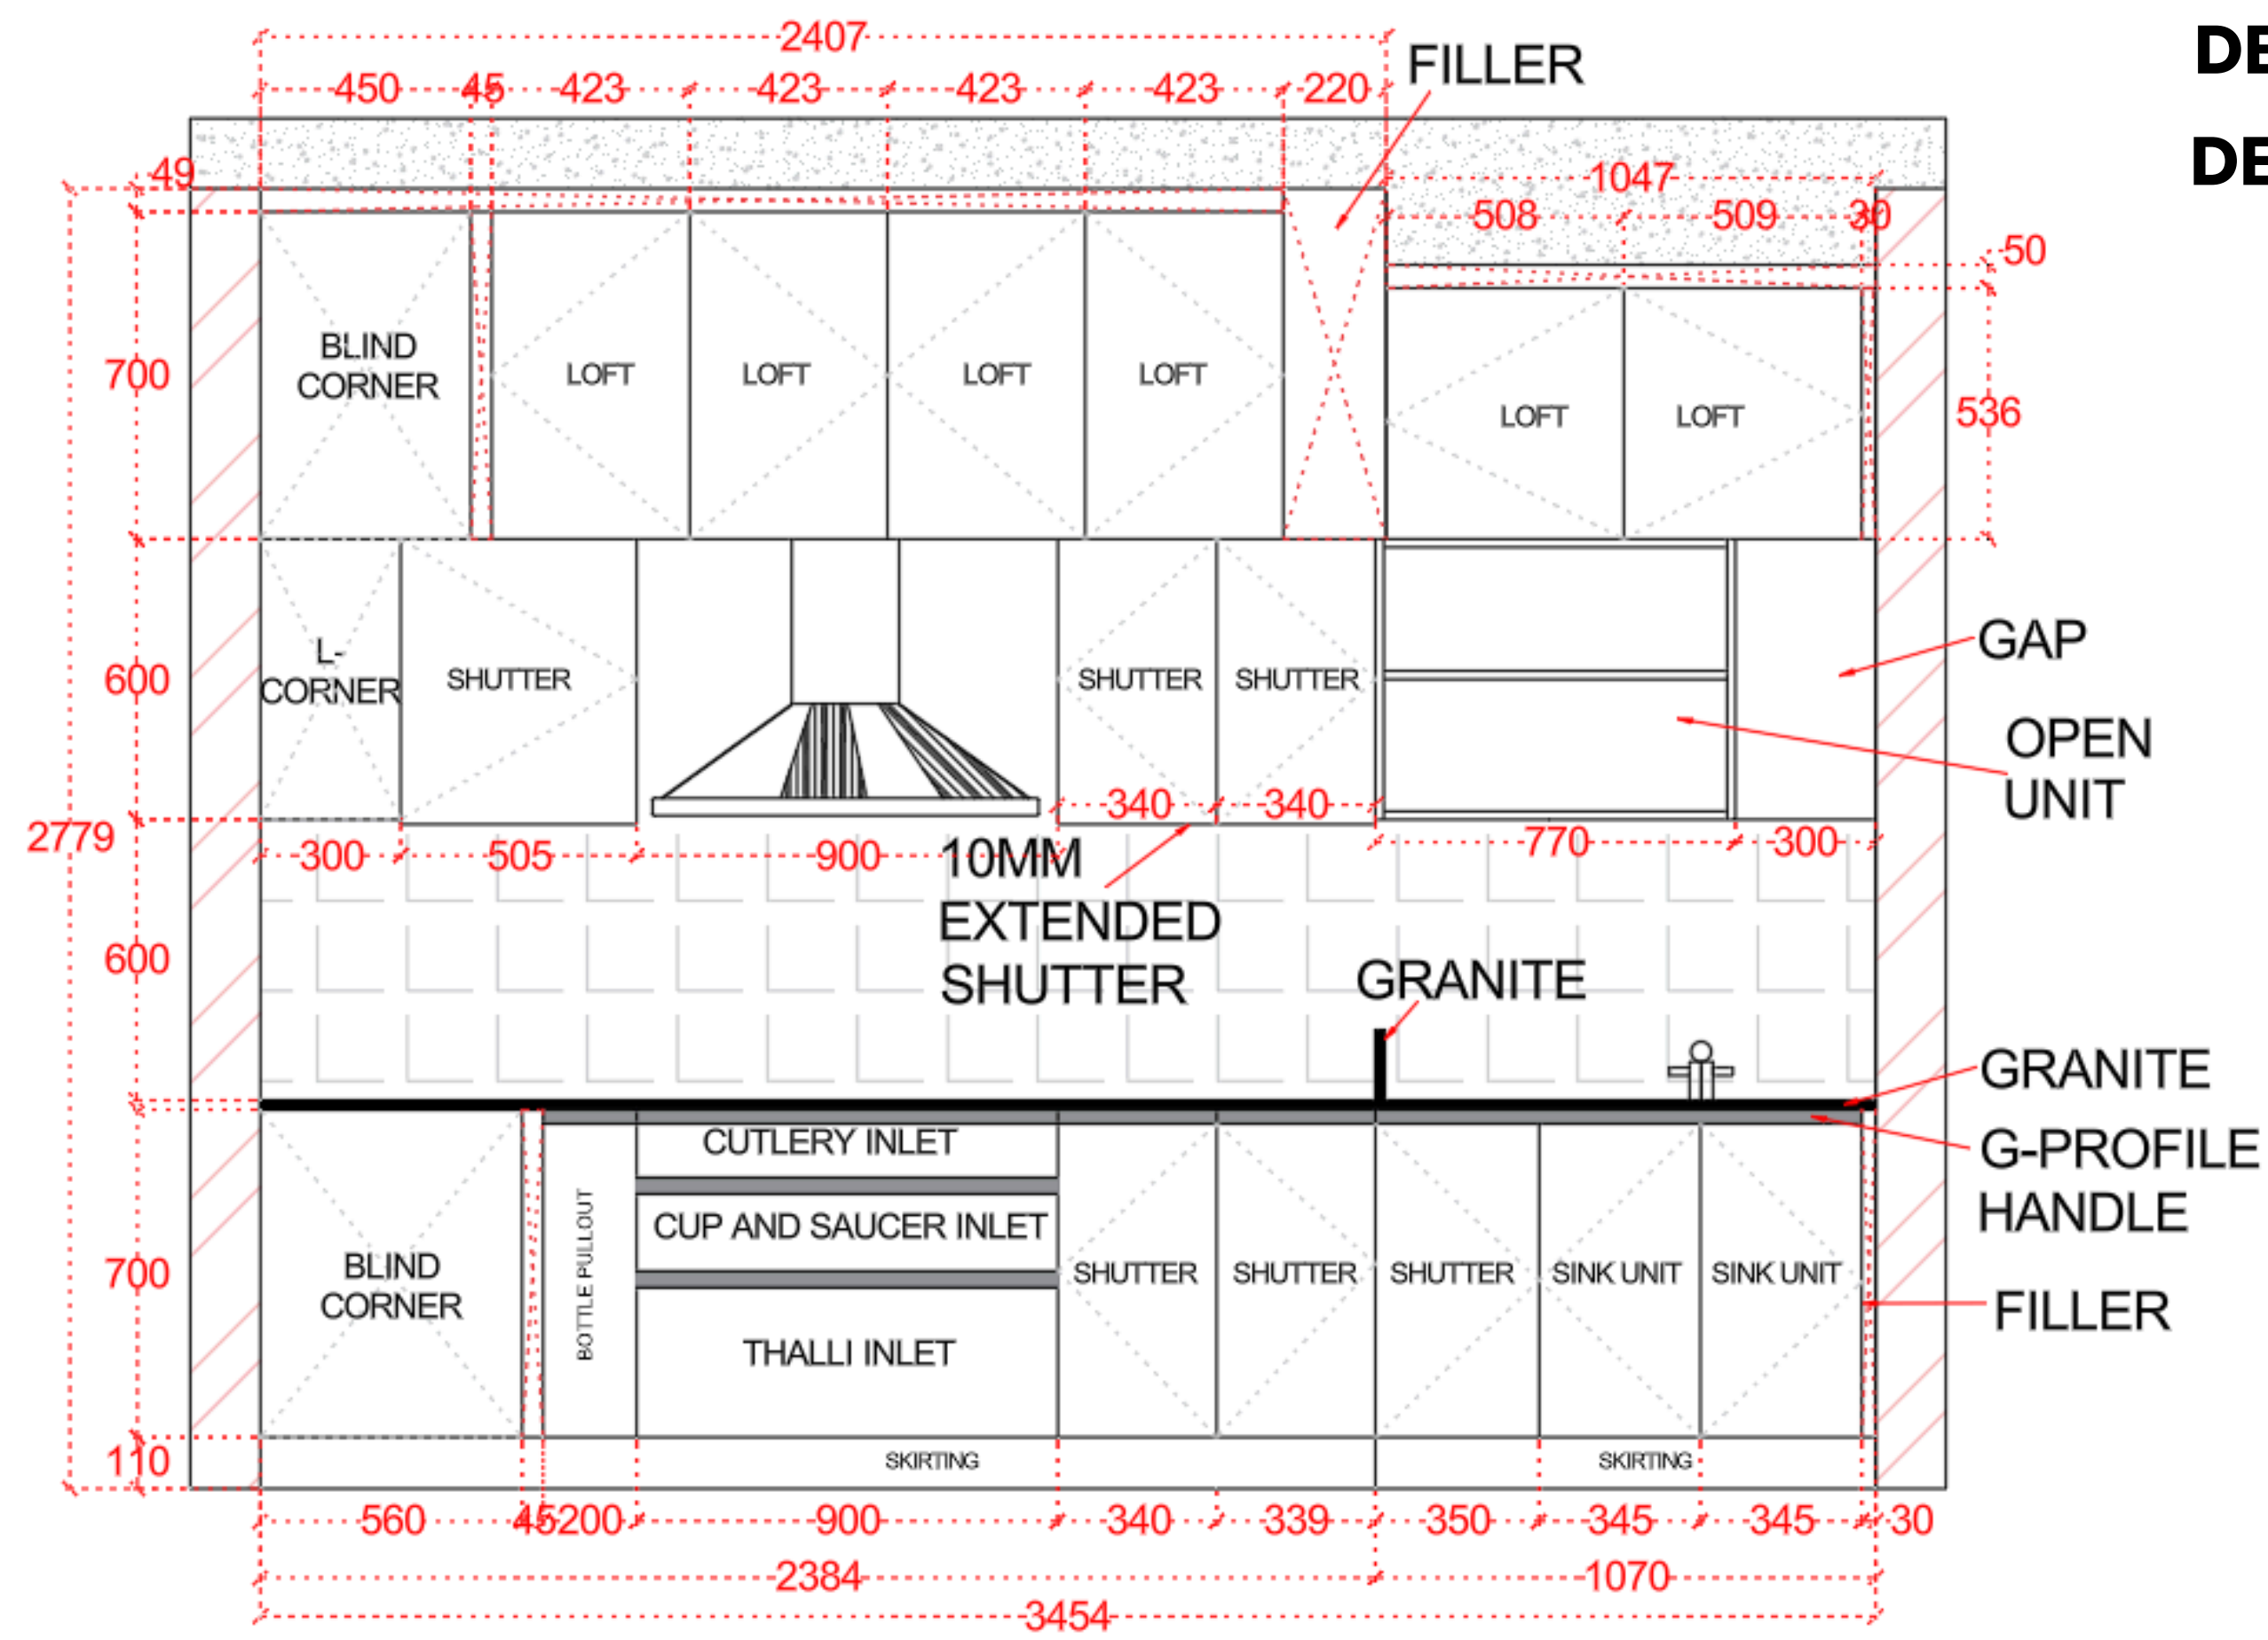


DEPTH OF BASE UNIT - 560 + 20

DEPTH OF WALL UNIT - 280 + 20

DEPTH OF LOLT- 180 + 20

KITCHEN WALL A INTERNAL

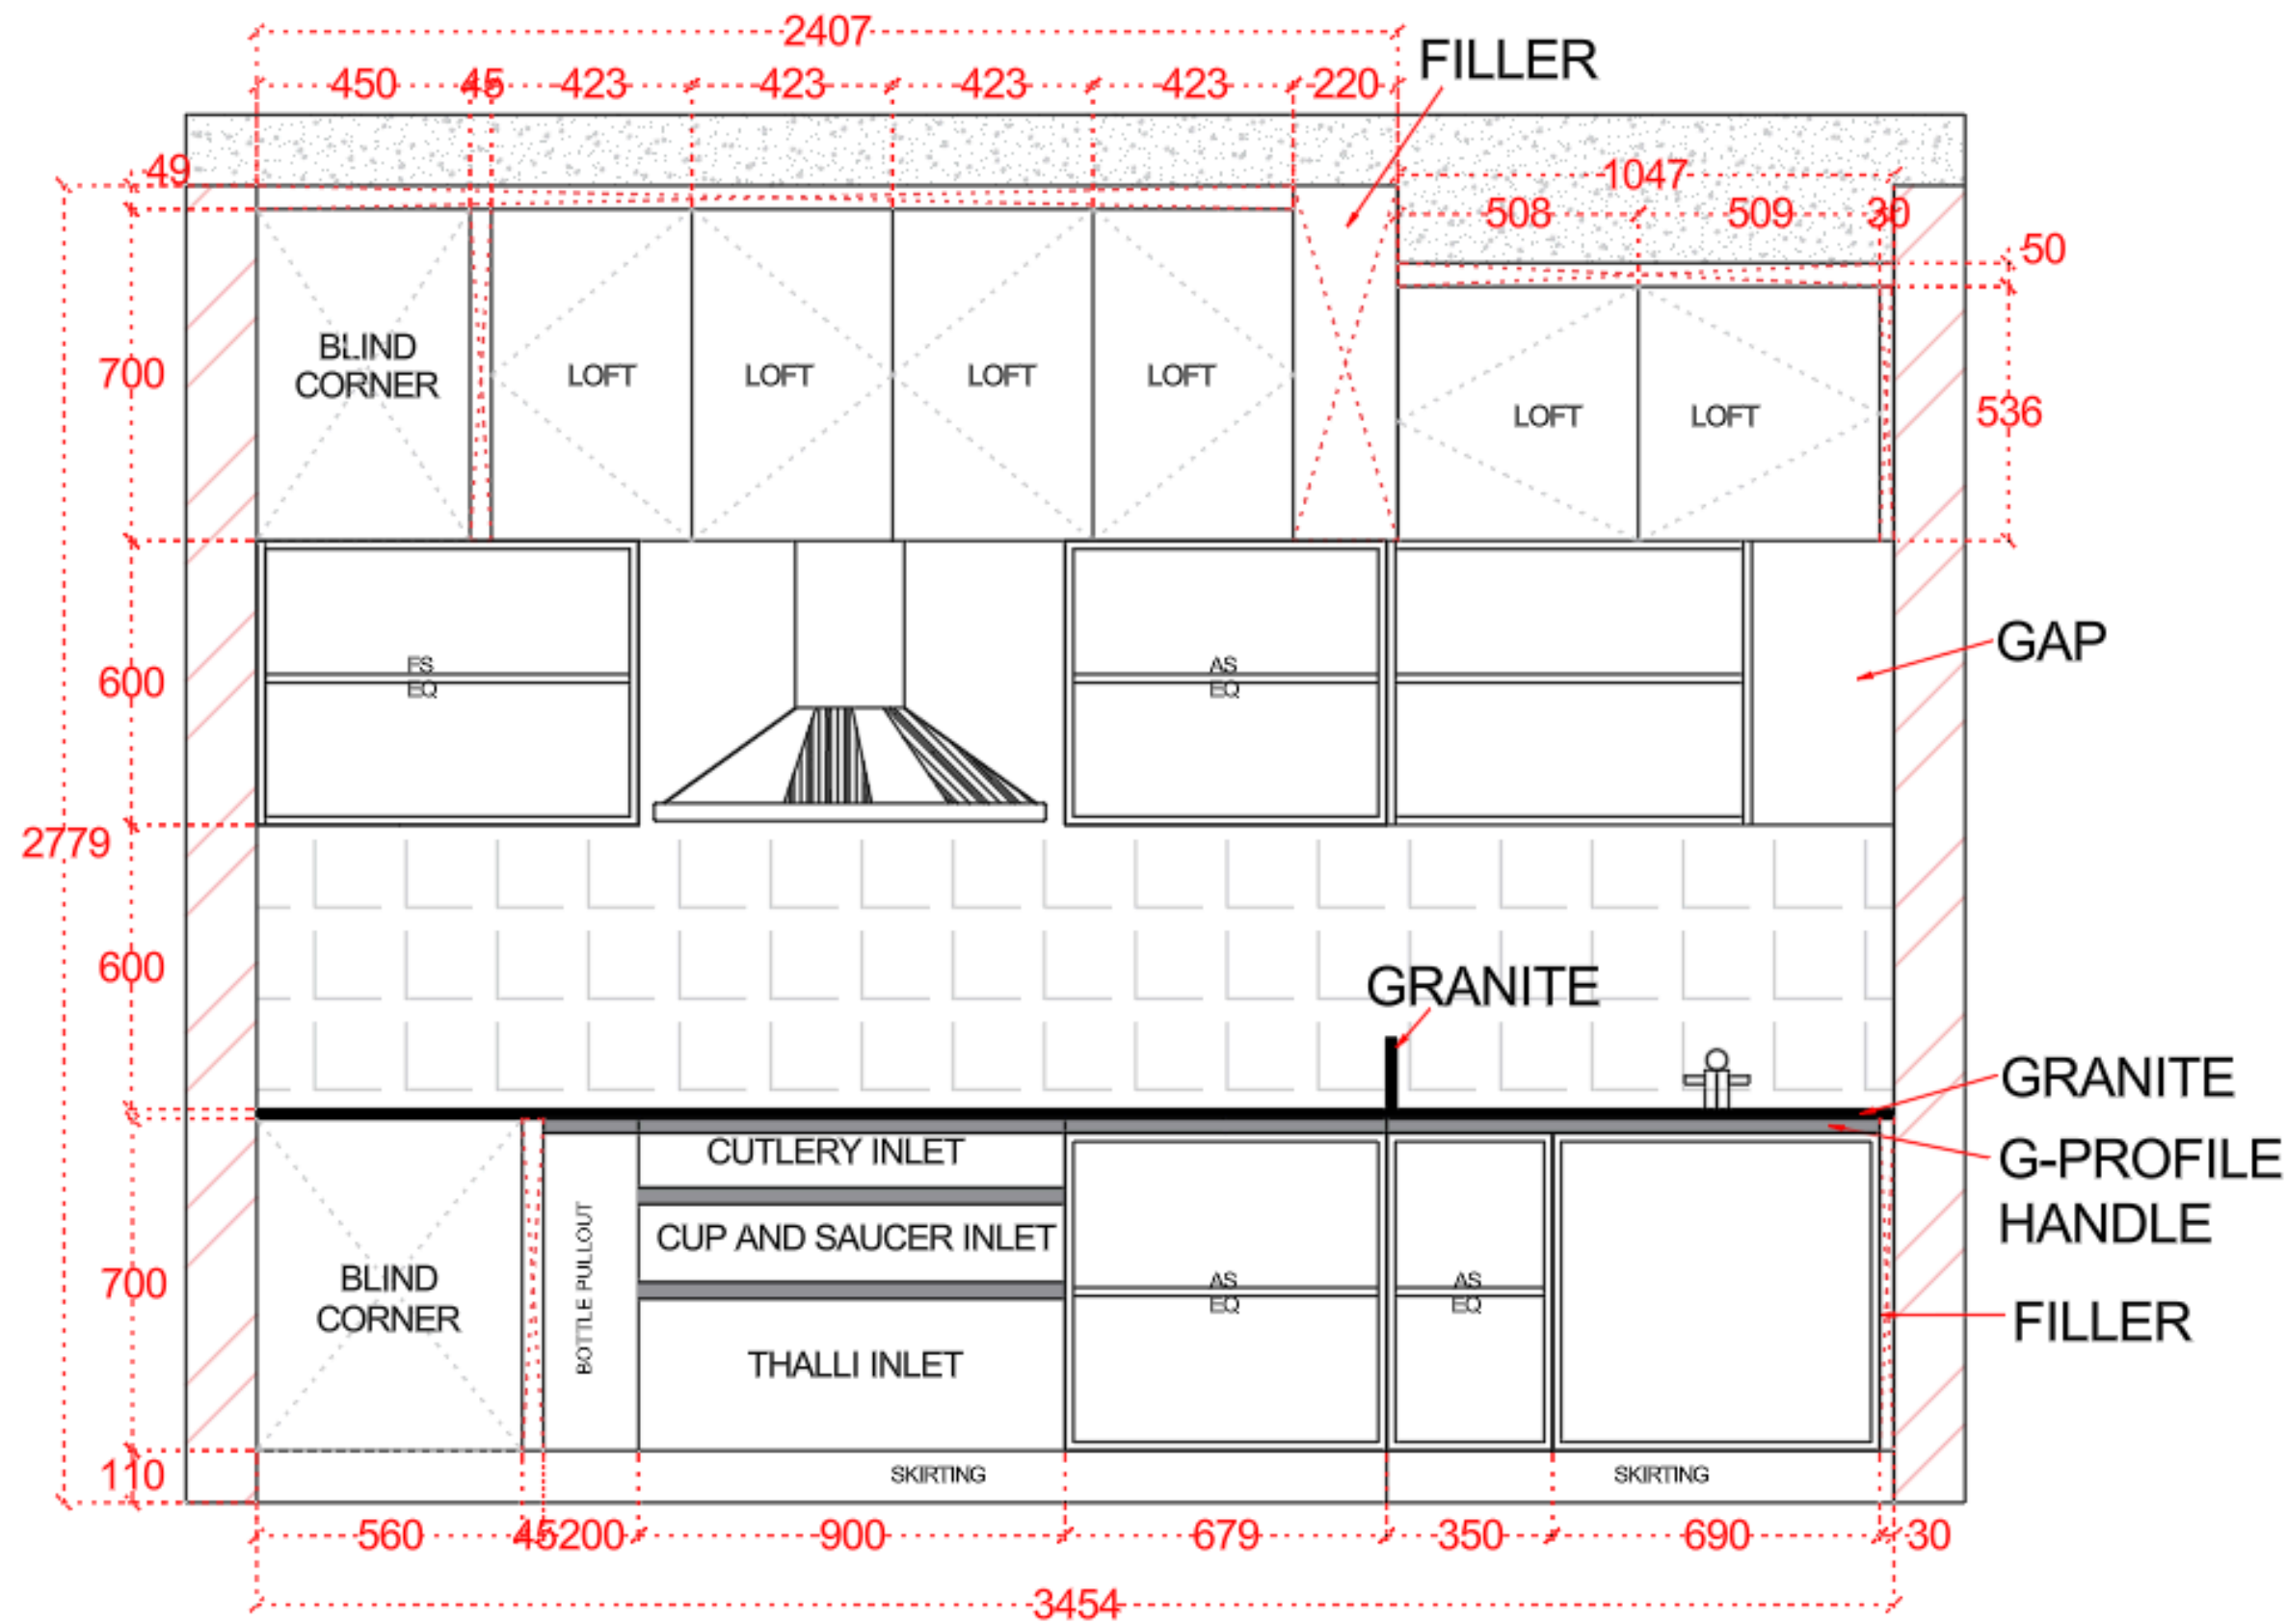


DEPTH OF BASE UNIT – 560 + 20

DEPTH OF WALL UNIT – 280 + 20

DEPTH OF LOLT– 180 + 20

KITCHEN WALL B EXTERNAL

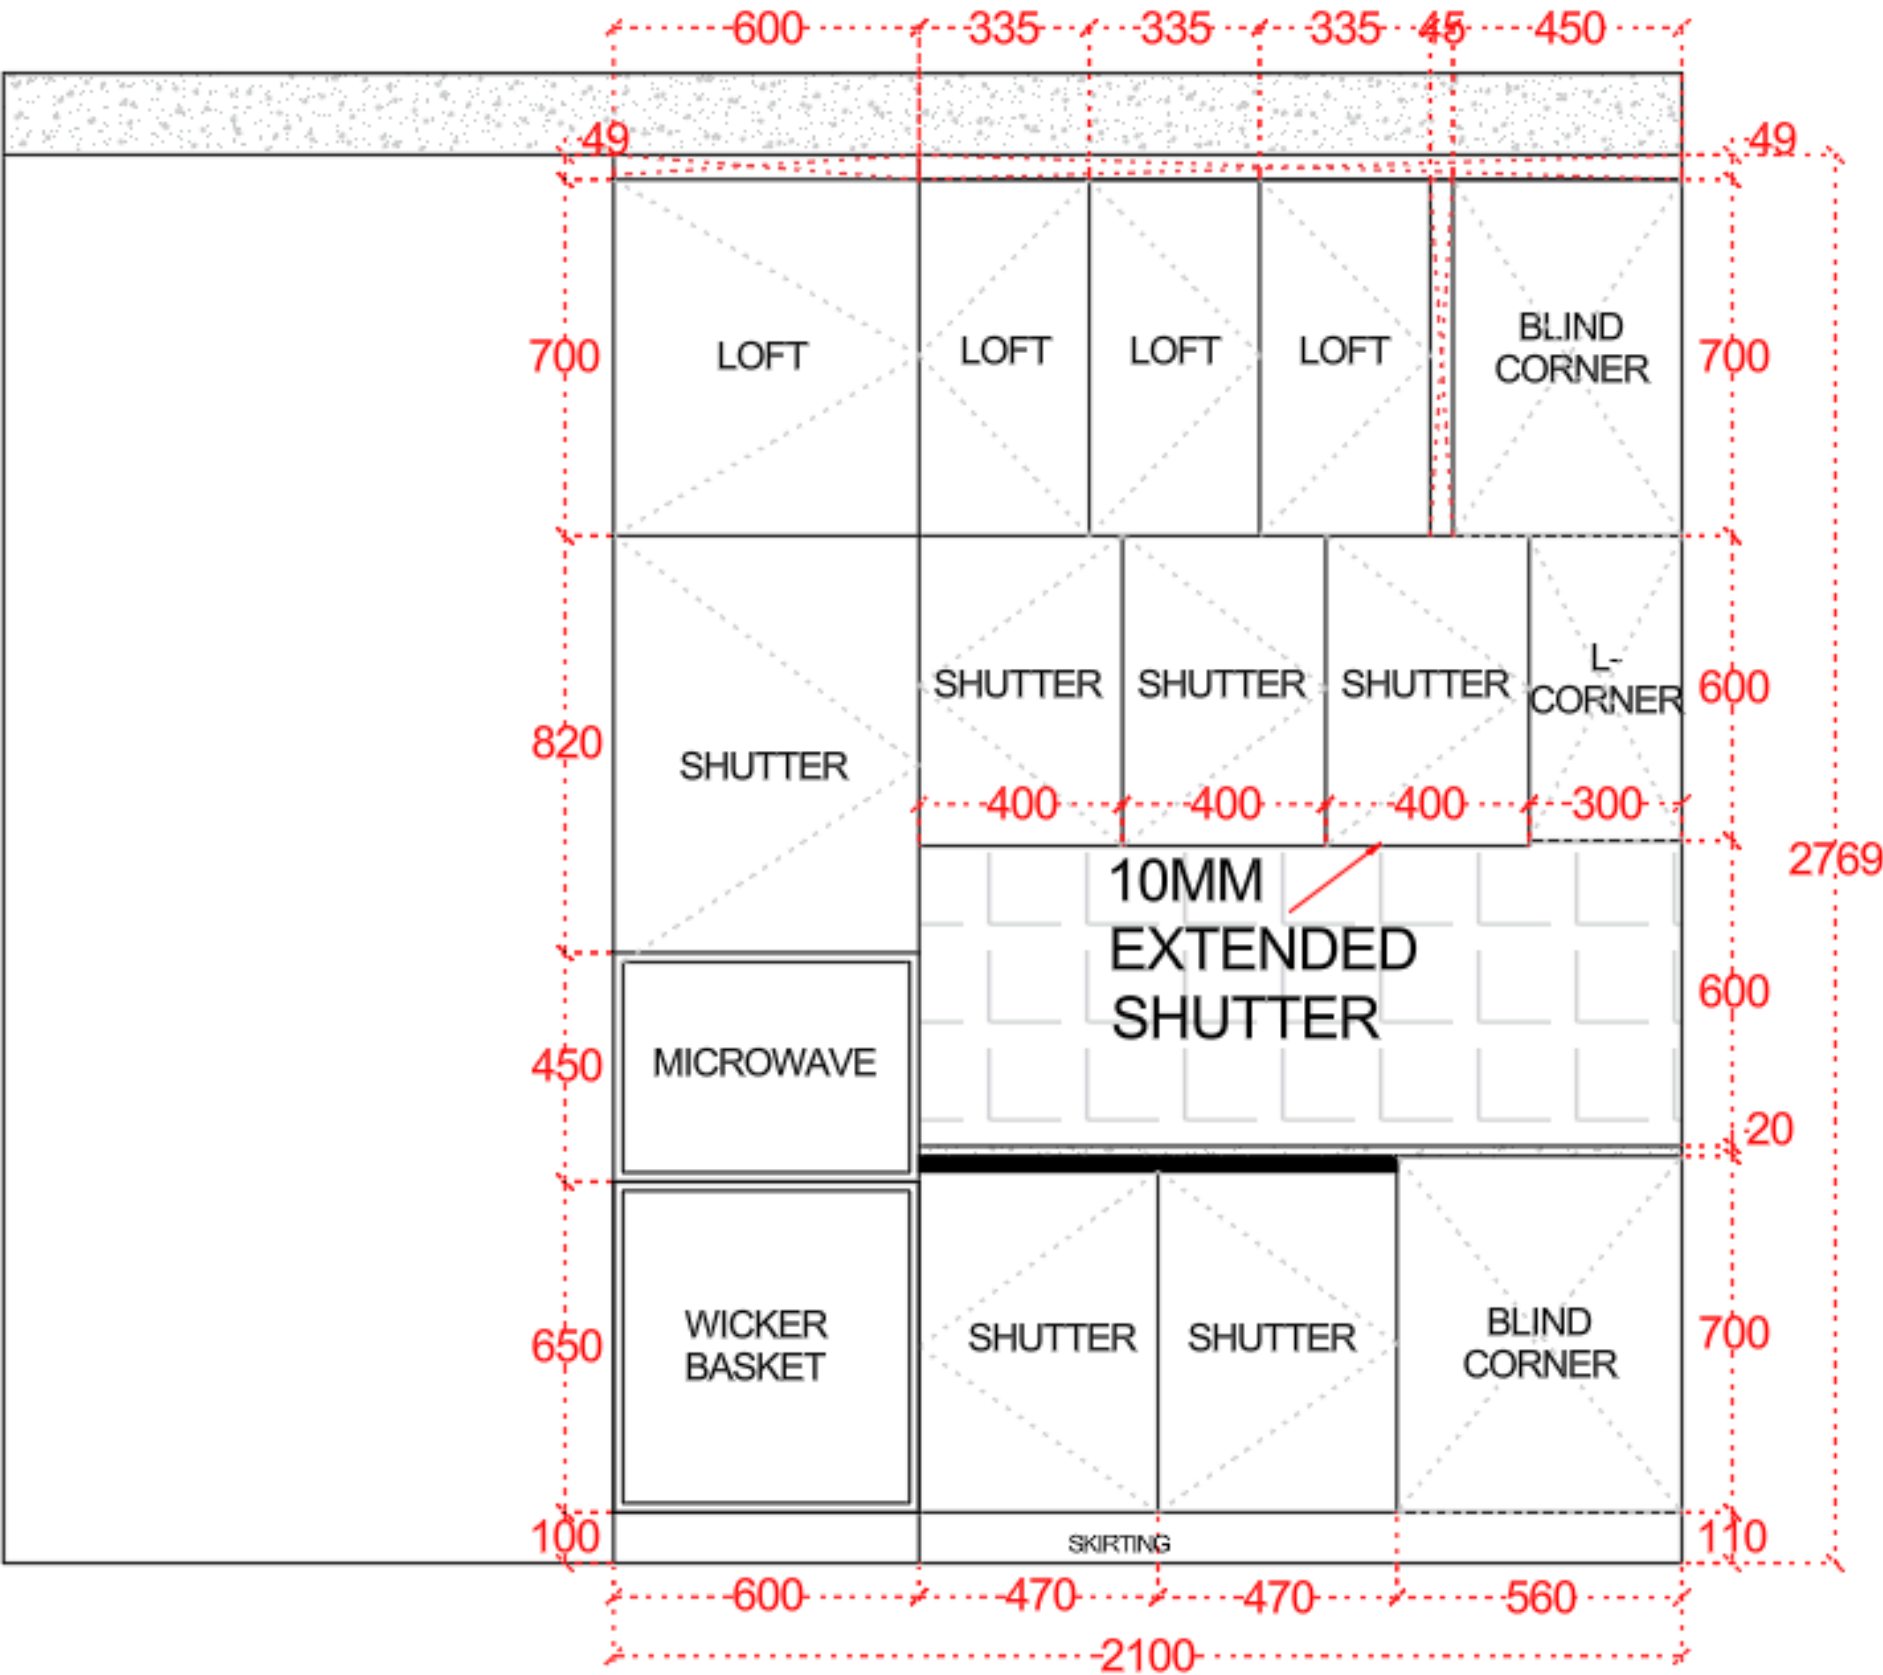

DEPTH OF BASE UNIT – 560 + 20

DEPTH OF WALL UNIT – 280 + 20


DEPTH OF LOLT– 180 + 20

KITCHEN WALL B INTERNAL

DEPTH OF BASE UNIT – 560 + 20

DEPTH OF WALL UNIT – 280 + 20

DEPTH OF LOLT– 180 + 20


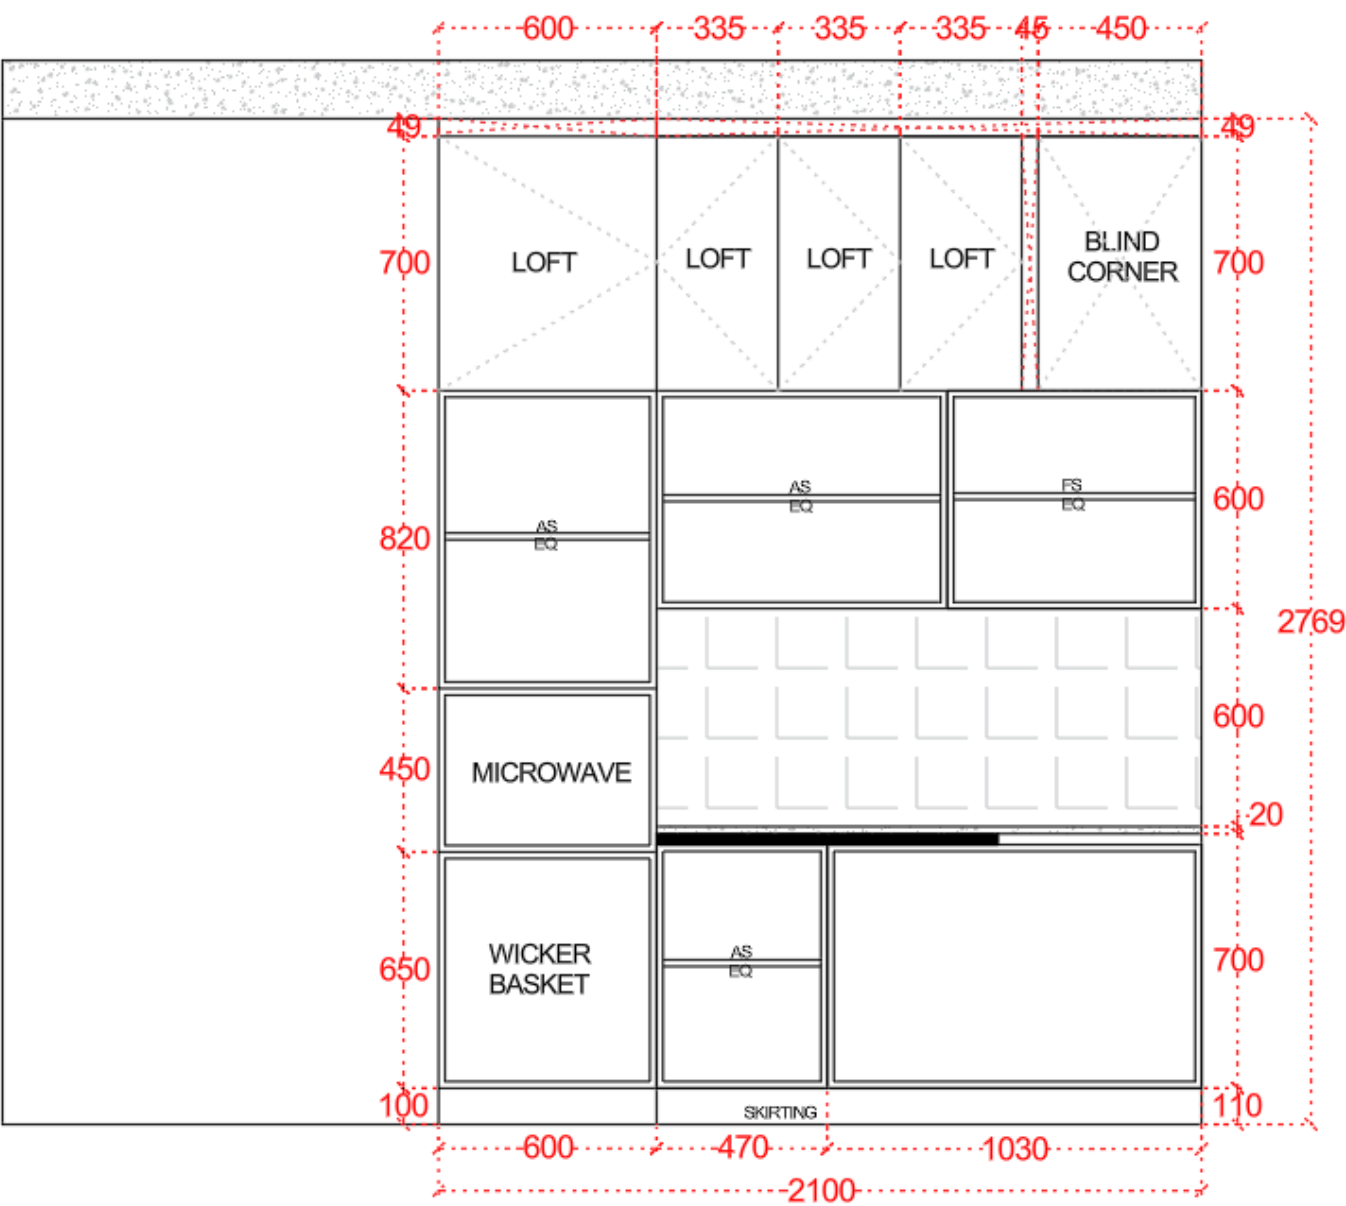


KITCHEN WALL C –EXTERNAL AND INTERNAL


DEPTH OF BASE UNIT – 560 + 20

DEPTH OF WALL UNIT – 280 + 20

DEPTH OF LOLT– 180 + 20

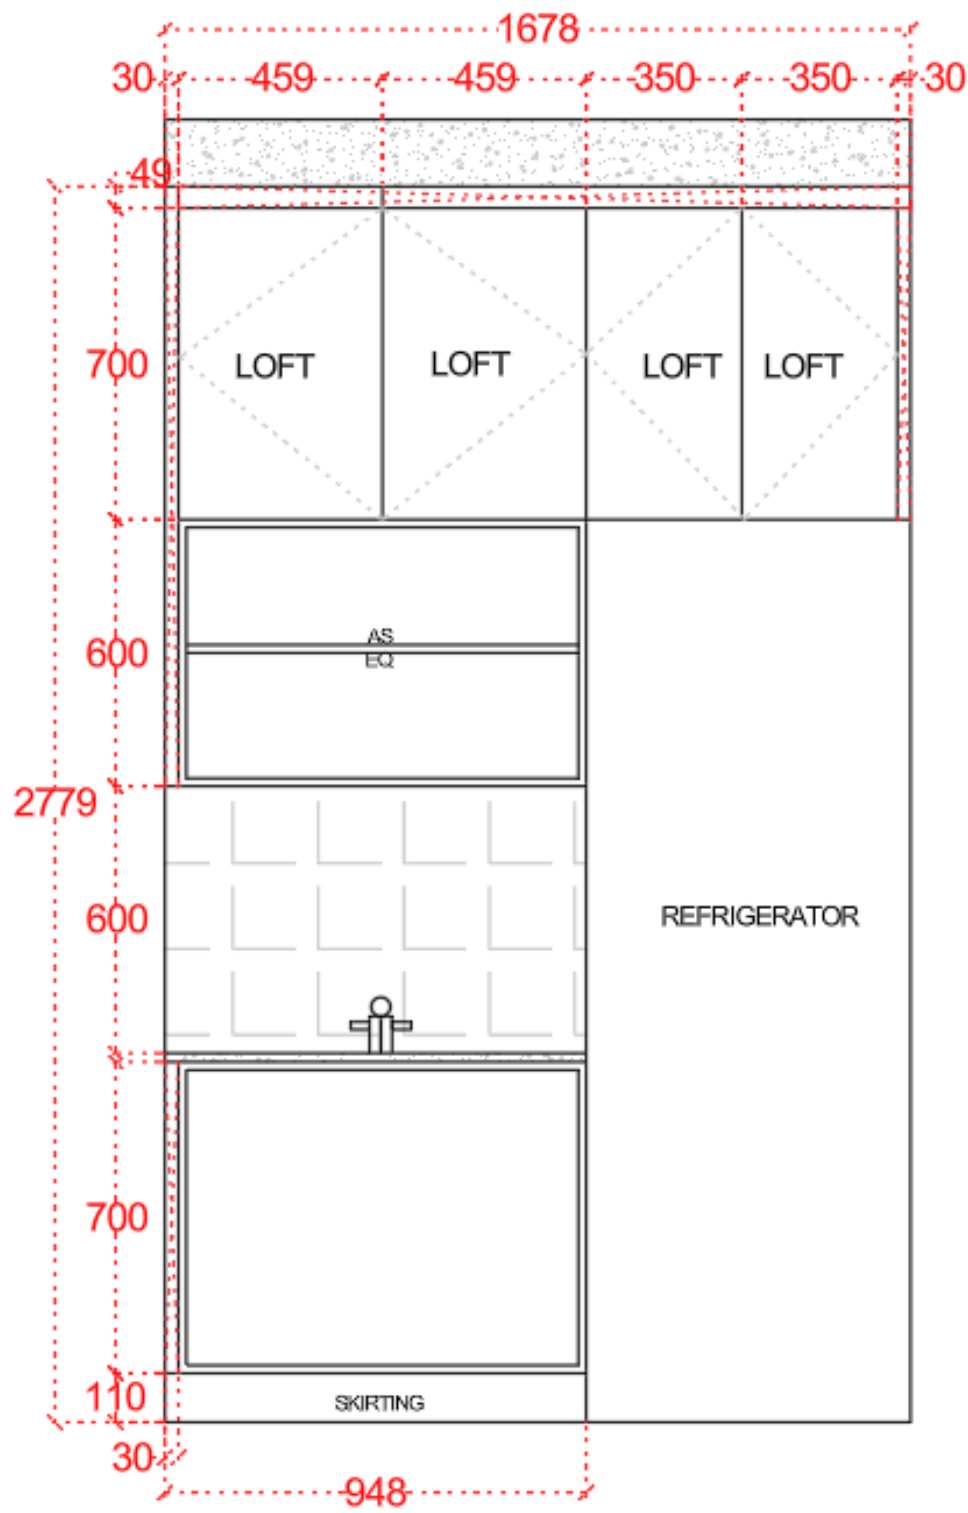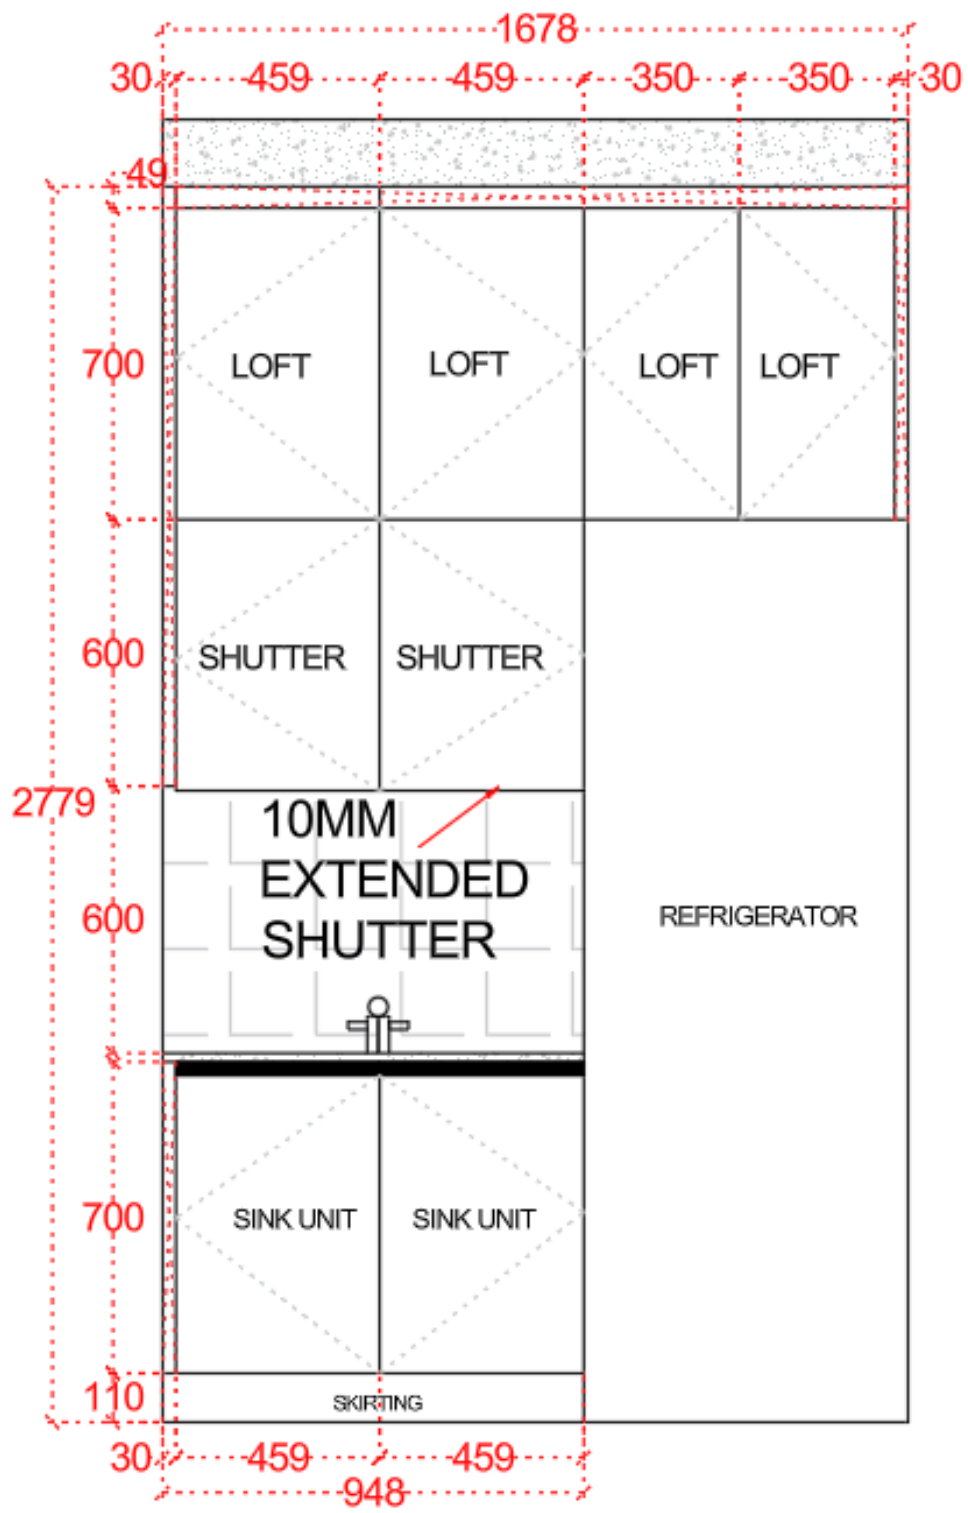

MASTER BEDROOM WARDROBE – EXTERNAL

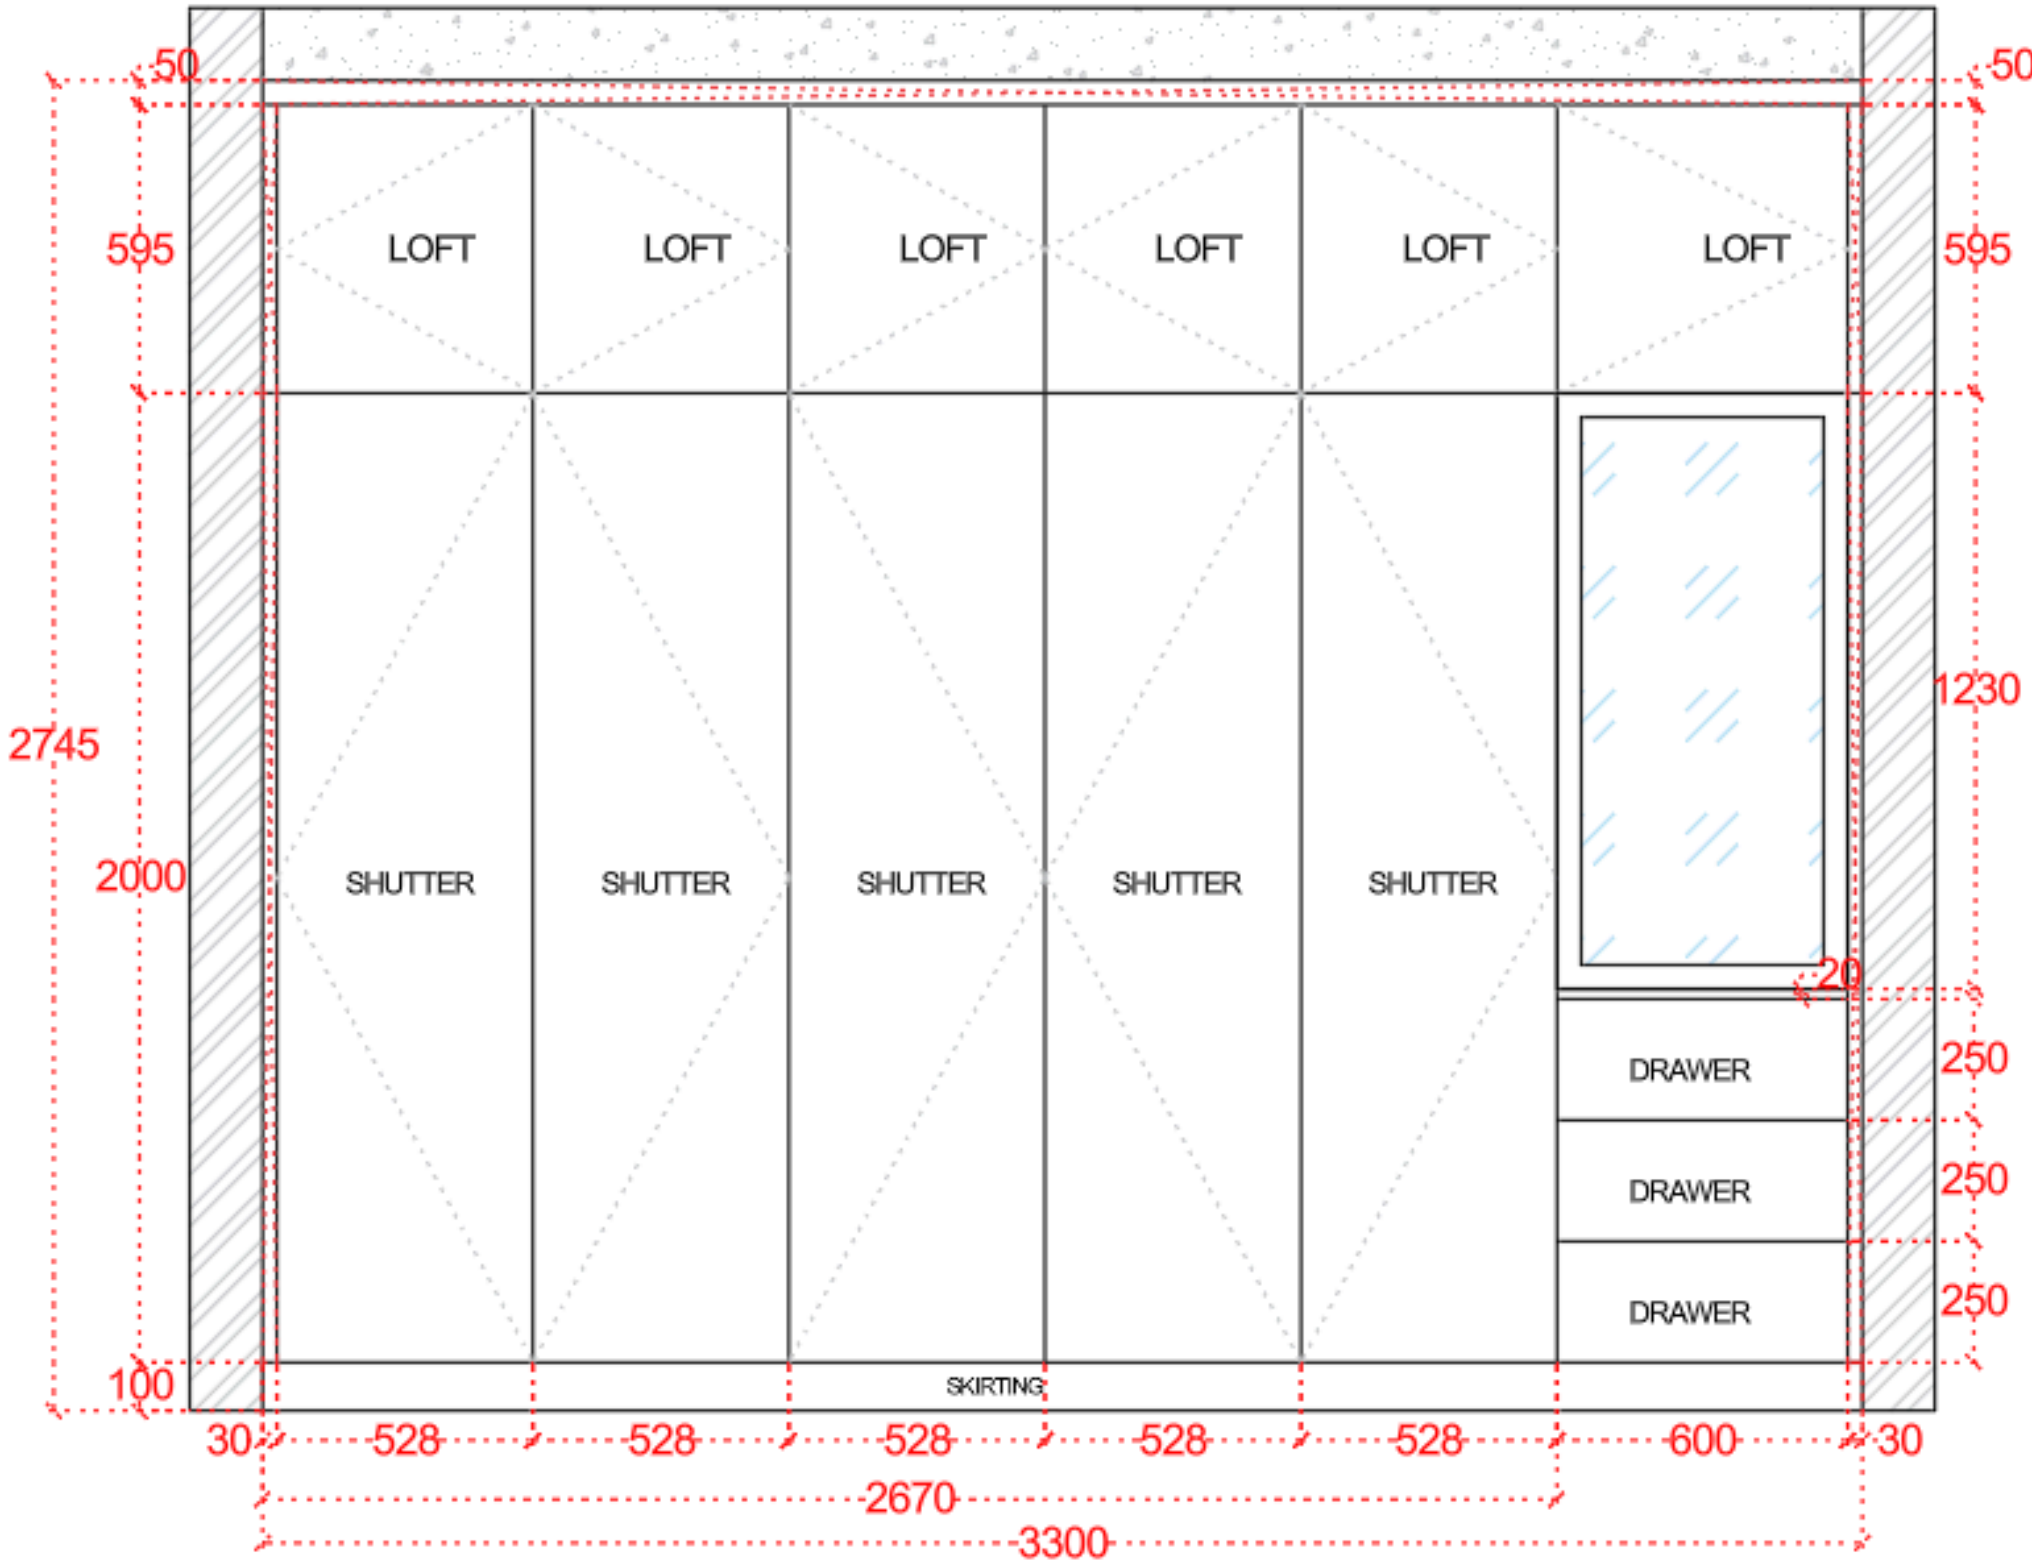


DEPTH OF BASE UNIT – 560 + 20

DEPTH OF WALL UNIT – 280 + 20

DEPTH OF LOLT– 180 + 20

MASTER BEDROOM WARDROBE – INTERNAL

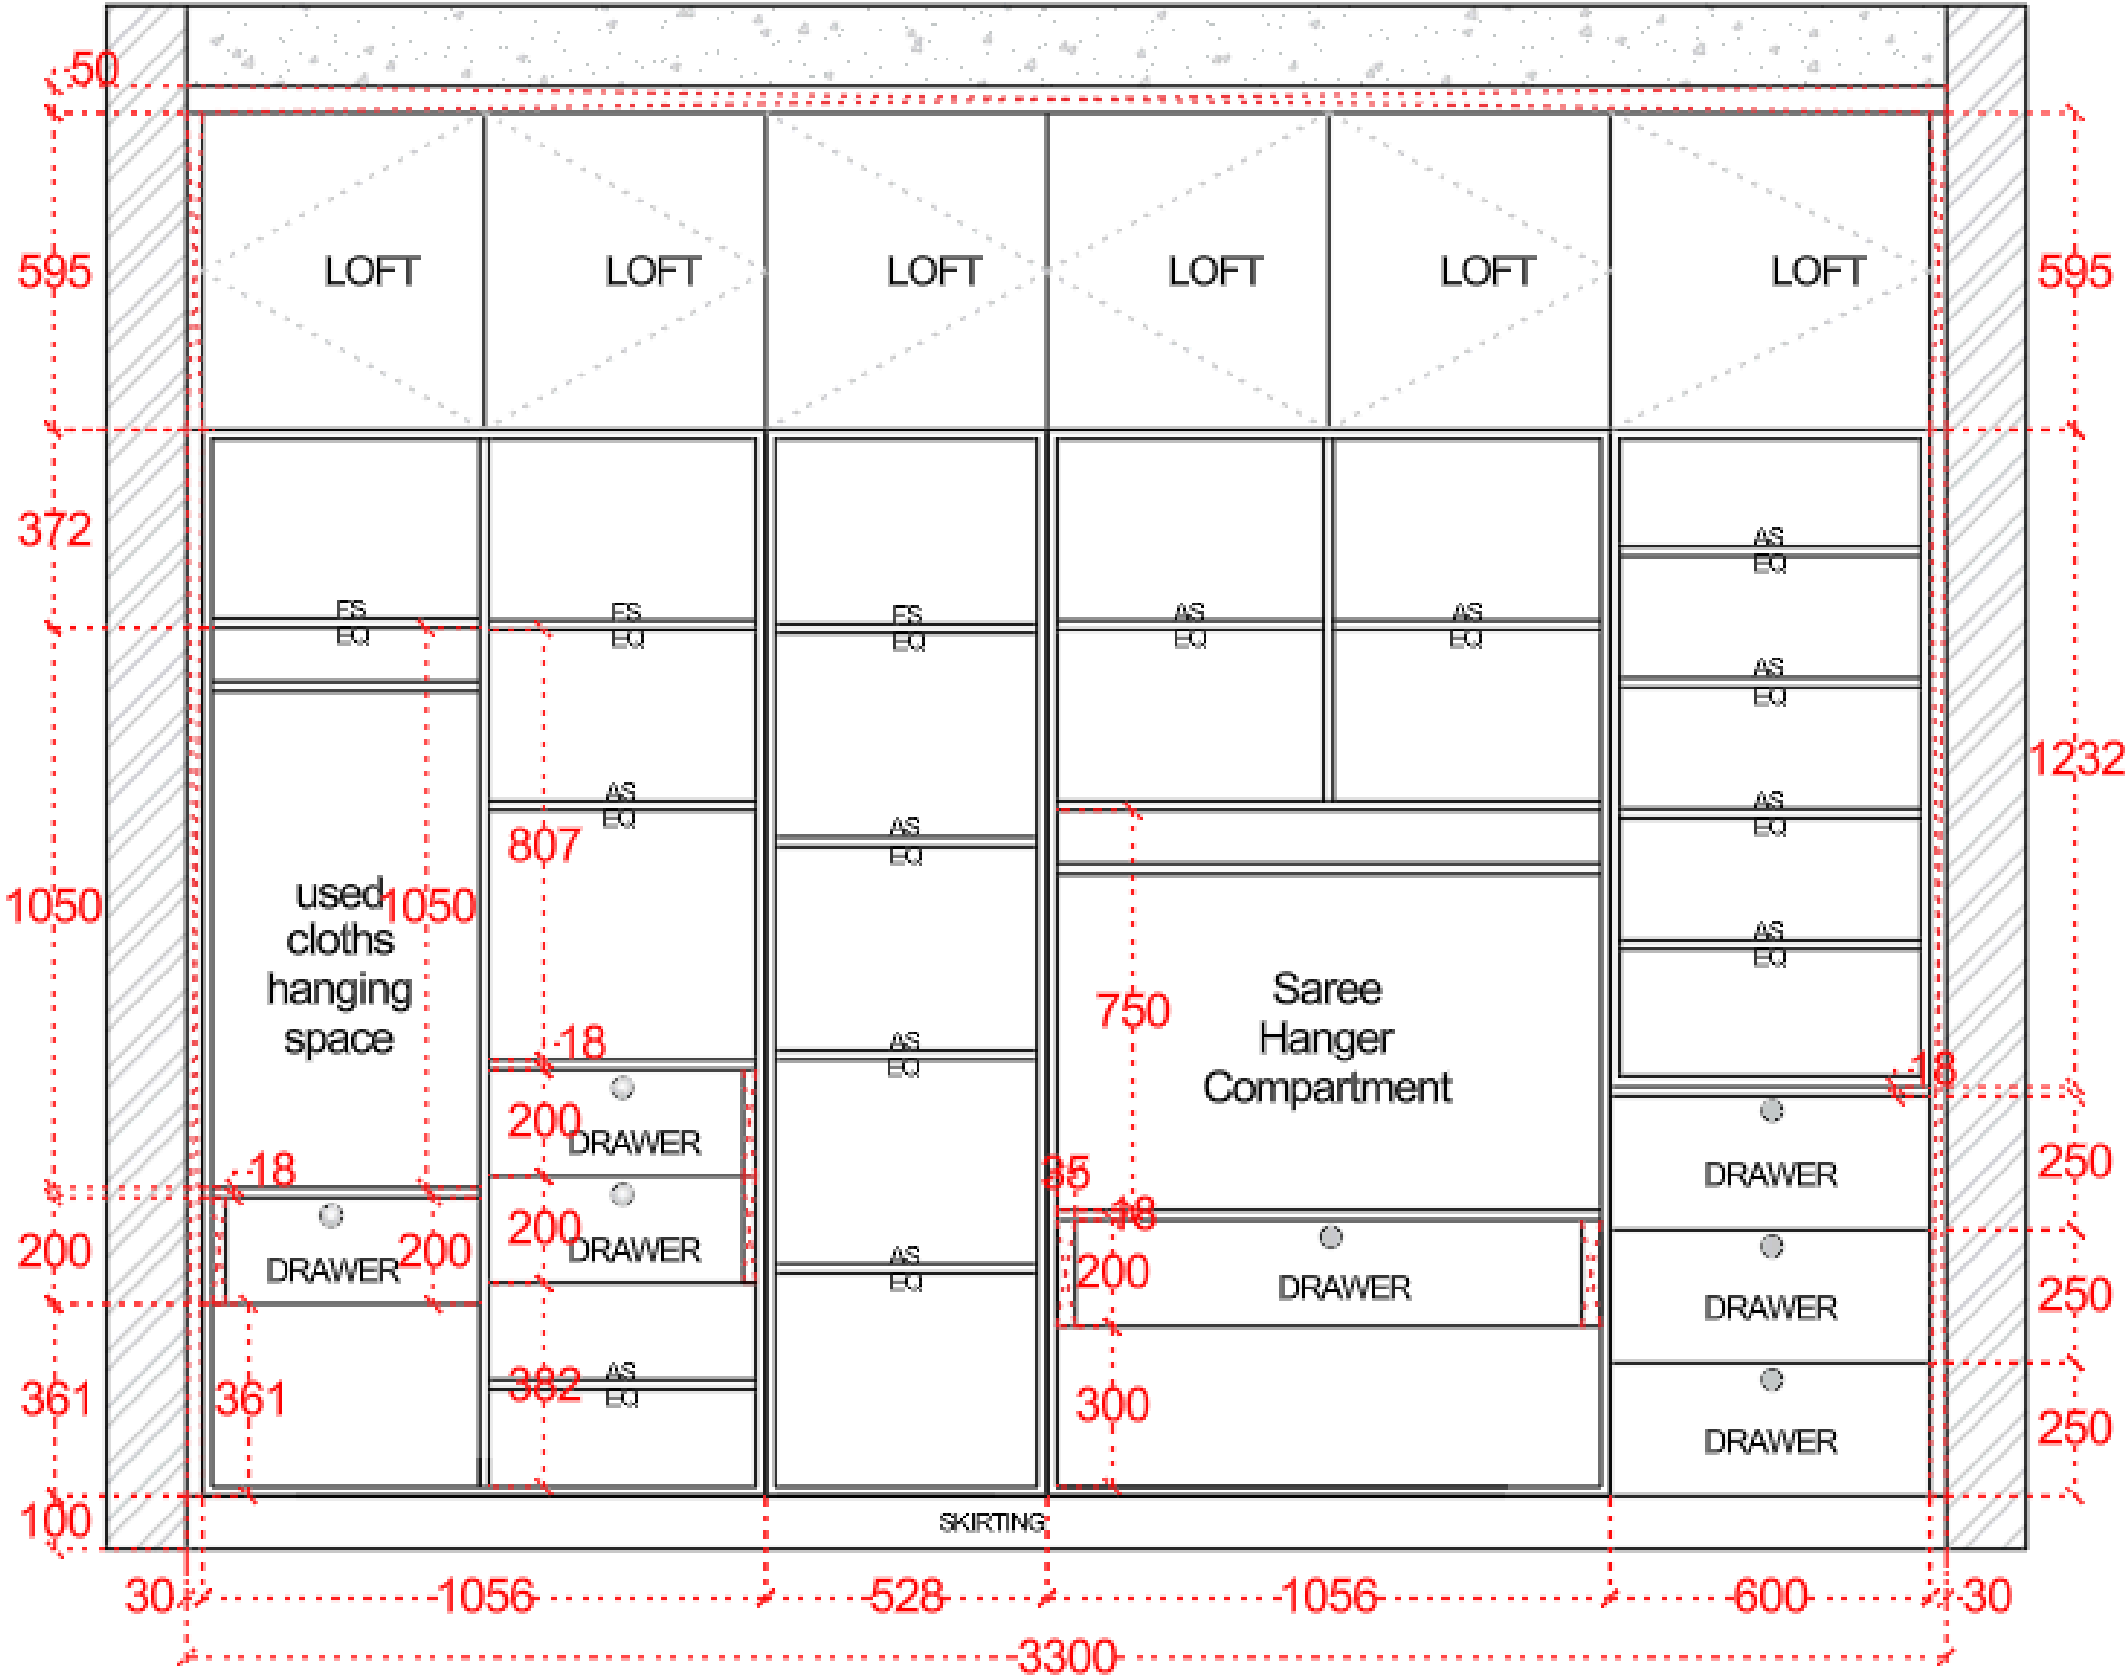

DEPTH OF BASE UNIT – 560 + 20



DEPTH OF WALL UNIT – 280 + 20

DEPTH OF LOLT– 180 + 20

MASTER BEDROOM – fLOATING UNIT AND SIDE TABLE



DEPTH OF STUDY UNIT – 430 + 20

DEPTH OF SIDE TABLE – 430 + 20

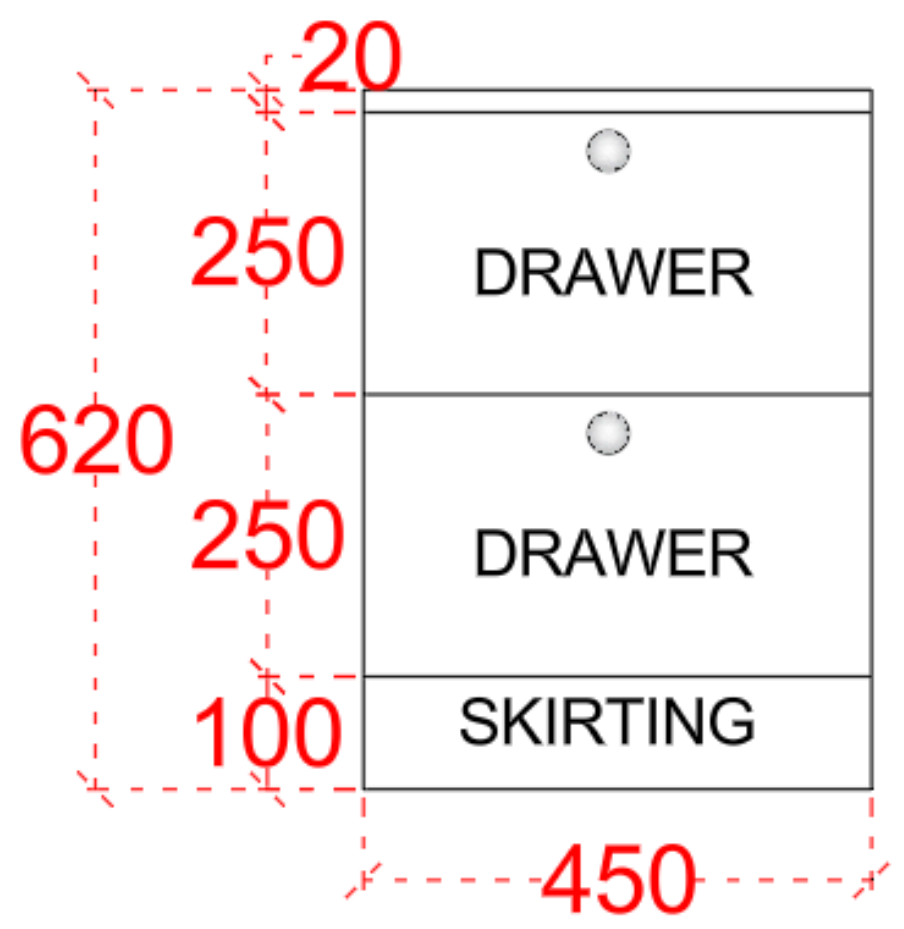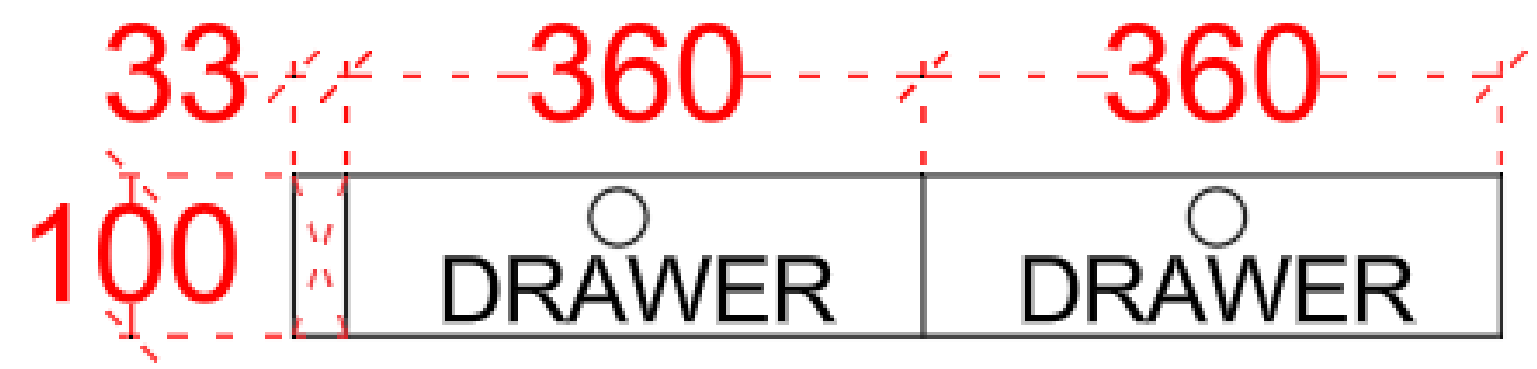

MASTER BEDROOM – VANITY

DEPTH OF UNIT – 110 + 20

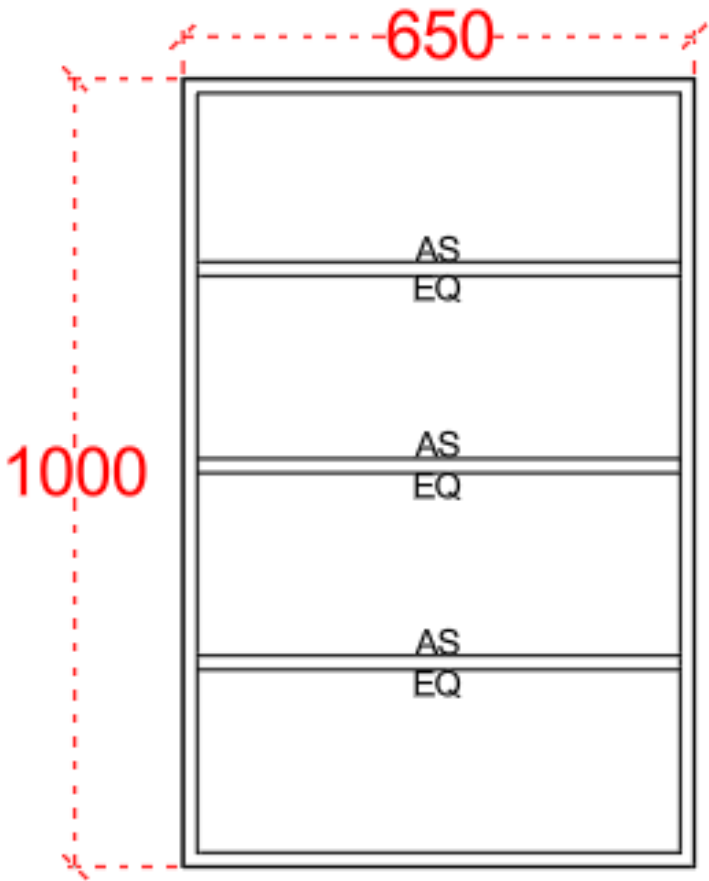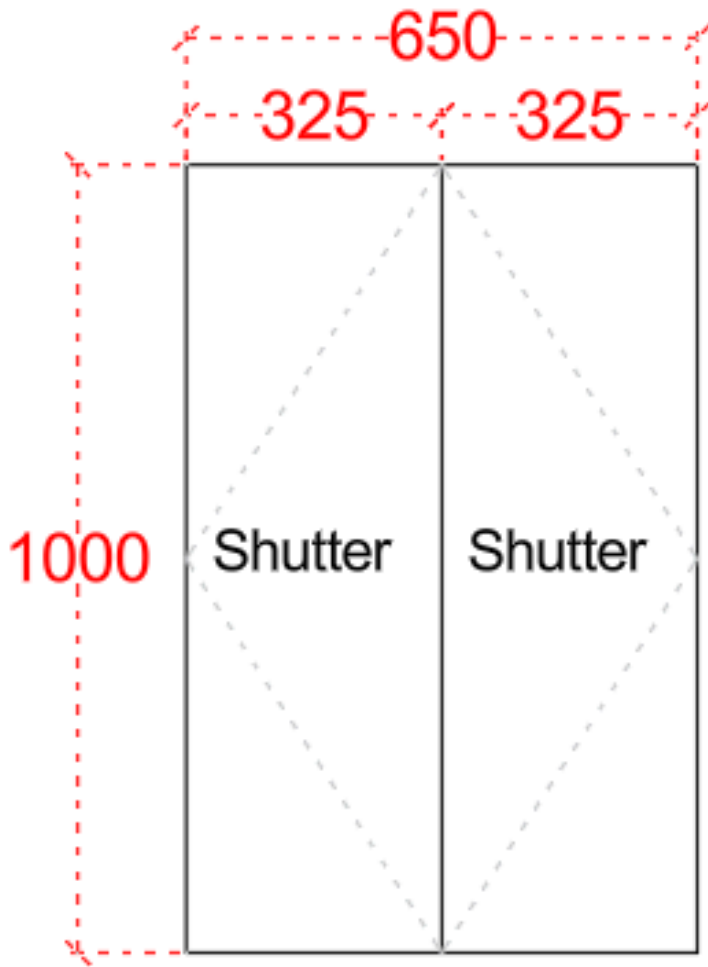


KIDS BEDROOM WARDROBE EXTERNAL

DEPTH OF STORAGE BEHIND MIRROR- 180 + 20


DEPTH OF DRAWERS - 400 + 20

DEPTH OF WARDROBE - 560 + 20

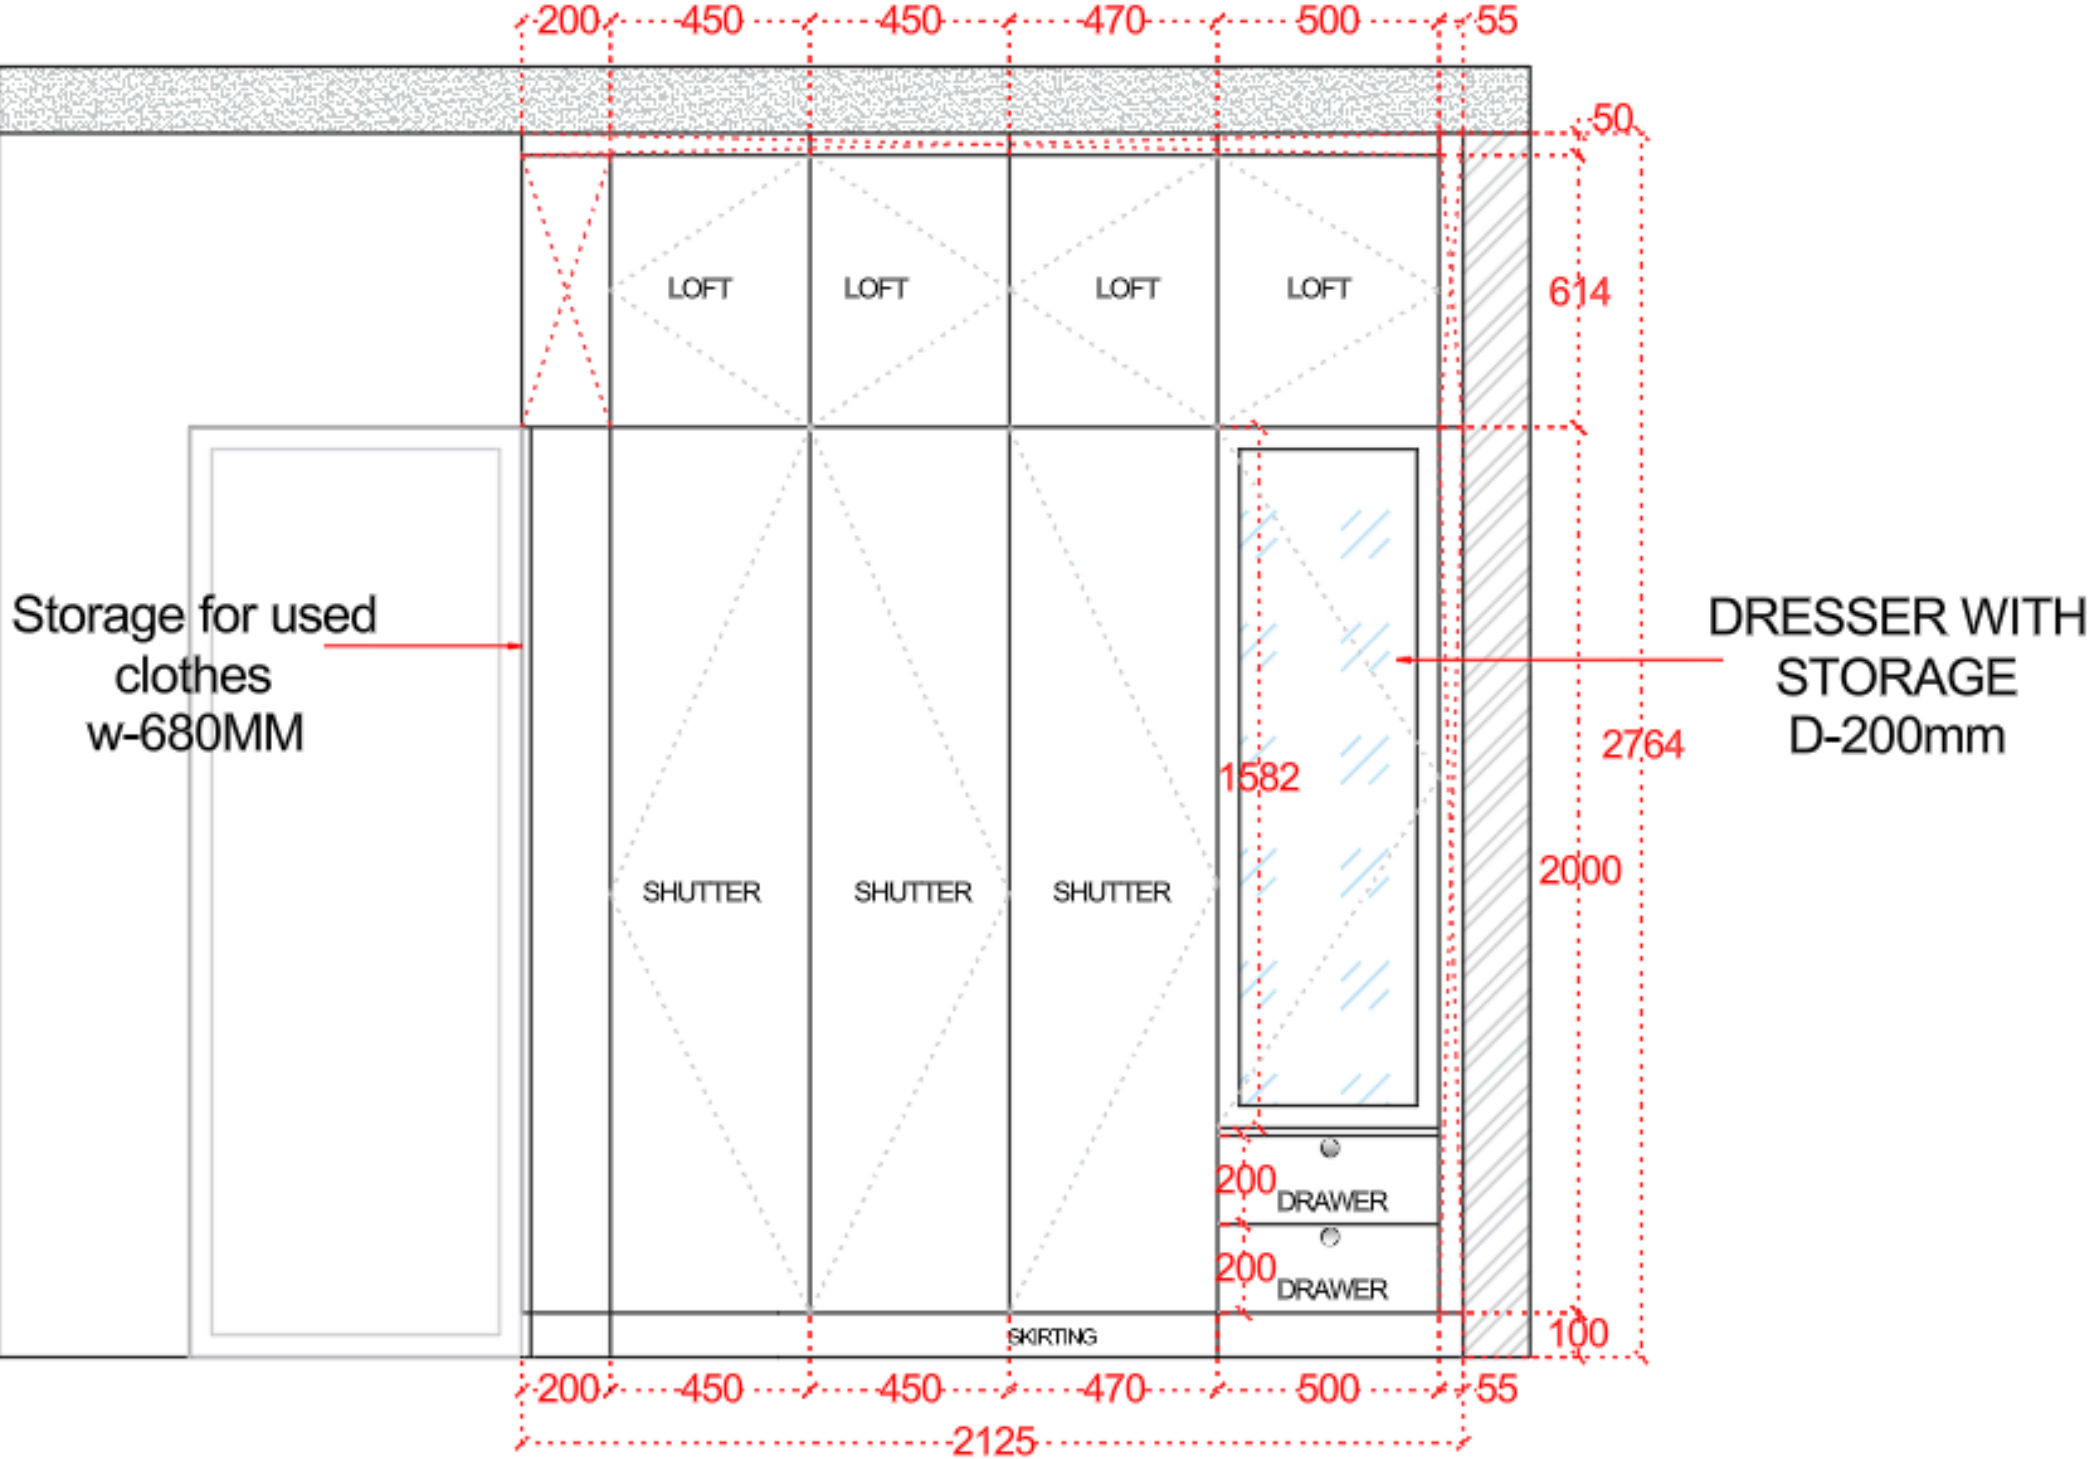


KIDS BEDROOM WARDROBE INTERNAL

DEPTH OF - 560 + 20

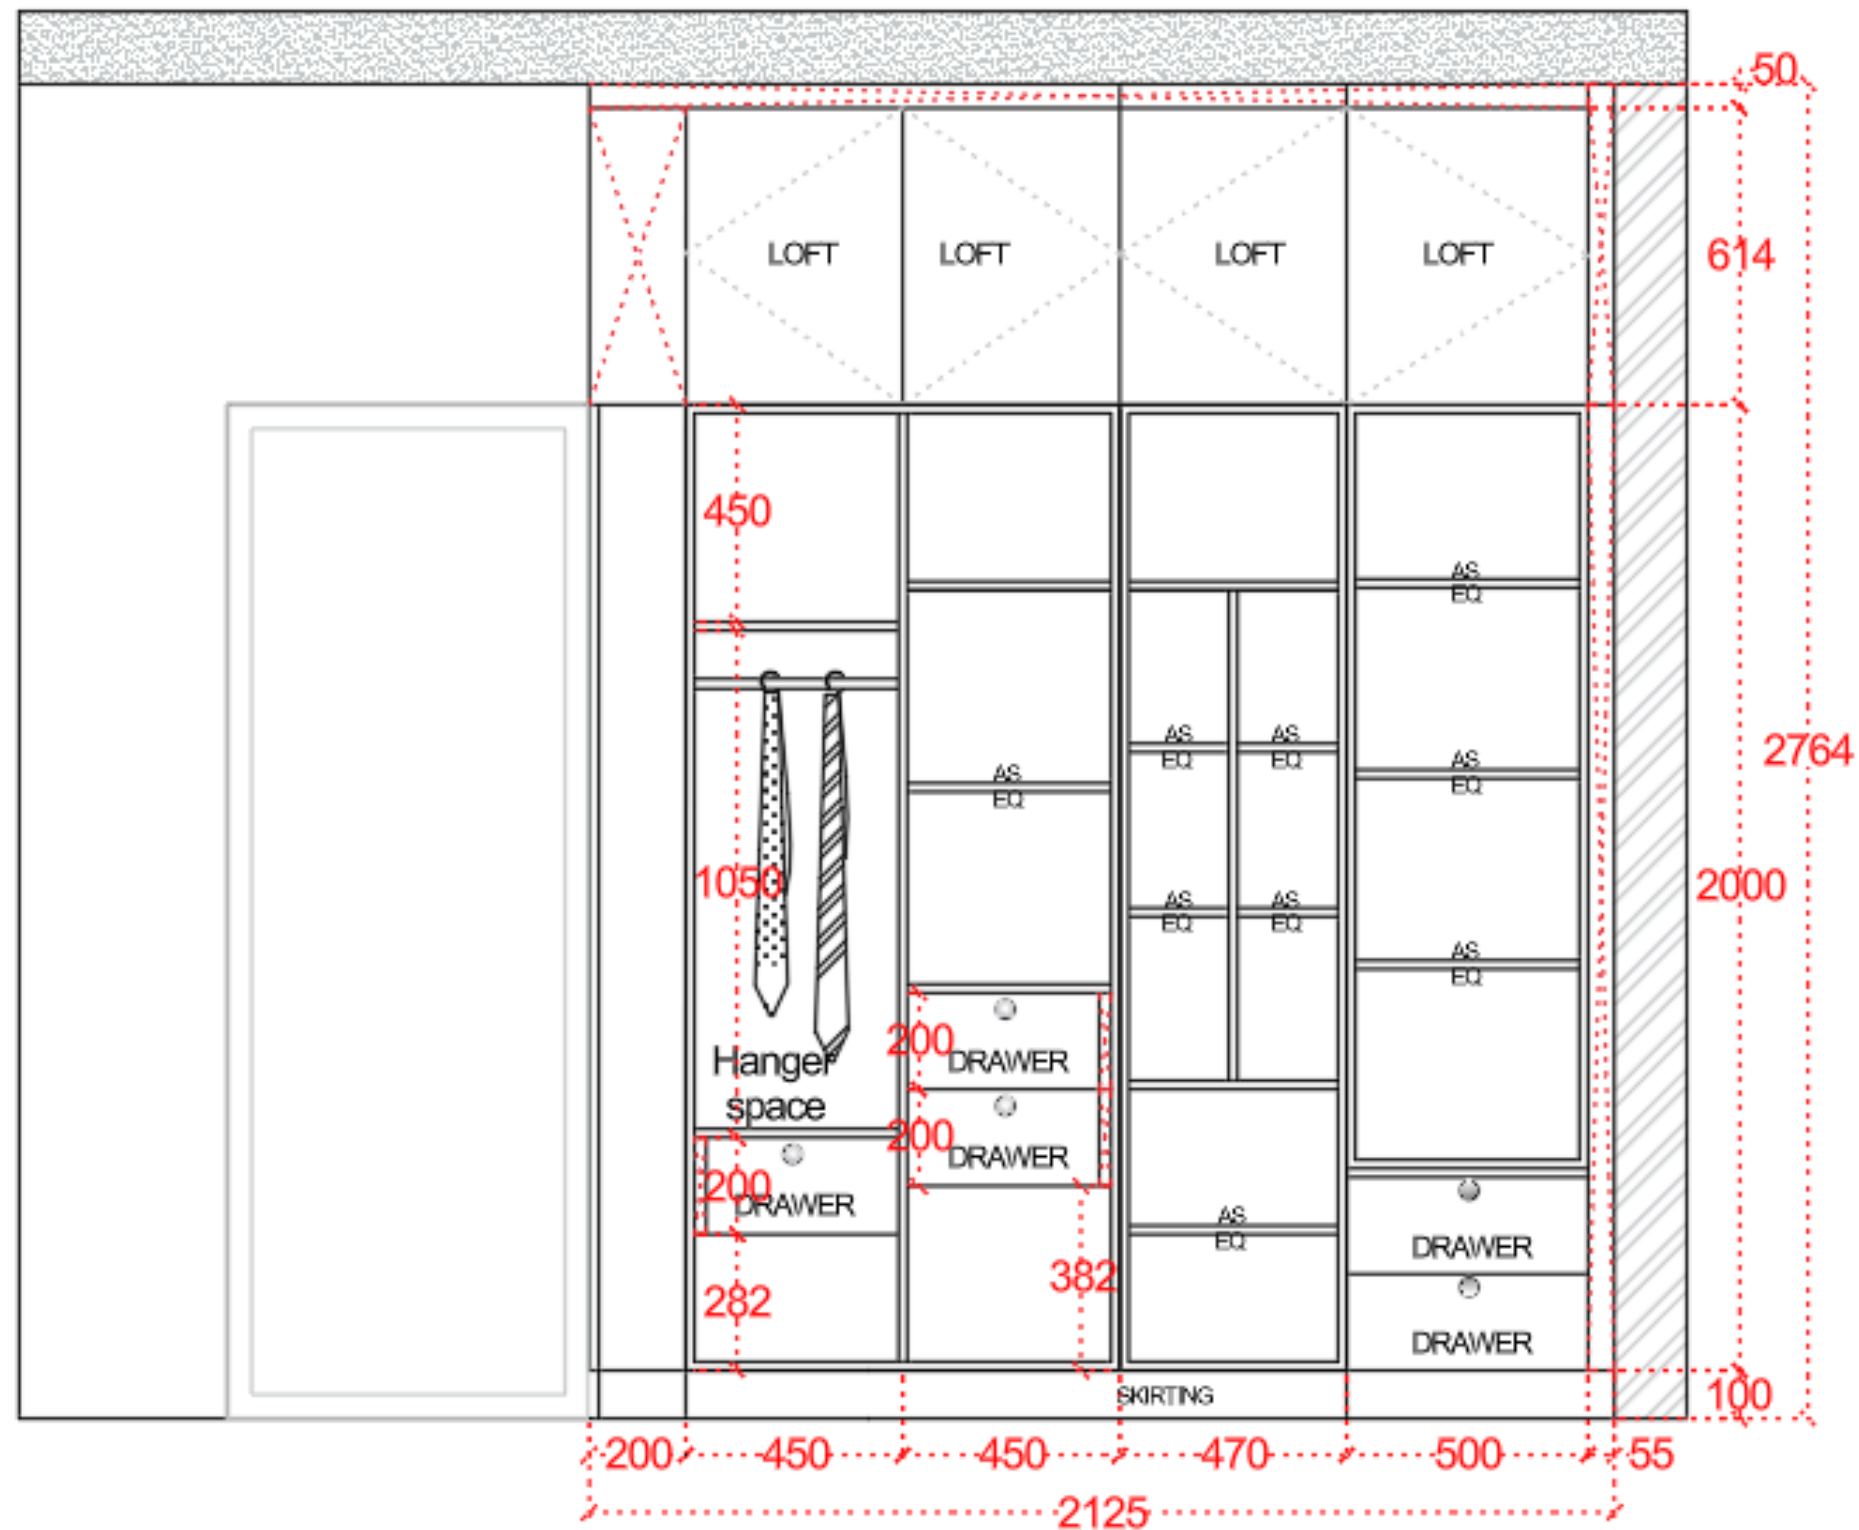

KIDS BEDROOM WARDROBE USED CLOTHES STORAGE


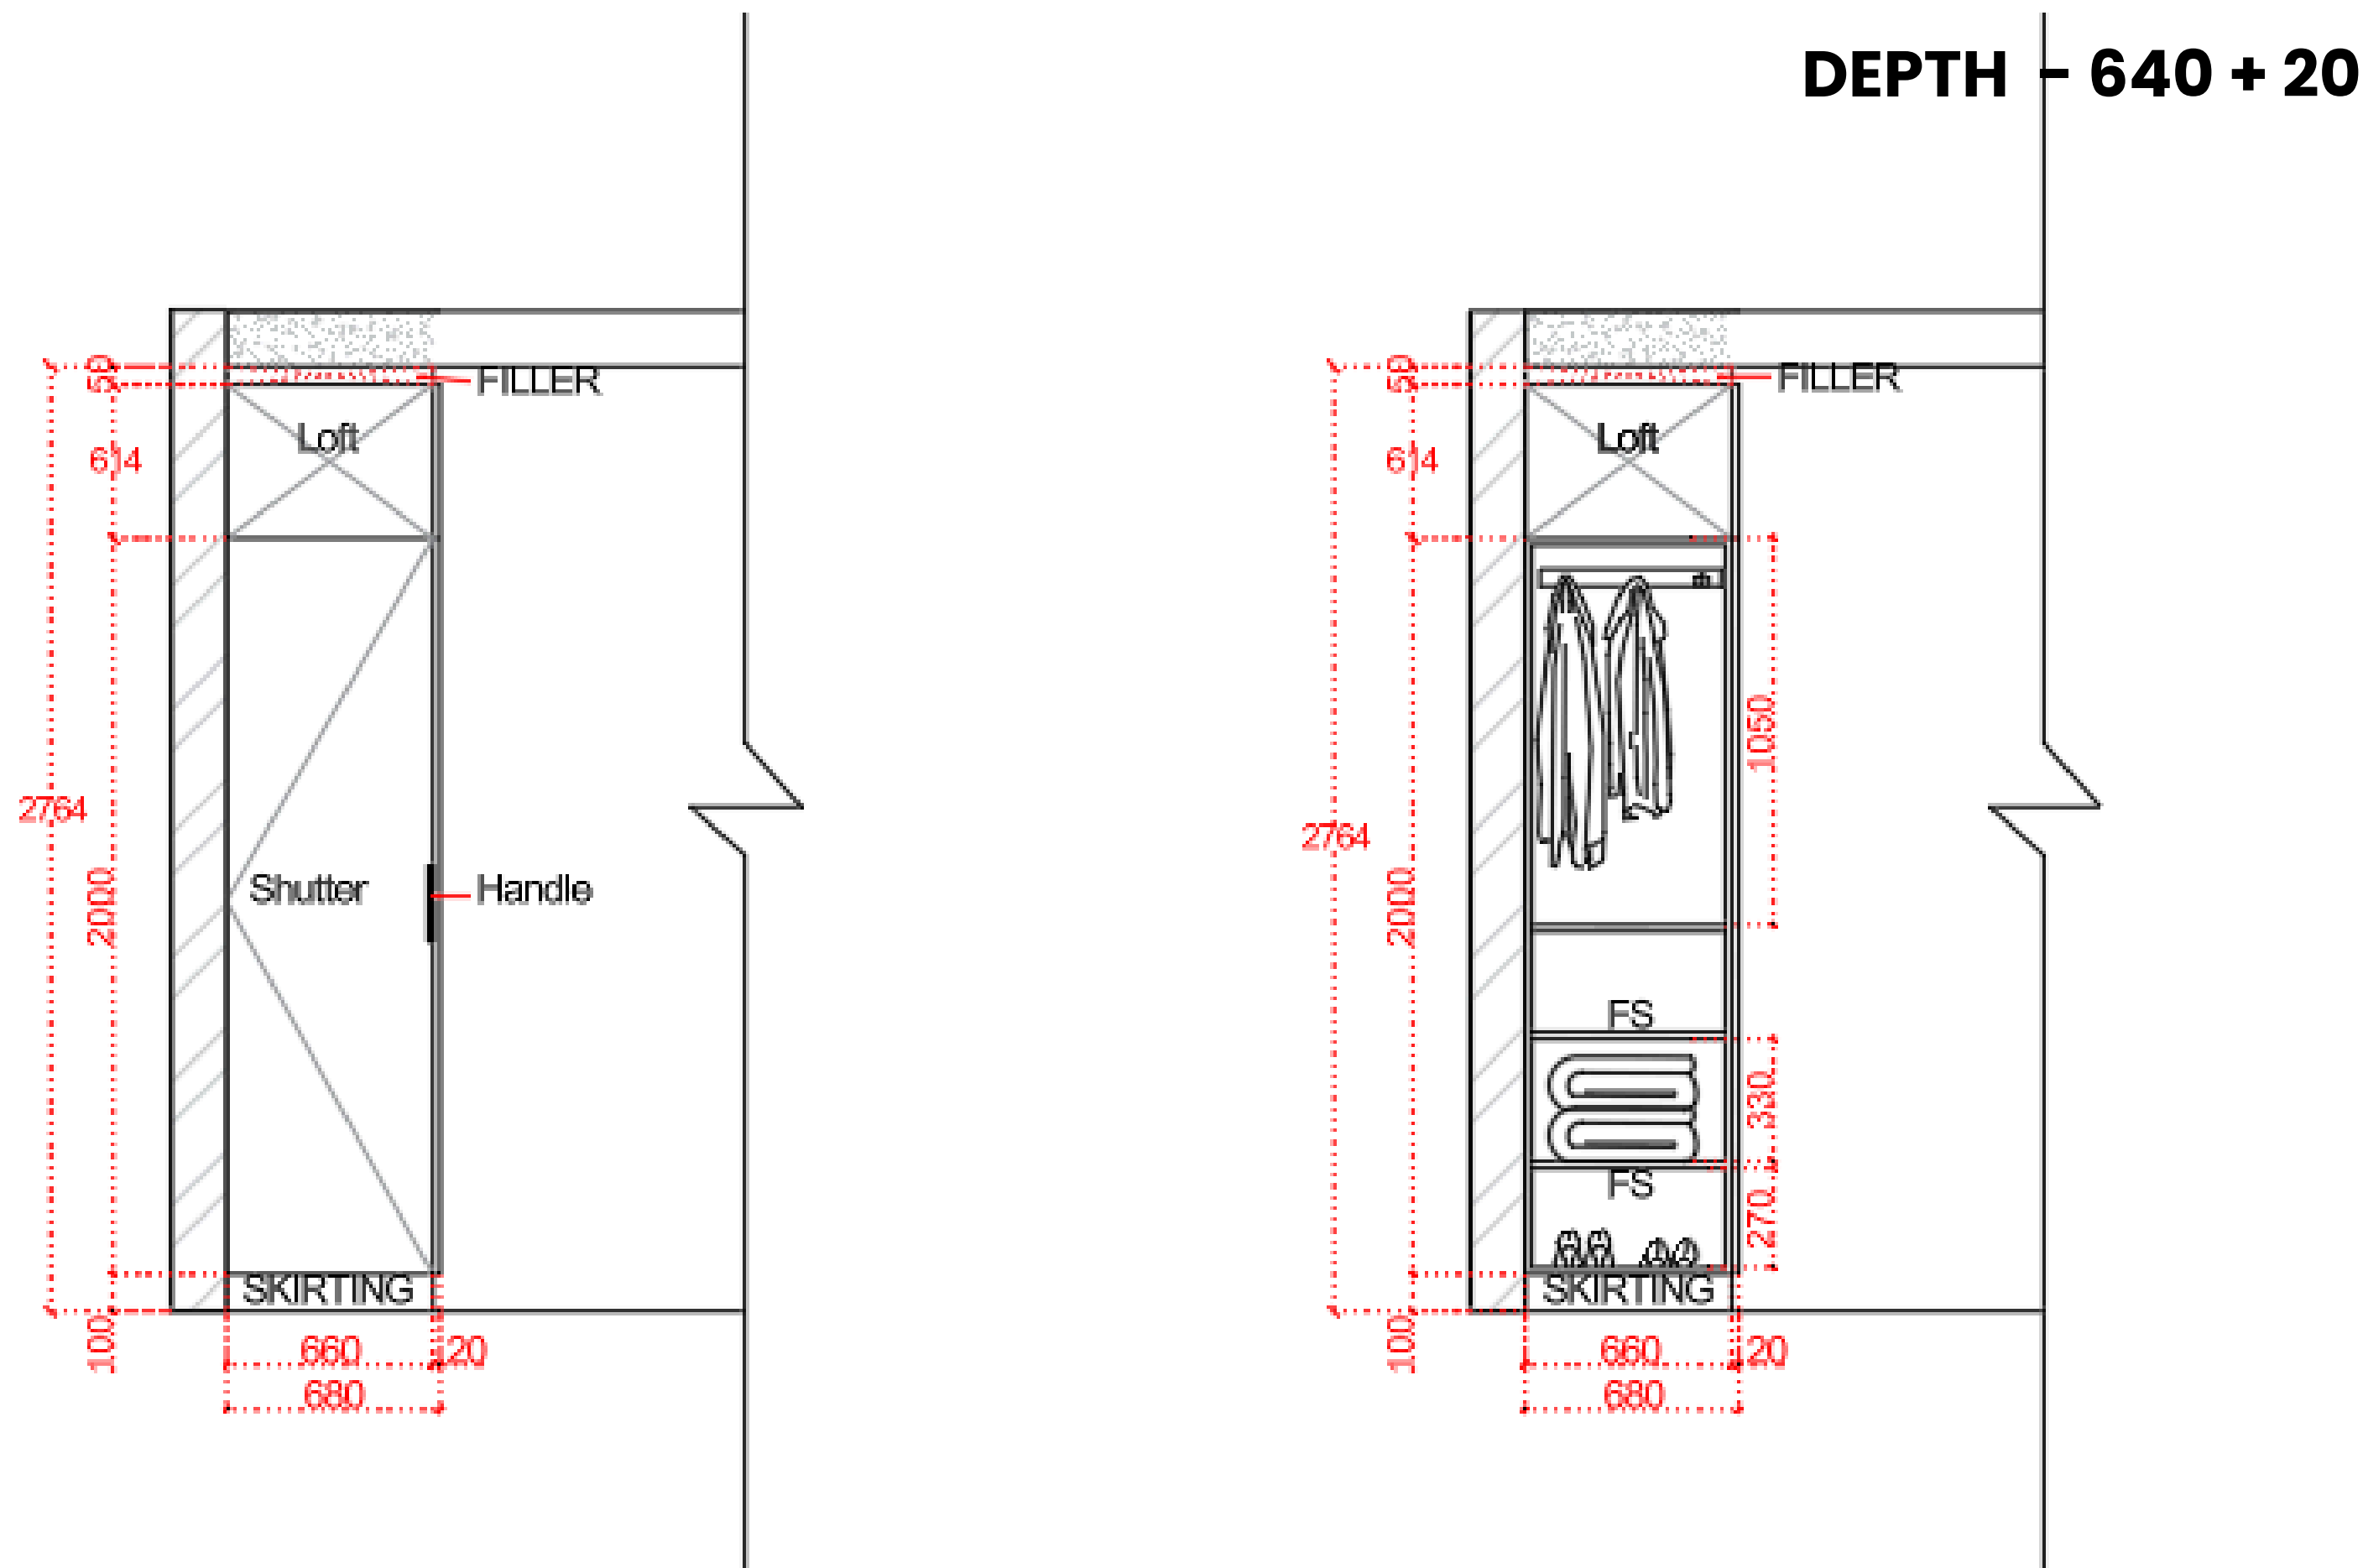


KIDS BEDROOM STUDY

DEPTH OF FLOATING UNIT – 530 + 20


DEPTH OF TALL UNIT – 280 + 20

DEPTH OF WALL UNIT – 280 + 20

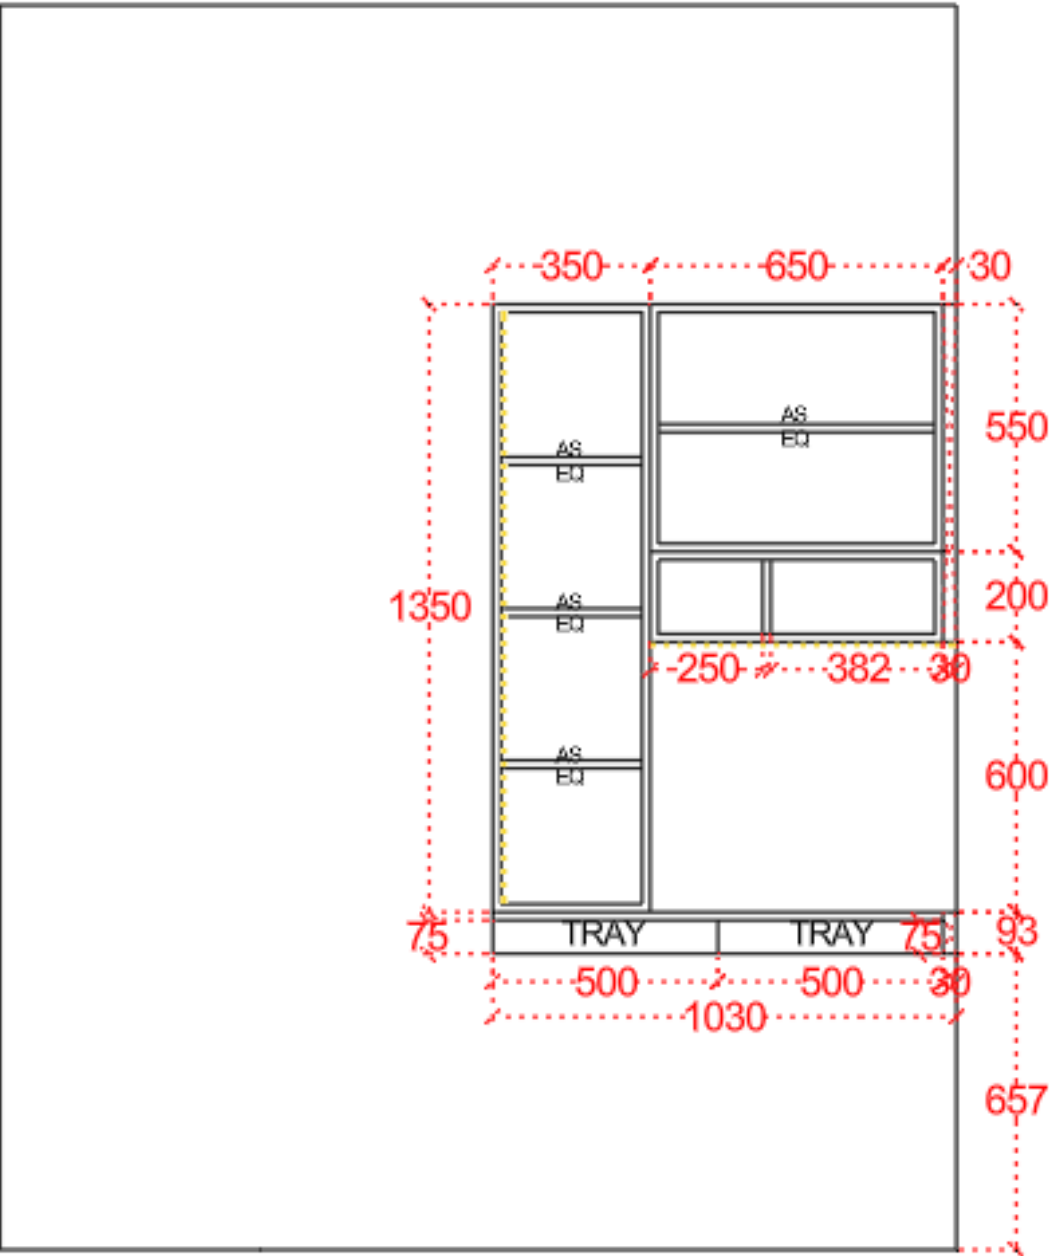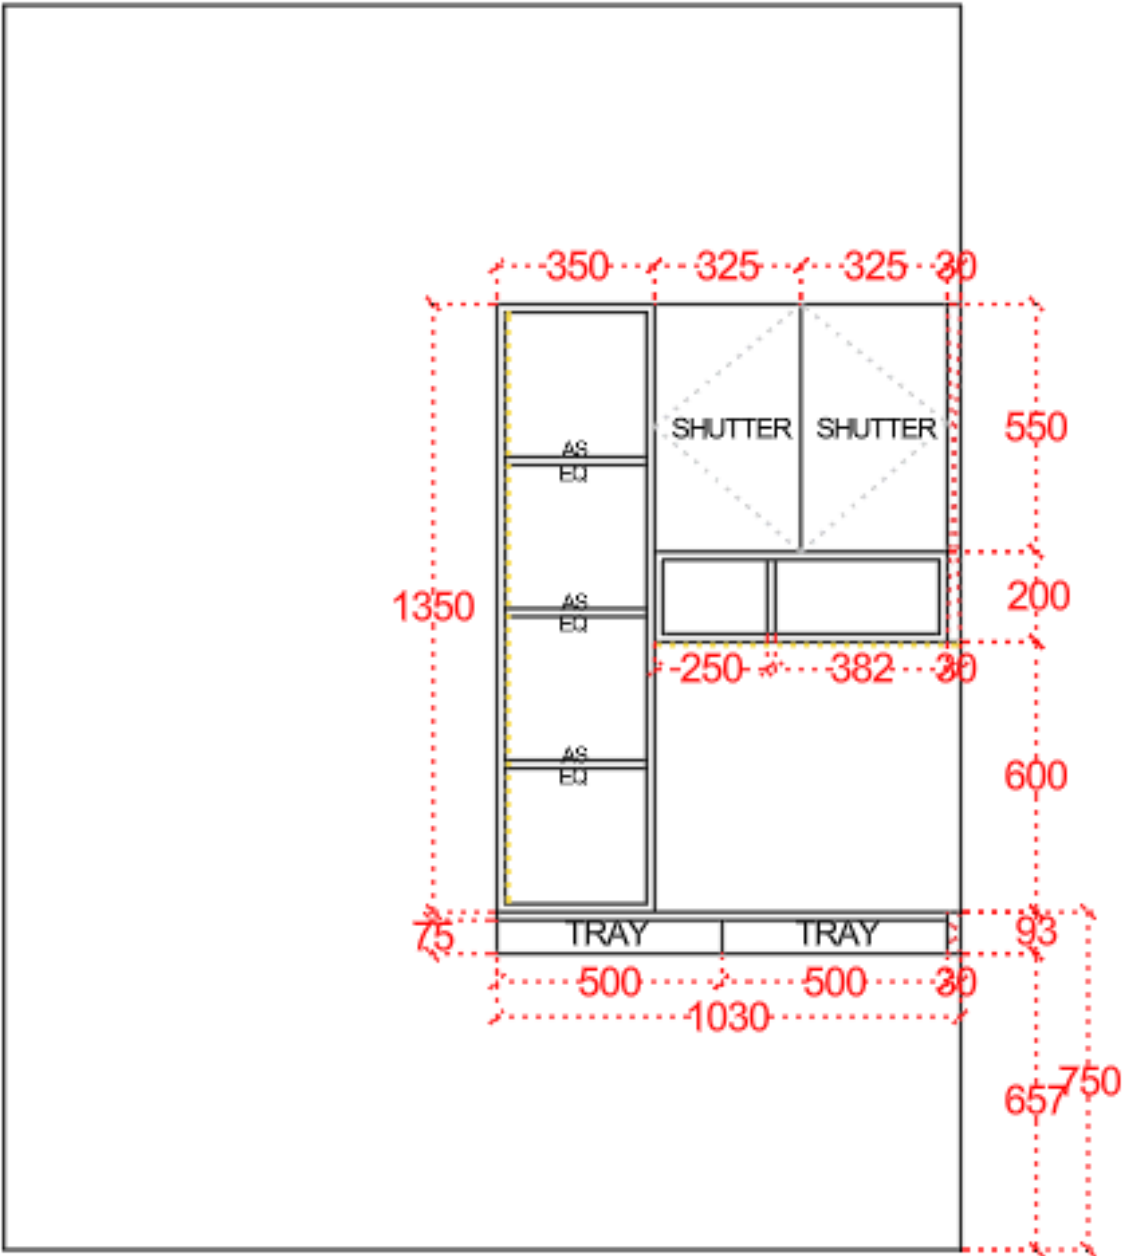


GUEST BEDROOM WARDROBE – EXTERNAL

DEPTH – 560 + 20

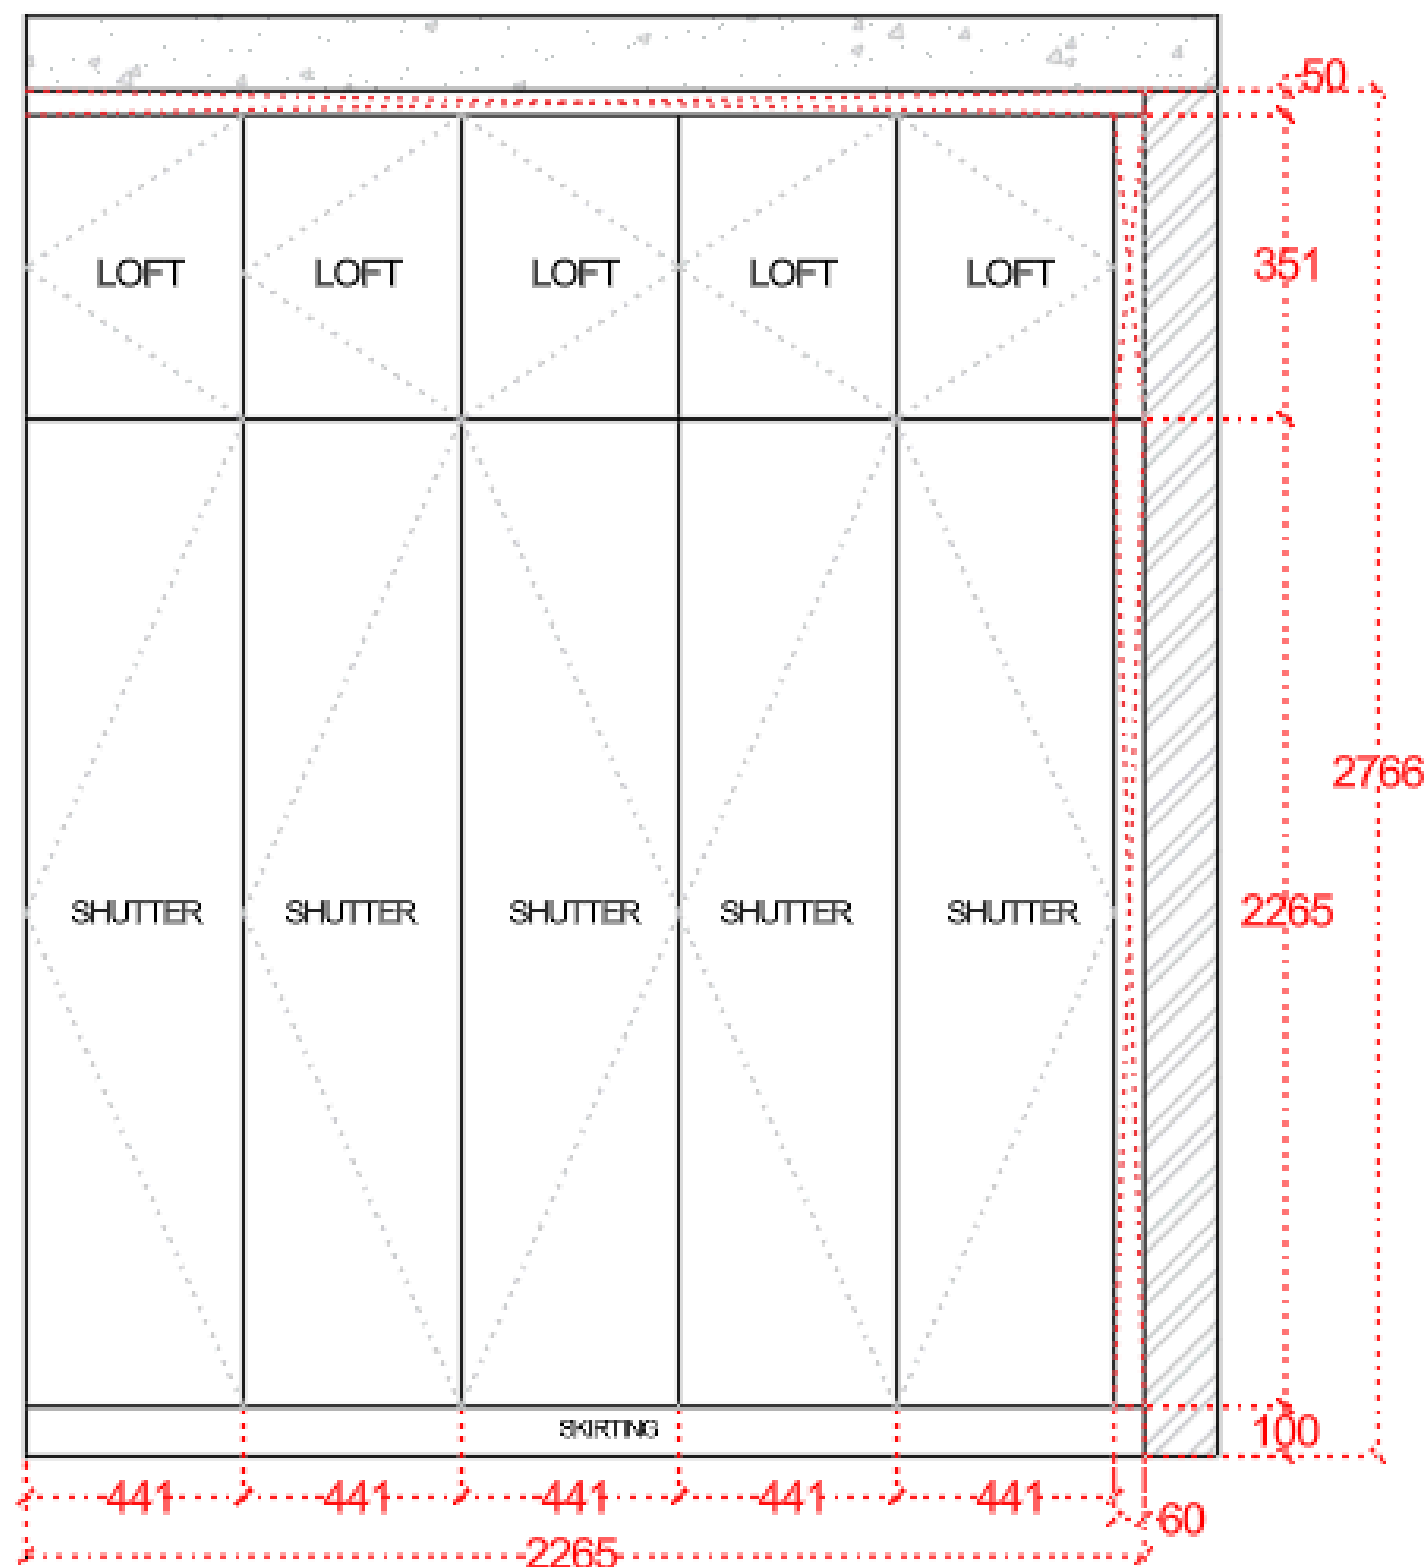

GUEST BEDROOM WARDROBE – INTERNAL


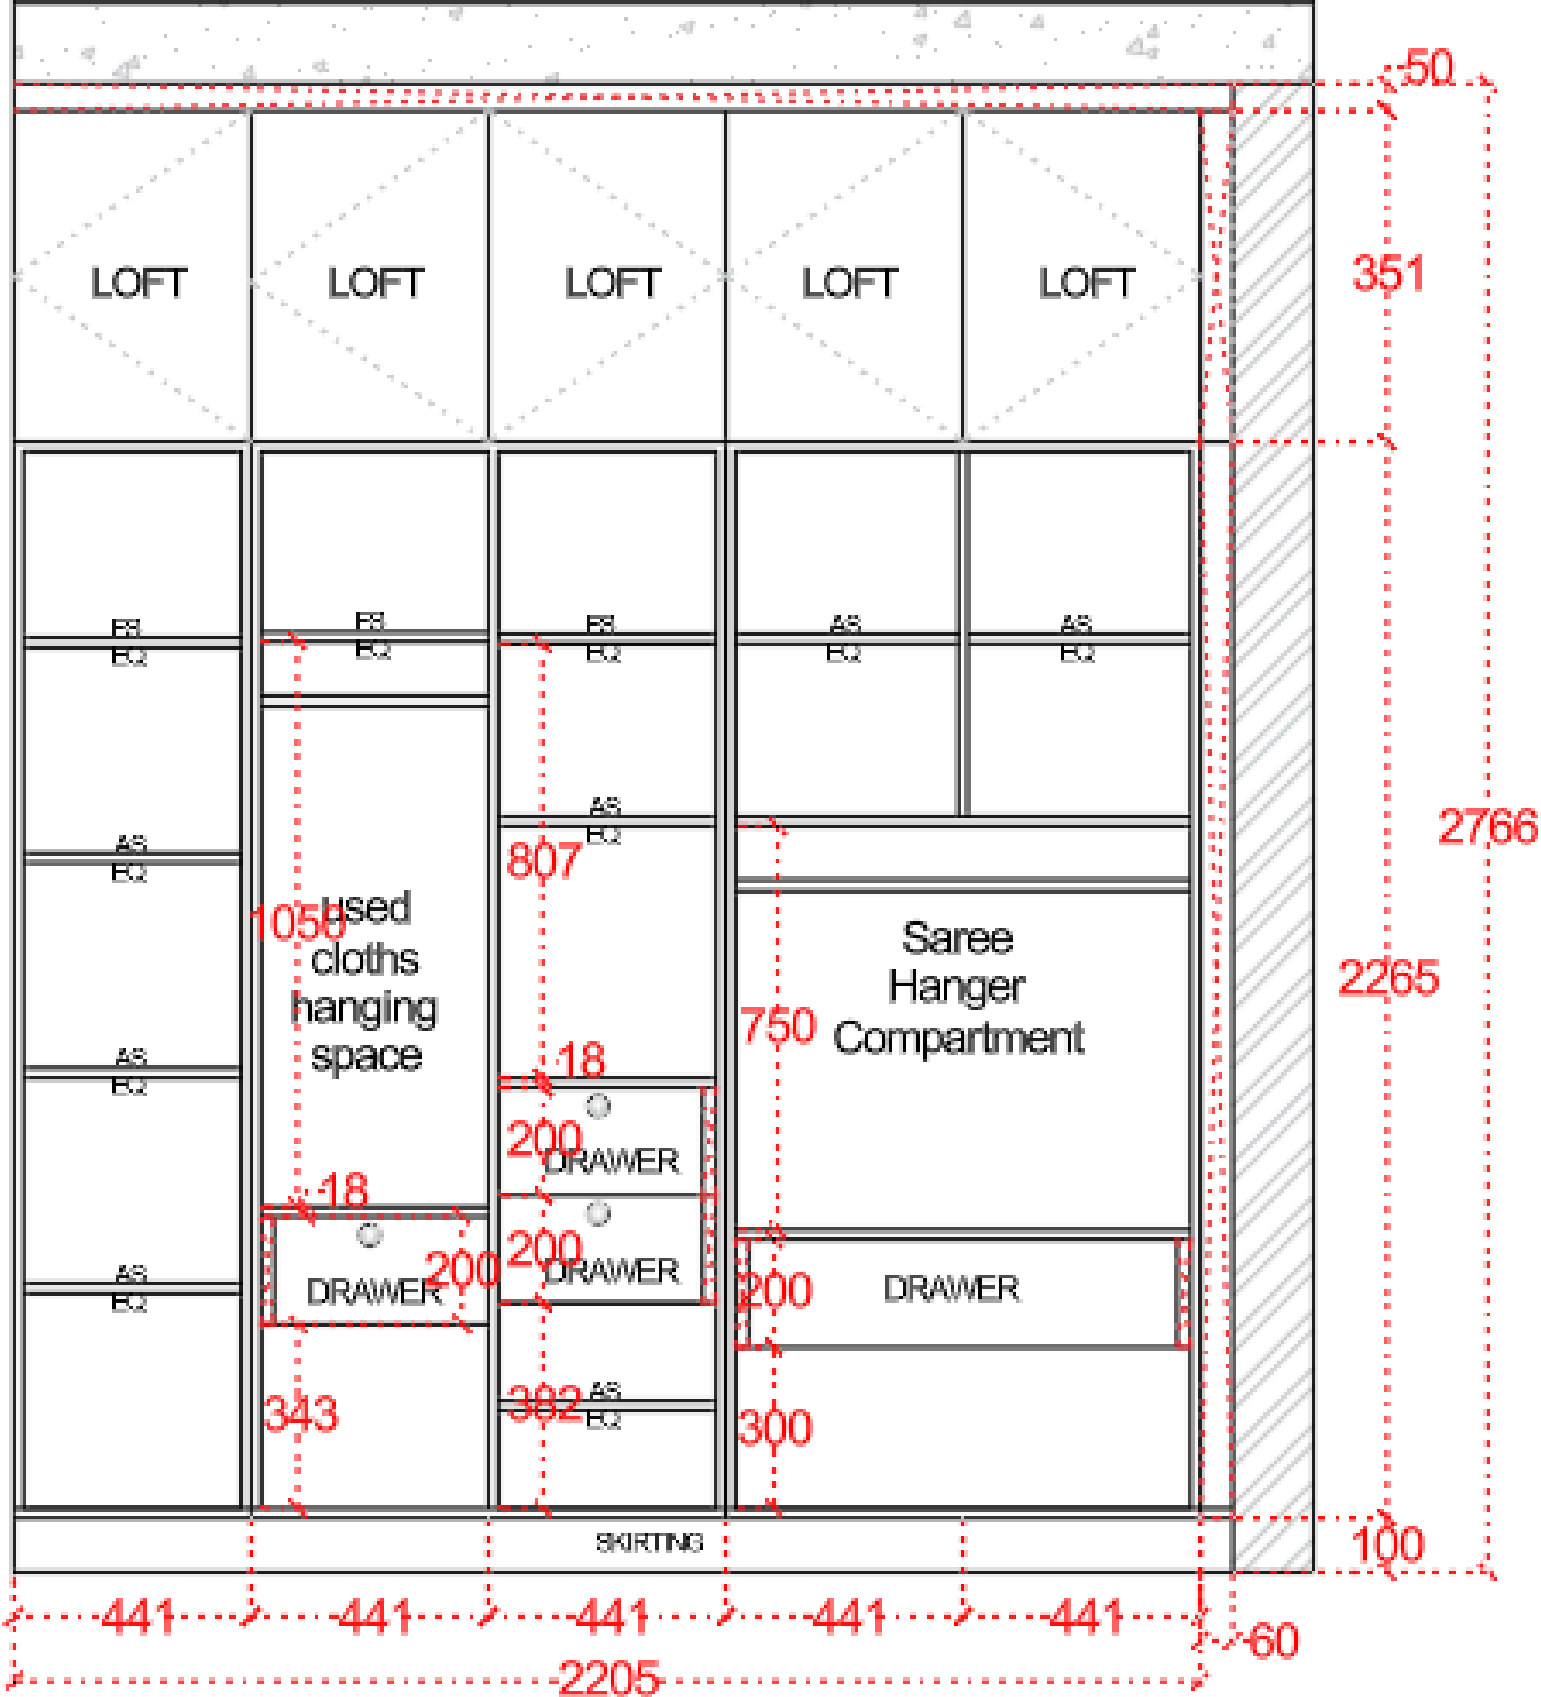


DEPTH – 560 + 20

GUEST BEDROOM- DRESSER

DEPTH OF STORAGE BEHIND MIRROR- 180 + 20

DEPTH OF DRAWERS - 400 + 20

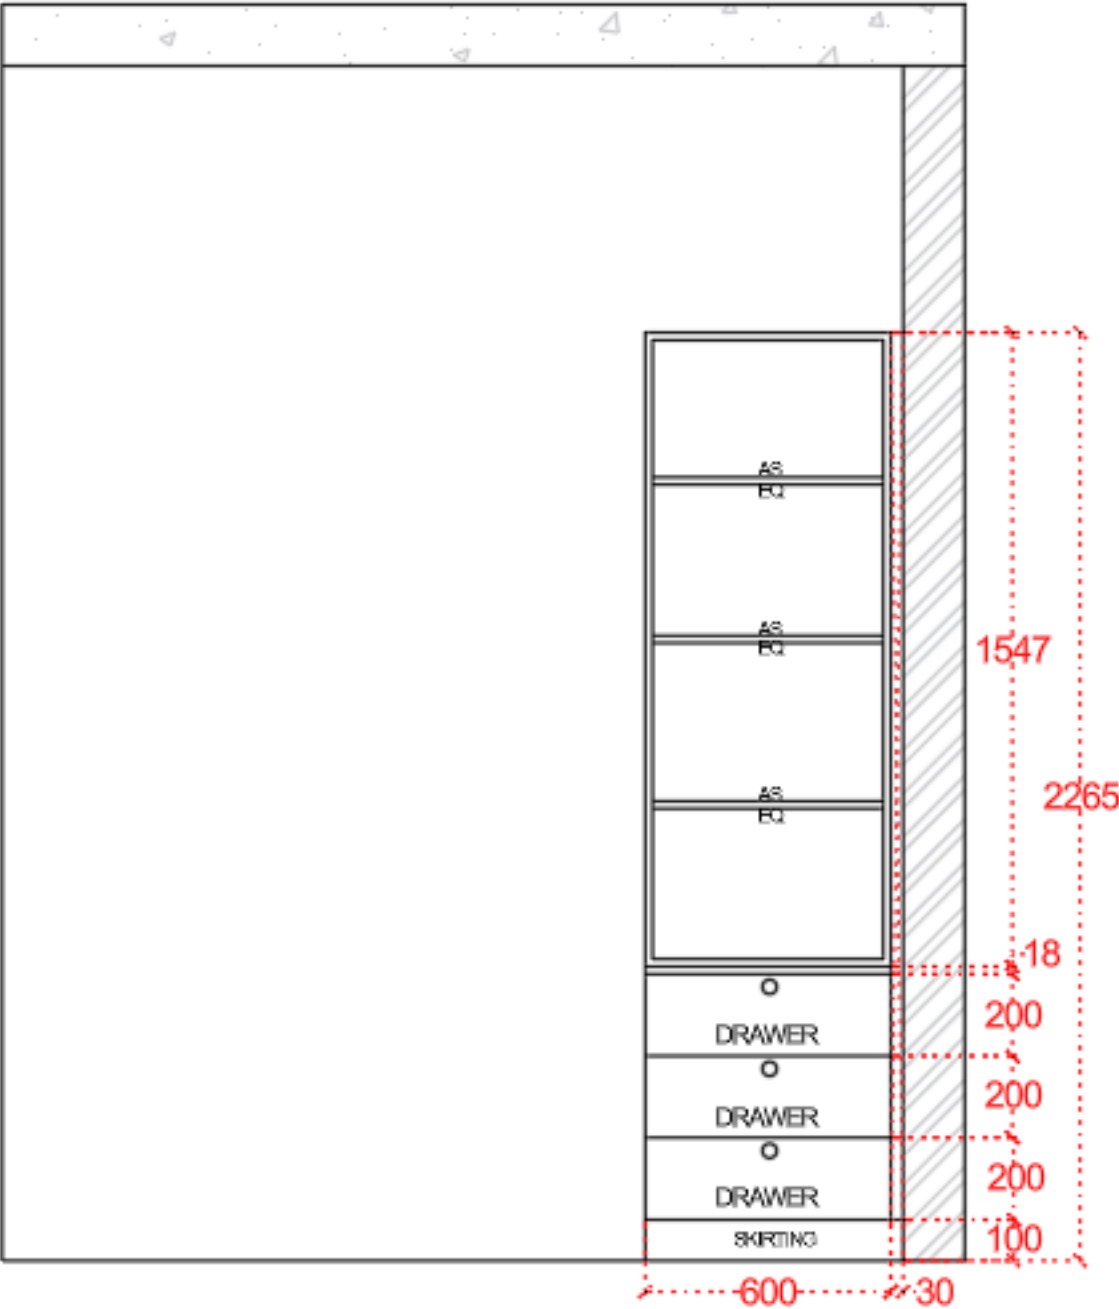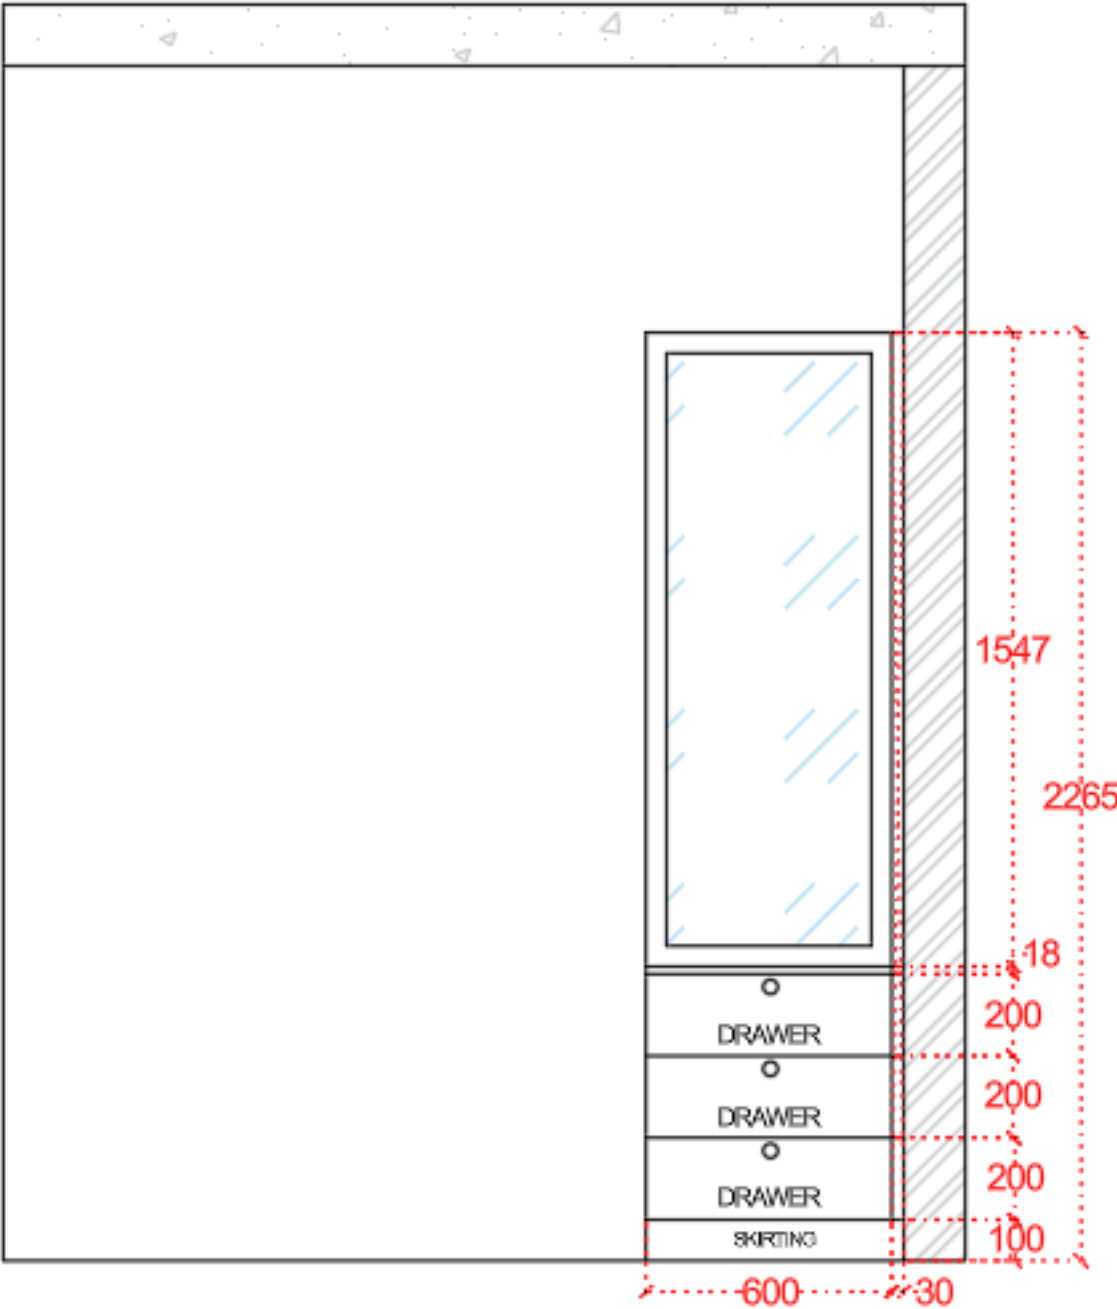

MOP UNIT – BALCONY

DEPTH – 280 + 20

